




LANDESGERICHTSTR. 6

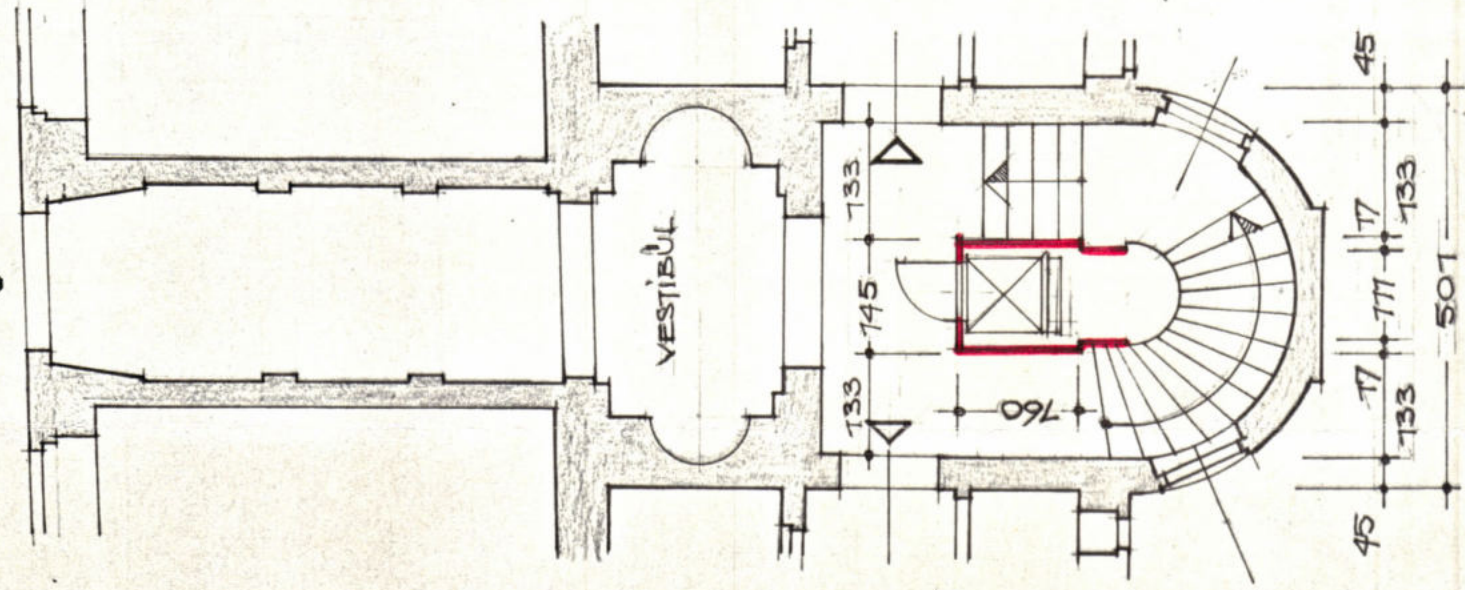


ERDGESCHOSS
U. KELLER

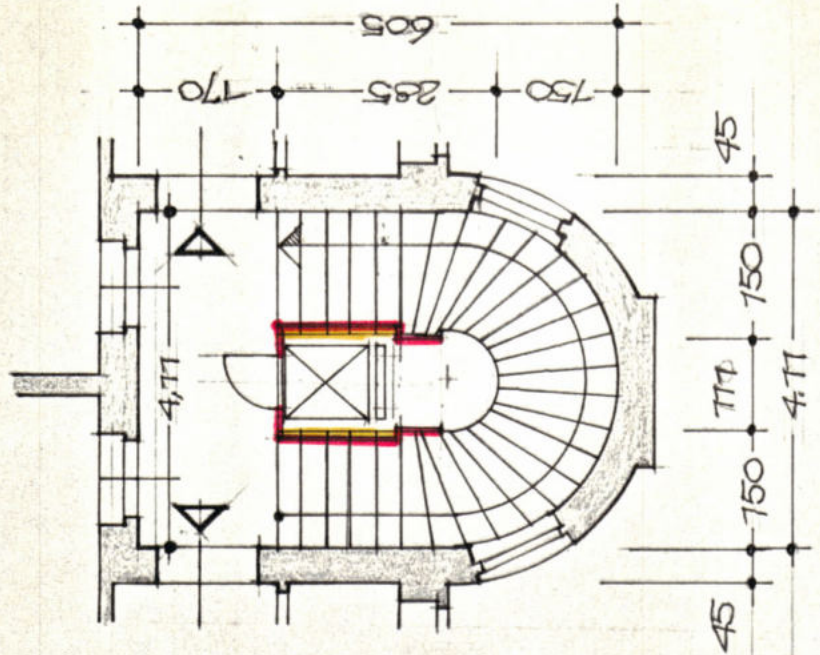

MEZZANIN - 3. STOCK

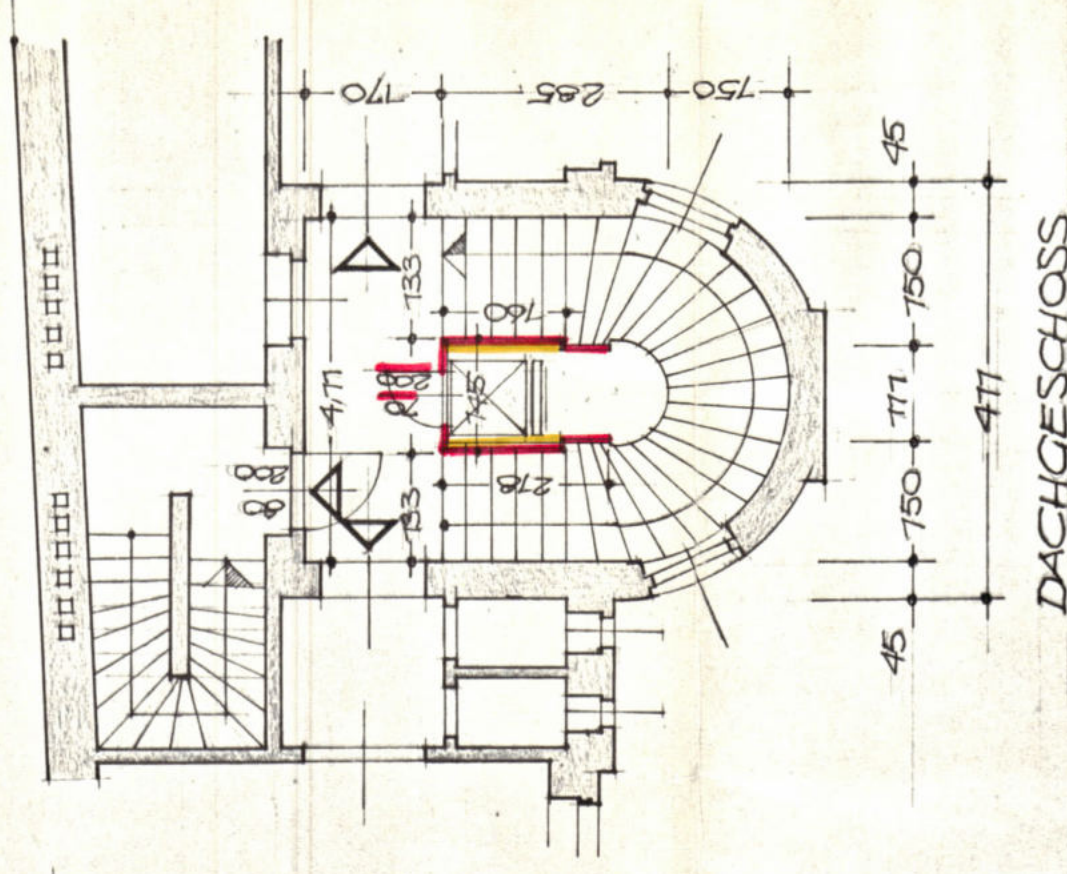


DACHGESCHOSS

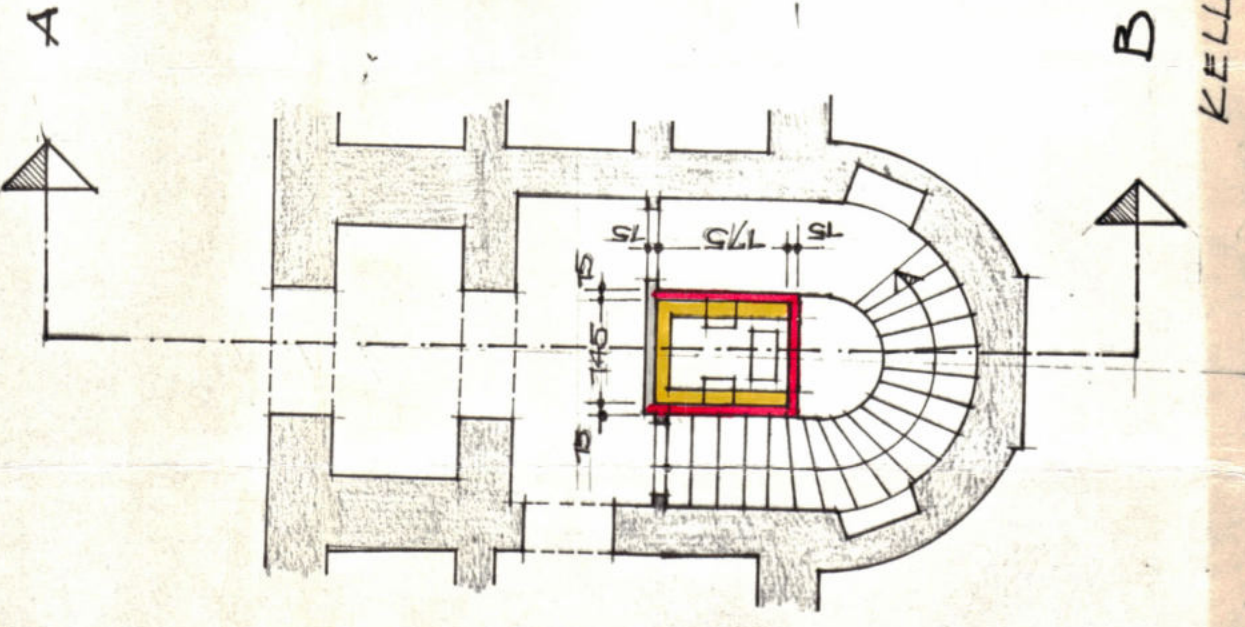


KELLER

ABBRUCH
DURISOL
-NEUE BAUTEILE
ALTBESTAND
STAHLBETON

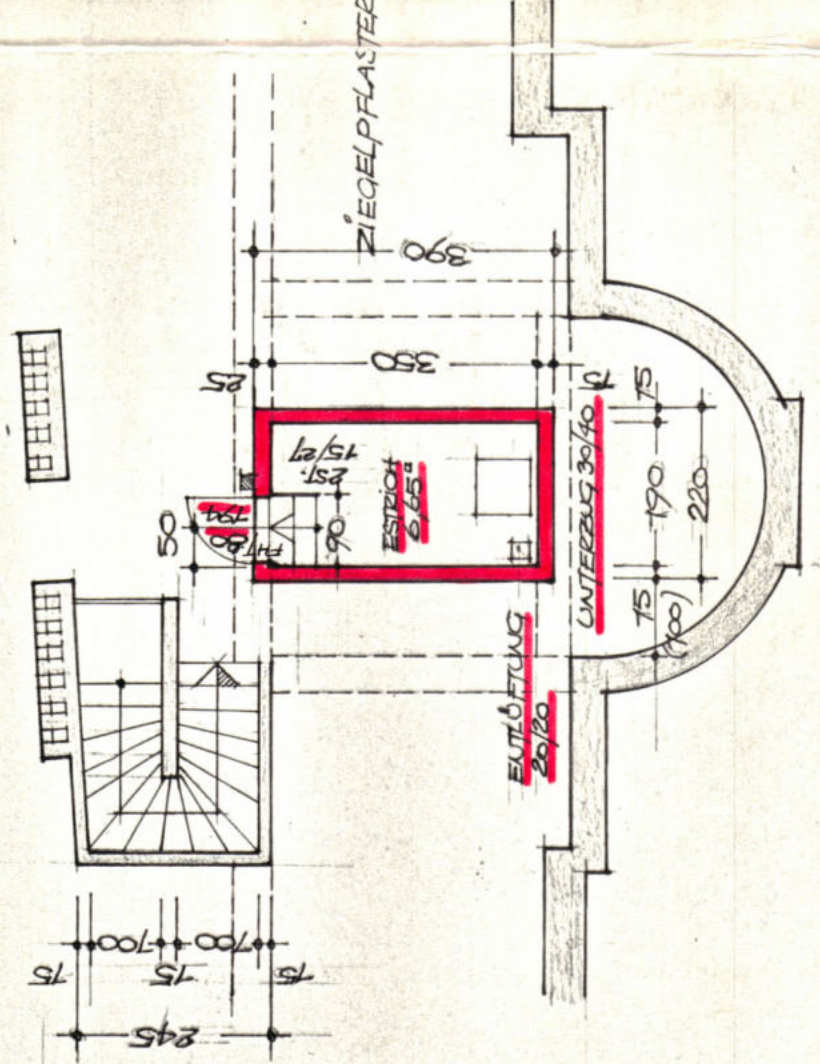

DACHBODEN - TREIBWERKSRAUM

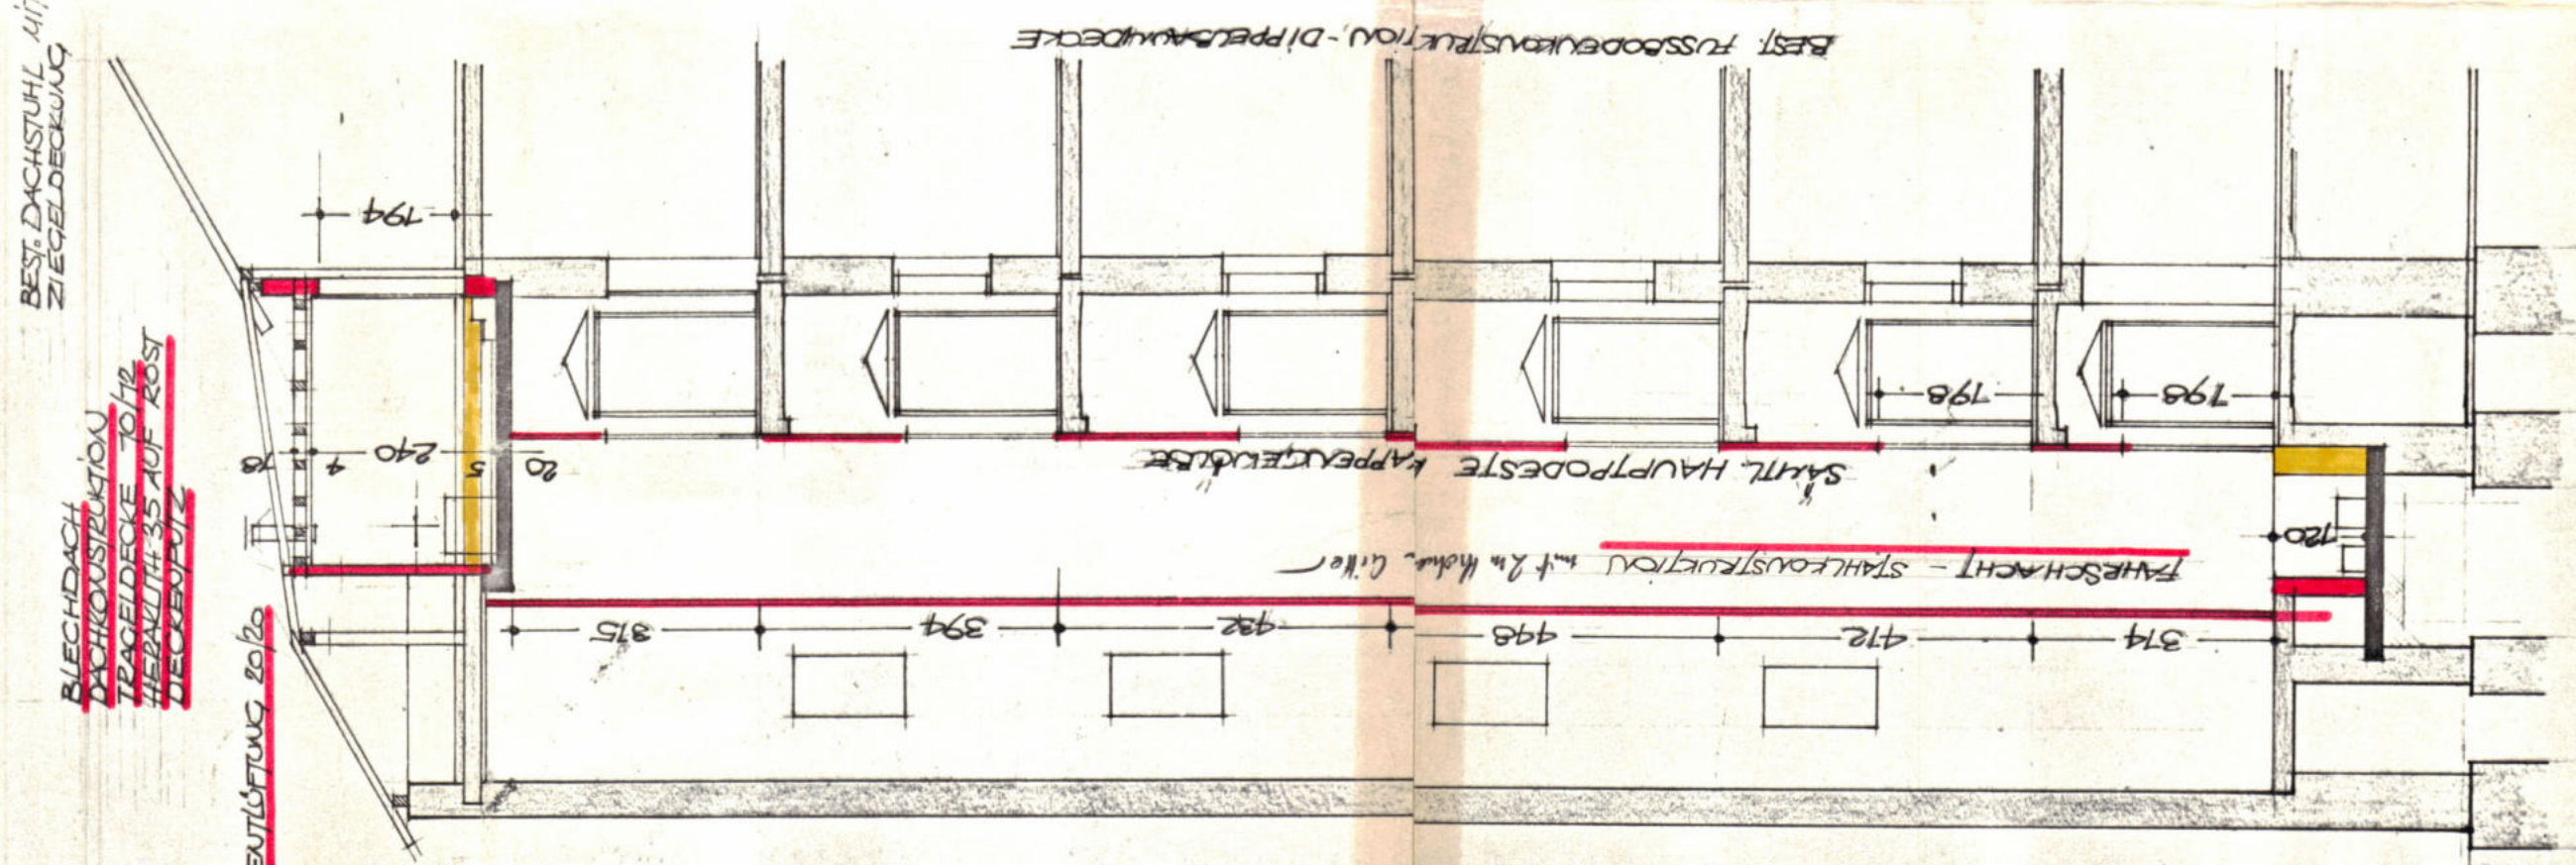

DACHGESCHOSS
120,00
2. STOCK
116,00
2. STOCK
111,71
1. STOCK
111,26
MEZZANIN
115,14
ERDGESCHOSS
109,00
SCHICHTSOLE
112,00
POL-KELLER

SCHNITT A - B

M. Abt. 20
Archivstück

Magistrat der Stadt Wien
Magistratsabteilung 35
Allgemeine Baupolizeibehörde
Hierauf bezieht sich die Bescheid
MA 35-101/191/72
Wien, 19. Okt. 1973
Für den Mithilingshalter



EINREICHPLAN

ZUM EINBAU EINES PERSONENAUFZUGES IM
HAUSE

WIEN I, LANDESGERICHTSTR. 6

GRUNDEISSE, SCHNITT
M 1: 700

BAUWERBER:
GRUNDEIGENTÜMER:
(HAUSEIGENTUM)
PLANVERFASSER:
BAUFÜHRER:

ING. A. WOLFGANG
WELTING
Stadtbr.
Vl. Stum
67-45-25 + 67-61-14
10. Okt. 1973

WIEN, OKTOBER 1973