(MA 30 Vid.)

21/2 C

Magistrat der Stadt Wien
Magistratsabteilung 37
Baupolizei
Hieraut bezieht sich der Bescheid
MA 37 /1- Landesgerichtsstraße 6/3340/93
Wien, 01. Aug. 1994
Für den Abteilungsleiter:

Dipl.-Ing. Czermak
Oberstadtbaurat

PLANUNG:	ing. wolfgang grill baumeister 1050 wien einsiedlerplatz 2 tel 55 44 54 fax 545 24 22 D – netz 0663/88 72 35

EINREICHPLAN 1:100

FÜR EINE BAULICHE ÄNDERUNG IM HAUSE

1010 WIEN LANDESGERICHTSSTRASSE 6

KAT.GEM. Innere Stadt
E.Z. 894

BAUWERBER:

Steh–Gast Betriebs Ges.m.b.H.
1010 Wien Landesgerichtsstrasse 6

Steh - Gast
Betriebs Ges.m.b.H.
Landesgerichtsstr. 6
1010 Wien, Tel. 406 30 8

GRUNDEIGENTÜMER:

Zentralverband der Hausbesitzer
Hausbesitzerhilfsverein
1010 Wien Landesgerichtsstrasse 6

Georg Neubauer Ges.m.b.H.
Immobilientreuhänder
1120 Wien Schönbrunnerstr 287
Telefon: 85 12 81, 83 14 01
KOM.RAT GEORG ... R
GESCHÄFTSFÜHRER

PLANVERFASSER u. BAUFÜHRER:

GRILL BAU
Gesellschaft m.b.H.
1050 Wien, Einsiedlerpl. 2/7
Tel. 55 44 54

WIEN IM Sept. 94

AV: MA 19 Stellungnahme im Akt

LAGEPLAN M 1:500

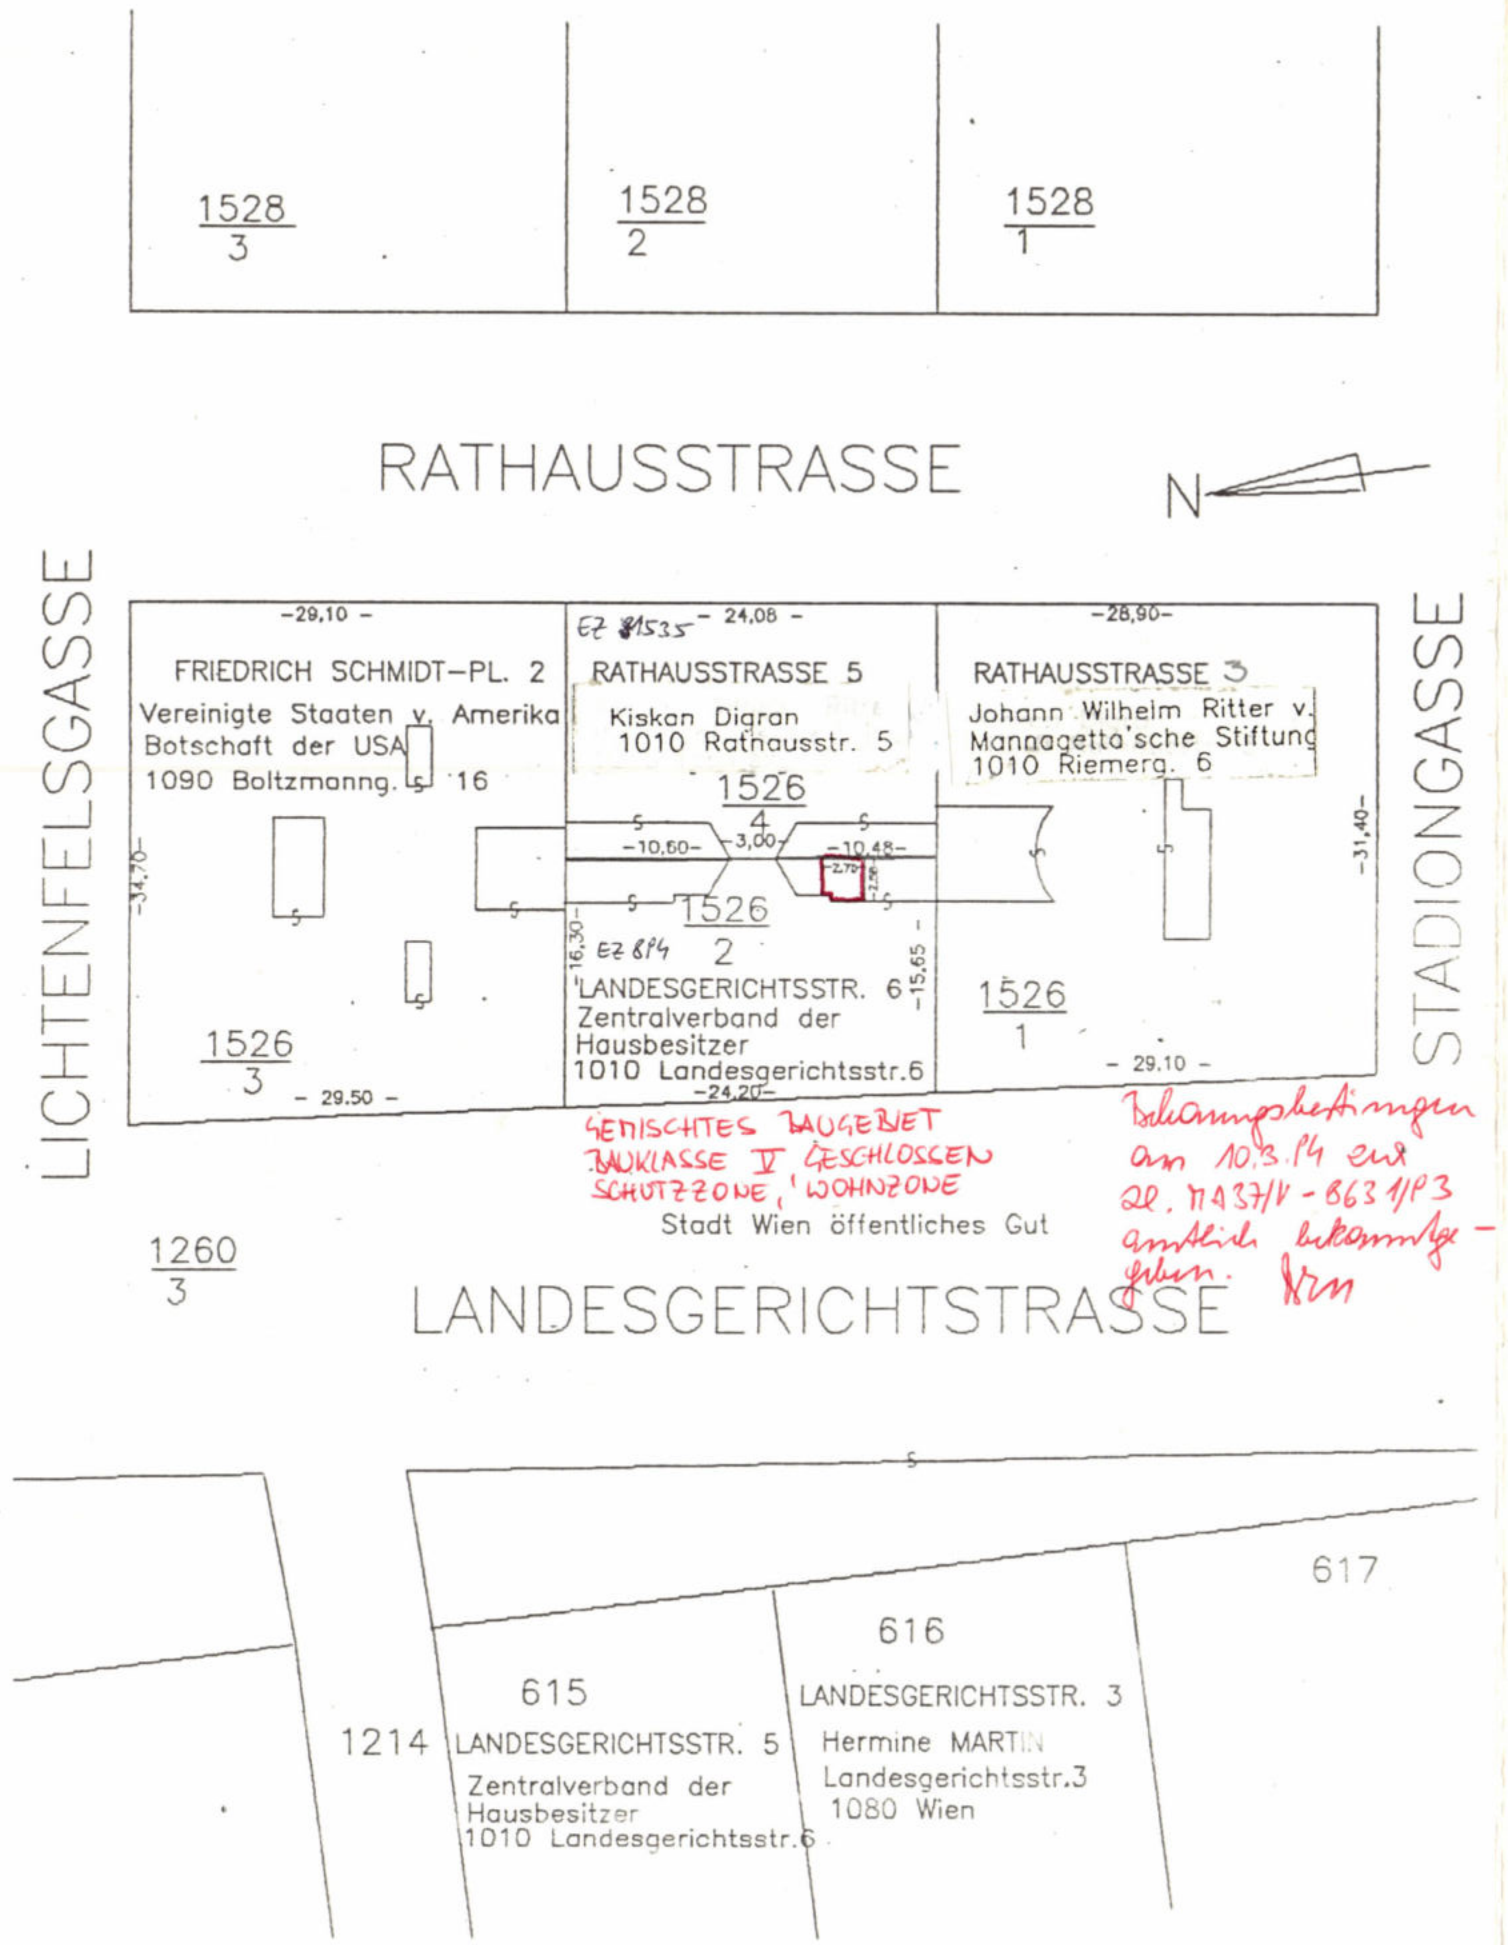

1528 / 3
1528 / 2
1528 / 1
RATHAUSSTRASSE
N
LICHTENFELSGASSE
STADIONGASSE
–29,10 –
EZ 1535 – 24,08 –
–28,90–
FRIEDRICH SCHMIDT–PL. 2
Vereinigte Staaten v. Amerika
Botschaft der USA
1090 Boltzmanng. 16
RATHAUSSTRASSE 5
Kiskan Digran
1010 Rathausstr. 5
1526 / 4
RATHAUSSTRASSE 3
Johann Wilhelm Ritter v.
Mannagetta'sche Stiftung
1010 Riemerg. 6
–34,70–
–31,40–
–10,60–
–3,00–
–10,48–
1526 / 2
EZ 894
16,30
–15,65
LANDESGERICHTSSTR. 6
Zentralverband der
Hausbesitzer
1010 Landesgerichtsstr. 6
–24,20–
1526 / 3
– 29,50 –
1526 / 1
– 29,10 –
Stadt Wien öffentliches Gut
1260 / 3
LANDESGERICHTSTRASSE
1214
615
LANDESGERICHTSSTR. 5
Zentralverband der
Hausbesitzer
1010 Landesgerichtsstr. 6
616
LANDESGERICHTSSTR. 3
Hermine MARTIN
Landesgerichtsstr. 3
1080 Wien
617

GEMISCHTES BAUGEBIET BAUKLASSE I GESCHLOSSEN SCHUTZZONE, WOHNZONE

Bebauungsbestimmungen am 10.3.94 zur Zl. MA 37/I - 8631/93 amtlich bekanntgegeben. Krn

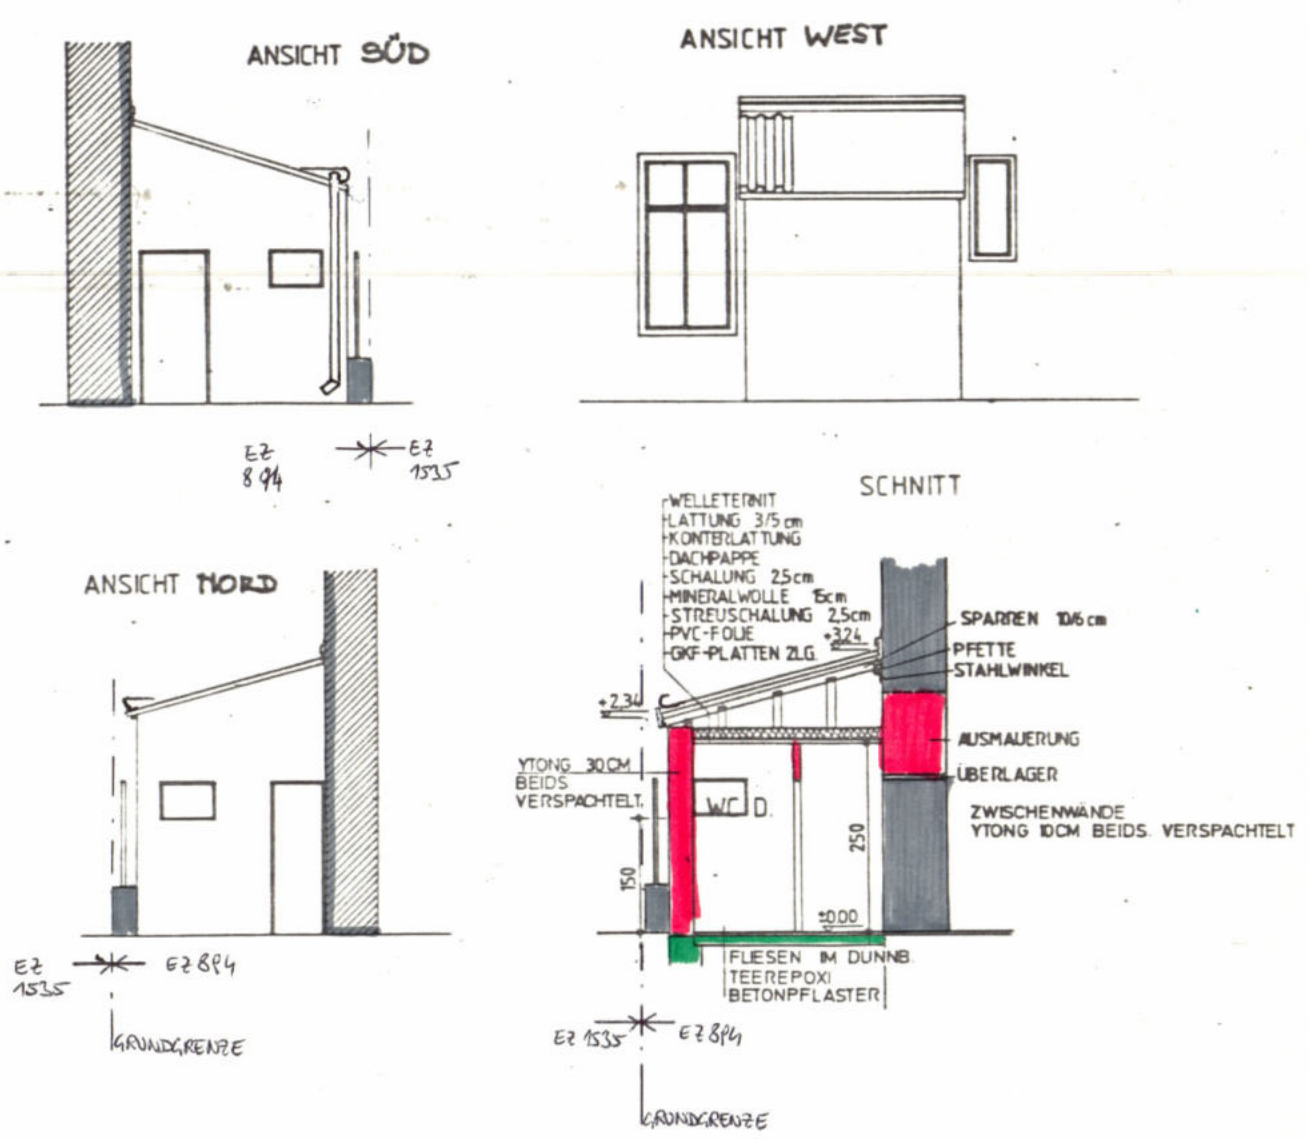

ANSICHT SÜD
EZ 894
EZ 1535
ANSICHT WEST
ANSICHT NORD
EZ 894
EZ 1535
GRUNDGRENZE
SCHNITT
WELLETERNIT
LATTUNG 3/5 cm
KONTERLATTUNG
DACHPAPPE
SCHALUNG 2,5cm
MINERALWOLLE 15cm
STREUSCHALUNG 2,5cm
PVC-FOLIE
GKF-PLATTEN 2LG
+3,24
+2,34
SPARREN 10/16 cm
PFETTE
STAHLWINKEL
AUSMAUERUNG
ÜBERLAGER
ZWISCHENWÄNDE YTONG 10CM BEIDS. VERSPACHTELT
YTONG 30CM BEIDS. VERSPACHTELT
WC D
250
150
±0,00
FLIESEN IM DÜNNB.
TEEREPOXI
BETONPFLASTER
EZ 1535
EZ 894
GRUNDGRENZE

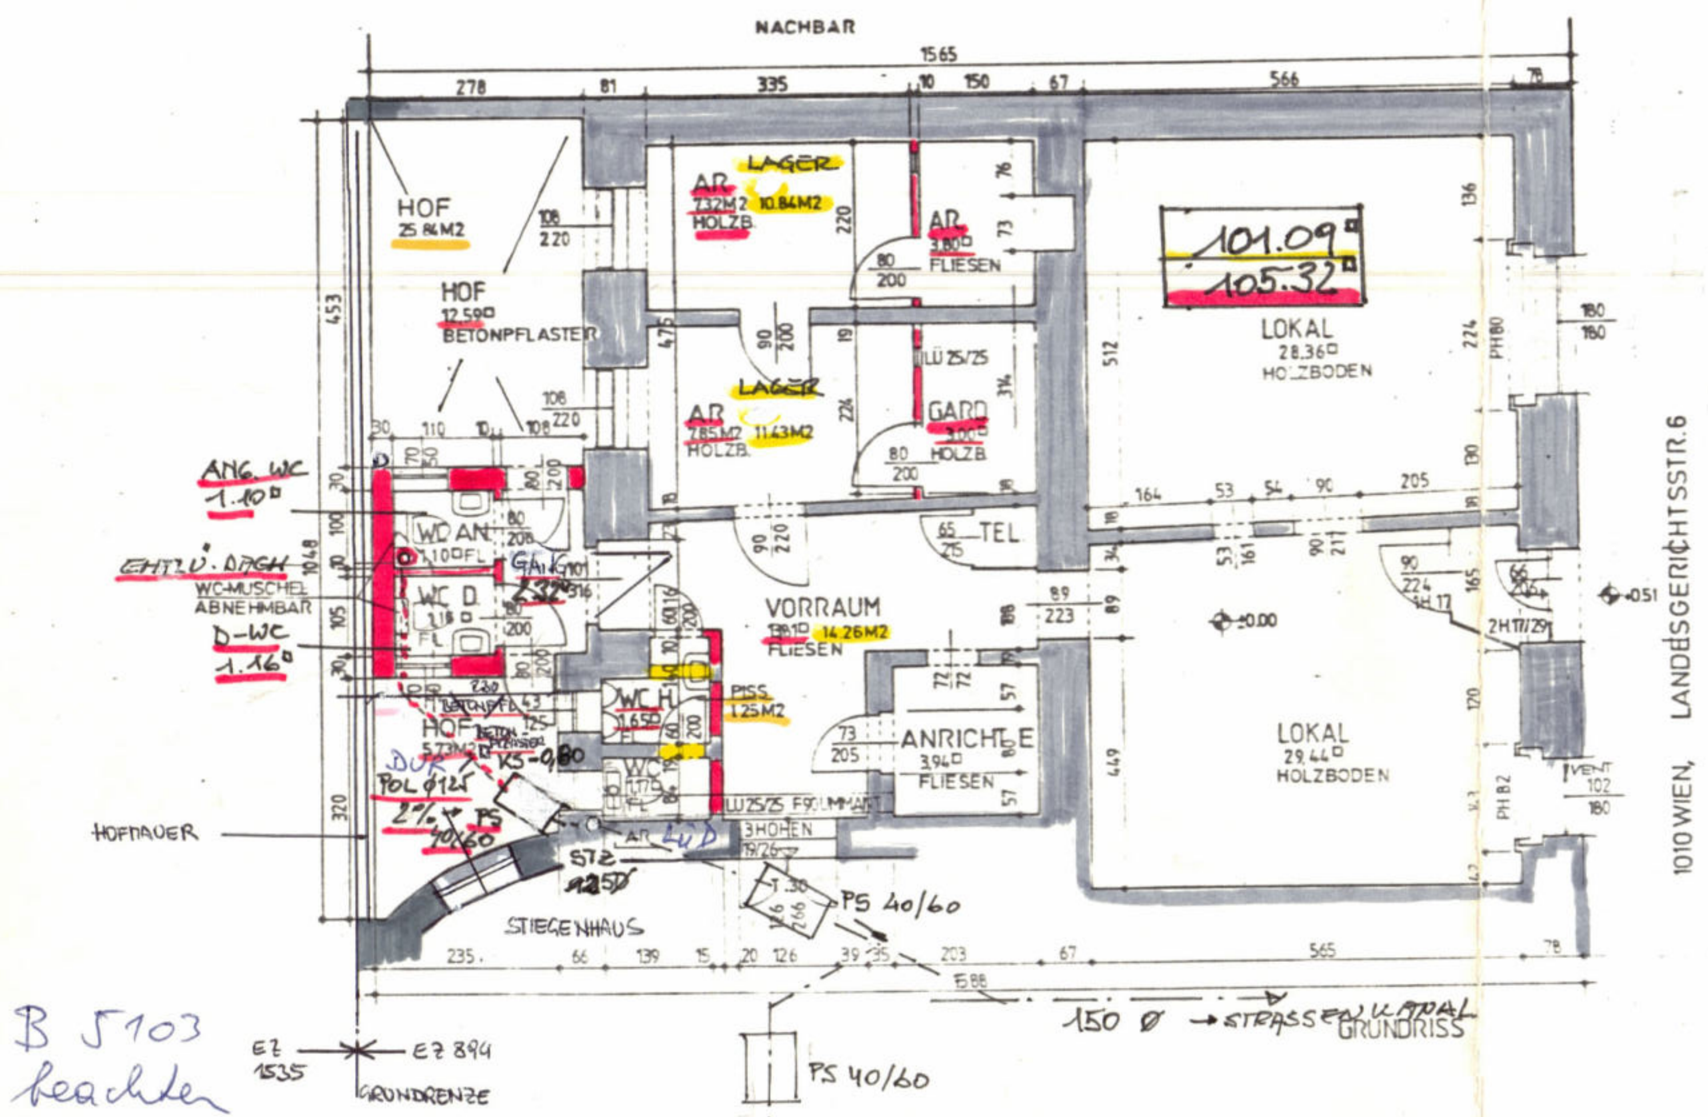

NACHBAR
1565
278
81
335
10
150
67
566
78
HOF 25,86 M2
HOF 12,59 BETONPFLASTER
AR 7,32 M2 HOLZB.
LAGER 10,84 M2
AR 3,80 FLIESEN
AR 7,85 M2 HOLZB.
LAGER 11,43 M2
LÜ 25/25
GARD. 3,00 HOLZB.
101.09
105.32
LOKAL 28,36 HOLZBODEN
LOKAL 29,44 HOLZBODEN
TEL
VORRAUM 13,81 14,26 M2 FLIESEN
ANRICHTE 3,94 FLIESEN
WC AN 1,10 FL
GANG 2,32
WC D 1,16 FL
HOF 5,73 M2 BETONPFLASTER
KS -0,80
DUK POL Ø125
2% PS 40/60
WC H 1,65 FL
PISS. 1,25 M2
WC 1,17 FL
AR LÜD
LÜ 25/25 F90 UMMANT.
3 HÖHEN 19/26
STZ 1,25
STIEGENHAUS
PS 40/60
PS 40/60
HOFMAUER
ANG. WC 1.10
ENTLÜ. DACH
WC-MUSCHEL ABNEHMBAR
D-WC 1.16
±0,00
+0,51
2 H 17/29
VENT 102/180
PH 80
PH 82
1010 WIEN, LANDESGERICHTSSTR. 6
235
66
139
15
20
126
39
35
203
67
565
78
588
453
320
150 Ø → STRASSENKANAL
GRUNDRISS
EZ 1535
EZ 894
GRUNDGRENZE
KANALVERLAUF IM KELLER

B 5103 beachten

~~Nach Richtigstellung~~ einverstanden
Önormen B 2501, ~~B 2502~~, B 2503 ~~u. B 5101~~
sind ~~(ist)~~ einzuhalten.
MA 30 – Kanalisation

2. Dez. 1993