


Magistrat der Stadt Wien
Magistratsabteilung 37
Baupolizei


Hierauf bezieht sich der Bescheid
MA 37 11- Bauantrag Nr. 6/84/85
Wien, 1. Juli 1995
Für den Stellungsleiter:




Dipl.-Ing. Krain
Oberbauinspektor

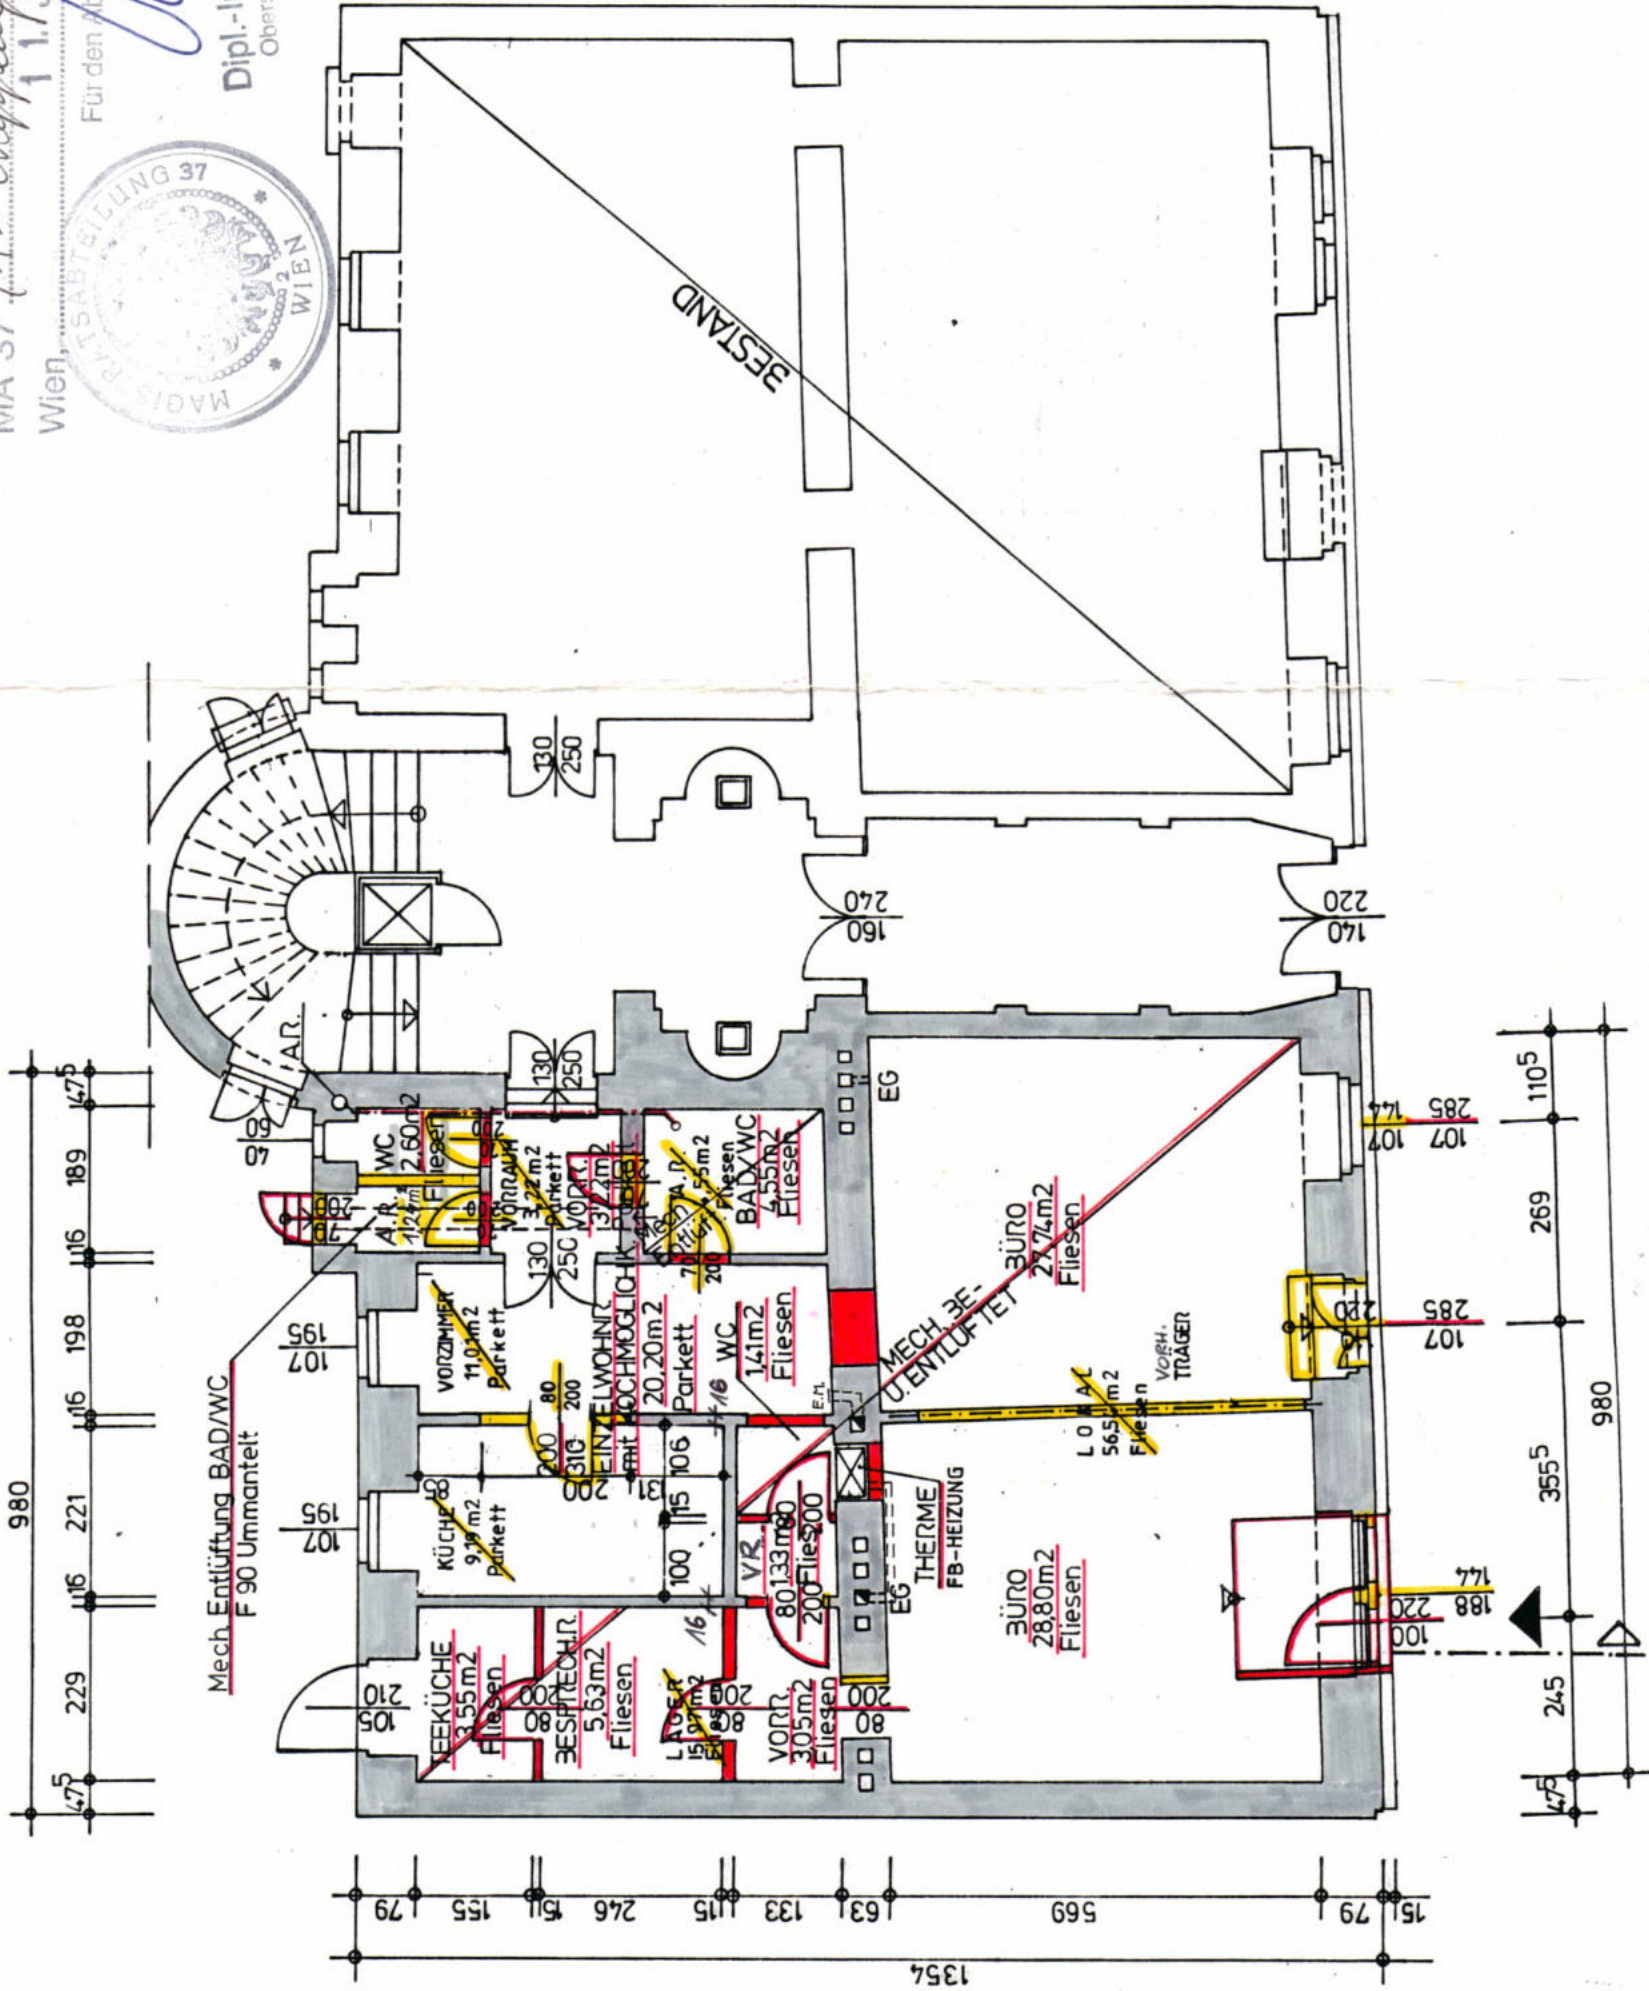

ERDGESCHOSS

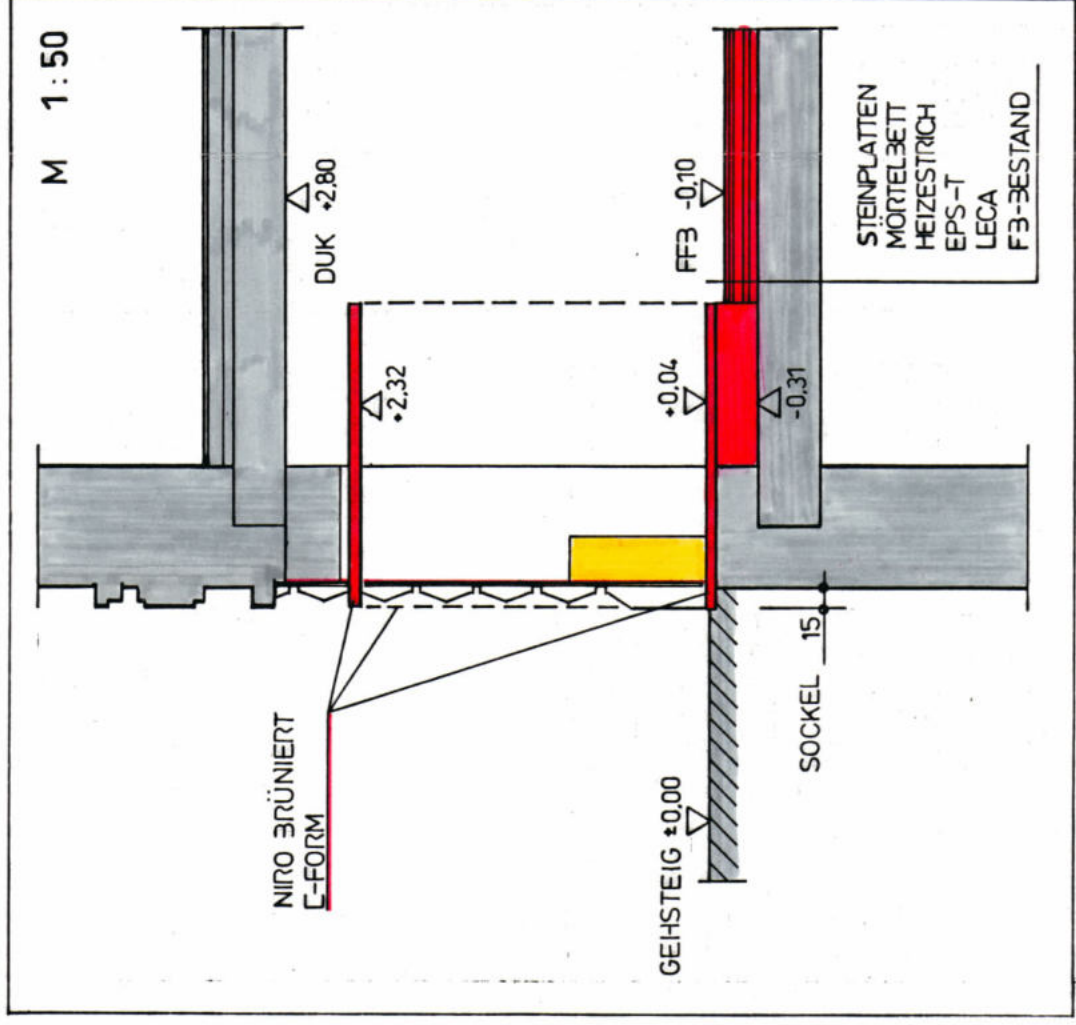


SCHNITT

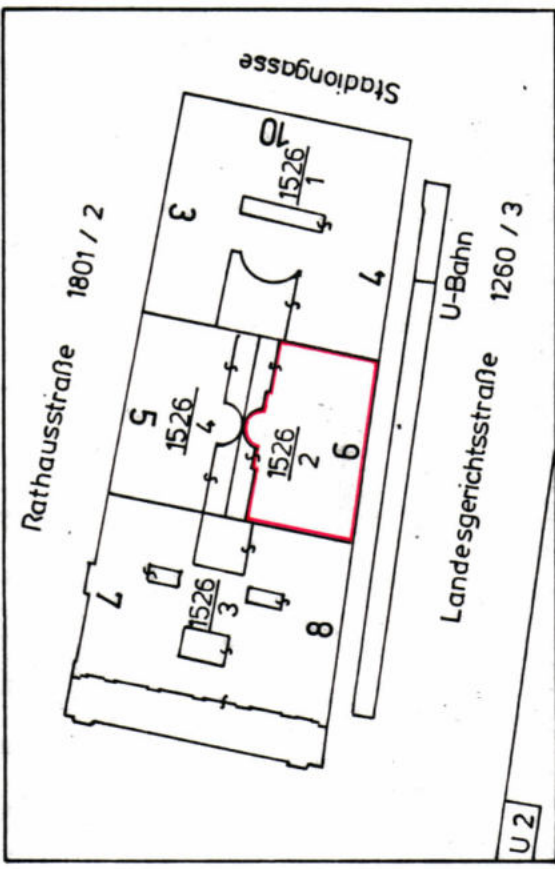

LAGEPLAN

M 1 : 1000

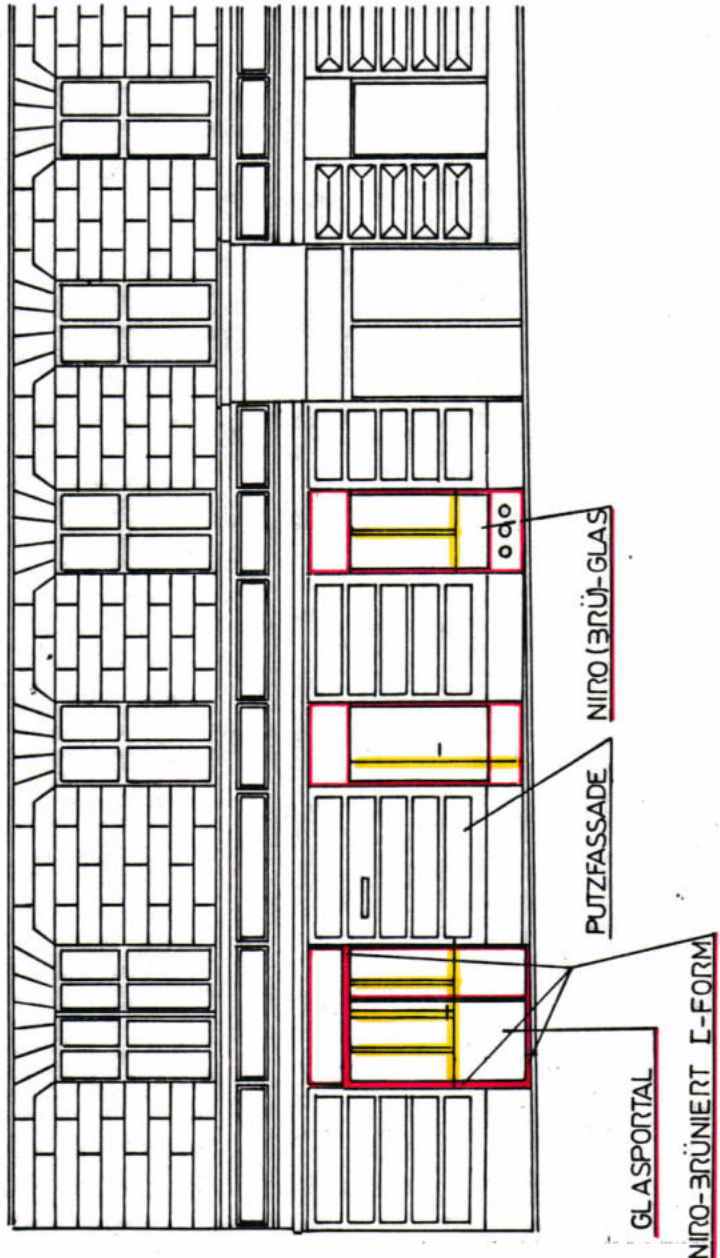

ANSICHT

PARIE	AMTLICHE VERMERKE	
A	B	C
20/2		

EINREICHPLAN

ÜBER BAULICHE ÄNDERUNGEN
WIEN 1, LANDESGERICHTSSTRASSE 6, TOP 2
FÜR DIE IMMO-CONTRACT

GRUNDSTÜCKSNUMMER	EINLAGEZAHL	KATASTRALGEMEINDE
1526 / 2	894	INNERE STADT
PLANINHALT		

ERDGESCHOSS, SCHNITT, ANSICHT, LAGEPLAN

LEGENDE	ST.LI. TÜREN	ST.LI. FENSTER	BODENBELÄGE
BAUSTOFFE	EINGANG	HAUPTFENSTER	ZIMMER
NEUBAU (ALLGEM.)	ZIMMER		SAN RME
STAHLBETON	SAN RME		NEBENRME
STAMPFBETON	NEBENRÄUME		GANG
MAUERWERK	GANG FLUR	NEBENFENSTER	TERR LOGGIA
VOLLZIEGEL F90	TERR LOGGIA		GARAGE
HOLZ	SCHLEUSE T30		TECHNIKRME
	MASCHRM. T30		SCHLEUSEN
	GESCH. LOKAL		BÜROS
WÄRMEDÄMMUNG			LAGER
LFTGS. SCHACHT F90/Aφ100			
BESTAND			
ABBRUCH			
BAUWERBER	GRUNDEIGENTUMER	BAUFÜHRER	

IMMO-CONTRACT
MAKLERGESELLSCHAFT ALBA
A-1100 WIEN / LANDESGERICHTSSTRASSE 6

Georg Neubauer Ges.m.b.H.
Immobilienhändler
1120 Wien, Schönbrunnstr. 287
Telefon: 815 12 81, 813 14 01
KOMRAT GEORGIENBAUER
GESCHÄFTS-UNTER

14.3.95
"ADRIA WORLD" Handel mit
Wassersportartikeln GmbH.
ADRIA WORLD
HABSGASSE 1
1120 WIEN / SINGULIERGASSE 305
TEL. 06659194778

PLANVERFASSER		ARCHITEKT, DIPL.-ING.	
GERHARD STEFFEL		GERHARD STEFFEL	
Staatlich geprüfter und beeideter Ziviltechniker Techn. Rat		Staatlich geprüfter und beeideter Ziviltechniker Techn. Rat	
Pöschel Auenberg 1080 Wien Tel. (0222) 42 76 71 Δ Fax 42 76 71/22		Pöschel Auenberg 1080 Wien Tel. (0222) 42 76 71 Δ Fax 42 76 71/22	
MASSTAB	FORMAT	PROJ.-BEZ./NR./PLANNR.:	ZEICHNER (IN) DATUM
1:100	75 x 29 cm	10820	R. 3 07.11.1994