




DIPL. ING. ANDRZEJ GLOGOWSKI

STAATLICH BEFUGTER UND BEEIDETER ZIVILINGENIEUR FÜR BAUWESEN

1230 WIEN, OTHELLOG. 1/7/19

TEL / FAX: 61 53 993

EMAIL: dipl.ing.glogowski@teleweb.at

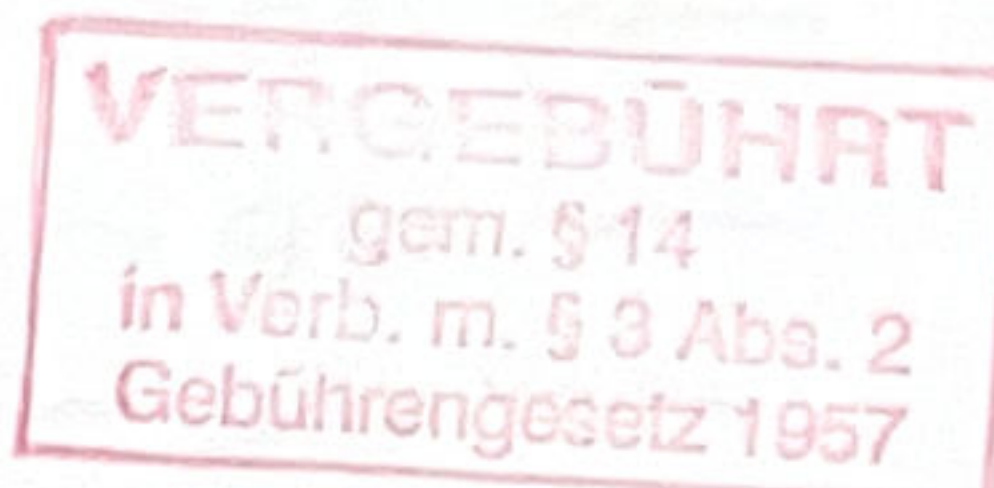


STATISCHE VORBEMESSUNG

FÜR DAS BAUVORHABEN

Gilt nicht als Ausführungsstatik

Dachgeschoßbausbau

Landesgerichtsstr.6, 1010 Wien

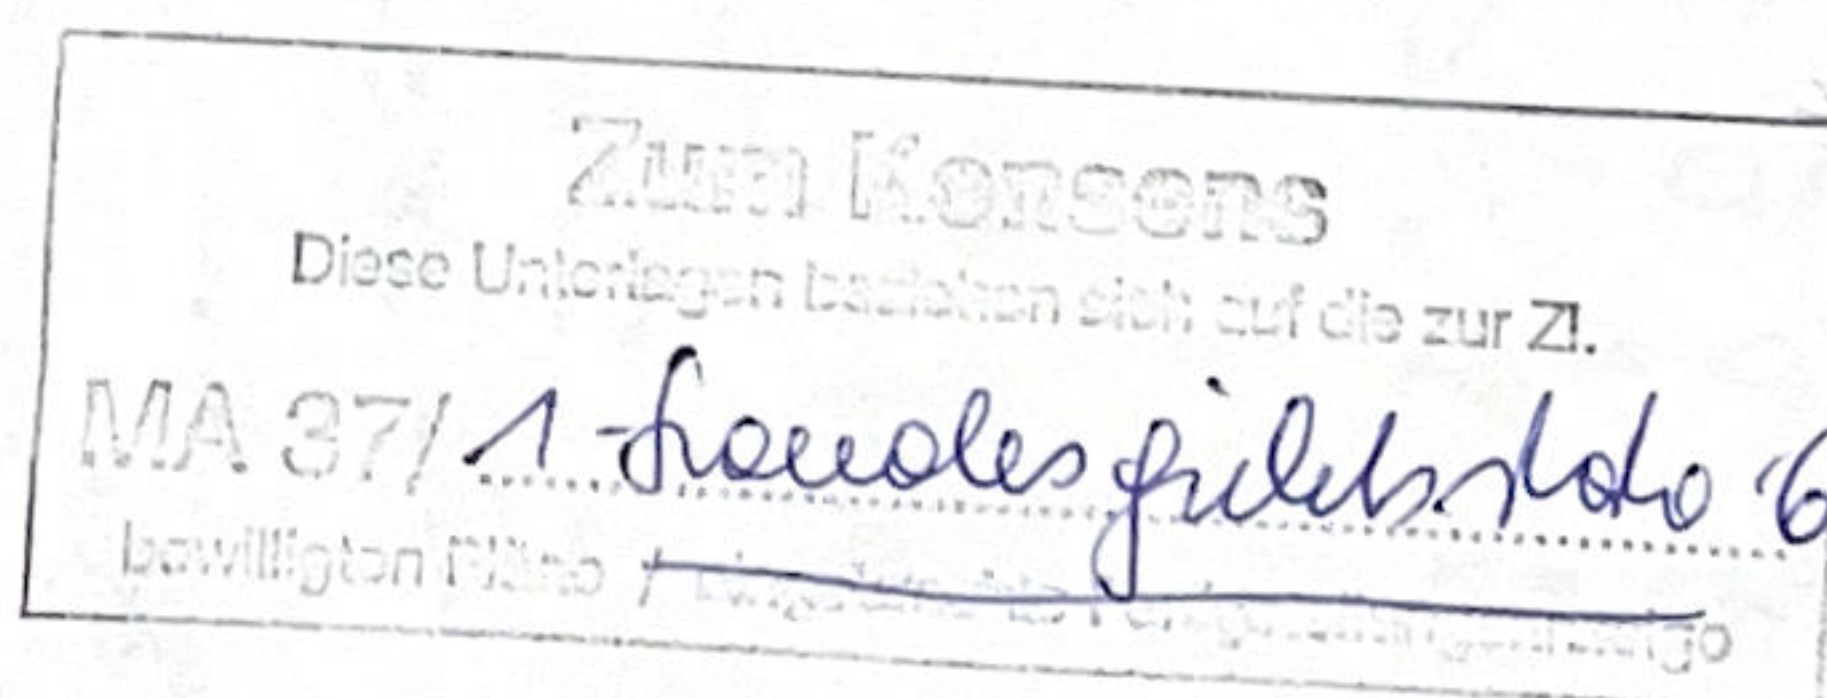

GZ: 2004/33

Statik Seiten: 1-23

Wien, im Mai 2004



RECHNUNG DER VERLUSTE

1. VERLUSTE AN DER ZUGABE

1.1 VERLUSTE AN DER ZUGABE

- 1.1.1 VERLUST AN DER ZUGABE
- 1.1.2 VERLUST AN DER ZUGABE
- 1.1.3 VERLUST AN DER ZUGABE
- 1.1.4 VERLUST AN DER ZUGABE

- ~ 0,5 kg/m²
- ~ 0,5 kg/m²
- ~ 0,5 kg/m²
- ~ 0,5 kg/m²

- 1.1.5 VERLUST AN DER ZUGABE
- 1.1.6 VERLUST AN DER ZUGABE
- 1.1.7 VERLUST AN DER ZUGABE

- g = 1,30 kg/m²
- g₁ = 1,34 kg/m²
- s₁ = 0,35 kg/m²
- s₂ = 0,35 kg/m²

1.2 VERLUSTE AN DER ZUGABE

- 1.2.1 VERLUST AN DER ZUGABE
- 1.2.2 VERLUST AN DER ZUGABE
- 1.2.3 VERLUST AN DER ZUGABE
- 1.2.4 VERLUST AN DER ZUGABE

- ~ 0,5 kg/m²
- ~ 0,5 kg/m²
- ~ 0,5 kg/m²
- ~ 0,5 kg/m²

- g = 0,85 kg/m²
- s₁ = 0,85 kg/m²
- s₂ = 0,85 kg/m²
- s₃ = 0,85 kg/m²

- 1.2.5 VERLUST AN DER ZUGABE
- 1.2.6 VERLUST AN DER ZUGABE
- 1.2.7 VERLUST AN DER ZUGABE

EINRECHENPLAN ÜBER DIE UMWIDMUNG IM 2. STUCK TL LANDESGERICHT WIEN

BEZUGSNUMMER: 1526/2
BAUVERFAHREN

Zuständigkeitsbereich der Hauptverteilung von Wien
und den Ländern Österreich
Landesgericht: 5
1010 Wien

GRUNDEIGENTUMER

Zuständigkeitsbereich der Hauptverteilung von Wien
und den Ländern Österreich
Landesgericht: 5
1010 Wien

PLANVERFAHREN

Architekt: Dipl.-Ing. JOSEF WOLFGANG
MILLERSTRASSE 21, 1060 WIEN
Tel: 5971358 Fax: 5932400

DATUM: 1. PLAN

September 2004

BEHÖRDE



BEZUGSNUMMER: 1526/2
BAUVERFAHREN

Zuständigkeitsbereich der Hauptverteilung von Wien
und den Ländern Österreich
Landesgericht: 5
1010 Wien

GRUNDEIGENTUMER

Zuständigkeitsbereich der Hauptverteilung von Wien
und den Ländern Österreich
Landesgericht: 5
1010 Wien

PLANVERFAHREN

Architekt: Dipl.-Ing. JOSEF WOLFGANG
MILLERSTRASSE 21, 1060 WIEN
Tel: 5971358 Fax: 5932400

DATUM: 1. PLAN

September 2004

BEHÖRDE



EINRECHENPLAN

ÜBER DIE UMWIDMUNG IM 2. STUCK TL LANDESGERICHT WIEN

BEZUGSNUMMER: 1526/2
BAUVERFAHREN

Zuständigkeitsbereich der Hauptverteilung von Wien
und den Ländern Österreich
Landesgericht: 5
1010 Wien

GRUNDEIGENTUMER

Zuständigkeitsbereich der Hauptverteilung von Wien
und den Ländern Österreich
Landesgericht: 5
1010 Wien

PLANVERFAHREN

Architekt: Dipl.-Ing. JOSEF WOLFGANG
MILLERSTRASSE 21, 1060 WIEN
Tel: 5971358 Fax: 5932400

DATUM: 1. PLAN

September 2004

BEHÖRDE



Magistrat der Stadt Wien
Magistratsabteilung 50
Eingangs-Nr.: 1526/2
Bescheid-Nr.: 1526/2
12.10.2004



1.3. GALERIE

V. BEZAG	$\sim 0,10 \text{ kJ/m}^2$
V. ESTRICH	$\sim 1,70 \text{ --}$
V. HOLZKONSTR.	$\sim 0,80 \text{ --}$
V. AD 2x	$\sim 0,10 \text{ --}$
V. GKF	$\sim 0,30 \text{ --}$
	$g = 2,90 \text{ kJ/m}^2$
	$p = 5,00 \text{ --}$

NL

1.4. DECKE Ü. 40G


V. BEZAG	$\sim 0,10 \text{ kJ/m}^2$
V. ESTRICH 5 cm	$\sim 1,70 \text{ --}$
V. TDP	$\sim 0,10 \text{ --}$
V. STB PL. $d = 20 \text{ cm}$	$\sim 5,00 \text{ --}$
	$g = 6,30 \text{ kJ/m}^2$
	$p = 5,00 \text{ --}$

NL

2. DACHKONSTRUKTION

2.1. PFSEITE Ü. GALERIE

STÄHLRAHMEN

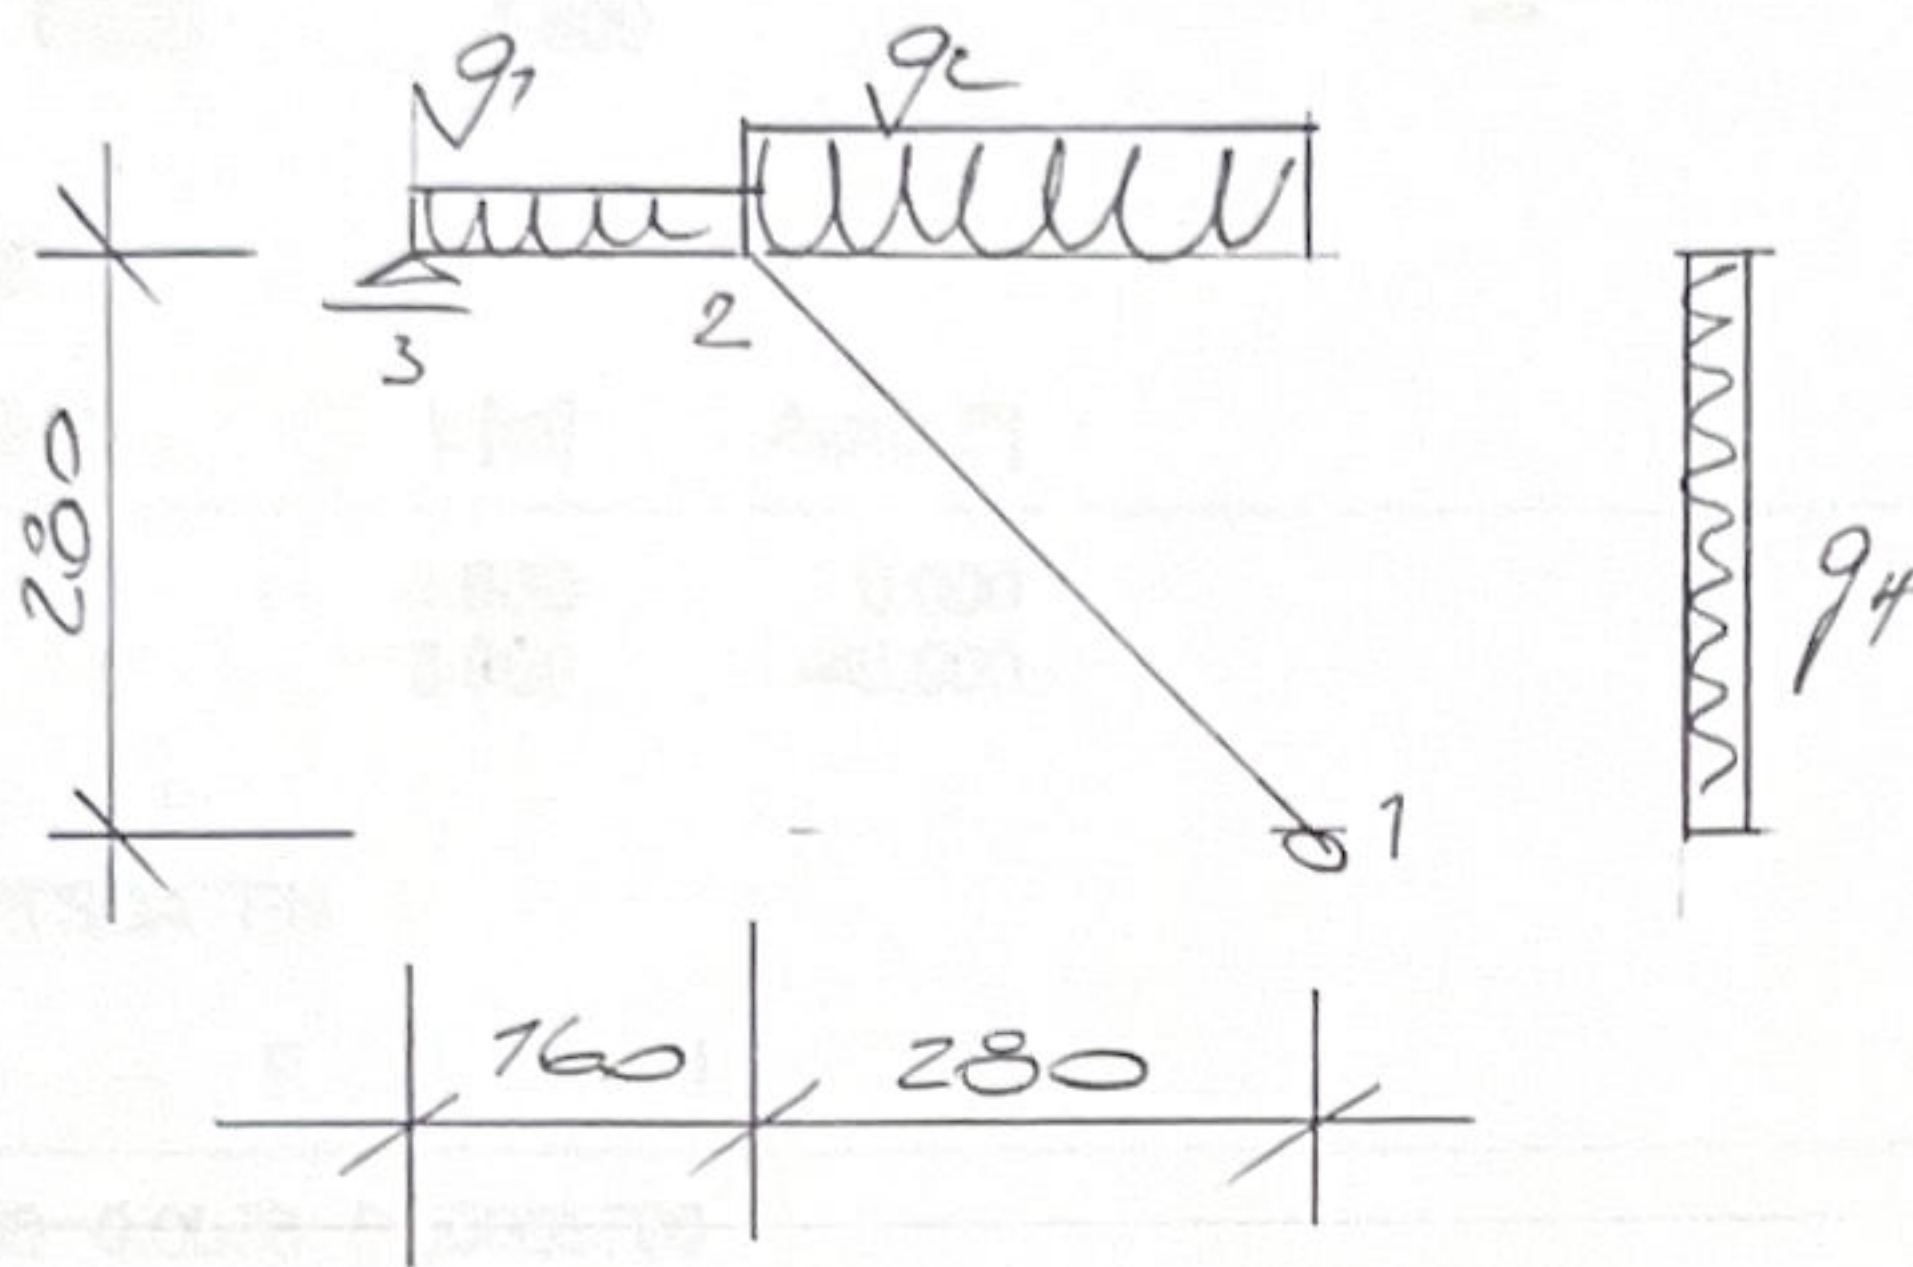

$$q_1 = 0,80 + 0,5 \times 9,0 \times 2,42 = 11,69 \text{ kN/m}$$

$$q_2 = 0,80 + 0,5 \times 9,0 \times 3,00 = 14,30 \text{ kN/m}$$

$$q_4 = 0,78 \times 0,5 \times 9,0 = 3,57 \text{ kN/m}$$

BEMESSUNG S. SEITEN 4-6

SYSTEMDATEN

Anzahl Knoten: 3
Anzahl Stäbe: 2
Bandbreite: 6

KNOTENDATEN

V-Phi, V-y, V-x: leer = frei, *** = gesperrt, sonst Feder

Nr	X	Y	V-Phi [rad/1000]	V-y [mm]	V-x [mm]
1	4.400	0.000		***	***
2	1.600	2.800			
3	0.000	2.800		***	

STABTABELLE

Stab	A-Kn	E-Kn	L [m]	Alpha [°]
1	3	2	1.600	0.000
2	2	1	3.960	-45.000

QUERSCHNITTSDATEN

Nr.	Type	F	I
1	HE-B 200	0.0078	0.00005700

STABDATEN

Stab	E-Modul [kN/m2]	F [m2]	J [m4]	A		E		Q-A	Q-E
				D	V	D	V		
1	2.100000E+008	0.0078	0.00005700					1	1
2	2.100000E+008	0.0078	0.00005700					1	1

LASTFALL 1 - Ständige Last

GLEICHLASTEN

Stab	P-y [kN/m]	P-x [kN/m]	Type
1	-11.7	0.0	global
2	-10.1	-2.5	global

KNOTENVERFORMUNGEN

Nr	V-Phi [rad/1000]	V-y [mm]	V-x [mm]
1	6.6	0.0	0.0
2	-3.0	-7.6	-7.6
3	-5.7	0.0	-7.6

LASTFALL 1 - Ständige Last

KNOTENVERFORMUNGEN

Nr	V-Phi [rad/1000]	V-y [mm]	V-x [mm]
Min	-5.7	-7.6	-7.6
Max	6.6	0.0	0.0

STABVERFORMUNGEN

Stab		V-Phi [rad/1000]	V-y [mm]	V-x [mm]
1	0	-5.7	0.0	-7.6
	1	-5.7	-0.9	-7.6
	2	-5.6	-1.8	-7.6
	3	-5.4	-2.7	-7.6
	4	-5.2	-3.5	-7.6
	5	-5.0	-4.4	-7.6
	6	-4.7	-5.1	-7.6
	7	-4.3	-5.9	-7.6
	8	-3.9	-6.5	-7.6
	9	-3.5	-7.1	-7.6
2	10	-3.0	-7.6	-7.6
	0	-3.0	-7.6	-7.6
	1	-1.8	-8.3	-8.3
	2	-0.6	-8.7	-8.6
	3	0.7	-8.6	-8.6
	4	2.0	-8.3	-8.2
	5	3.2	-7.5	-7.5
	6	4.3	-6.5	-6.5
	7	5.2	-5.1	-5.1
	8	5.9	-3.6	-3.6
	9	6.4	-1.8	-1.8
	10	6.6	0.0	0.0
Min		-5.7	-8.7	-8.6
Max		6.6	0.0	0.0

SCHNITTKRÄFTE [kN]

Stab		M	Q	N	M	Q	N
1	0	-0.0	31.2	-0.0			
	1	4.8	29.3	0.0			
	2	9.4	27.4	0.0			
	3	13.6	25.5	0.0			
	4	17.5	23.7	0.0			
	5	21.2	21.8	0.0			
	6	24.5	19.9	0.0			
	7	27.6	18.1	0.0			
	8	30.3	16.2	0.0			
	9	32.7	14.3	0.0			
2	10	34.9	12.4	0.0			
	0	34.9	8.8	8.8			
	1	37.7	5.3	6.7			
	2	39.1	1.8	4.5			

LASTFALL 1 - Ständige Last

SCHNITTKRÄFTE [kN]

Stab	M	Q	N	M	Q	N
3	39.1	-1.8	2.4			
4	37.7	-5.3	0.3			
5	34.9	-8.8	-1.9			
6	30.7	-12.3	-4.0			
7	25.1	-15.9	-6.1			
8	18.1	-19.4	-8.3			
9	9.8	-22.9	-10.4			
10	0.0	-26.4	-12.5			
Min	-0.0	-26.4	-12.5			
Max	39.1	31.2	8.8			

$C_{long} = \frac{39.100.00}{\sqrt{70}} = 68600 \frac{N}{a^2}$

C_{G200}


AUFLAGERREAKTIONEN

Nr	M [kNm]	P-y [kN]	P-x [kN]
1	0.0	27.5	9.8
3	0.0	31.2	0.0
Summe	-0.0	58.7	9.8
Min	0.0	27.5	0.0
Max	0.0	31.2	9.8

Lastsumme Y: -58.7
X: -9.8

2.2. STRASSENSCHÜTTE

STÄHLRAHMEN

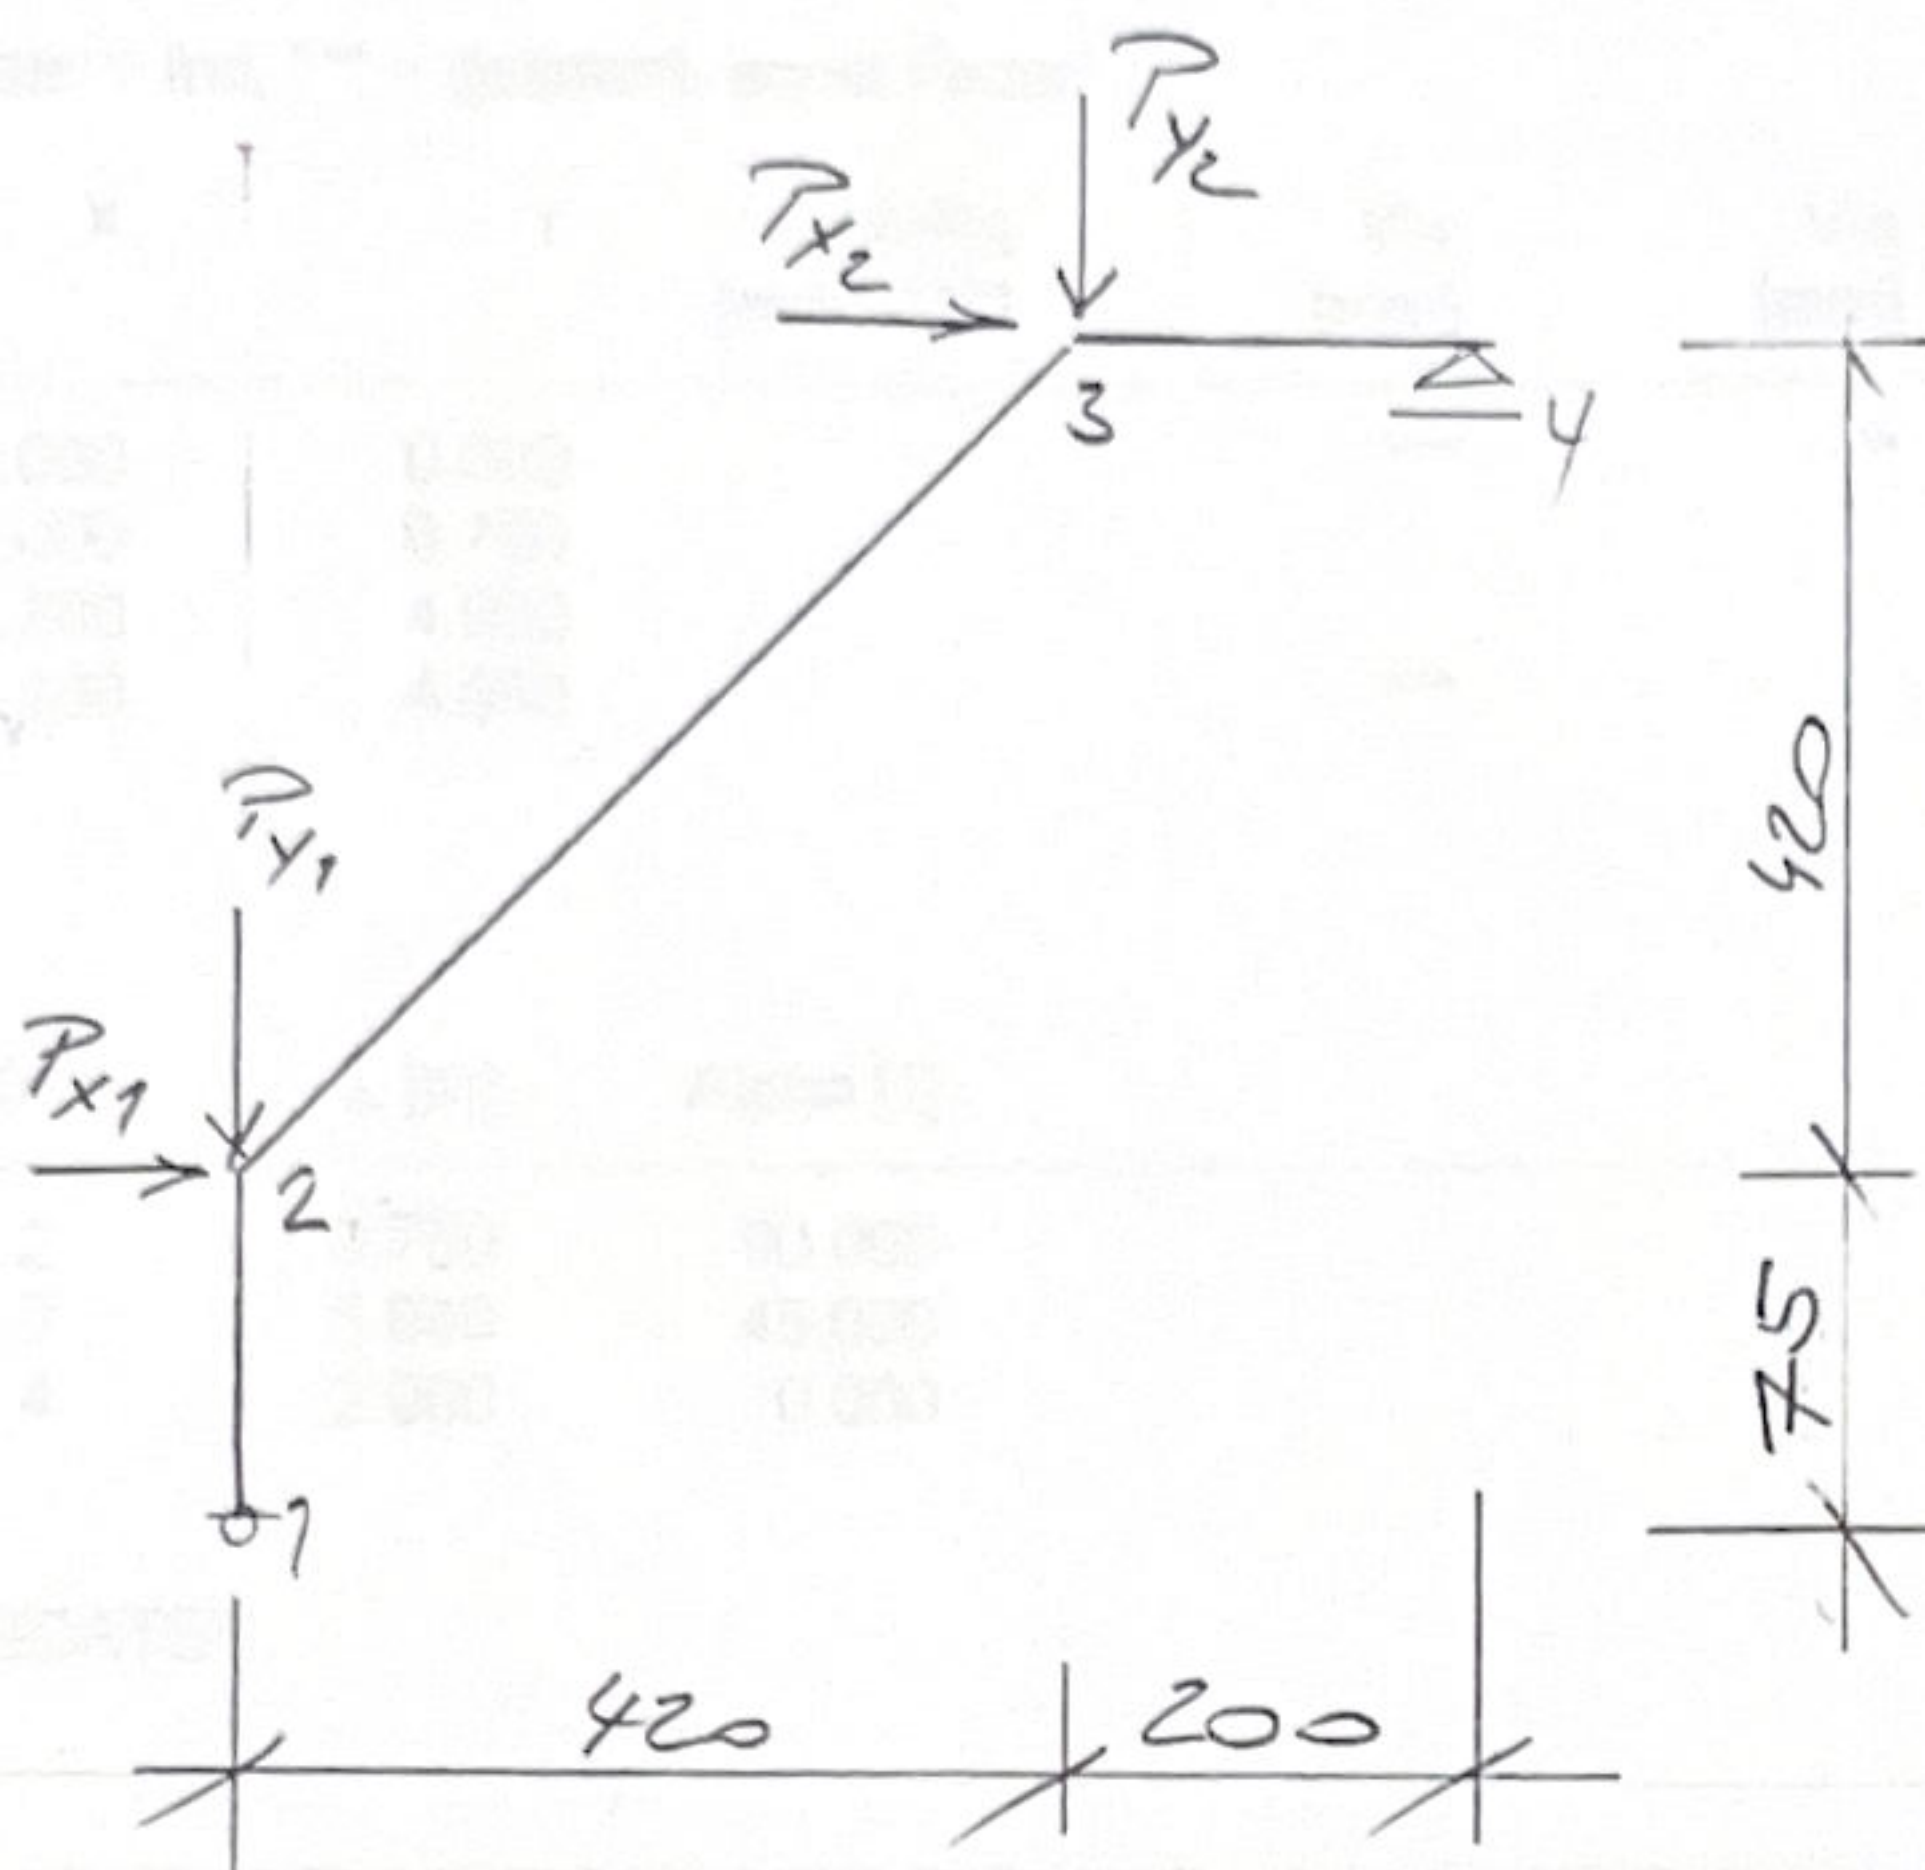

$$P_{x1} = 0,5 \times (0,75 + 4,20) \times 0,5 \times 6,0 \times 0,78 = 5,79 \text{ kN}$$

$$P_{y1} = 0,5 \times 6,0 \times 0,5 \times 4,20 \times 3,92 = 95,25 \text{ kN}$$

$$P_{x2} = 0,5 \times 4,20 \times 0,5 \times 6,0 \times 0,78 = 4,91 \text{ kN}$$

$$P_{y2} = 0,5 \times 6,0 \times 0,5 \times (20 \times 3,0 + 4,20 \times 3,92) = 24,25 \text{ kN}$$

BEMESSUNG S. SEITEN 8-10

SYSTEMDATEN

Anzahl Knoten: 4
Anzahl Stäbe: 3
Bandbreite: 6

KNOTENDATEN

V-Phi, V-y, V-x: leer = frei, *** = gesperrt, sonst Feder

Nr	X	Y	V-Phi [rad/1000]	V-y [mm]	V-x [mm]
1	0.000	0.000		***	***
2	0.000	0.750			
3	4.200	4.950			
4	6.200	4.950		***	

STABTABELLE

Stab	A-Kn	E-Kn	L [m]	Alpha [°]
1	1	2	0.750	90.000
2	2	3	5.940	45.000
3	3	4	2.000	0.000

QUERSCHNITTSDATEN

Nr.	Type	F	I
1	HE-B 240	0.0106	0.00011260

STABDATEN

Stab	E-Modul [kN/m2]	F [m2]	J [m4]	A			E			Q-A	Q-E
				D	V	H	D	V	H		
1	2.100000E+008	0.0106	0.00011260							1	1
2	2.100000E+008	0.0106	0.00011260							1	1
3	2.100000E+008	0.0106	0.00011260							1	1

LASTFALL 1 - Ständige Last

KNOTENLASTEN

KNr	M [kNm]	P-y [kN]	P-x [kN]
2	0.0	-15.3	5.8
3	0.0	-24.3	4.9

TFALL 1 - Ständige Last

STÄNDIGE LASTENVERFORMUNGEN

Nr	V-Phi [rad/1000]	V-y [mm]	V-x [mm]
1	-4.2	0.0	0.0
2	-4.1	-0.0	3.1
3	2.2	-6.8	9.9
4	4.0	0.0	9.9
	-4.2	-6.8	0.0
x	4.0	0.0	9.9

ABVERFORMUNGEN

tab		V-Phi [rad/1000]	V-y [mm]	V-x [mm]
1	0	-4.2	0.0	0.0
	1	-4.2	-0.0	0.3
	2	-4.2	-0.0	0.6
	3	-4.2	-0.0	0.9
	4	-4.2	-0.0	1.3
	5	-4.2	-0.0	1.6
	6	-4.1	-0.0	1.9
	7	-4.1	-0.0	2.2
	8	-4.1	-0.0	2.5
	9	-4.1	-0.0	2.8
2	10	-4.1	-0.0	3.1
	0	-4.1	-0.0	3.1
	1	-3.8	-1.7	4.8
	2	-3.5	-3.2	6.3
	3	-3.1	-4.6	7.7
	4	-2.6	-5.8	8.9
	5	-2.0	-6.7	9.8
	6	-1.3	-7.4	10.5
	7	-0.6	-7.8	10.9
	8	0.3	-7.9	11.0
3	9	1.2	-7.6	10.7
	10	2.2	-6.8	9.9
	0	2.2	-6.8	9.9
	1	2.6	-6.4	9.9
	2	2.9	-5.8	9.9
	3	3.1	-5.2	9.9
	4	3.4	-4.6	9.9
	5	3.6	-3.9	9.9
	6	3.7	-3.1	9.9
	7	3.9	-2.4	9.9
Min	8	3.9	-1.6	9.9
	9	4.0	-0.8	9.9
	10	4.0	0.0	9.9
Min		-4.2	-7.9	0.3
Max		4.0	0.0	11.0

LASTFALL 1 - Ständige Last

SCHNITTKRÄFTE [kN]

Stab		M	Q	N	M	Q	N
1	0	0.0	10.7	-18.5			
	1	0.8	10.7	-18.5			
	2	1.6	10.7	-18.5			
	3	2.4	10.7	-18.5			
	4	3.2	10.7	-18.5			
	5	4.0	10.7	-18.5			
	6	4.8	10.7	-18.5			
	7	5.6	10.7	-18.5			
	8	6.4	10.7	-18.5			
	9	7.2	10.7	-18.5			
2	10	8.0	10.7	-18.5			
	0	8.0	5.7	1.2			
	1	11.4	5.7	1.2			
	2	14.8	5.7	1.2			
	3	18.2	5.7	1.2			
	4	21.7	5.7	1.2			
	5	25.1	5.7	1.2			
	6	28.5	5.7	1.2			
	7	31.9	5.7	1.2			
	8	35.3	5.7	1.2			
3	9	38.7	5.7	1.2			
	10	42.1	5.7	1.2			
	0	42.1	-21.0	0.0			
	1	37.9	-21.0	0.0			
	2	33.7	-21.0	-0.0			
	3	29.5	-21.0	0.0			
	4	25.3	-21.0	0.0			
	5	21.0	-21.0	0.0			
	6	16.8	-21.0	0.0			
	7	12.6	-21.0	0.0			
	8	8.4	-21.0	0.0			
	9	4.2	-21.0	0.0			
	10	-0.0	-21.0	0.0			
Min		-0.0	-21.0	-18.5			
Max		42.1	10.7	1.2			


$$\sigma_{crk4} = \frac{4210000}{923} =$$

$$= 4536 \text{ N/cm}^2 < \sigma_{crk}$$

AUFLAGERREAKTIONEN

Nr	M [kNm]	P-y [kN]	P-x [kN]
1	-0.0	18.5	-10.7
4	-0.0	21.0	0.0
Summe	0.0	39.5	-10.7
Min	-0.0	18.5	-10.7
Max	-0.0	21.0	0.0
Lastsumme		Y: -39.5	X: 10.7

2.3. HOFSTÜTZE Ü. DG

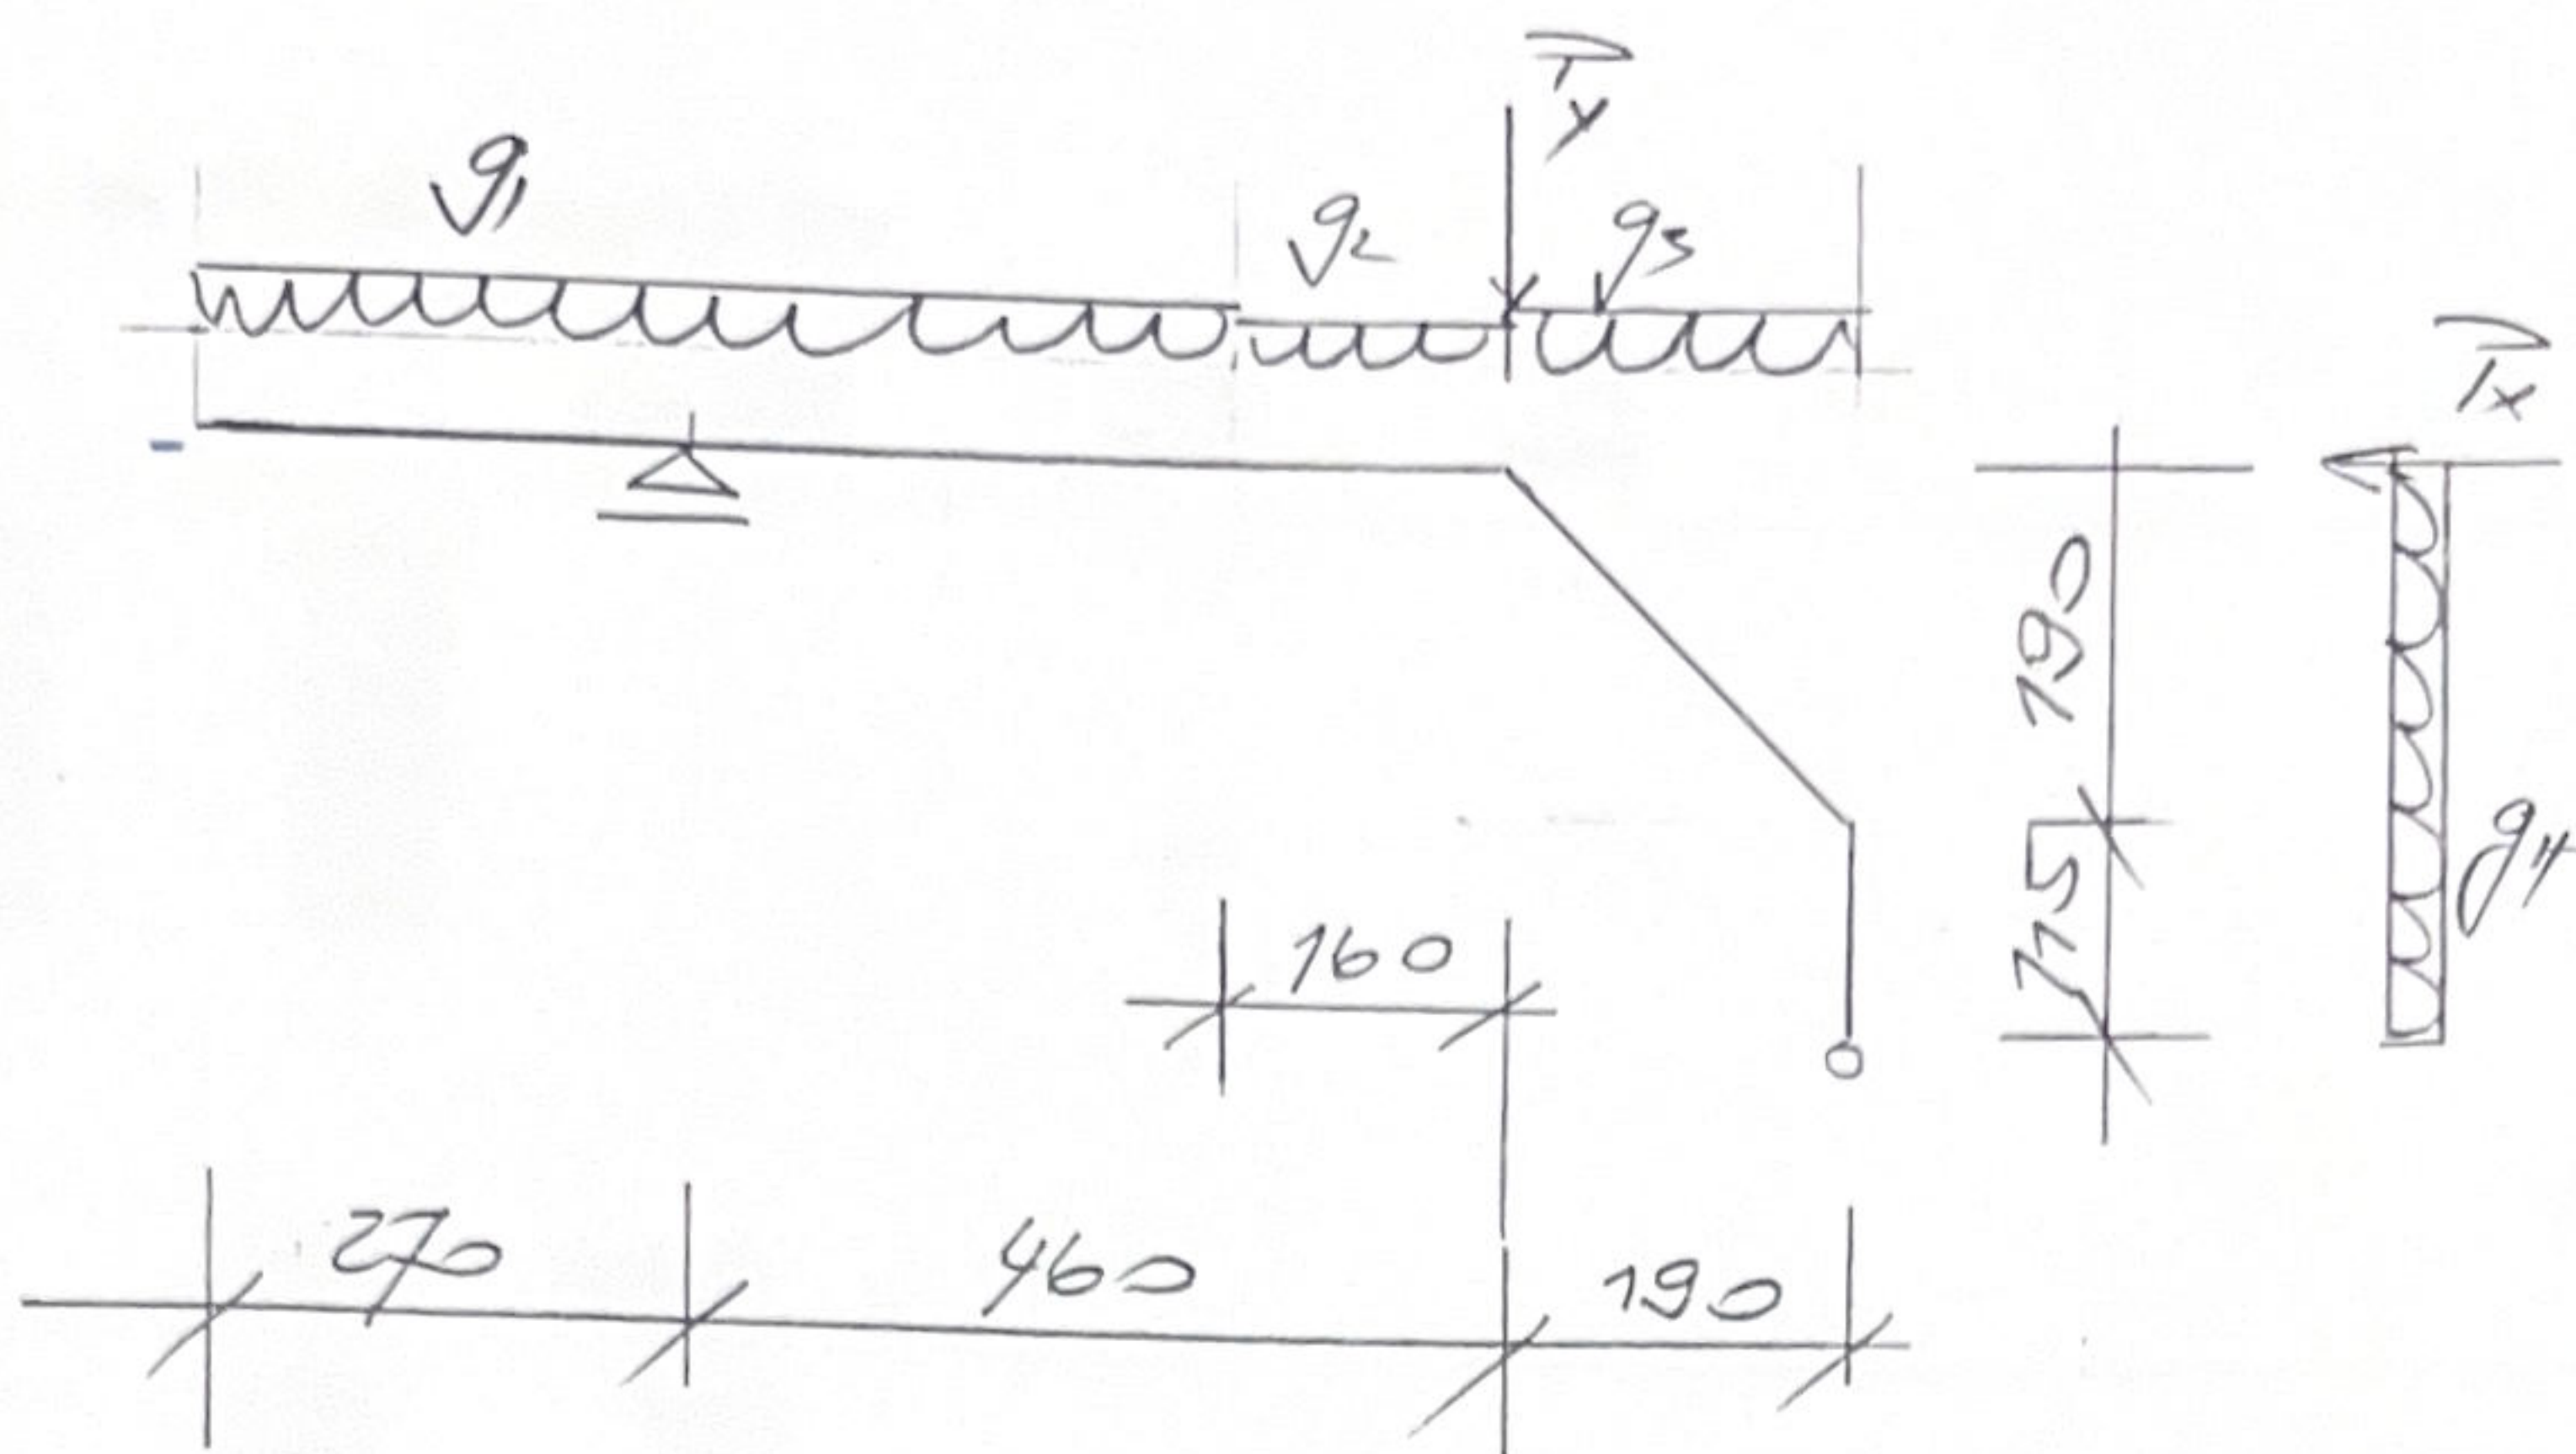

$$q_1 = 0,50 \times 9,0 \times 7,40 + 0,80 = 34,10 \text{ kN/m}$$

$$q_2 = 0,5 \times 9,0 \times 2,40 + 0,80 = 11,60 \text{ kN}$$

$$q_3 = 0,5 \times 9,0 \times 3,00 + 0,80 = 14,30 \text{ kN}$$

$$T_y = 27,5 \text{ kN}$$

$$T_x = 9,8 \text{ kN}$$

$$q_4 = 0,78 \times 0,5 \times 9,0 = 3,57 \text{ kN/m}$$

BEMESSUNG S. SEITEN 12-15

SYSTEMDATEN

Anzahl Knoten: 6
Anzahl Stäbe: 5
Bandbreite: 6

KNOTENDATEN

V-Phi, V-y, V-x: leer = frei, *** = gesperrt, sonst Feder

Nr	X	Y	V-Phi [rad/1000]	V-y [mm]	V-x [mm]
1	9.200	0.000		***	***
2	9.200	1.150			
3	7.300	3.050			
4	5.700	3.050			
5	2.700	3.050		***	
6	0.000	3.050			

STABTABELLE

Stab	A-Kn	E-Kn	L [m]	Alpha [°]
1	6	5	2.700	0.000
2	5	4	3.000	0.000
3	4	3	1.600	0.000
4	3	2	2.687	-45.000
5	2	1	1.150	-90.000

QUERSCHNITTSDATEN

Nr.	Type	F	I
1	HE-B 240	0.0106	0.00011260

STABDATEN

Stab	E-Modul [kN/m2]	F [m2]	J [m4]	A			E			Q-A	Q-E
				D	V	H	D	V	H		
1	2.100000E+008	0.0106	0.00011260							1	1
2	2.100000E+008	0.0106	0.00011260							1	1
3	2.100000E+008	0.0106	0.00011260							1	1
4	2.100000E+008	0.0106	0.00011260							1	1
5	2.100000E+008	0.0106	0.00011260							1	1

LASTFALL 1 - Ständige Last

KNOTENLASTEN

KNr	M [kNm]	P-y [kN]	P-x [kN]
3	0.0	-27.5	9.8

LASTFALL 1 - Ständige Last

GLEICHLASTEN

Stab	P-y [kN/m]	P-x [kN/m]	Type
1	-34.1	0.0	global
2	-34.1	0.0	global
3	-11.6	0.0	global
4	-10.1	2.5	global
5	0.0	3.5	global

KNOTENVERFORMUNGEN

Nr	V-Phi [rad/1000]	V-y [mm]	V-x [mm]
1	3.8	0.0	0.0
2	4.3	-0.0	-4.6
3	2.2	-7.6	-12.1
4	-1.5	-8.2	-12.1
5	-0.2	0.0	-12.1
6	4.5	-8.9	-12.1
Min	-1.5	-8.9	-12.1
Max	4.5	0.0	0.0

STABVERFORMUNGEN

Stab		V-Phi [rad/1000]	V-y [mm]	V-x [mm]
1	0	4.5	-8.9	-12.1
	1	4.5	-7.7	-12.1
	2	4.4	-6.5	-12.1
	3	4.4	-5.3	-12.1
	4	4.2	-4.2	-12.1
	5	3.9	-3.1	-12.1
	6	3.5	-2.1	-12.1
	7	2.9	-1.2	-12.1
	8	2.1	-0.5	-12.1
	9	1.0	-0.1	-12.1
2	10	-0.2	0.0	-12.1
	0	-0.2	0.0	-12.1
	1	-1.6	-0.3	-12.1
	2	-2.6	-0.9	-12.1
	3	-3.3	-1.8	-12.1
	4	-3.6	-2.9	-12.1
	5	-3.7	-4.0	-12.1
	6	-3.5	-5.0	-12.1
	7	-3.2	-6.1	-12.1
	8	-2.7	-7.0	-12.1
3	9	-2.1	-7.7	-12.1
	10	-1.5	-8.2	-12.1
	0	-1.5	-8.2	-12.1
	1	-1.1	-8.5	-12.1
	2	-0.8	-8.6	-12.1
	3	-0.4	-8.7	-12.1
	4	0.0	-8.7	-12.1
	5	0.4	-8.7	-12.1

LASTFALL 1 - Ständige Last

STABVERFORMUNGEN

Stab		V-Phi [rad/1000]	V-y [mm]	V-x [mm]
4	6	0.8	-8.6	-12.1
	7	1.1	-8.4	-12.1
	8	1.5	-8.2	-12.1
	9	1.9	-8.0	-12.1
	10	2.2	-7.6	-12.1
	0	2.2	-7.6	-12.1
	1	2.8	-7.1	-11.6
	2	3.3	-6.6	-11.0
	3	3.7	-5.9	-10.4
	4	4.1	-5.2	-9.6
5	5	4.3	-4.4	-8.9
	6	4.5	-3.5	-8.0
	7	4.6	-2.6	-7.2
	8	4.6	-1.8	-6.3
	9	4.5	-0.9	-5.4
	10	4.3	-0.0	-4.6
	0	4.3	-0.0	-4.6
	1	4.2	-0.0	-4.1
	2	4.1	-0.0	-3.6
	3	4.1	-0.0	-3.1
	4	4.0	-0.0	-2.7
	5	3.9	-0.0	-2.2
	6	3.9	-0.0	-1.8
	7	3.8	-0.0	-1.3
	8	3.8	-0.0	-0.9
	9	3.8	-0.0	-0.4
	10	3.8	0.0	0.0
	Min	-3.7	-8.7	-12.1
	Max	4.6	0.0	0.0

SCHNITTKRÄFTE [kN]

Stab		M	Q	N	M	Q	N
1	0	-0.0	0.0	0.0			
	1	-1.2	-9.2	0.0			
	2	-5.0	-18.4	0.0			
	3	-11.2	-27.6	0.0			
	4	-19.9	-36.8	0.0			
	5	-31.1	-46.0	-0.0			
	6	-44.7	-55.2	-0.0			
	7	-60.9	-64.4	-0.0			
	8	-79.5	-73.7	0.0			
	9	-100.7	-82.9	0.0			
2	10	-124.3	-92.1	0.0			
	0	-124.3	110.4	0.0			
	1	-92.7	100.2	0.0			
	2	-64.2	90.0	0.0			
	3	-38.7	79.7	0.0			
	4	-16.3	69.5	0.0			
	5	3.0	59.3	0.0			
	6	19.2	49.0	0.0			
	7	32.4	38.8	0.0			

$$\sigma_{VORH} = \frac{12430000}{920}$$

$$= 13394 \text{ N/cm}^2 < \sigma_{zul}$$

LASTFALL 1 - Ständige Last

SCHNITTKRÄFTE [kN]

Stab		M	Q	N	M	Q	N
3	8	42.5	28.6	-0.0			
	9	49.6	18.4	-0.0			
	10	53.5	8.1	-0.0			
	0	53.5	8.1	0.0			
	1	54.7	6.3	0.0			
	2	55.5	4.4	0.0			
	3	56.1	2.6	-0.0			
	4	56.4	0.7	0.0			
	5	56.3	-1.2	0.0			
	6	56.0	-3.0	0.0			
4	7	55.4	-4.9	-0.0			
	8	54.4	-6.7	-0.0			
	9	53.2	-8.6	0.0			
	10	51.7	-10.4	0.0			
	0	51.7	-19.9	-33.8			
	1	46.1	-21.3	-36.1			
	2	40.2	-22.8	-38.5			
	3	33.9	-24.2	-40.9			
	4	27.2	-25.7	-43.3			
	5	20.1	-27.1	-45.7			
5	6	12.6	-28.6	-48.1			
	7	4.7	-30.0	-50.5			
	8	-3.6	-31.5	-52.9			
	9	-12.2	-32.9	-55.3			
	10	-21.3	-34.4	-57.7			
	0	-21.3	16.5	-65.1			
	1	-19.3	16.9	-65.1			
	2	-17.4	17.3	-65.1			
	3	-15.4	17.7	-65.1			
	4	-13.3	18.1	-65.1			
	5	-11.2	18.5	-65.1			
	6	-9.1	18.9	-65.1			
	7	-6.9	19.3	-65.1			
	8	-4.6	19.7	-65.1			
	9	-2.3	20.1	-65.1			
	10	0.0	20.5	-65.1			
Min		-124.3	-92.1	-65.1			
Max		56.4	110.4	0.0			


AUFLAGERREAKTIONEN

Nr	M [kNm]	P-y [kN]	P-x [kN]
1	0.0	65.1	-20.5
5	-0.0	202.5	0.0
Summe	-0.0	267.6	-20.5
Min	-0.0	65.1	-20.5
Max	0.0	202.5	0.0
Lastsumme	Y:	-267.6	
	X:	20.5	

STÜRE 6/d = 50/20
C 25/30



3. DECKE Ü. 40G

ES WIRD EINE STB PLATTE ÜBER DIE
DIPPERBÄUME AUSGEFÜHRT.

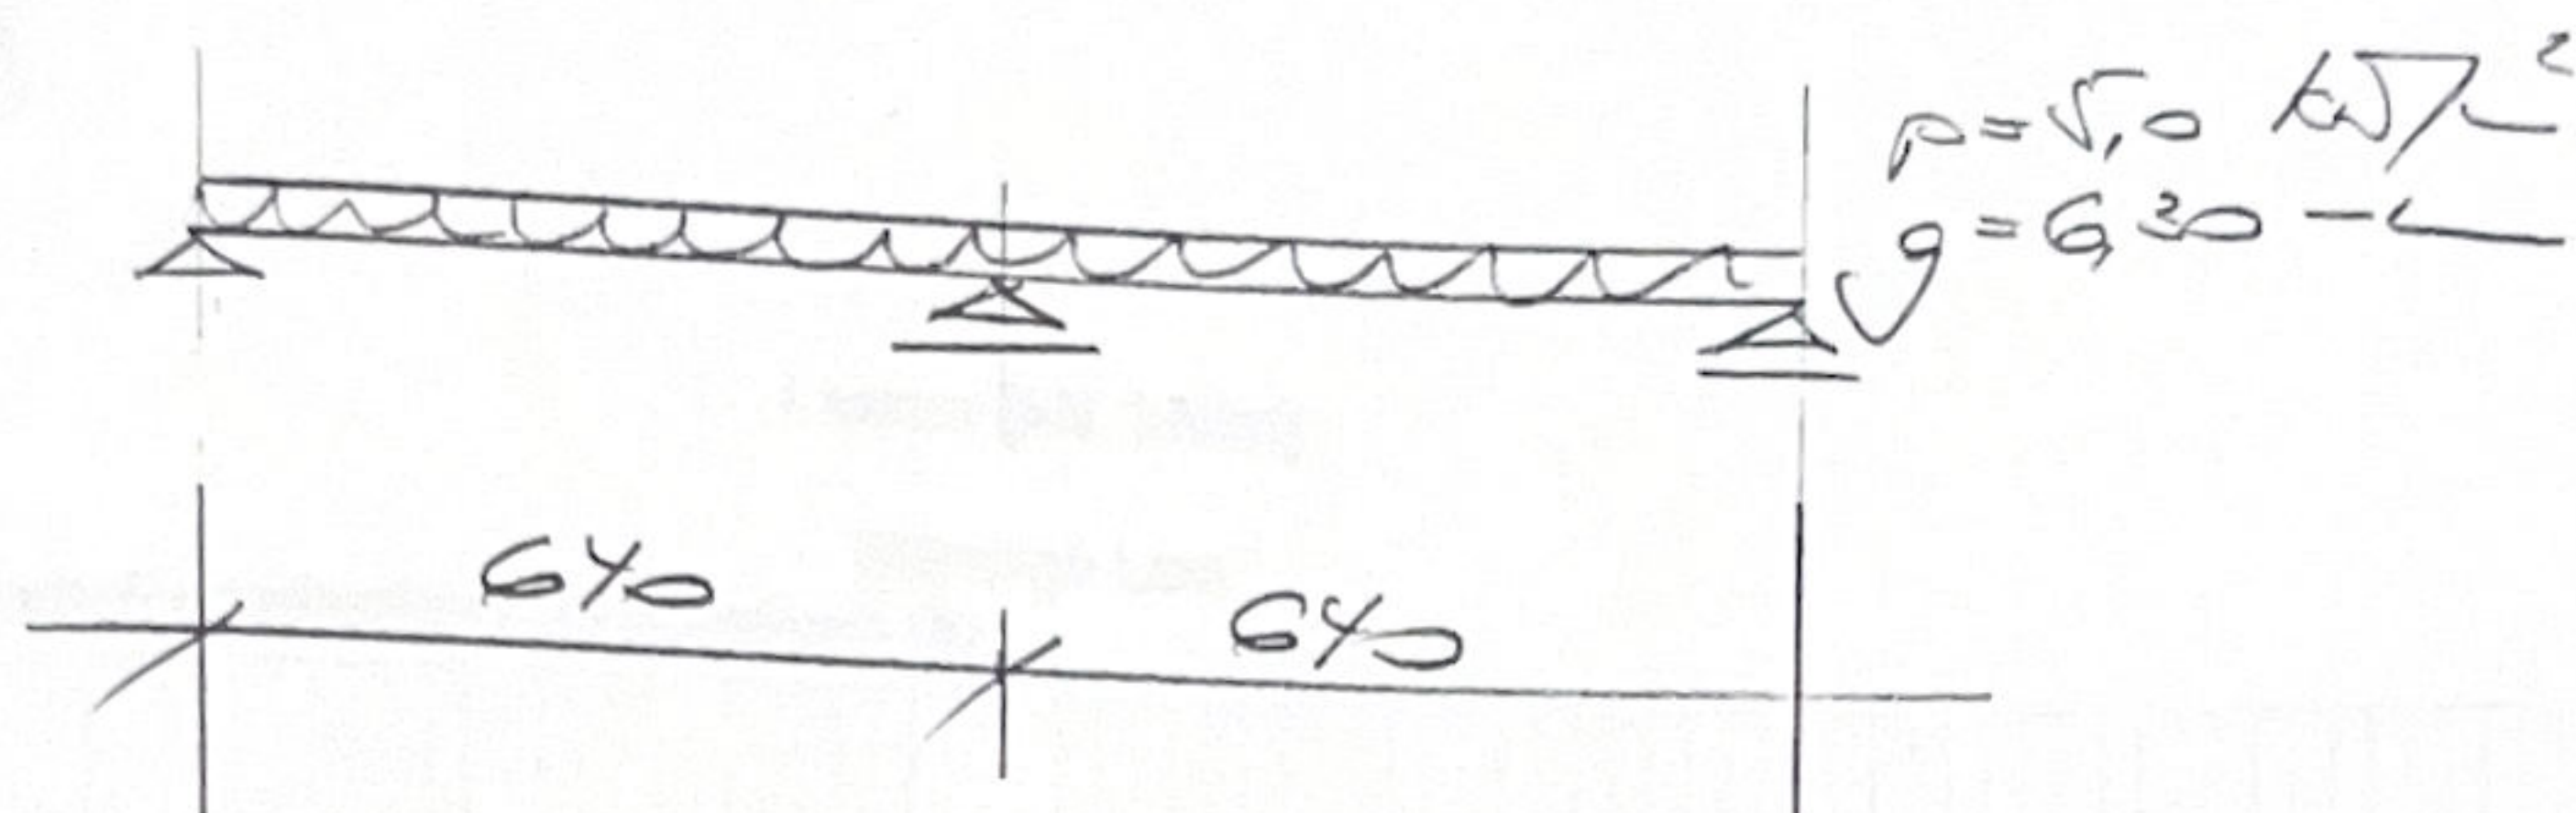


BEWEISUNG S. SEITEN 17-20


Norm: ÖNORM B4700
Beton: C30/37
Stahl: BSt550

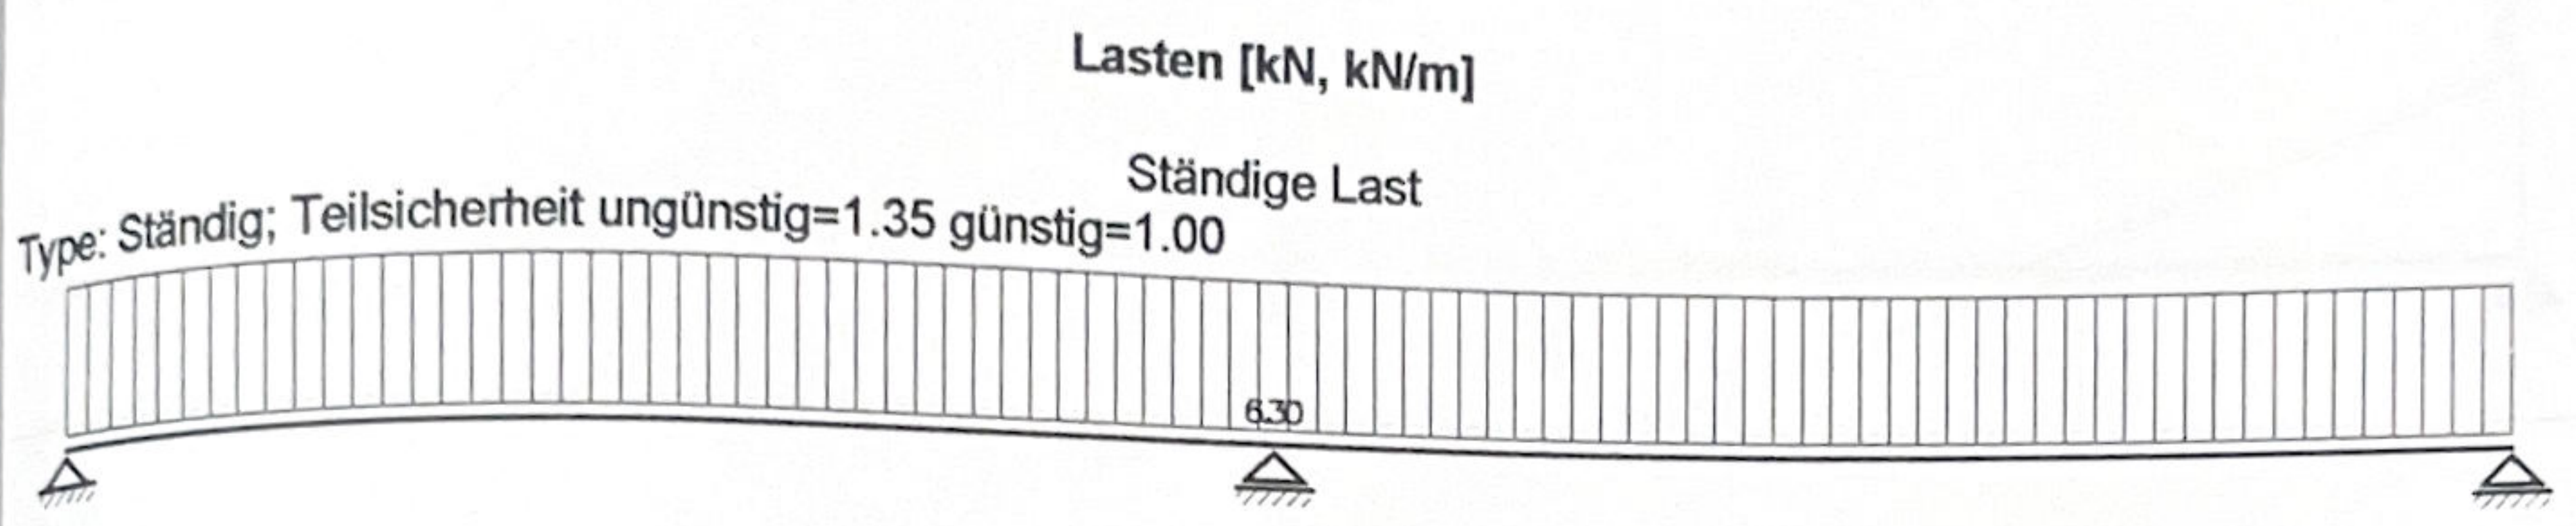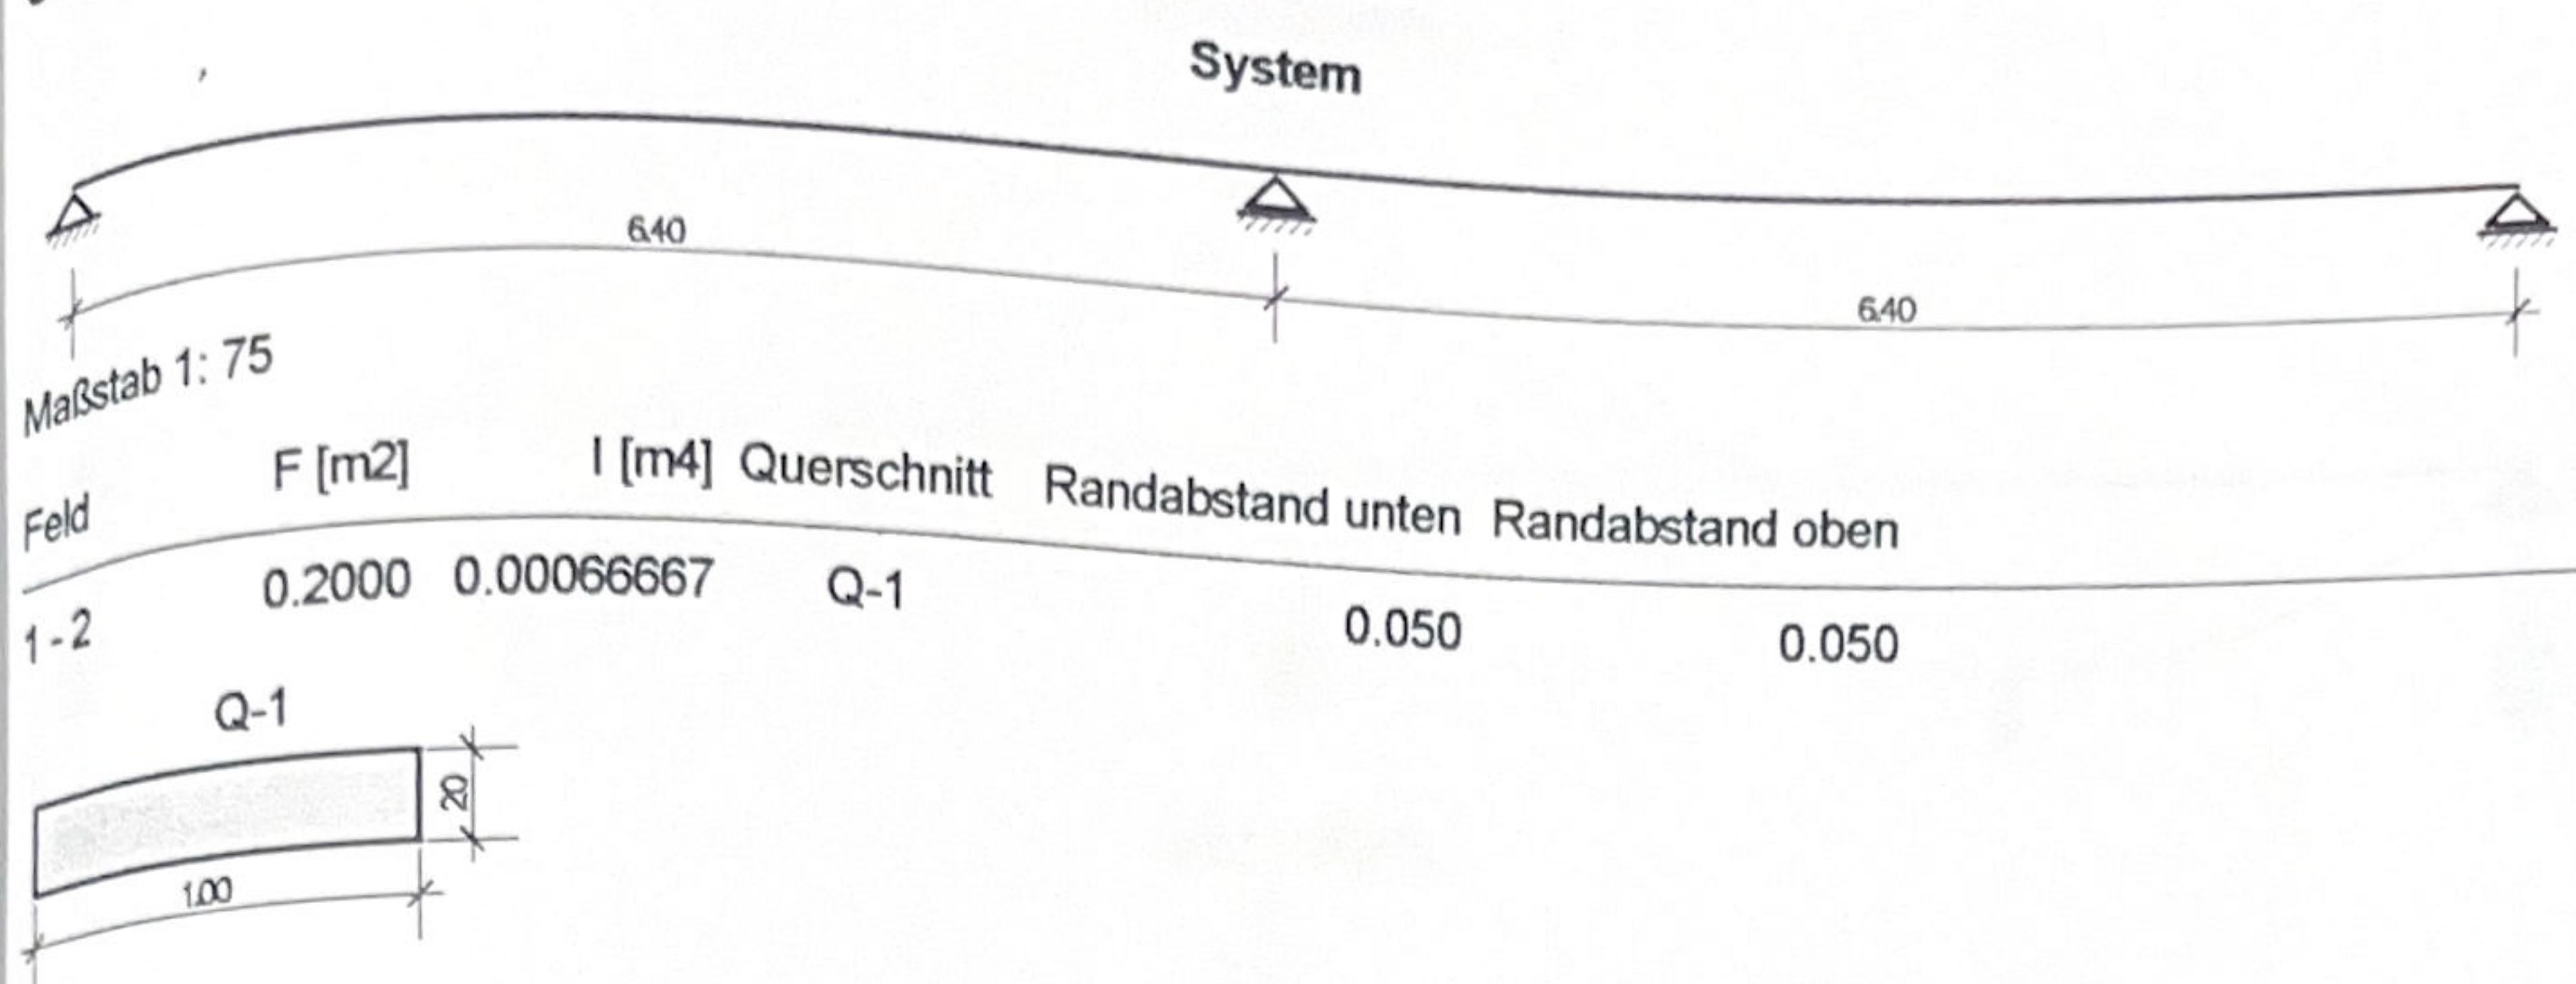

Feld	Abstand	max M	min M	max Q	min Q	max AR	min AR
1	0.00	0.00	0.00	15.12	15.12	15.12	15.12
	2.56	18.06	18.06	-1.01	-1.01		
	6.40	-32.26	-32.26	-25.20	-25.20	50.40	50.40
2	0.00	-32.26	-32.26	25.20	25.20	50.40	50.40
	3.84	18.06	18.06	1.01	1.01		
	6.40	0.00	0.00	-15.12	-15.12	15.12	15.12

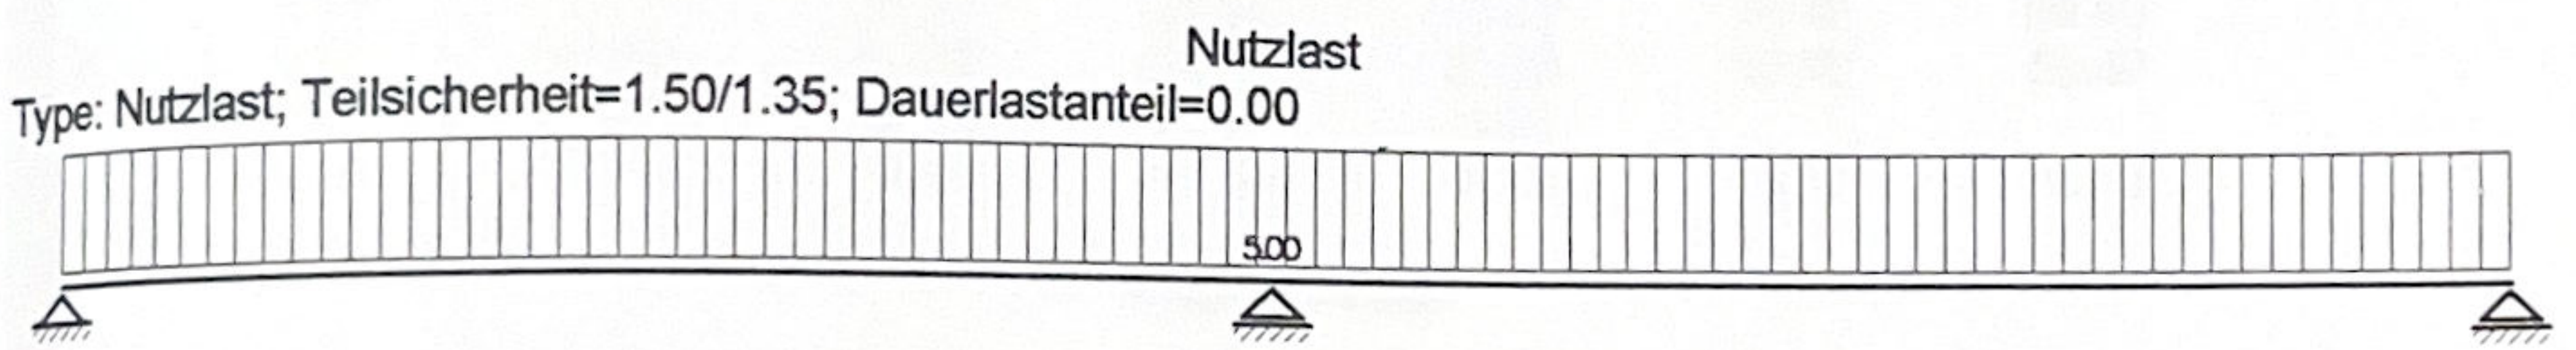


Feld	Abstand	max M	min M	max Q	min Q	max AR	min AR
1	0.00	0.00	0.00	14.00	-2.00	14.00	-2.00
	2.56	19.46	-5.12	1.20	-2.00		
	6.40	0.00	-25.60	0.00	-20.00	40.00	0.00
2	0.00	0.00	-25.60	20.00	0.00	40.00	0.00
	3.84	19.46	-5.12	2.00	-1.20		
	6.40	0.00	0.00	2.00	-14.00	14.00	-2.00

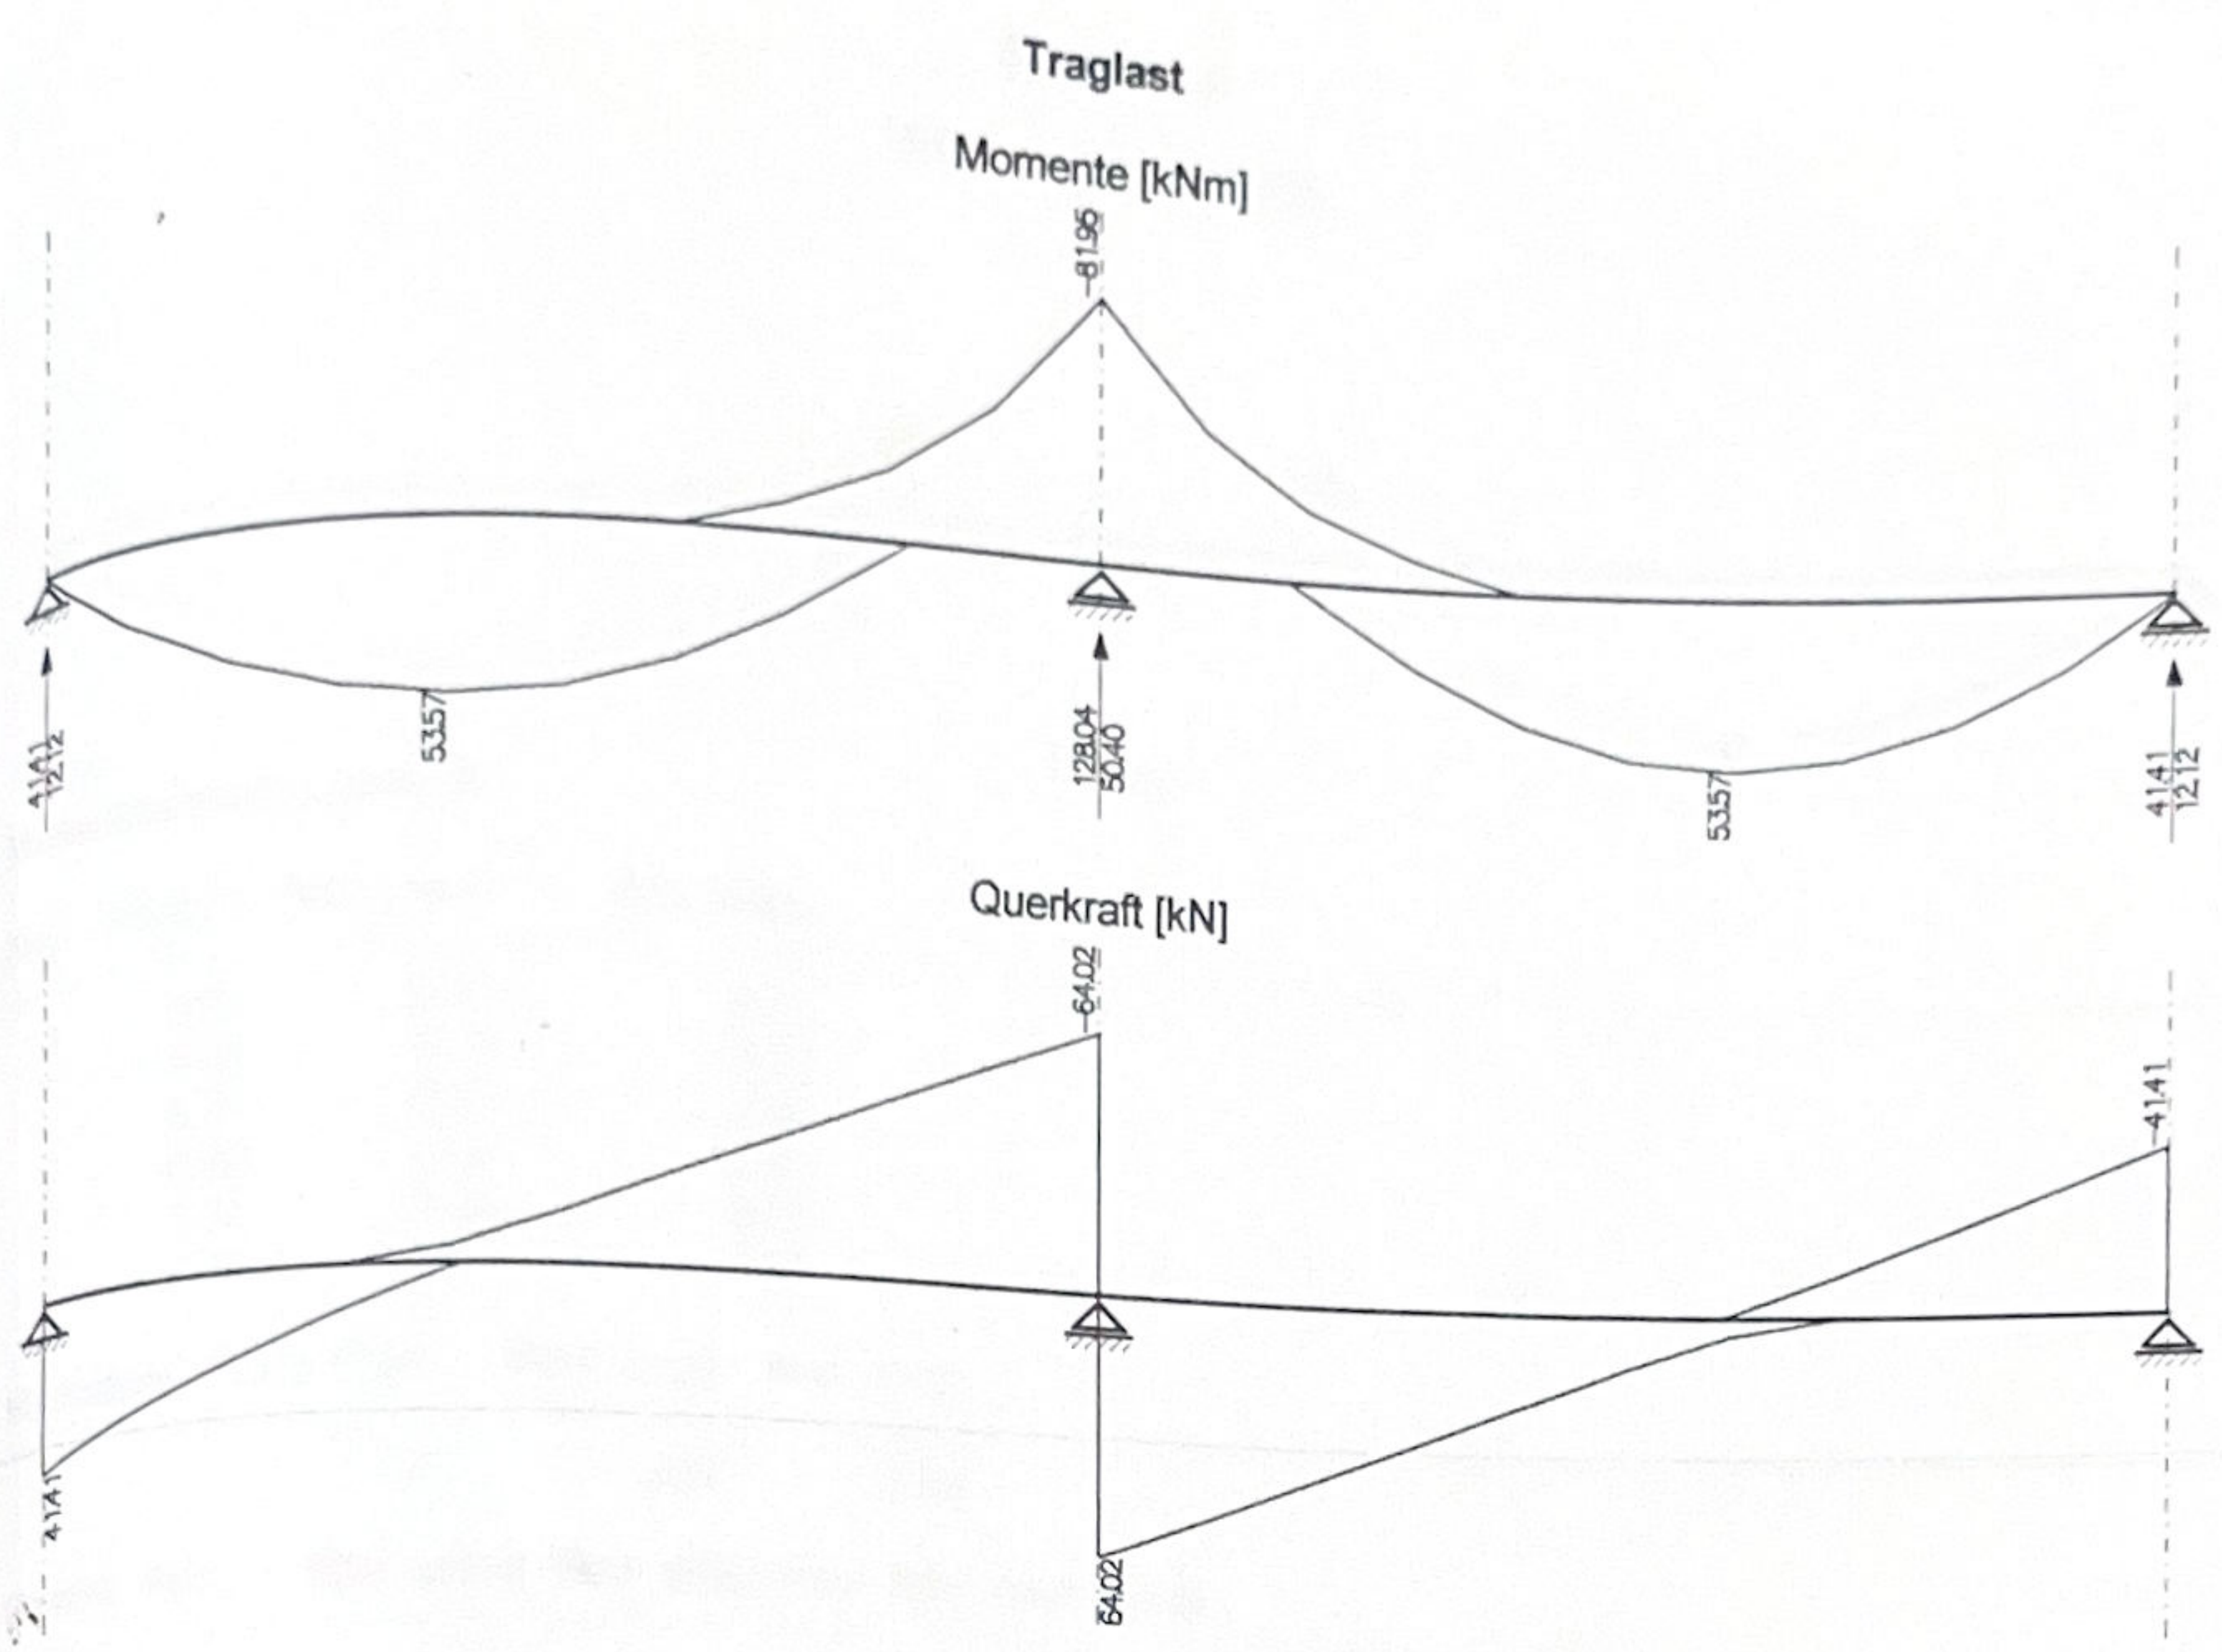

Dauerlast							
Feld	Abstand	max M	min M	max Q	min Q	max AR	min AR
1	0.00	0.00	0.00	15.12	15.12	15.12	15.12
	2.56	18.06	18.06	-1.01	-1.01	15.12	15.12
	6.40	-32.26	-32.26	-25.20	-25.20	50.40	50.40
2	0.00	-32.26	-32.26	25.20	25.20	50.40	50.40
	3.84	18.06	18.06	1.01	1.01	50.40	50.40
	6.40	0.00	0.00	-15.12	-15.12	15.12	15.12


Gebrauchslast							
Feld	Abstand	max M	min M	max Q	min Q	max AR	min AR
1	0.00	0.00	0.00	29.12	13.12	29.12	13.12
	2.56	37.52	12.94	0.19	-3.01	29.12	13.12
	6.40	-32.26	-57.86	-25.20	-45.20	90.40	50.40
2	0.00	-32.26	-57.86	45.20	25.20	90.40	50.40
	3.84	37.52	12.94	3.01	-0.19	29.12	13.12
	6.40	0.00	0.00	-13.12	-29.12	29.12	13.12

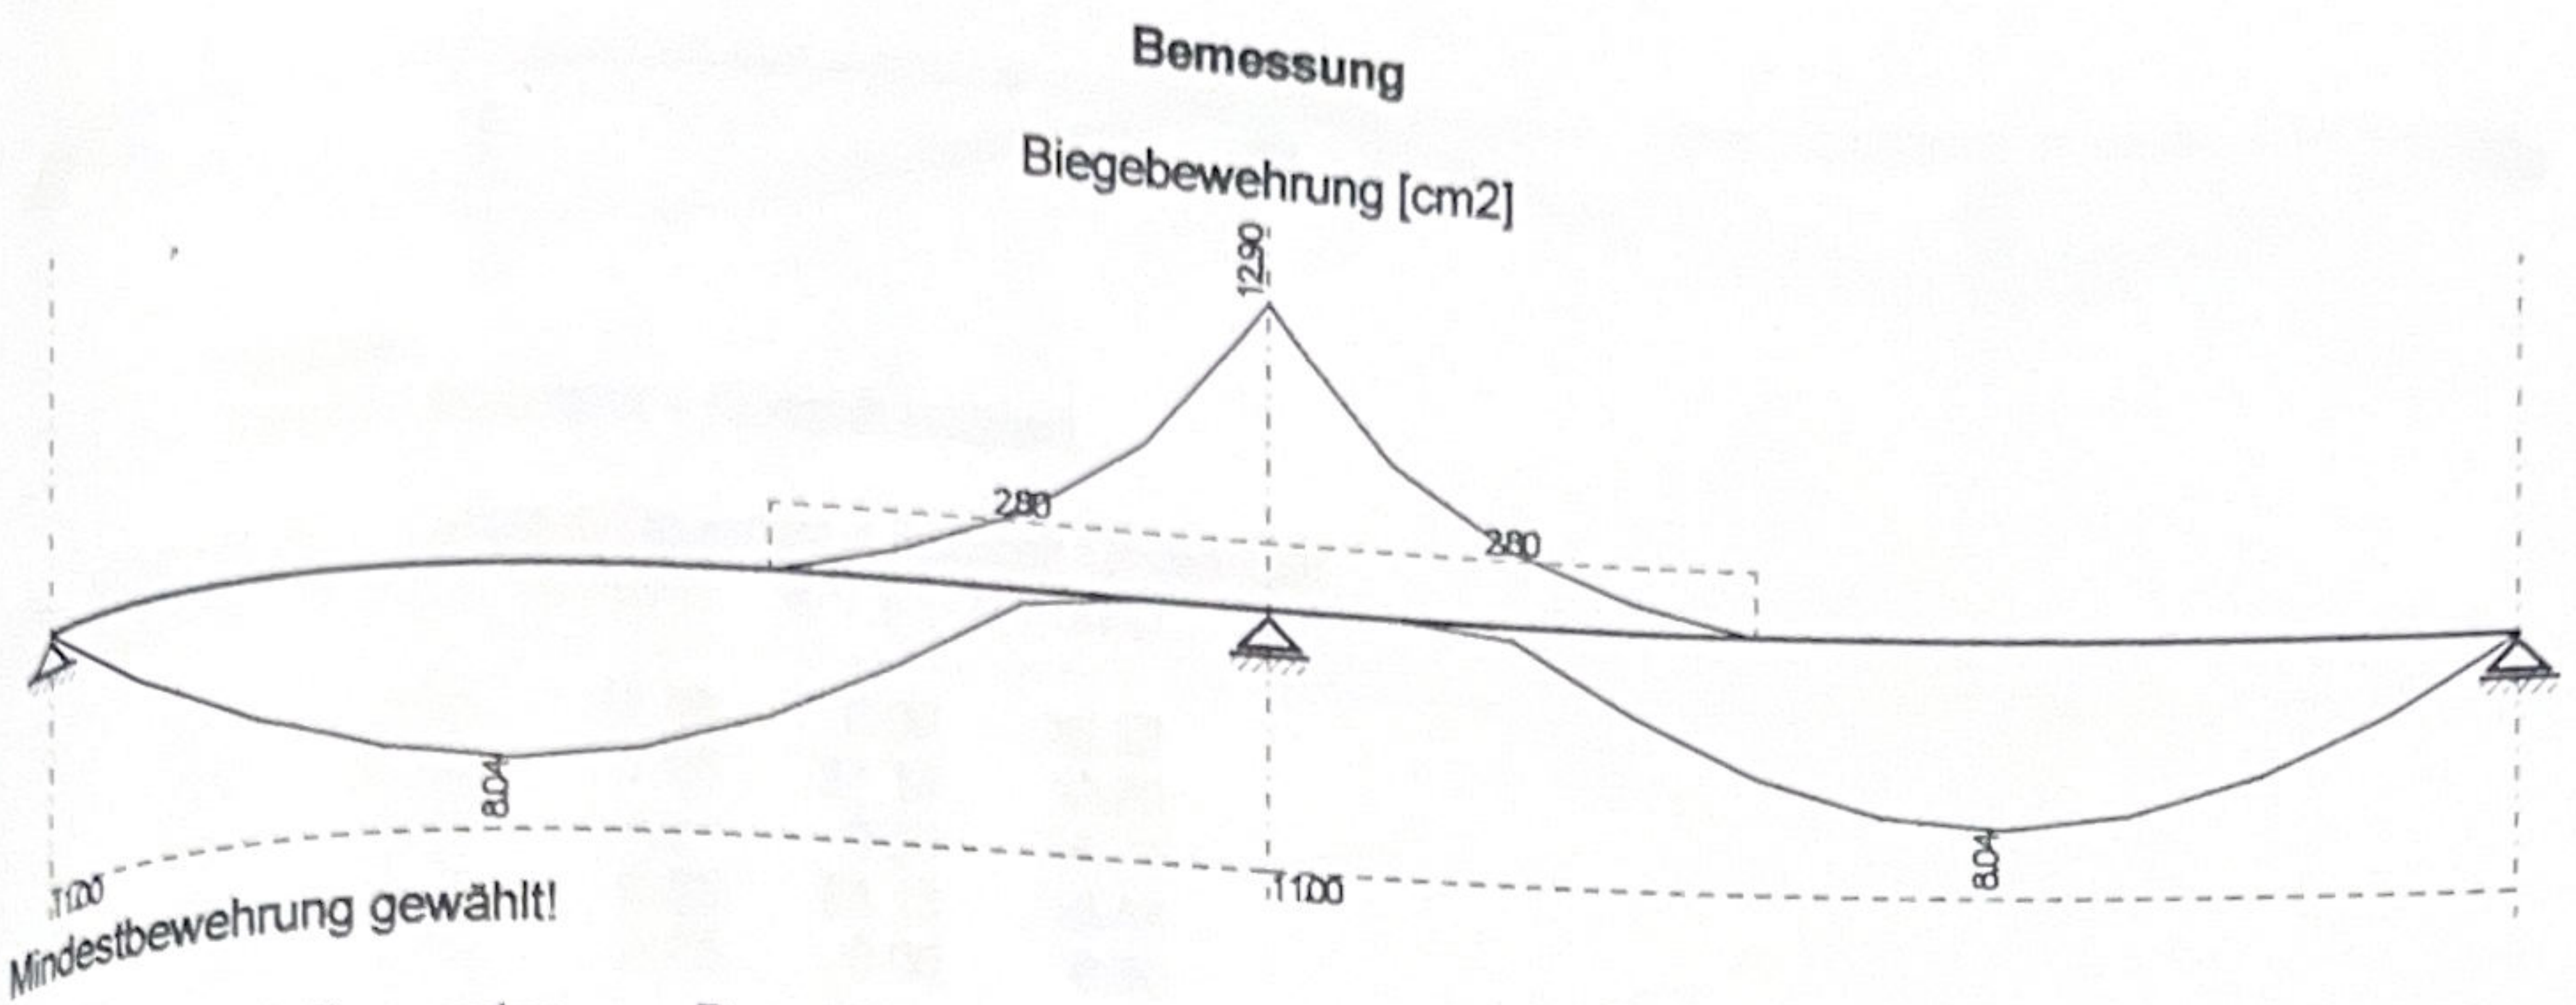

Feld	Abstand	Bew. unten	Bew. oben
1	0.00	0.00	0.00
	2.56	8.04	0.00
	6.40	0.00	12.90
2	0.00	0.00	12.90
	3.84	8.04	0.00
	6.40	0.00	0.00


Mindestbewehrung	Feld	Bew. unten	Bew. oben
	1 - 2	2.80	2.80

Gewählt	Feld	Bew. unten	Bew. oben links	Bew. oben rechts
	1 - 2	11.00	-	-

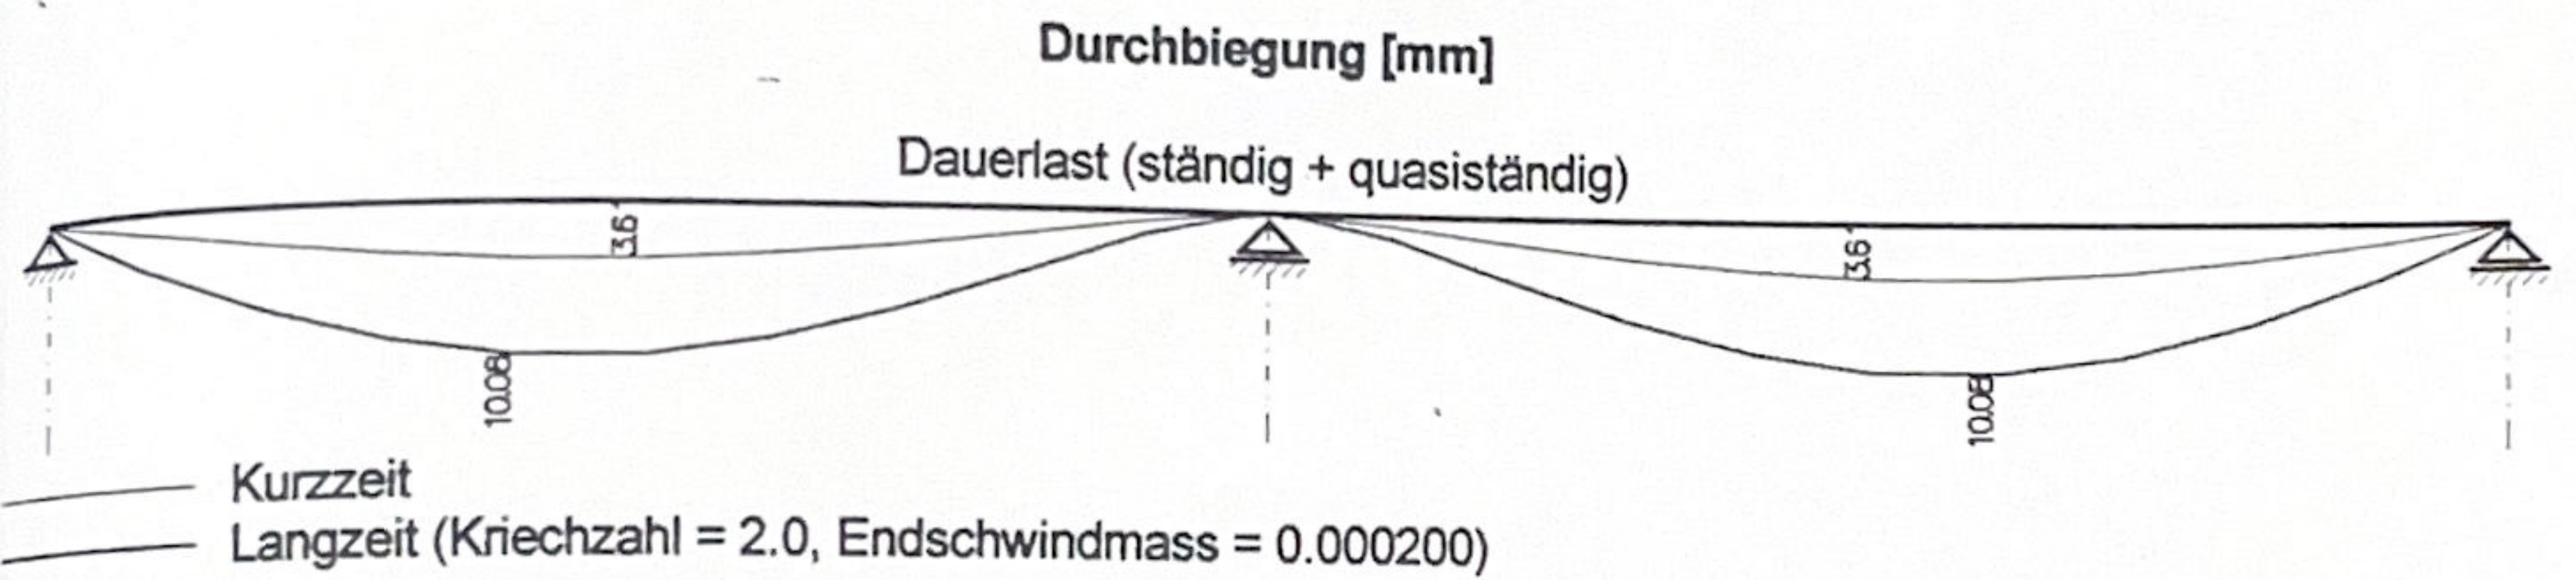

(K) ... Kurzzeit, (L) ... Langzeit.

Feld	Abstand	V-Y (K)	V-Phi (K)	V-Y (L)	V-Phi (L)
1	0.00	0.00	-2.05	0.00	-5.79
	3.20	3.61	0.31	10.03	1.00
2	0.00	0.00	0.00	0.00	0.00
	3.20	3.61	-0.31	10.03	-1.00
	6.40	0.00	2.05	0.00	5.79

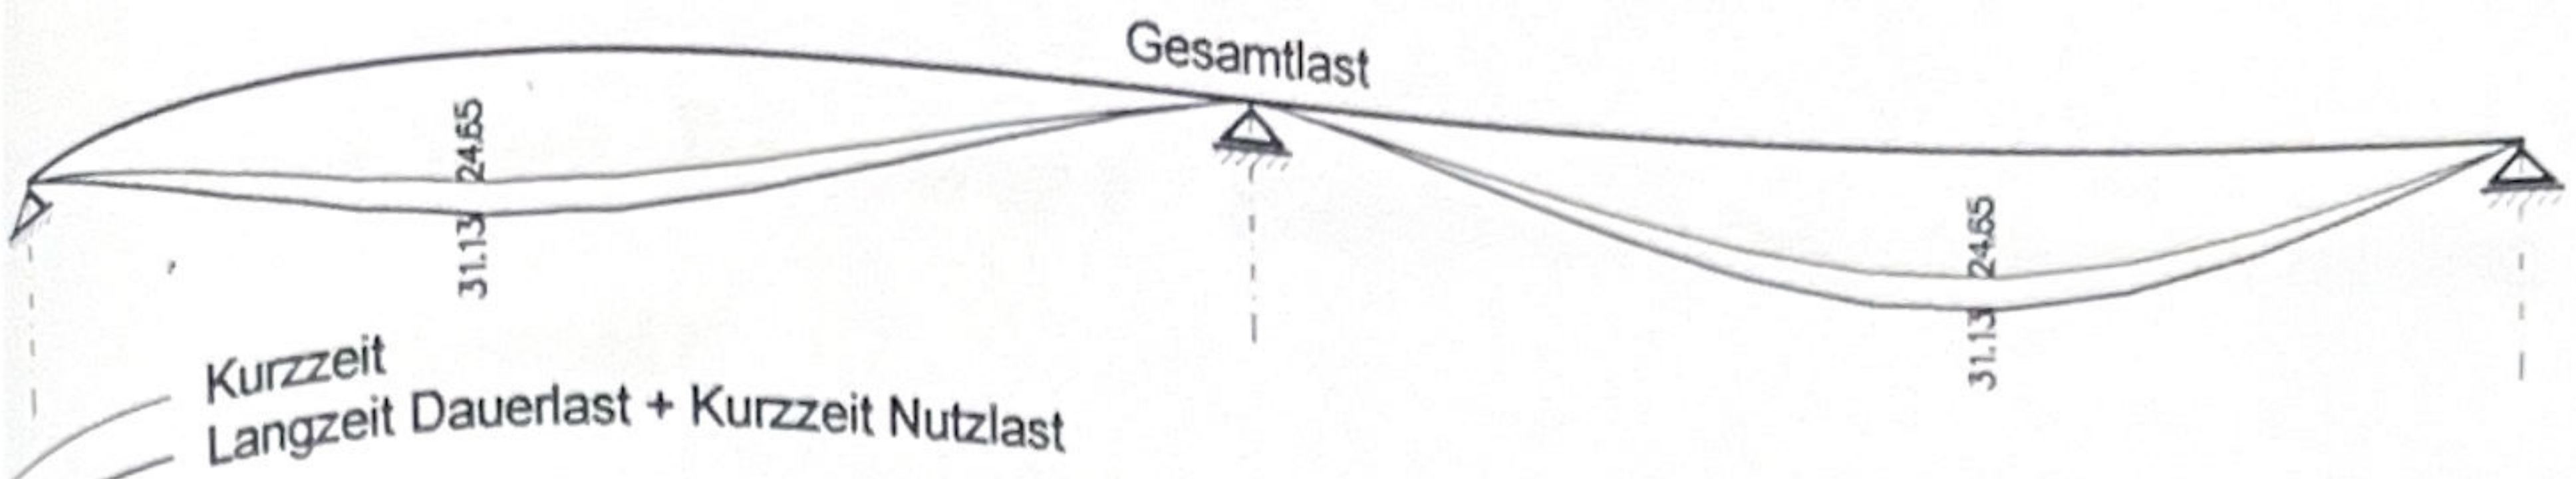

Feld	Abstand	Kurzzeit, (L) ... Langzeit Dauerlast + Kurzzeit Gesamtlast.			
		V-Y (K)	V-Phi (K)	V-Y (L)	V-Phi (L)
1	0.00	0.00	-13.08	0.00	-16.82
	2.56	24.65	-1.70	31.13	-2.20
2	0.00	0.00	-4.21	0.00	-4.21
	3.84	24.65	-0.95	31.13	-0.44
	6.40	0.00	2.85	0.00	6.60

Rissebeschränkung für Lastbeanspruchung

Rechnerische Reißbreite $w_k = 0.30 \text{ mm}$

Feld	Abstand [m]	As_u [cm ²]	As_o [cm ²]	M [kNm]	Sigma_II [MN/m ²]	rho_t [%]	h_t [m]	h_1 [m]	d_sg [mm]
1	0.640	11.00		8.39	55	1.10	0.100	0.050	43
1	5.120	11.00	3.20	-5.16	96	0.32	0.100	0.050	21
2	1.920	11.00	2.80	4.52	30	1.10	0.100	0.050	43
2	1.280	11.00	3.20	-5.16	96	0.32	0.100	0.050	21

4. FUNDIERUNG

DAS HAUS IST MITTELS ZIEGERSTREIFENFUNDAMENTE
GESRÜNDET.

AUSSCHLAGGEBEND - MITTELMAUER

AUFLAST AUF d. FUNDAMENT.

v. DACH	$31,20 \times \frac{1}{9,0} + 21,0 \times \frac{1}{6,0}$	$= 6,97 \text{ kN/m}$
v. GALERIE	$202,50 \times \frac{1}{9,0}$	$= 22,50 \text{ kN/m}$
v. DECKE Ü. 4 OG		$= 90,40 \text{ kN/m}$
v. DECKEN EG - 3 OG	$5 \times 6,0 \times 4,30$	$= 129,00 \text{ kN/m}$
v. DECKE Ü. KG	$5,50 \times 7,0$	$= 38,50 \text{ kN/m}$
v. Mauer	$0,30 \times 7,6 \times 8,50 + 0,90 \times 19,30 \times$ $\times 8,50 + 8,20 \times 13,90$	$= 287,00$
		$\Sigma 568,37 \text{ kN/m}$

$$b_{\text{dach}} = 0,90 \text{ m}$$

$$G_{\text{dach}} = \frac{568,37}{0,90} = 631,5 \text{ kN/m}^2 > G_{\text{zul}}$$

ES WIRD EINE STB. PLATTE $d=25 \text{ cm}$
AUSGEFÜHRT.

22

✓ GESIMSSICHERUNG

