


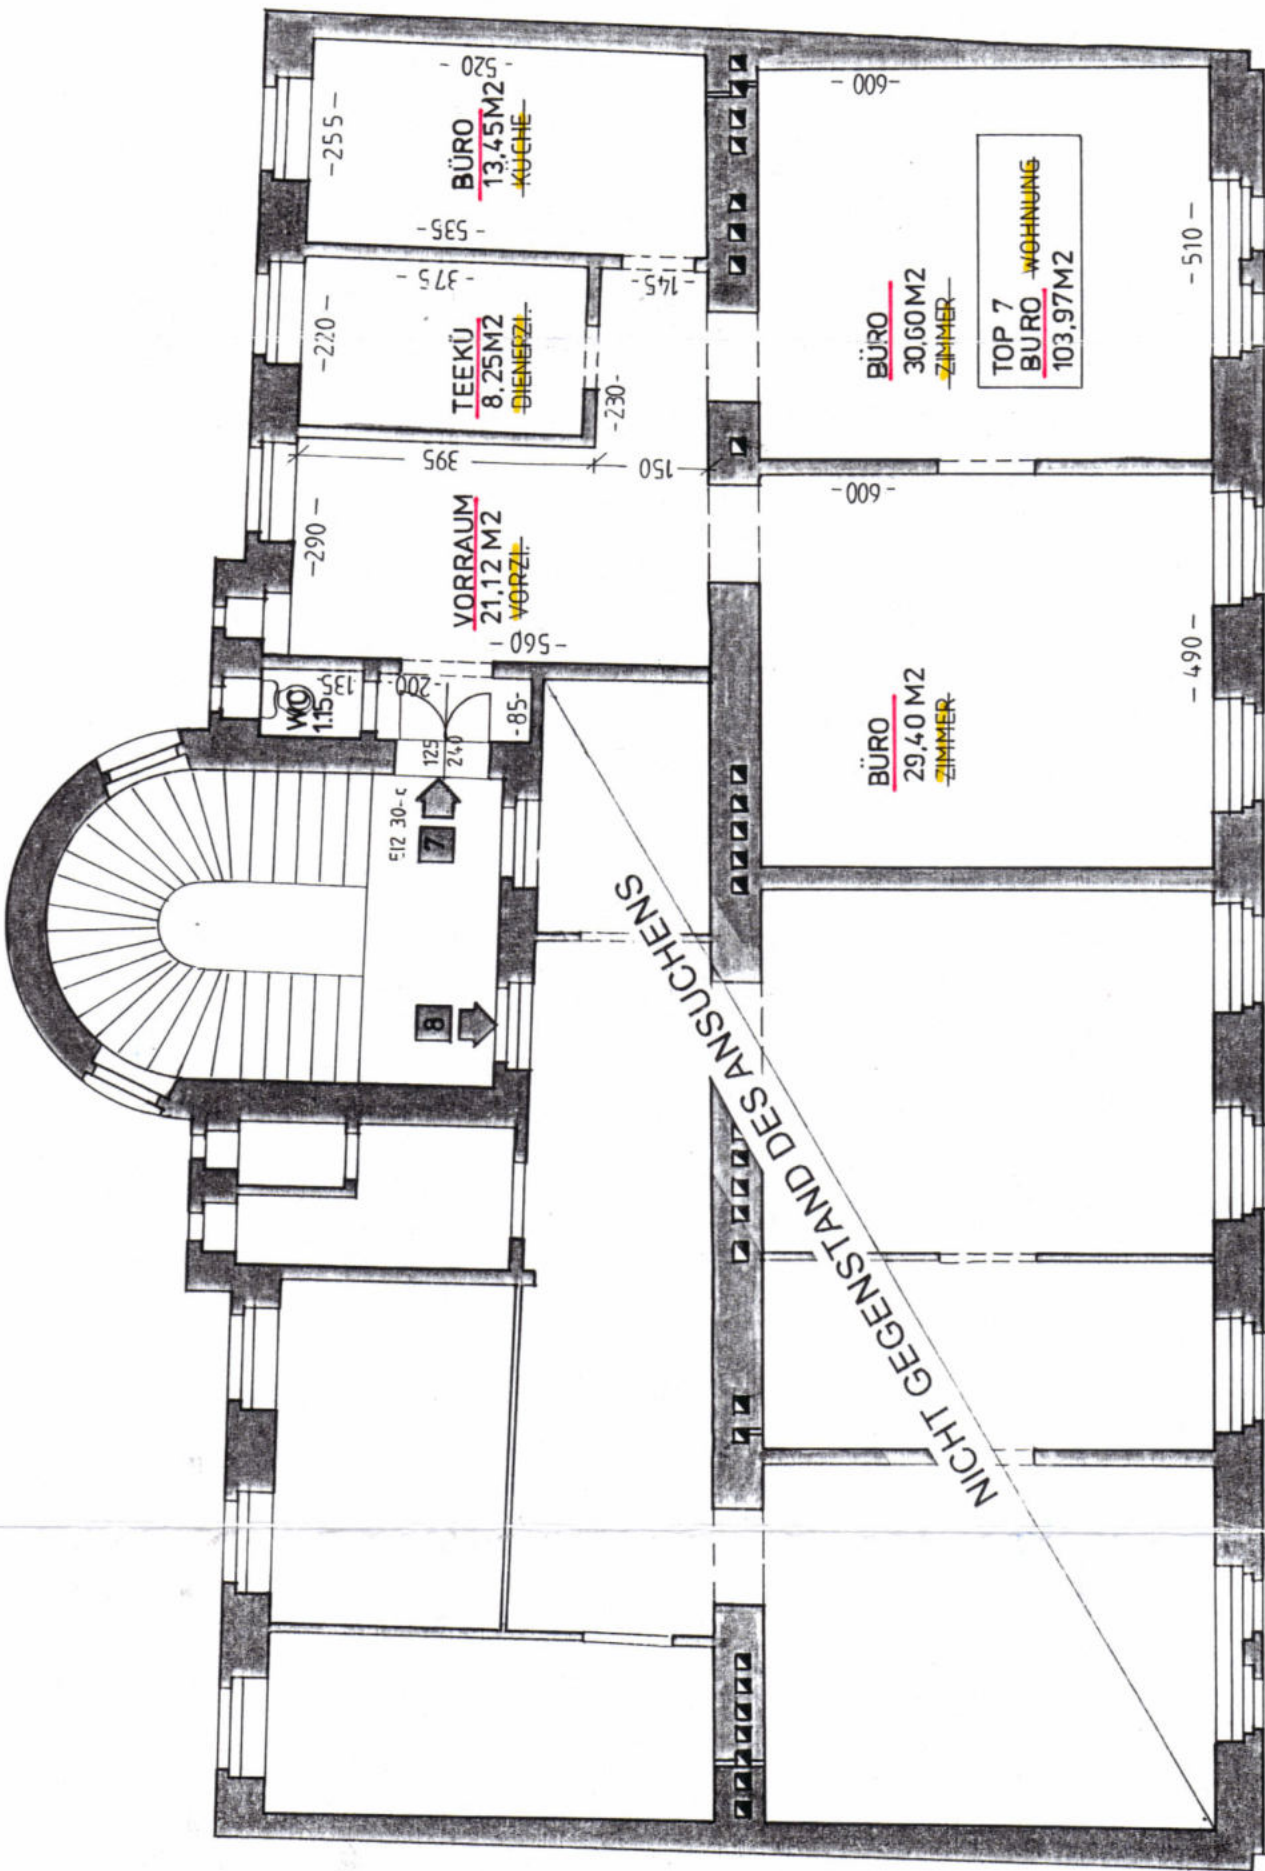

2. STOCK

LEGENDE:

- BESTAND
- NEUERSTELLUNG
- ABBRUCH



Berechnung der erforderlichen KFZ-Pflichtstellplätze

Großer Vortragssaal 135,07 m²
Kleiner Vortragssaal 23,47 m²
TOP 7 – Büro 73,45 m²
TOP 7 – Büro 13,45+30,60+29,40= 231,99 m²

erforderliche Pflichtstellplätze -> 231,99:80=2,90= -> 2
Widmungsänderung TOP 7
Wohnung -> Büro -1

erforderliche PKW Pflichtstellplätze 1

Aufgrund dieser Gegebenheiten wird 1 PKW Pflichtstellplatz erforderlich.

§ 119a BO für Wien



23
3

PARIE	A	B	C	1	2	3	4
EINREICHPLAN § 119 a ÜBER DIE UMWIDUNG VON WHG. IN BÜRO IM 2. STOCK, TOP 7 DES HAUSES LANDESGERICHTSSSTRASSE 6 1010 WIEN <i>unterliegt dem § 119 A d. BO f. Wien</i>							
EZ	GST		KATASTRALGEM.				
894	1526/2		Innere Stadt				
BAUWERBER							
Zentralverband der Hausbesitzer von Wien und den Ländern Österreichs Landesgerichtsstr. 6 1010 Wien Tel. 406 33 18 u. 406 33 19 Fax 406 53 49							
GRUNDEIGENTÜMER							
Zentralverband der Hausbesitzer von Wien und den Ländern Österreichs Landesgerichtsstr. 6 1010 Wien Tel. 406 33 18 u. 406 33 19 Fax 406 53 49							
Zentralverband der Hausbesitzer von Wien und den Ländern Österreichs Landesgerichtsstr. 6 1010 Wien Tel. 406 33 18 u. 406 33 19 Fax 406 53 49							
PLANVERFASSER							
Architekt Dipl.-Ing. ADOLF WOHNANKA MILLERGASSE 21, 1060 WIEN Tel.: 597 13 68 Fax: 596 24 30							
BAUFÜHRER							
MA 37 – Baupolizei Geldstrafe 1957 in der Höhe von EUR 360 wurde erfindlich bekanntgegeben, siehe Akt Wien, 06. OKT. 2004							
DATUM							
September 2004							
BEHÖRDE							
Magistrat der Stadt Wien Magistratsabteilung 37 Baupolizei Hierauf bezieht sich der Einreichplan MA 37 Wien, 05. OKT. 2004 FÜR DEN ANWANDERER: Fischer Dipl.-Ing. Fischer							