




1. STOCK

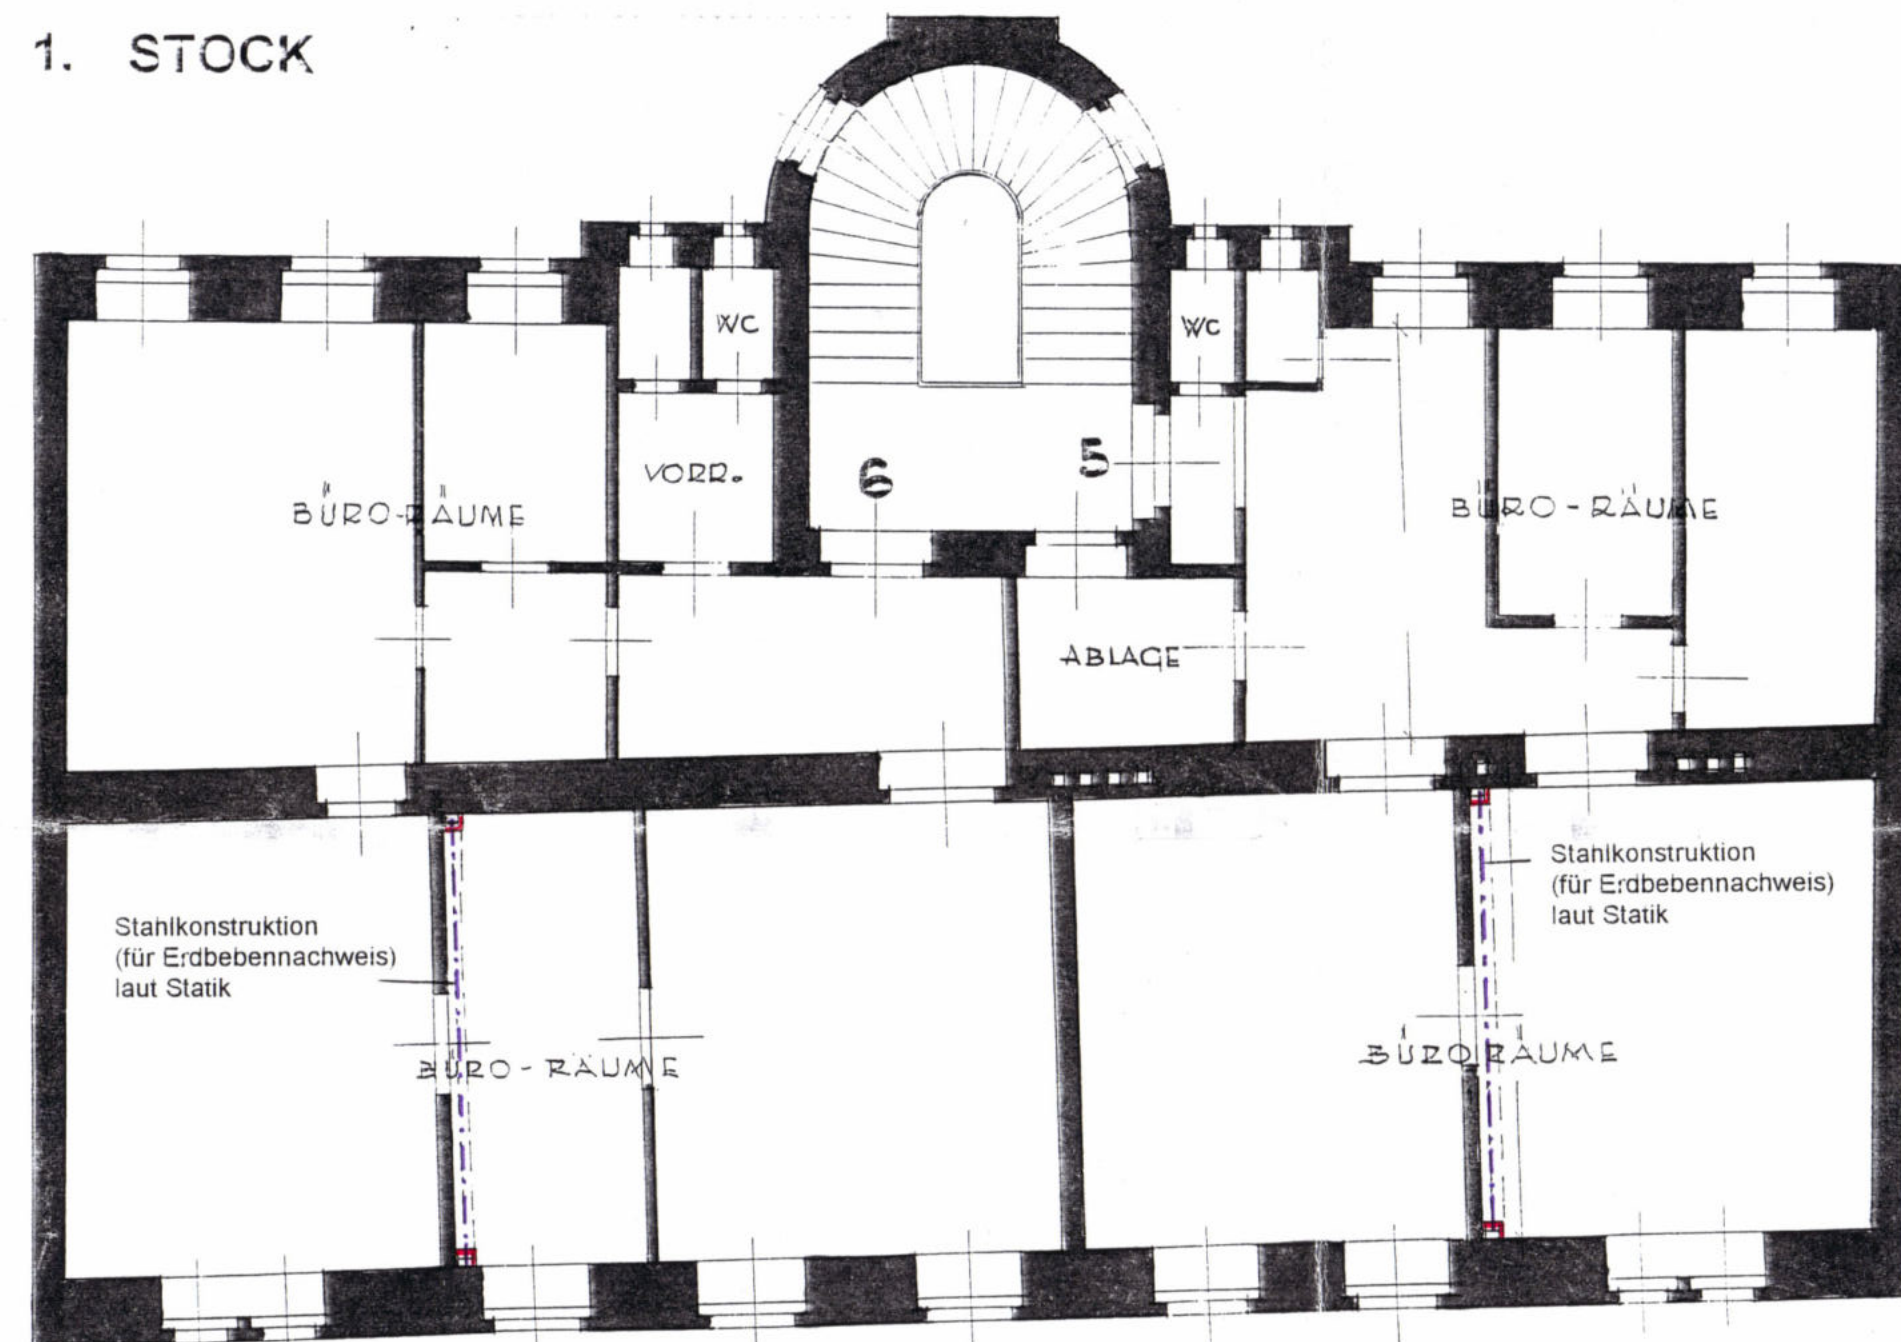


HOCHPARTERRE

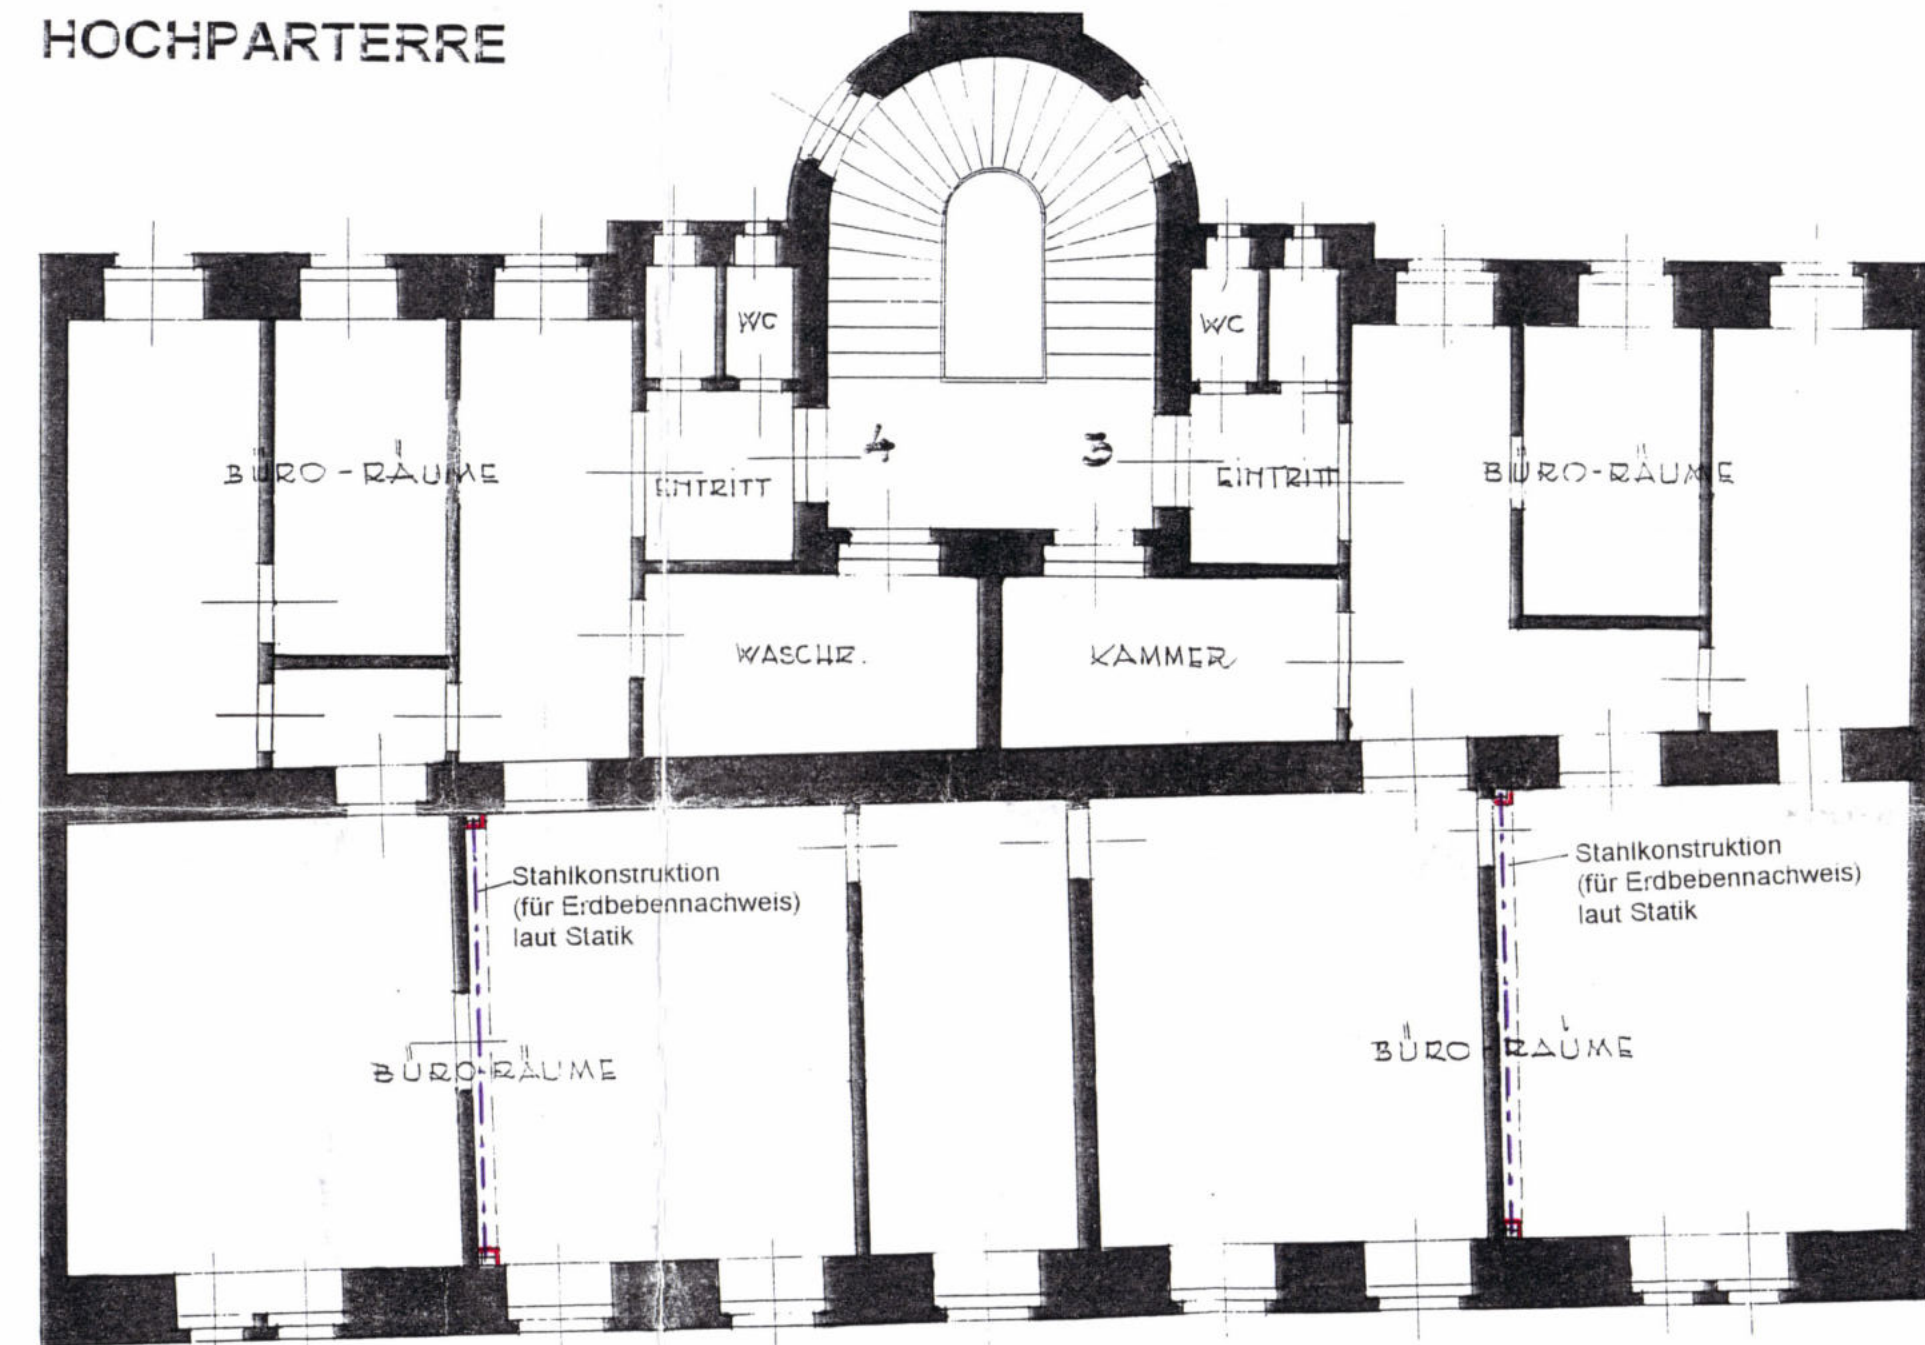

LAGEPLAN 1:250

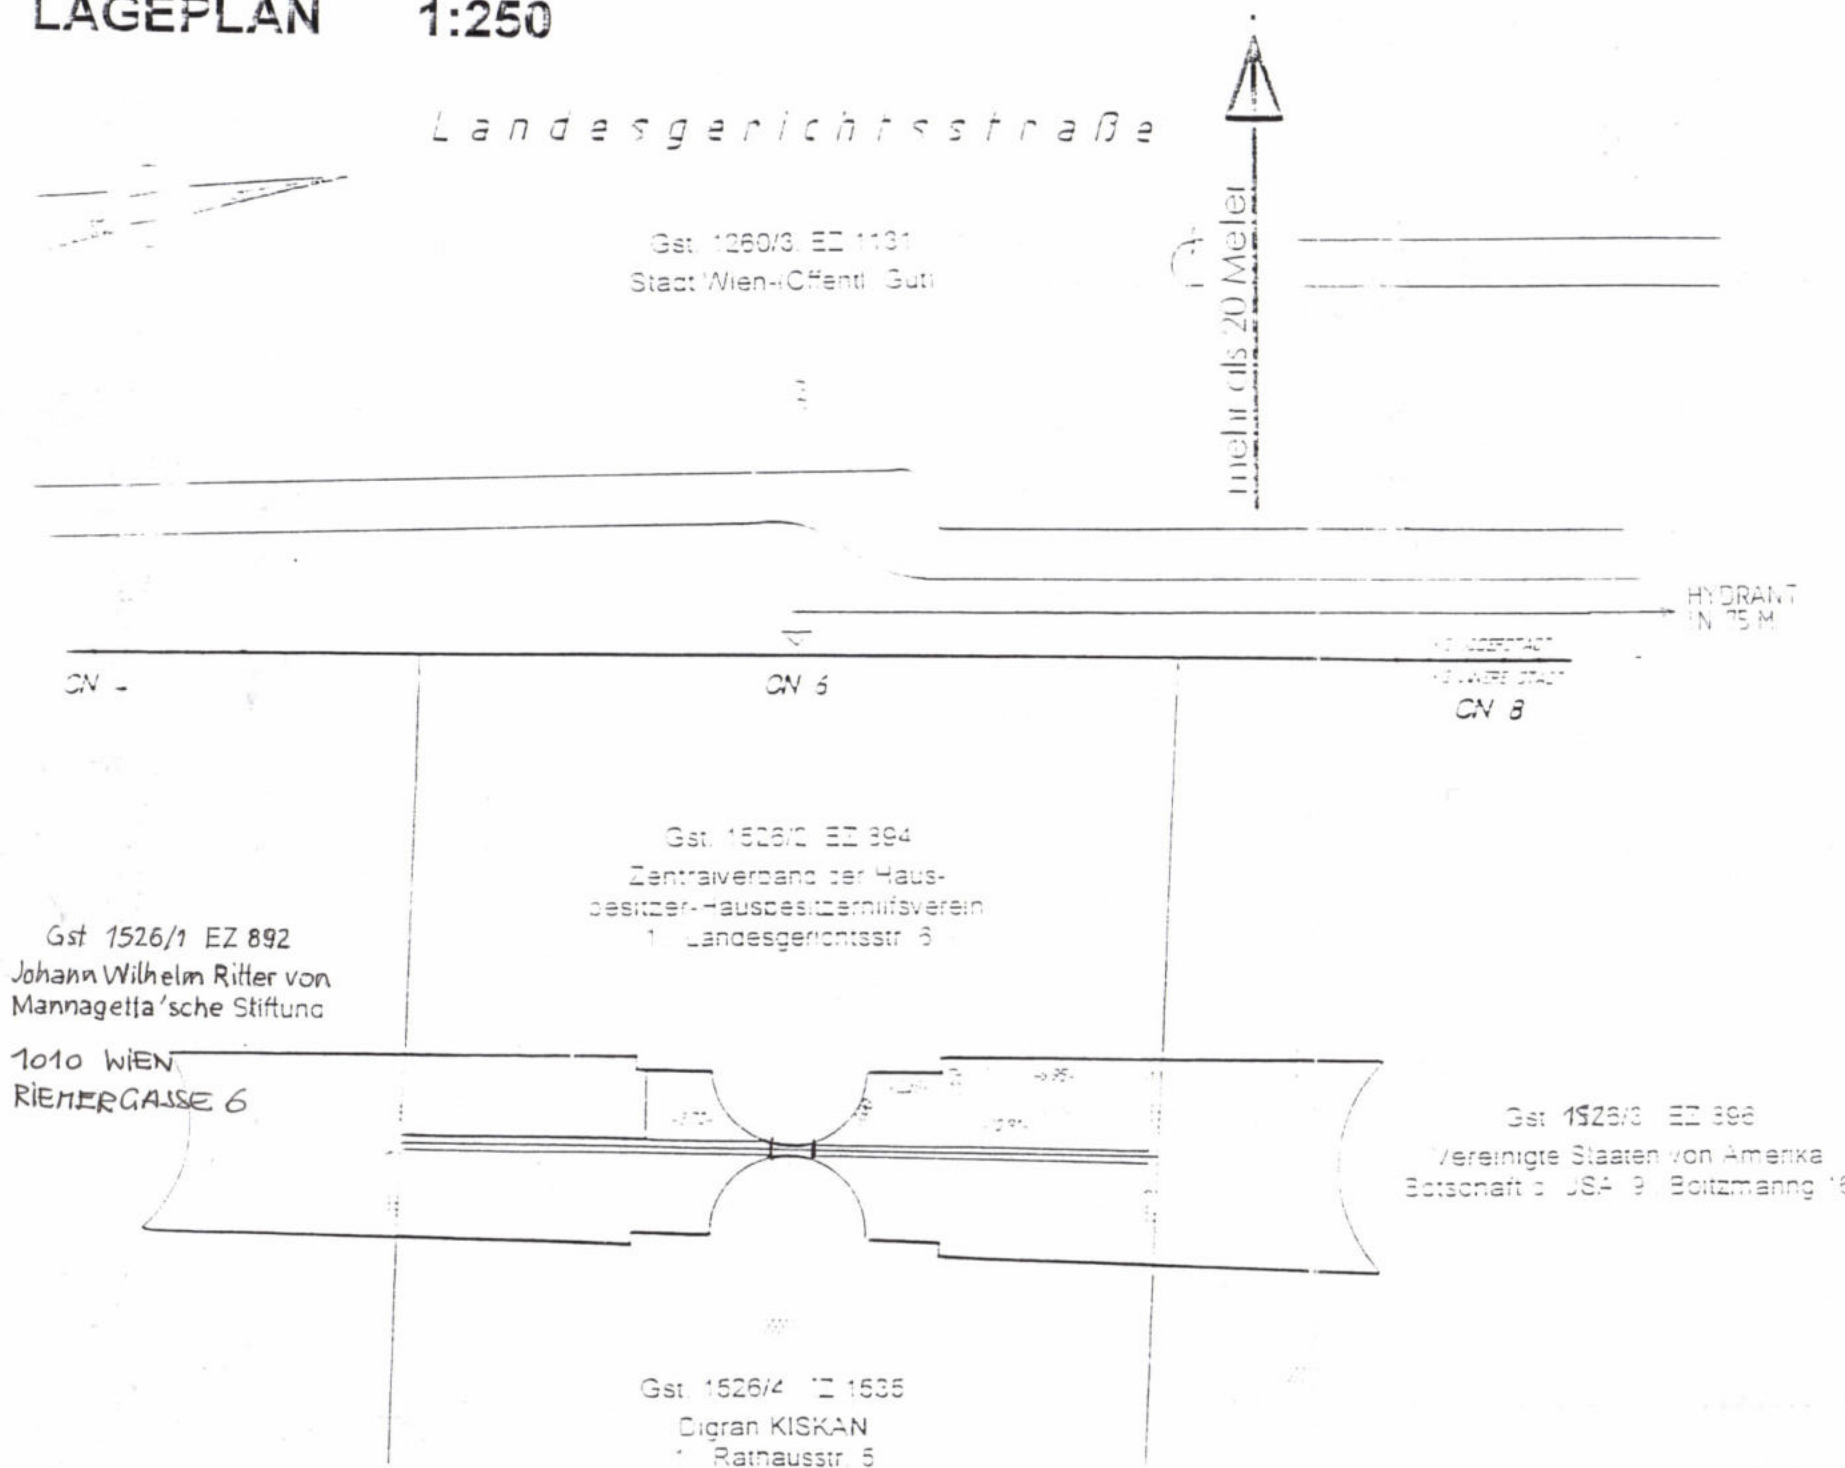


TIEFPARTERRE

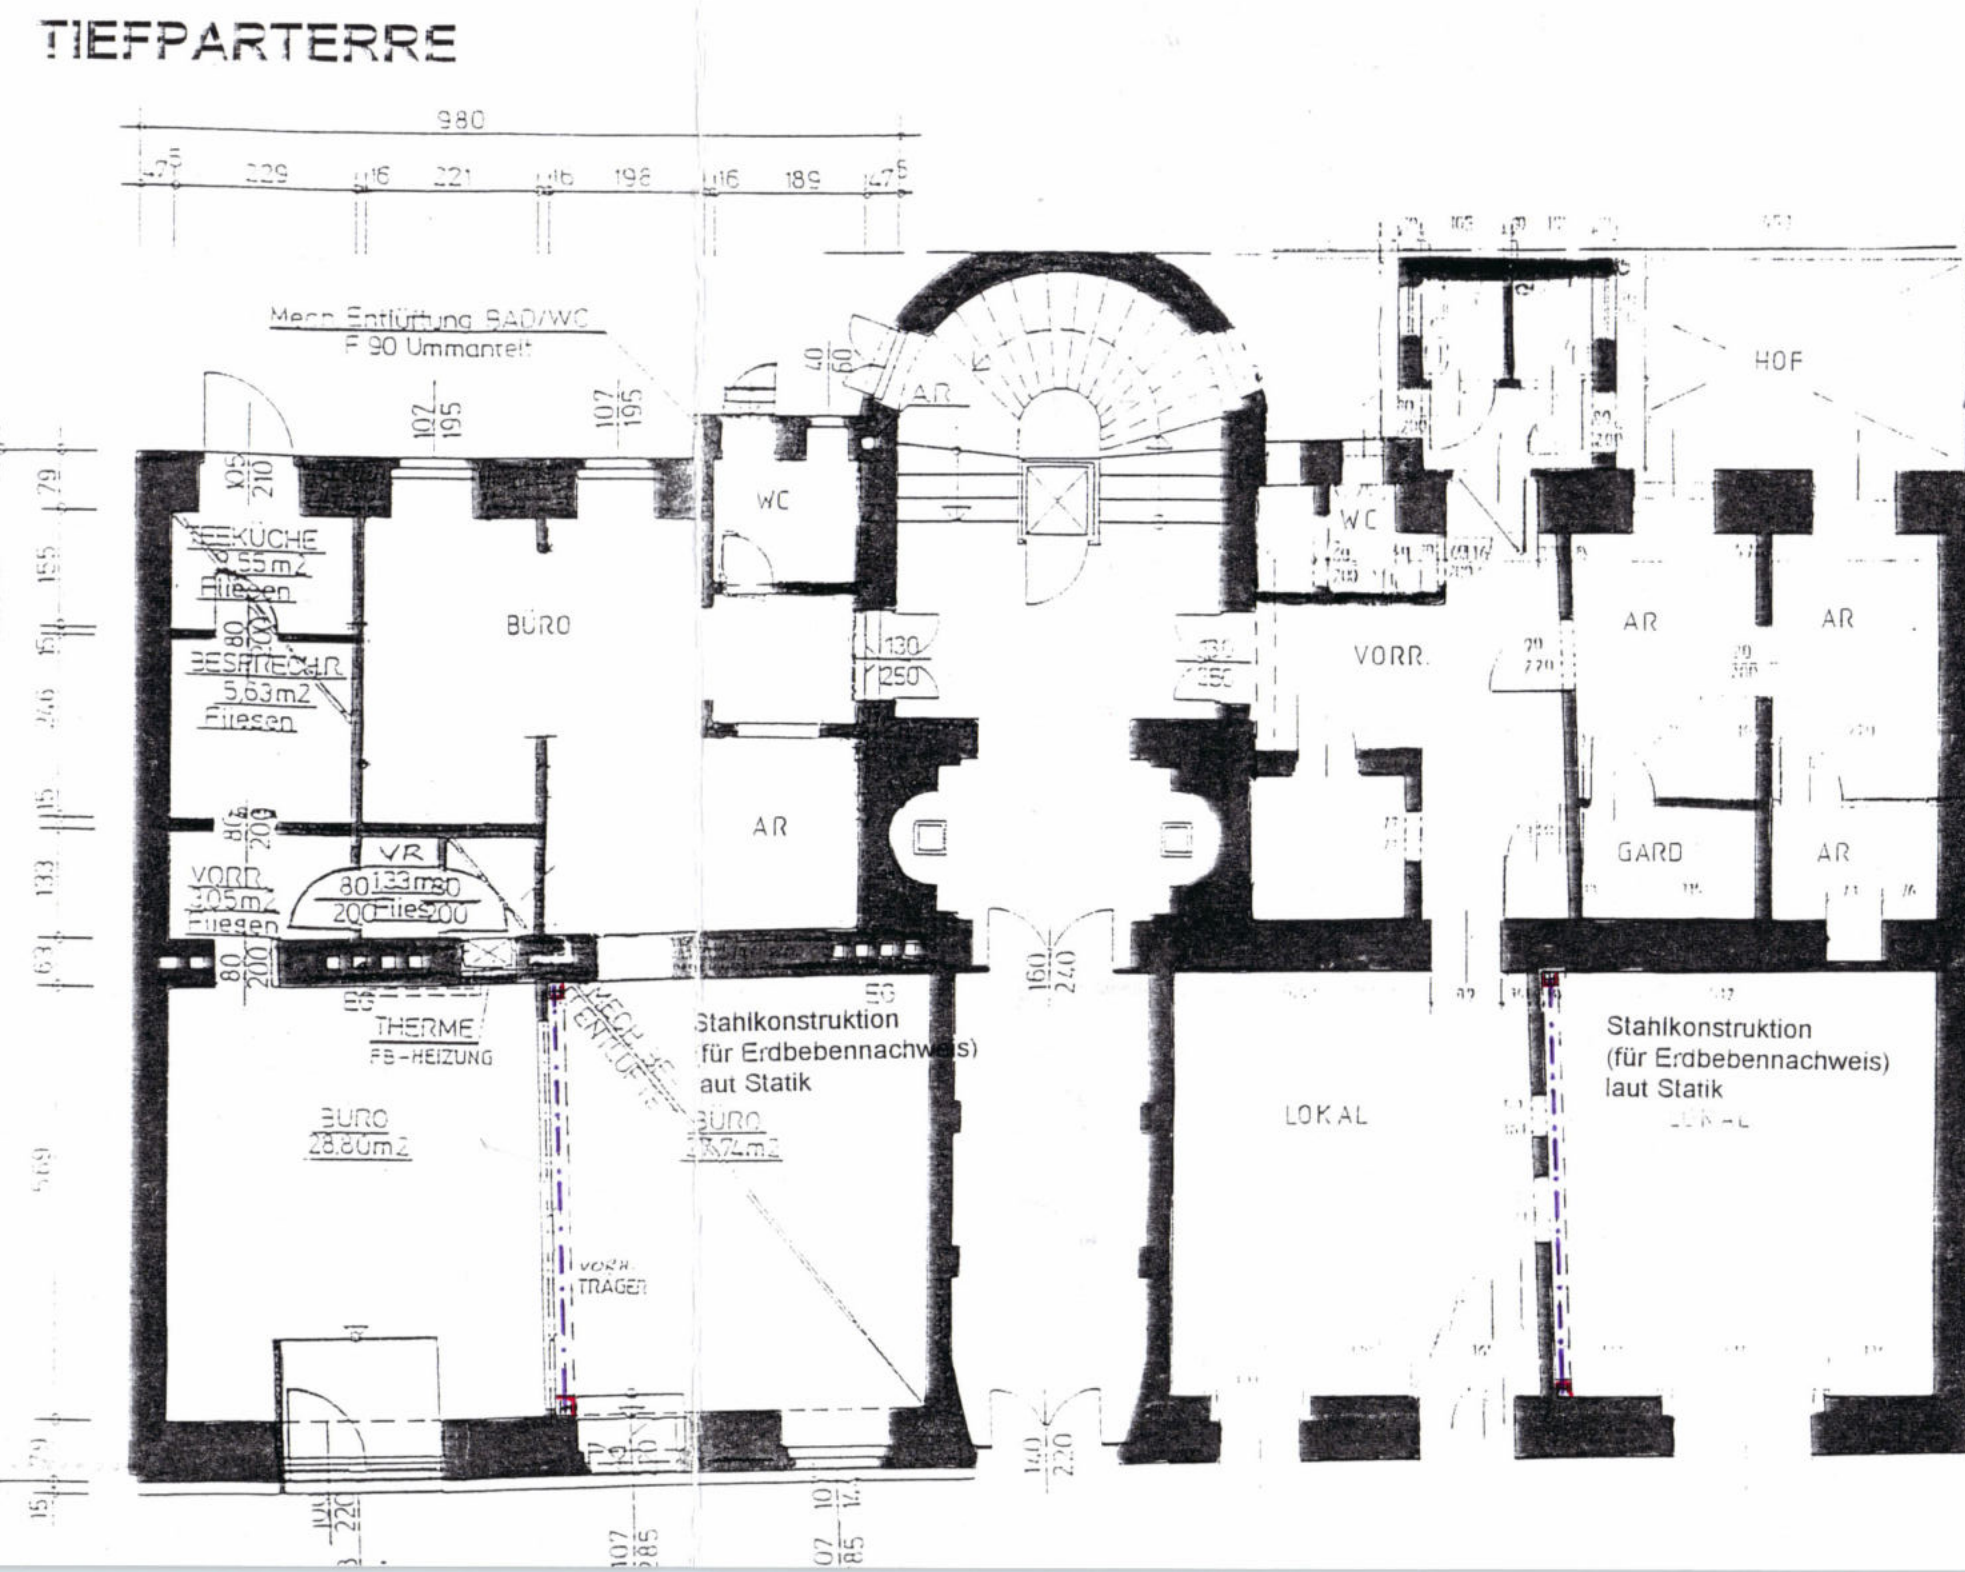

SCHNITT

(des gesamten Hauses laut Konsens für den Erdbebennachweis)

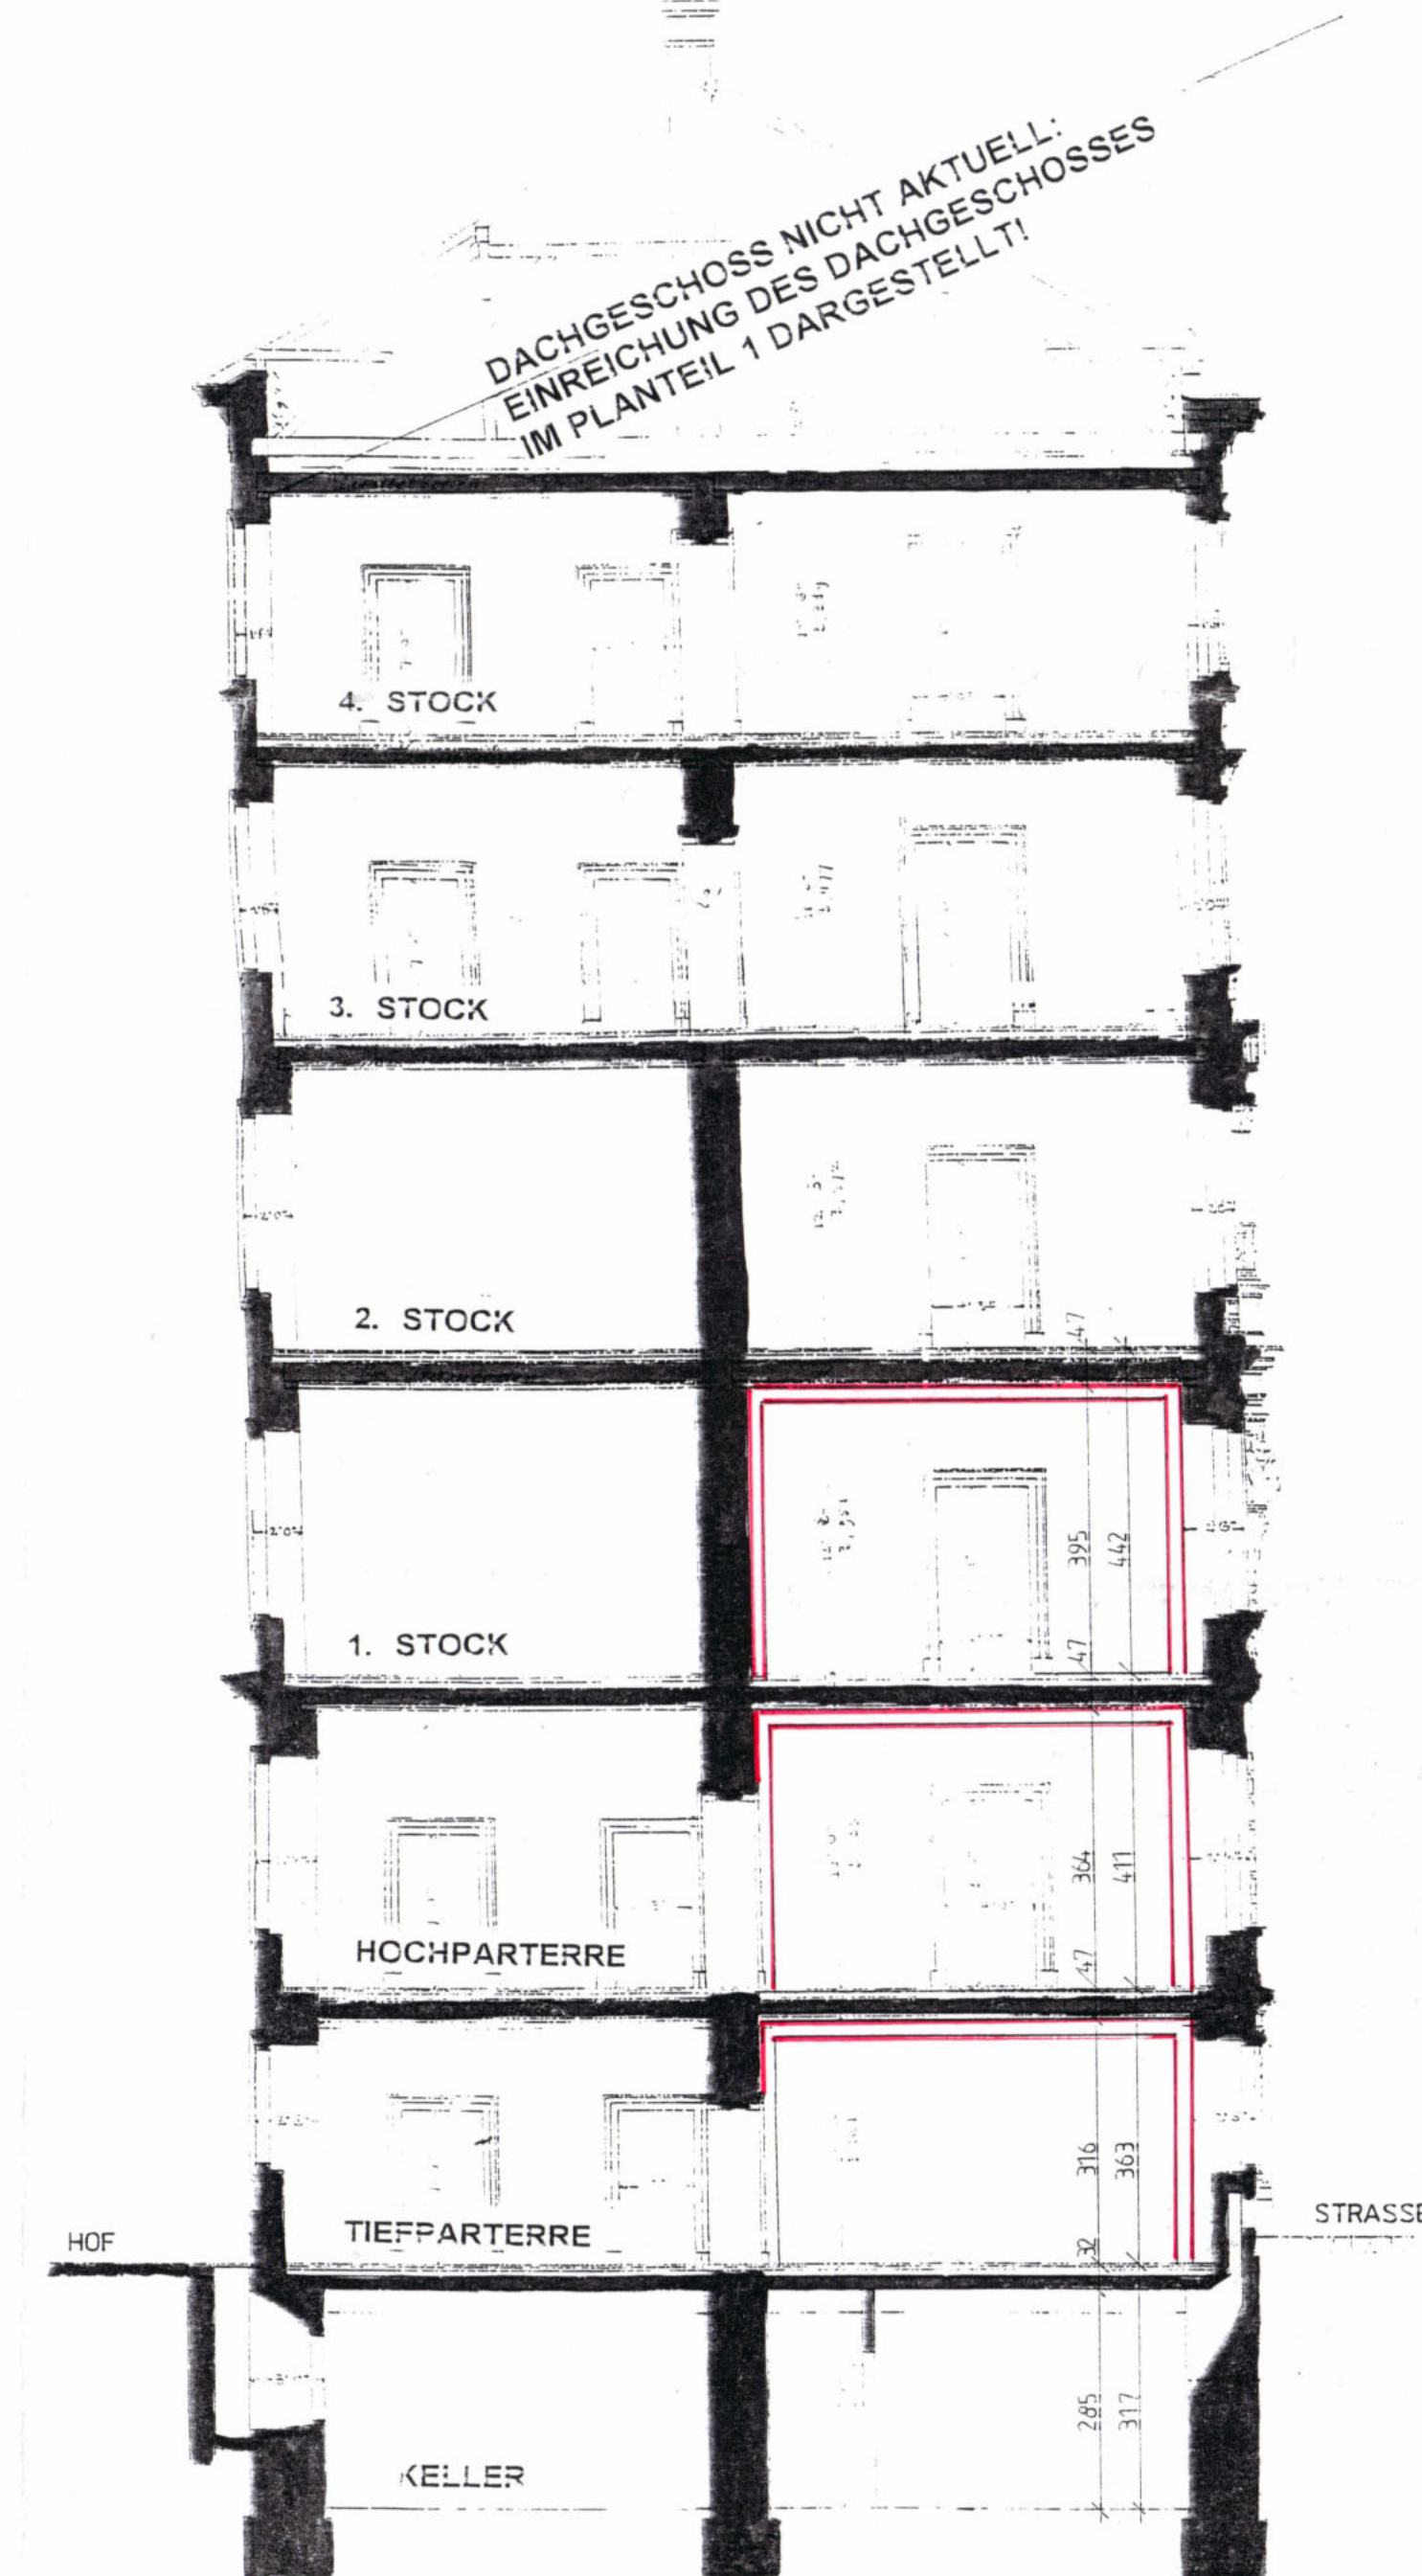

LEGENDE:

BESTAND

NEUERRICHTUNG

STAHLKONSTRUKTION

Stahkonstruktion (für Erdbebennachweis) laut Statik

Die tragenden Bauteile im Tiefparterre, Hochparterre und 1. Stock werden F90 ummantelt.

PARIE	A	B	C	1	2	3	4
EINREICHPLAN							
ÜBER DEN DACHGESCHOSSAUSBAU DES HAUSES							
LANDESGERICHTSSTRASSE 6 1010 WIEN							
unterliegt dem § 119 A d. BO f. Wien							
EZ	GST		KATASTRALGEM.				
894	1526/2						
BAUWERBER							
Zentralverband der Hausbesitzer von Wien und den Ländern Österreichs Landesgerichtsstr. 6 1010 Wien				Zentralverband der Hausbesitzer von Wien und den Ländern Österreichs Landesgerichtsstr. 6 1010 Wien Tel. 406 33 19 Fax 406 53 49			
GRUNDEIGENTÜMER							
Zentralverband der Hausbesitzer von Wien und den Ländern Österreichs Landesgerichtsstr. 6 1010 Wien				Zentralverband der Hausbesitzer von Wien und den Ländern Österreichs Landesgerichtsstr. 6 1010 Wien Tel. 406 33 19 Fax 406 53 49			
PLANVERFASSER				BAUFÜHRER			
Architekt Dipl.-Ing. ADOLF WOHANKA MILLERGASSE 21 Tel.: 597 13 68				Dipl.-Ing. ADOLF WOHANKA MILLERGASSE 21 Tel.: 597 13 68 Fax: 596 24 30			
DATUM				PLANNR.		BAUTEIL	
Juni 2004						U. 10.100	
BEHORDE				Magistratsabteilung 37 Baupolizei			
Hierauf bezieht sich der Bauantrag				Hierauf bezieht sich der Bauantrag			
MA 37				MA 37			
Wien				Wien			
Fdr den Abrechnungsstellen:				Fdr den Abrechnungsstellen:			
Fdr den Abrechnungsstellen:				Fdr den Abrechnungsstellen:			