




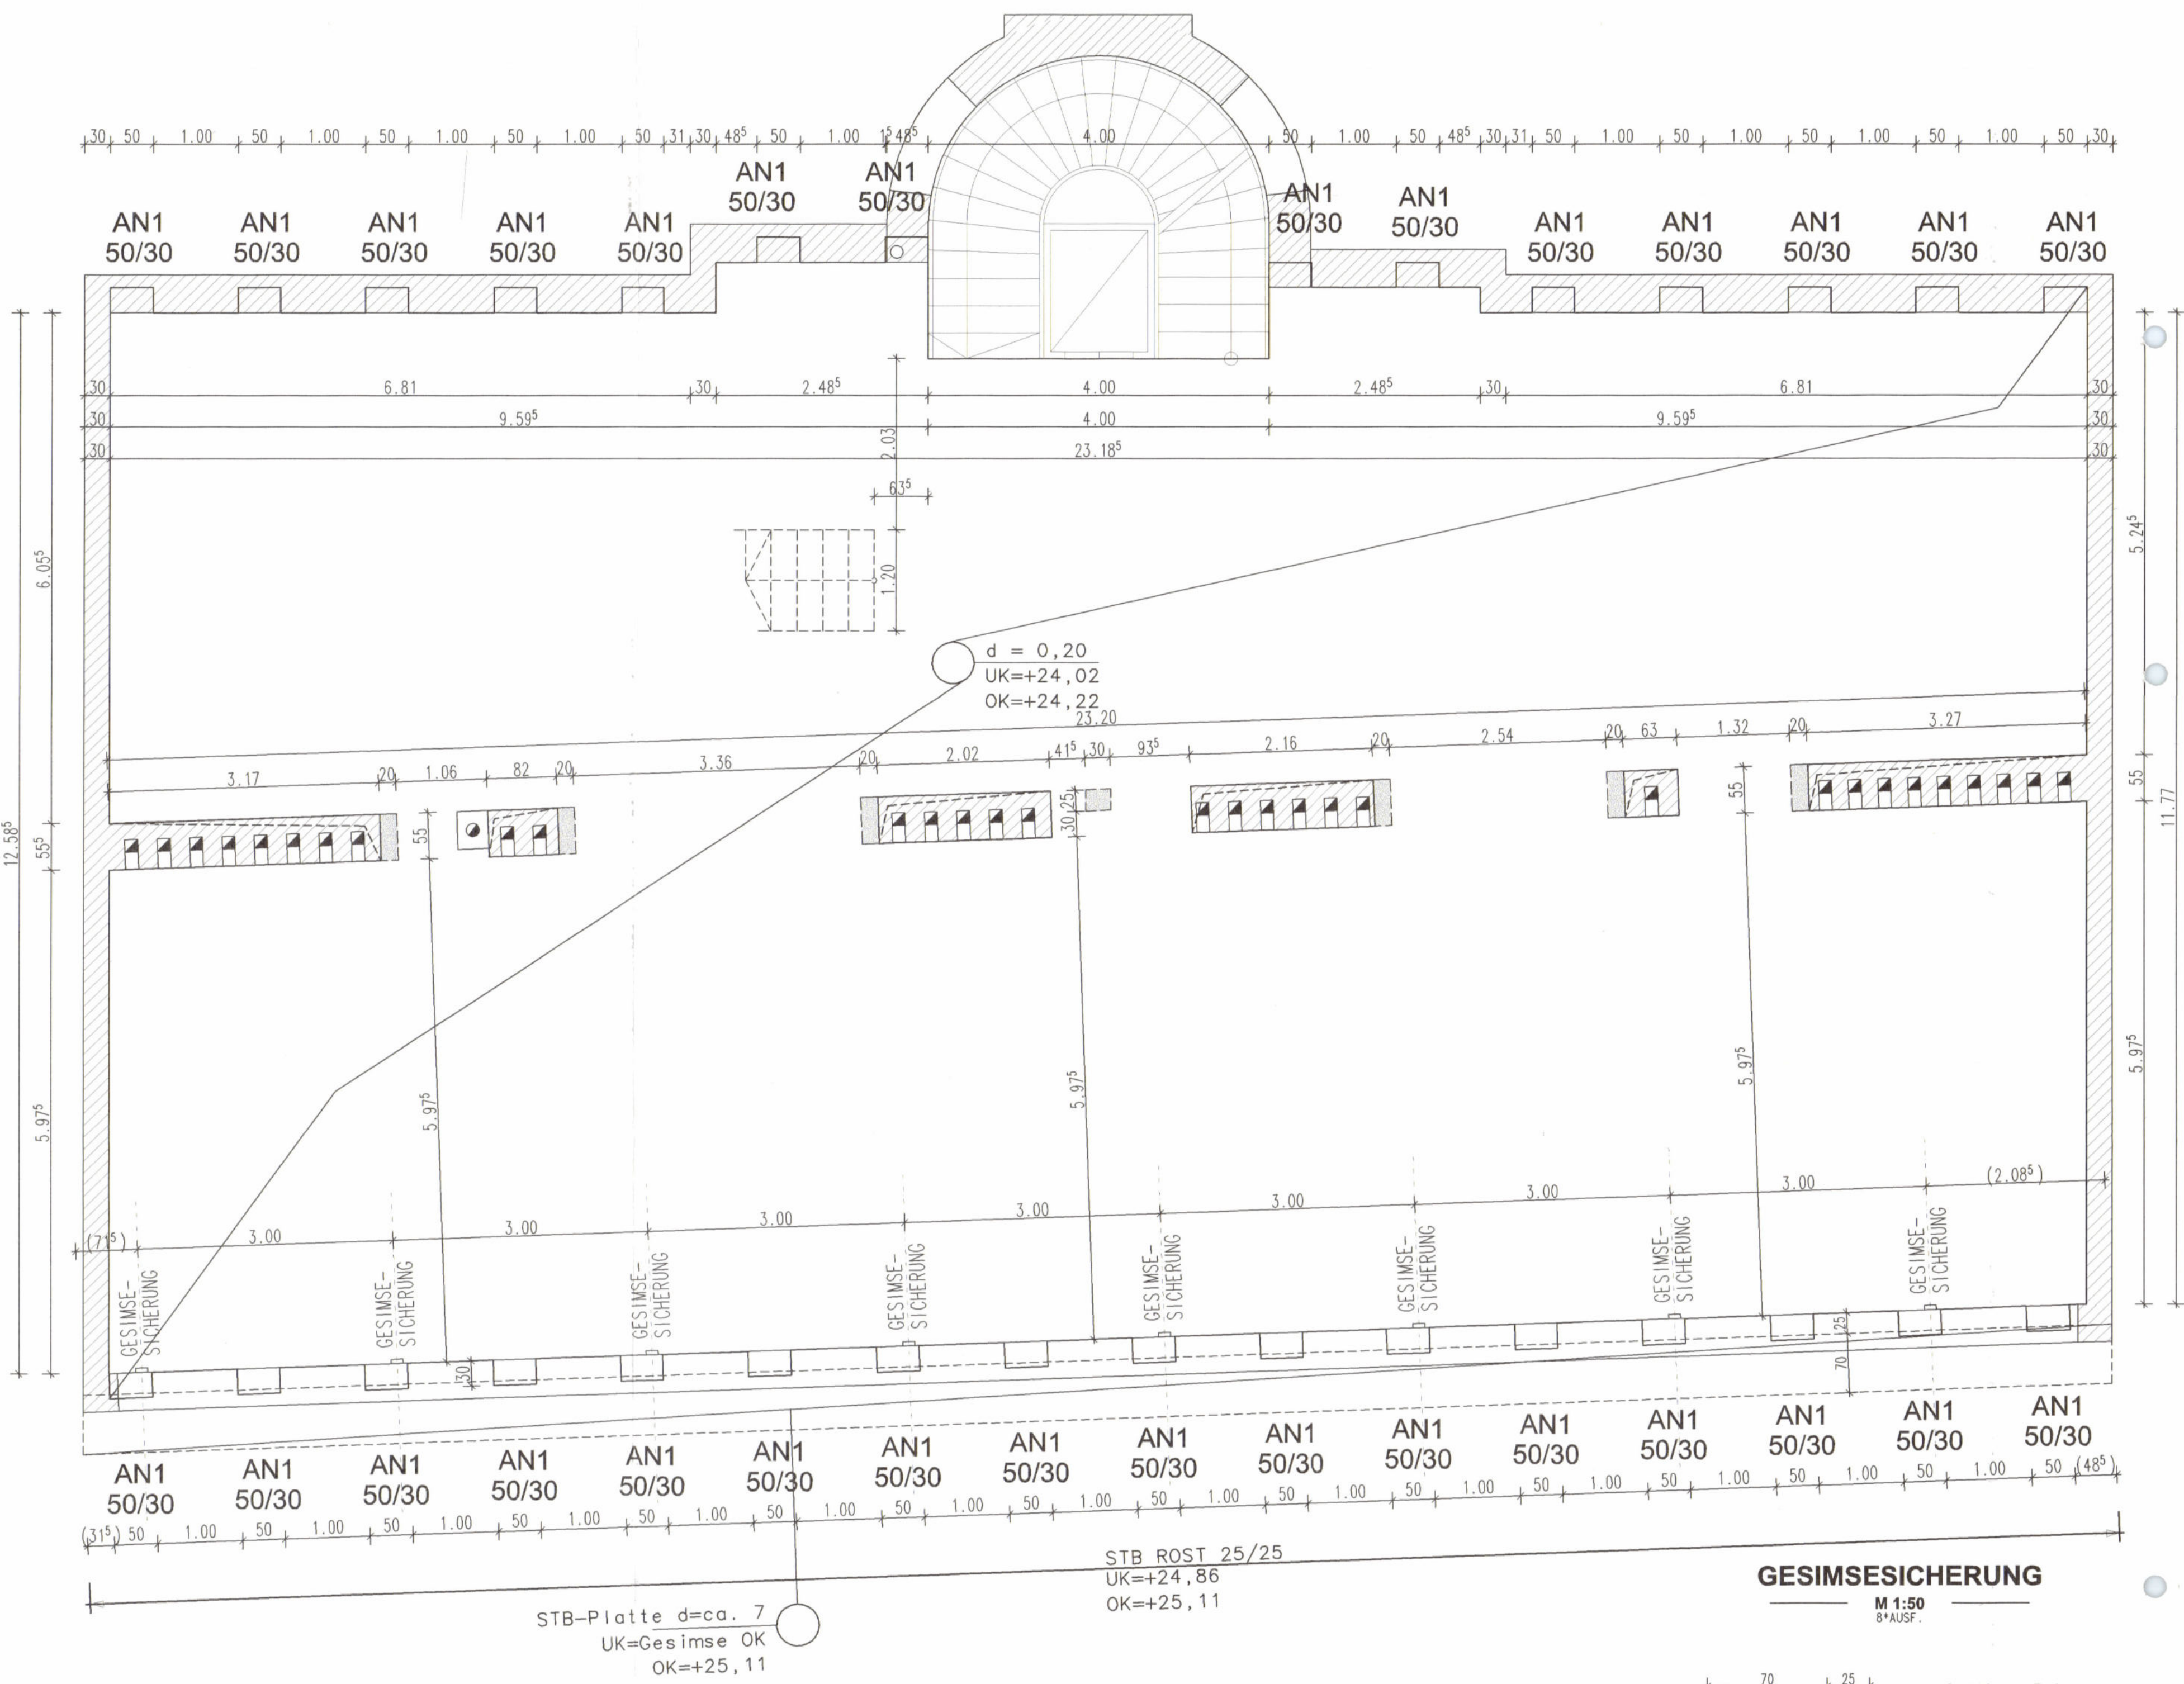


AUFLAGERNISCHEN AN1
M 1:25
32* AUSF.

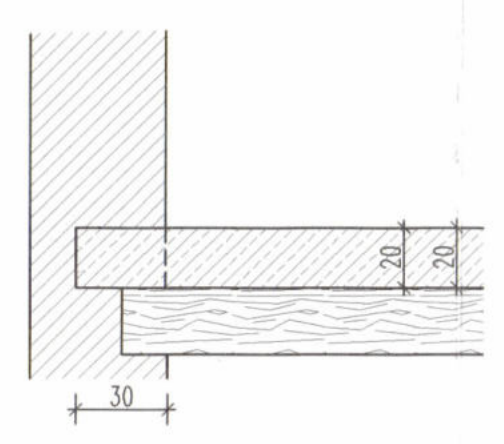

PLATTENQUERSCHNITT
M 1:25

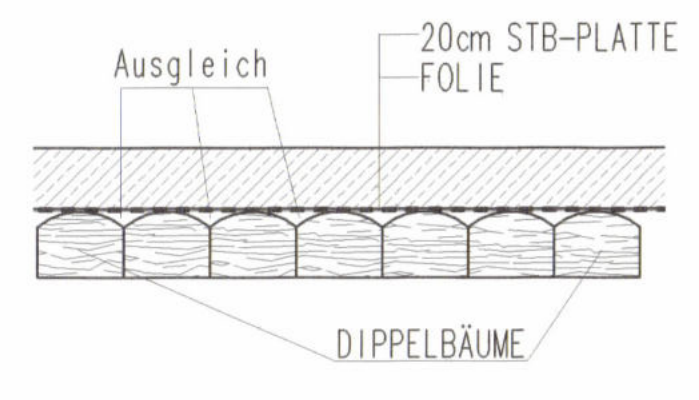


GESIMSESICHERUNG
M 1:50
8* AUSF.

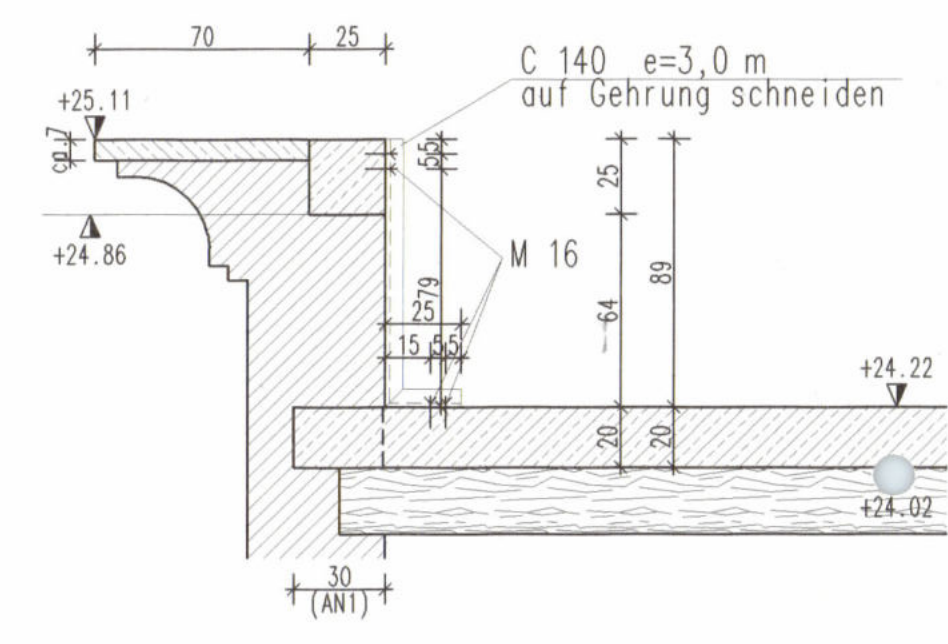


STB-Platte d=ca. 7
ÜBER GANZE LÄNGE
UK=Gesimse OK=+25,11

STB ROST 25/25
ÜBER GANZE LÄNGE
UK=+24,86
OK=+25,11

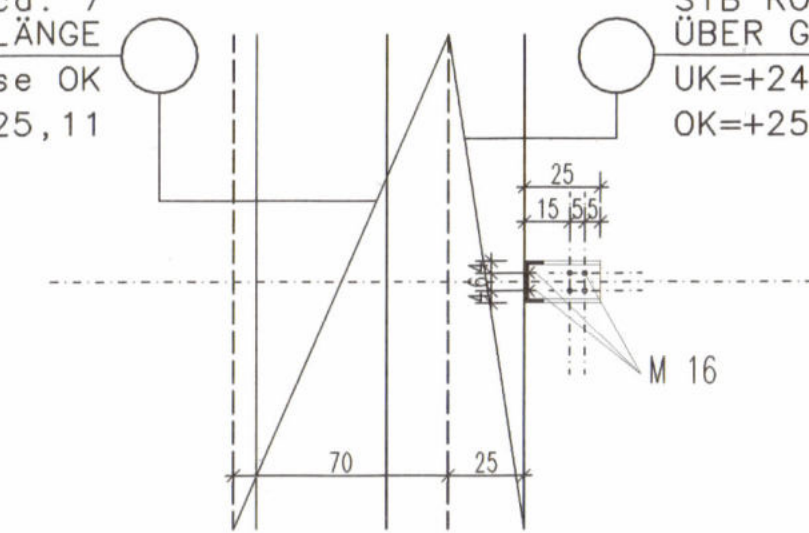

BIEGEANWEISUNG NACH ÖNORM B 4700

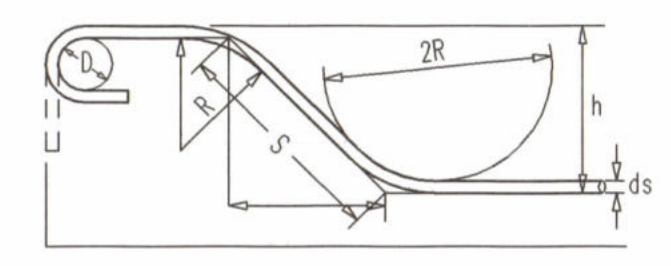

D=5ds
2R=20ds
Alle Biegekräfte sind von außen nach außen gemessen.

MATERIALGÜTEN:		BETONDECKUNG	
(WENN NICHT ANDERS ANGEZEIGT)		PLANMINDESTMASS GEM. ÖNORM B4700-(WENN NICHT ANDERS ANGEZEIGT)	
BETON:	C30/37	-	2,5CM
STABSTAHL:	BSt 550	MATTENÜBERGRIFFE (WENN NICHT ANDERS ANGEZEIGT)	
MATTEN:	M 55	IN LÄNGSRICHTUNG: 40 cm	
LAGENSCHHEMA F. DECKENBEWEHRUNG:		IN QUERRICHTUNG: 40 cm	
BEZEICHNUNG DER BEWEHRUNGSLAGEN:		! UNFALLSCHUTZ !	
VERLEGERICHTUNG:		GERADE NACH OBEN ENDEnde STÄBE (STECKEISEN) MÜSSEN ABGEDECKT ODER ZUSÄTZLICH HAKENFÖRMIG (OHNE VERRINGERUNG DER HAFTLÄNGE) ABGEBOGEN WERDEN.	
LEGENDE:		PLANDARSTELLUNG 1 BEDEUTET 1 AUSGEFÜHRT!!!	
BEMERKUNGEN:		1.) BÜGELMASSE SIND AUSSENMASSE.	
		2.) VERTEILEREISEN: WENN NICHT ANDERS ANGEZEIGT, STÖSSE BEI EINHALTUNG DER ANGEZEIGTEN ÜBERGRIFFE VERSETZEN.	
		3.) KRÜMMUNGEN, AUFBIEGUNGEN, WINKELHAKEN, SCHLÄUFEN UND SCHLINGEN SIND NACH ÖNORM B4200 TEIL 8 BZW. ÖNORM B4700 AUSZUFÜHREN.	
		4.) NICHT HERAUSGEZEICHNETE EISEN SIND BIEGEFORM A	

LEGENDE	
	STAHLBETON
	MAUERWERK
	MAUERWERK DARÜBER
	STAHLBETON DARÜBER

3	-	-	-
2	-	-	-
1	-	-	-
0	STB	10.05.05	Erstausgabe
Index	gez.	Datum	Inhalt


Zum Konsens
Diese Unterlagen beziehen sich auf die zur ZL
MA 37/1-226PS-5/2004
Invalide Pläne / eingebrachte Fertigstellungsansätze




Datum 10.05.2005	Masstab 1 : 50	Plangröße	Dateiname -	gezeichnet STB
Planinhalt Schalungsplan Decke über 4.OG				Plannummer S -001/0
Projekt Dachgeschossausbau Landesgerichtsstr. 6				Geschäftszahl 2004/33

Planverfasser

D.I. ANDRZEJ GLOGOWSKI
ZIVILINGENIEUR F. BAUWESEN
OTHELLOGASSE 1/7/19
A-1230 WIEN
TELEFON +43 (0)1-615 39 93
FAX +43 (0)1-615 39 93

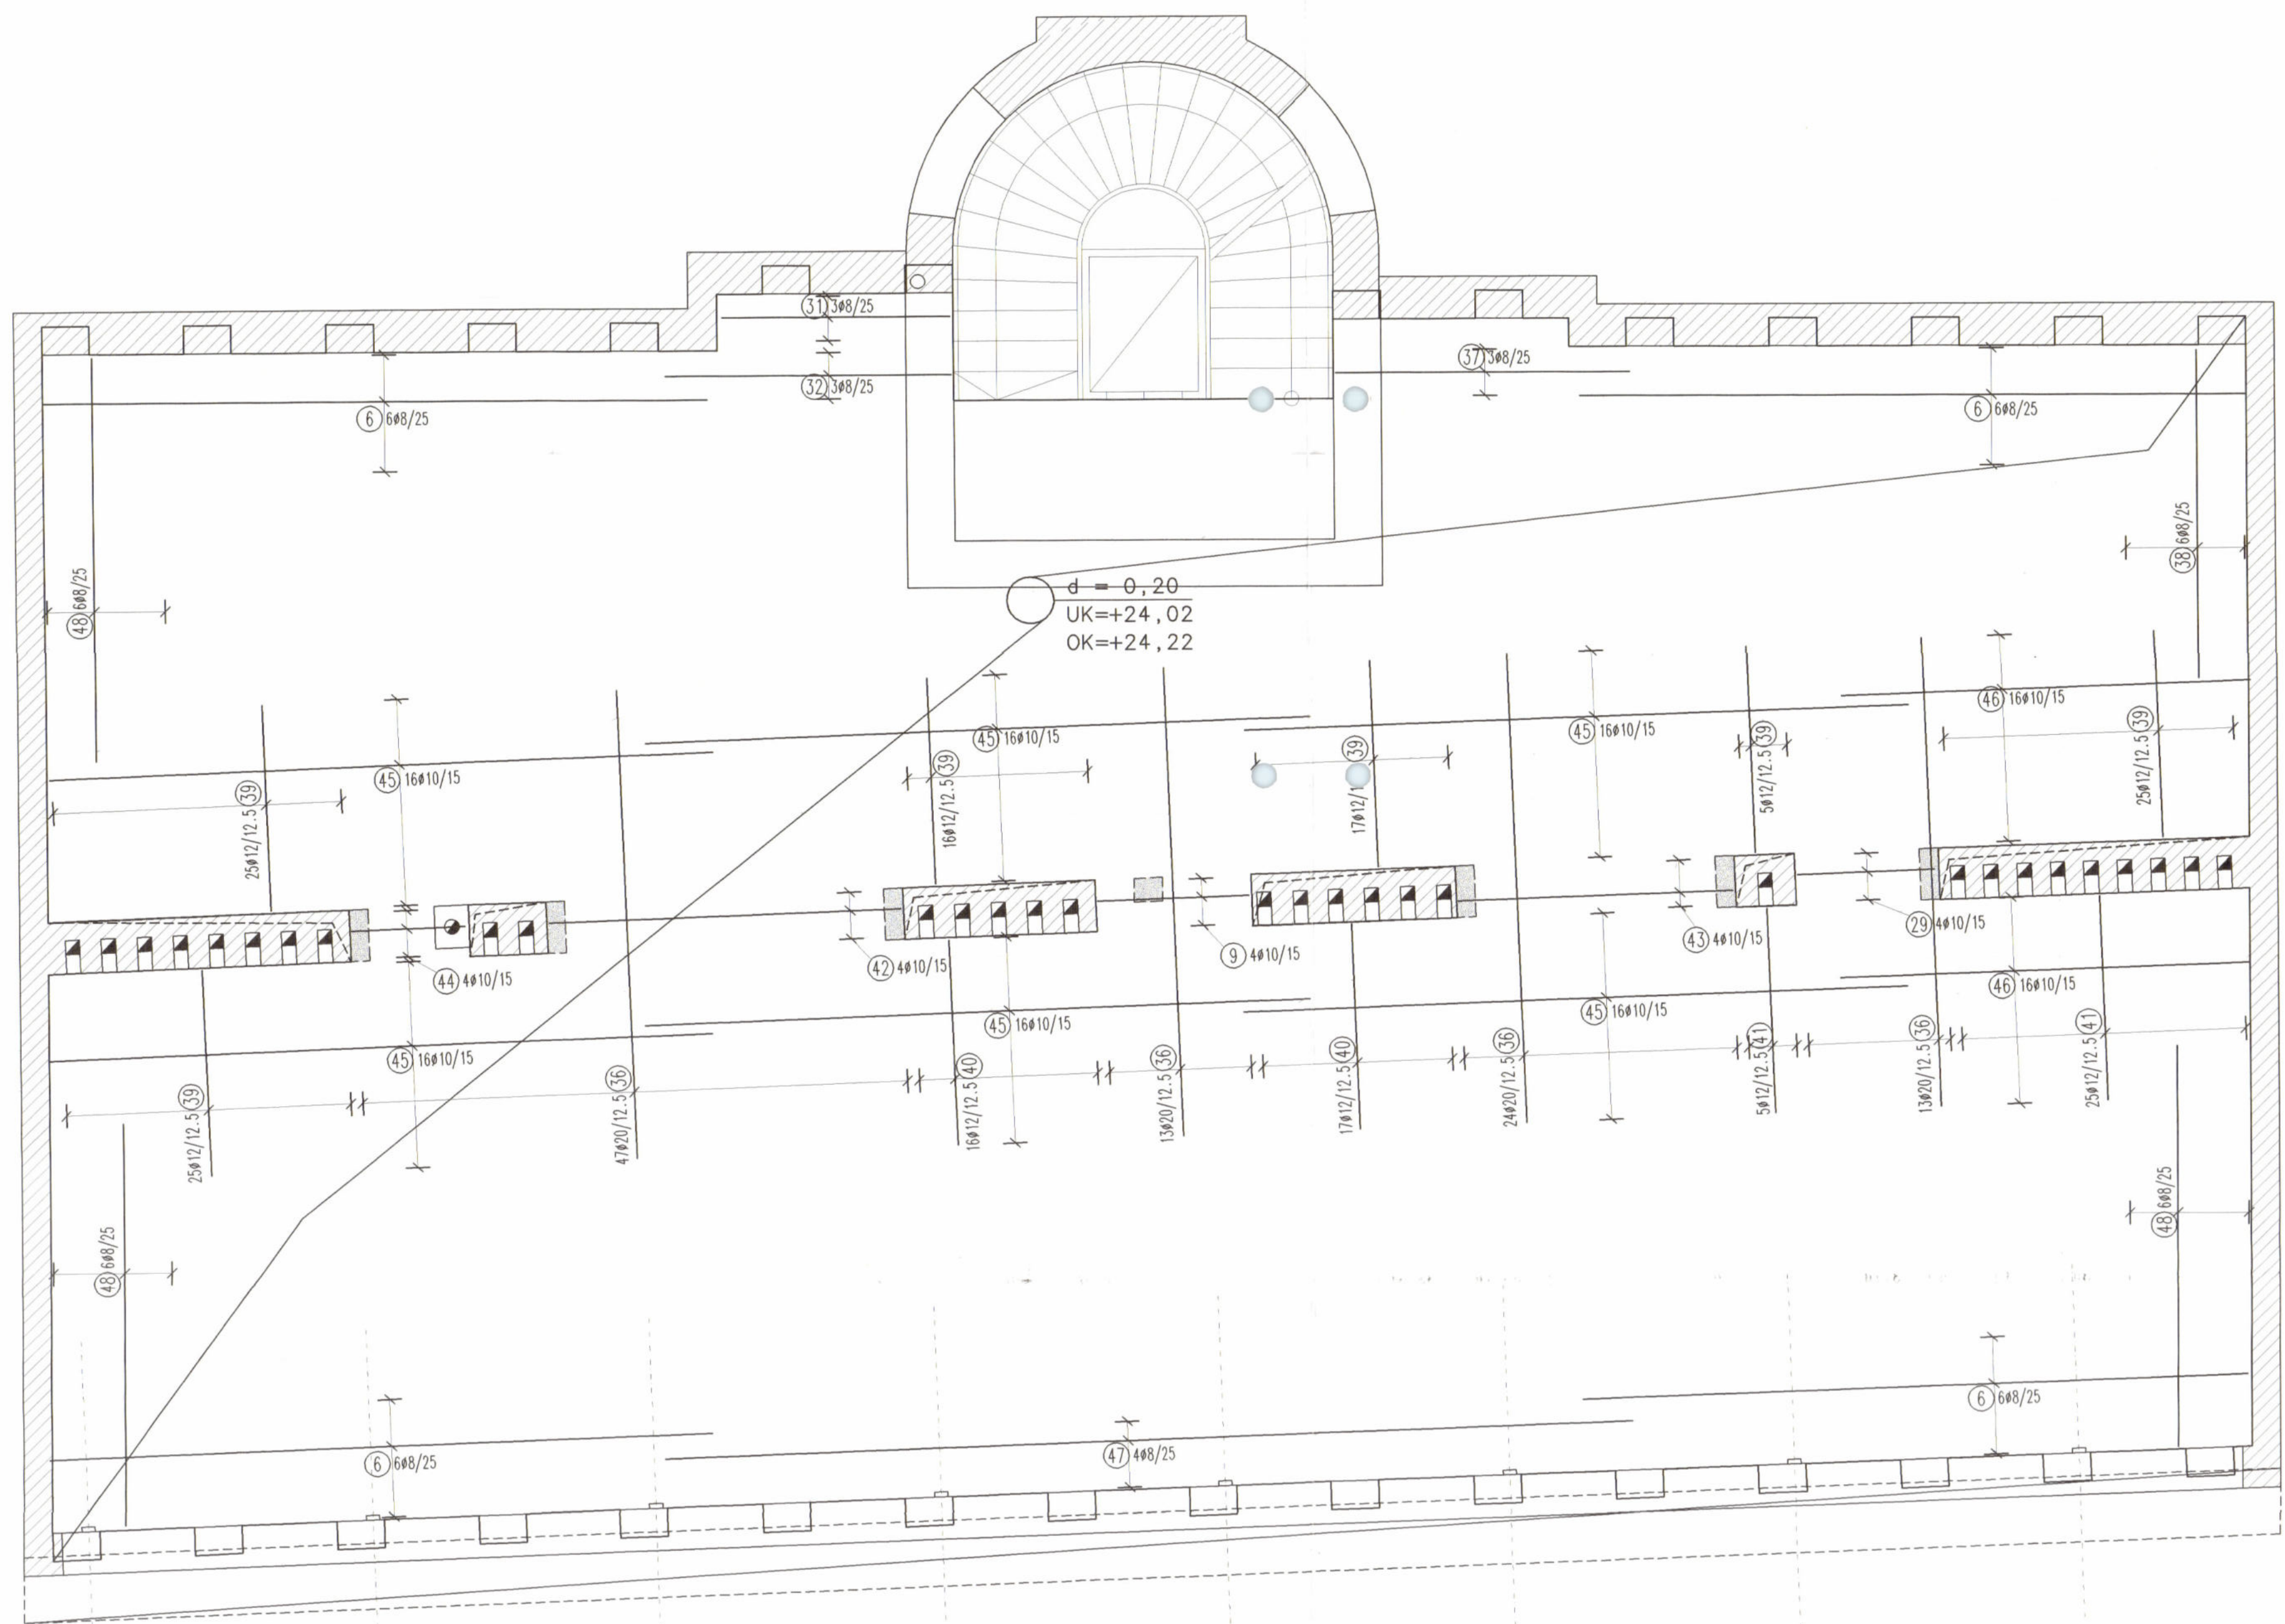

OBERE BEWEHRUNG

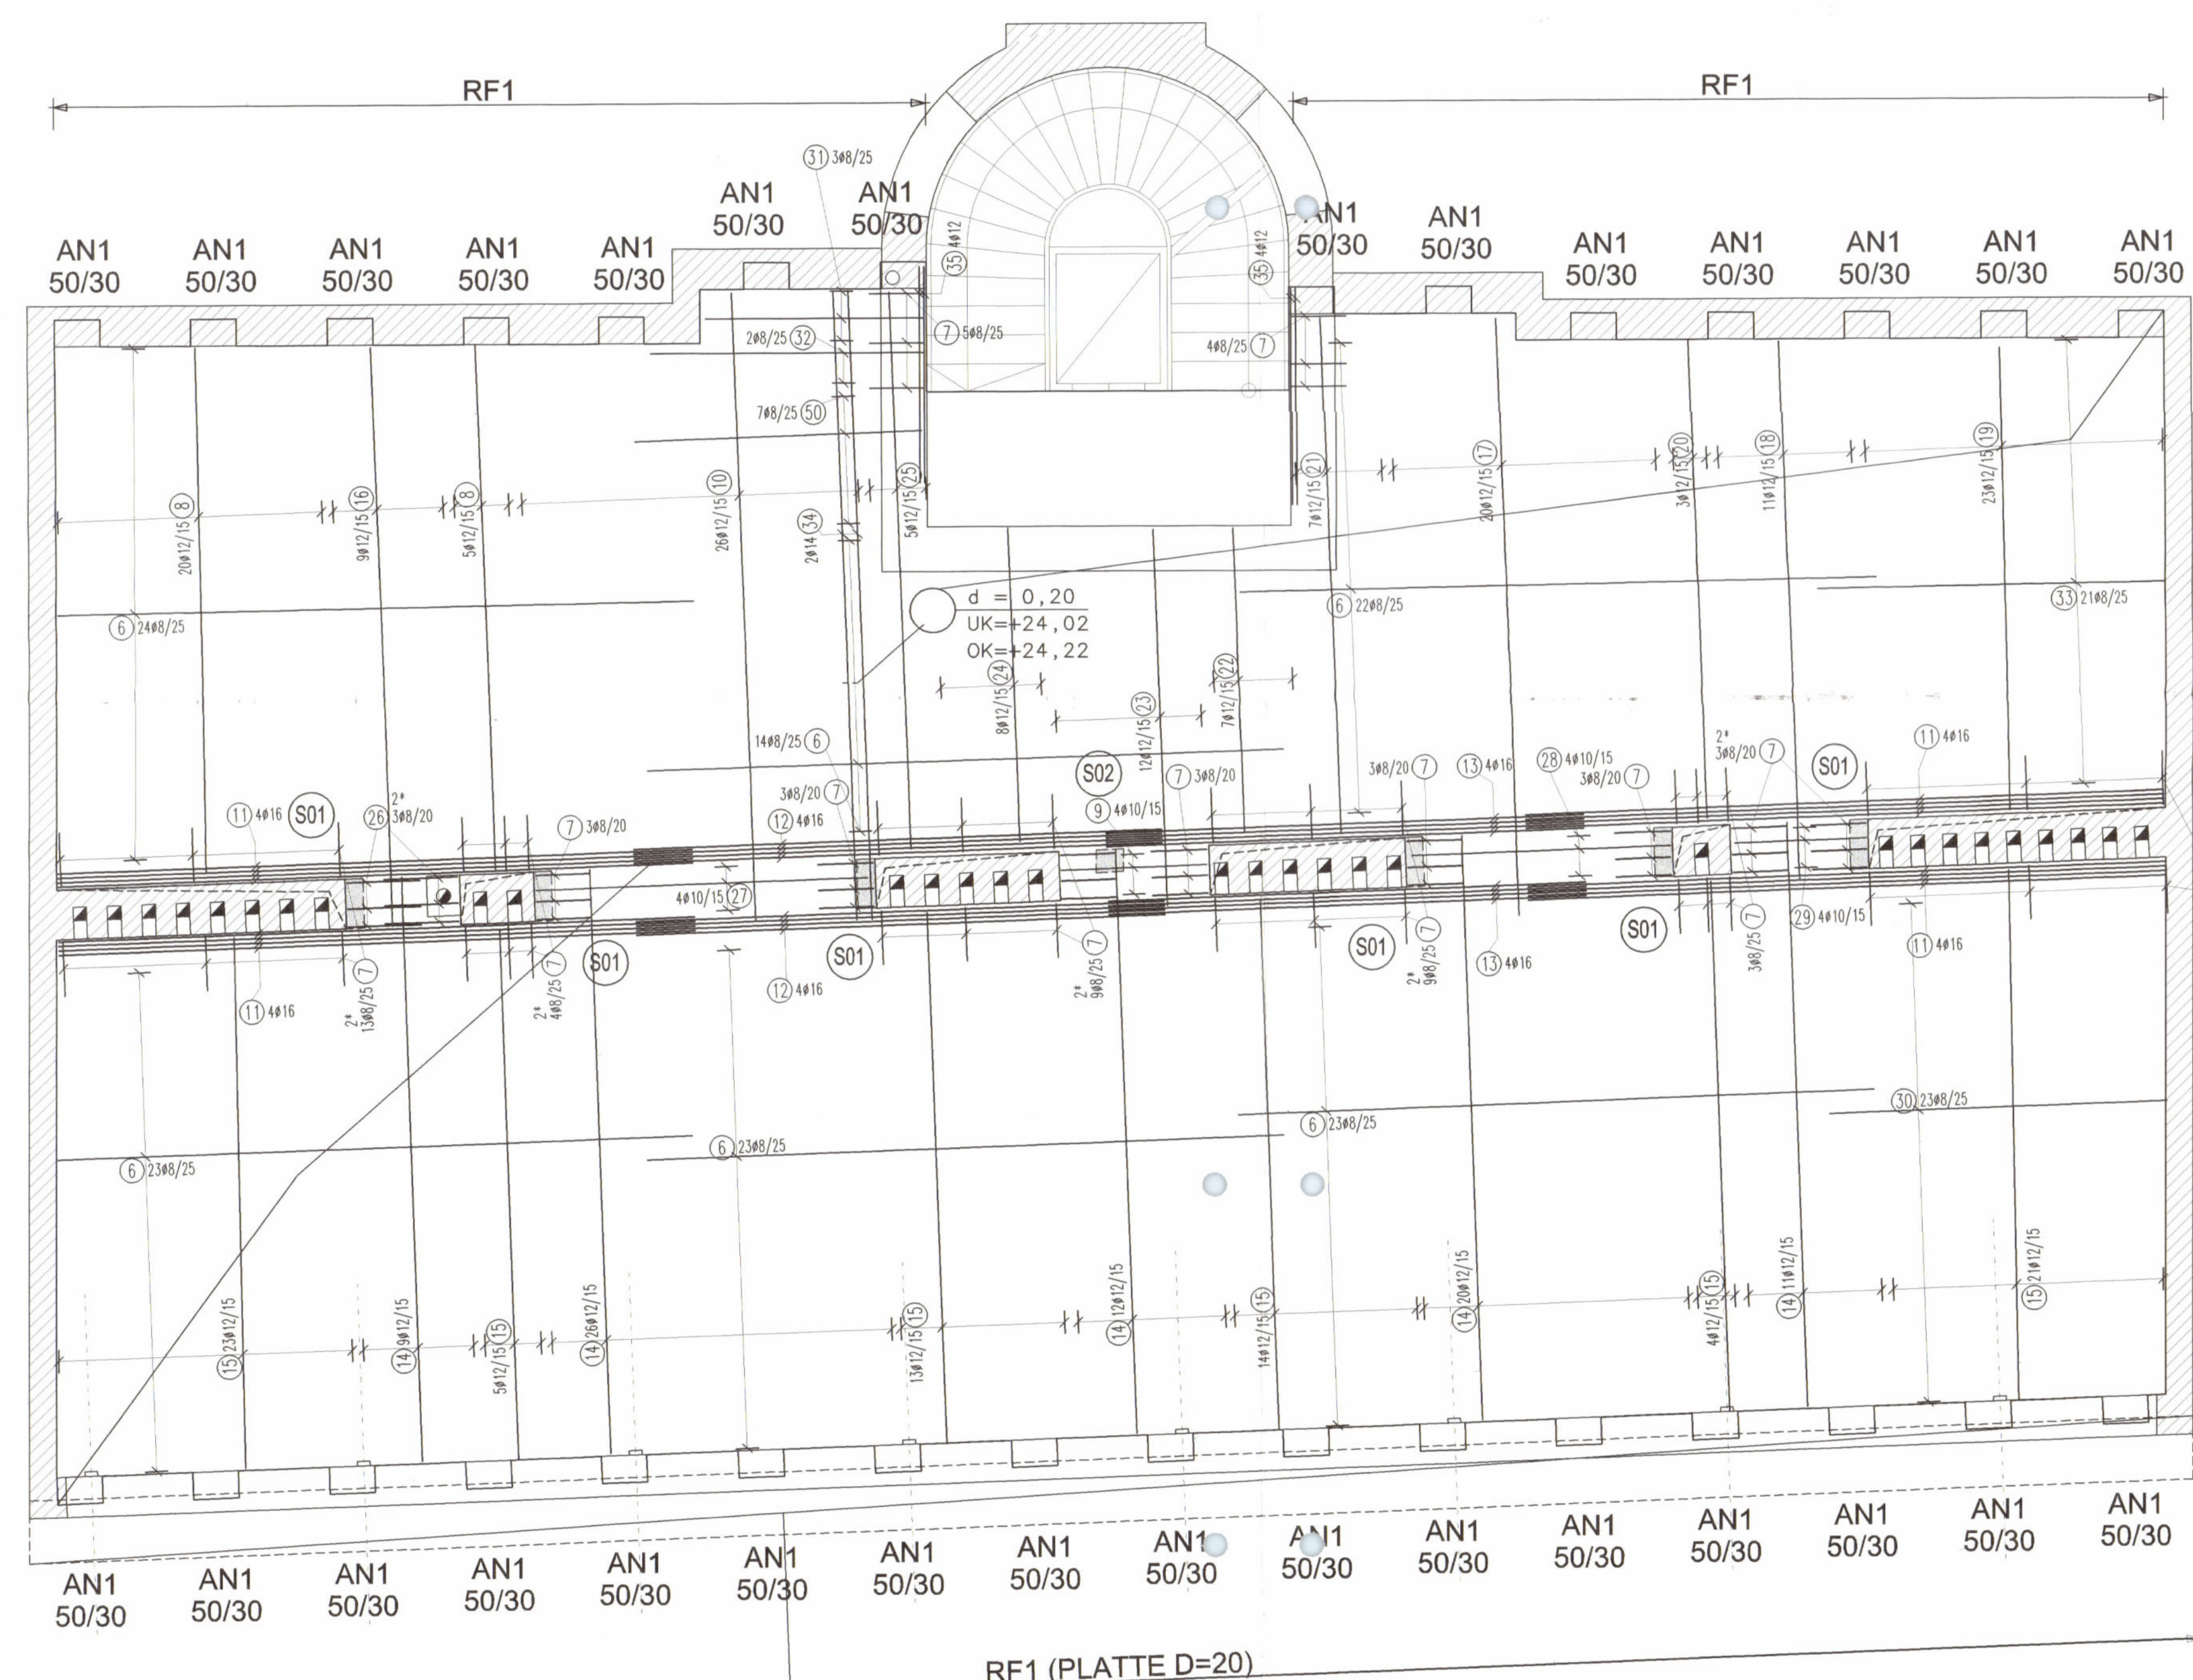

UNTERE BEWEHRUNG

Pos	Stk	Dm	Lng [m]	Biegeform (unmaßstäblich)	Ges. Lng [m]	Gewicht [kg]
1	21	12	14.00	1400	294.00	261.07
2	8	8	14.00	1400	112.00	44.24
3	120	12	2.60	13	312.00	277.06
4	120	8	1.38	43	165.60	65.41
5	220	8	1.80	13	396.00	156.42
6	153	8	7.00	700	1071.00	423.05
7	137	8	1.33	13	182.21	71.97
8	25	12	5.85	585	146.25	129.87
9	8	10	1.60	160	12.80	7.90
10	26	12	7.00	700	182.00	161.62
11	16	16	7.00	700	112.00	176.96
12	8	16	5.80	580	46.40	73.31
13	8	16	5.25	525	42.00	66.36
14	78	12	6.50	650	507.00	450.22
15	80	12	5.90	590	472.00	419.14
16	9	12	6.45	645	58.05	51.55
17	20	12	6.65	665	133.00	118.10
18	11	12	6.00	600	66.00	58.61
19	23	12	5.15	515	118.45	105.18
20	3	12	5.35	535	16.05	14.25
21	7	12	5.75	575	40.25	35.74
22	7	12	3.40	340	23.80	21.13
23	12	12	4.20	420	50.40	44.76
24	8	12	3.50	350	28.00	24.86
25	5	12	6.20	620	31.00	27.53
26	6	8	1.73	13	10.38	4.10
27	4	10	3.65	365	14.60	9.01
28	4	10	2.85	285	11.40	7.03
29	8	10	1.45	145	11.60	7.16
30	23	8	3.70	370	85.10	33.61
31	6	8	2.40	240	14.40	5.69
32	5	8	3.00	300	15.00	5.93
33	21	8	3.80	380	79.80	31.52
34	2	14	7.00	700	14.00	16.94
35	8	12	2.40	240	19.20	17.05
36	97	20	5.00	500	485.00	1197.95
37	3	8	3.10	310	9.30	3.67
38	6	8	3.50	350	21.00	8.30
39	113	12	2.20	220	248.60	220.76
40	33	12	2.19	219	72.27	64.18
41	38	12	2.18	218	65.40	58.08
42	4	10	3.71	371	14.84	9.16
43	4	10	2.90	290	11.60	7.16
44	4	10	1.20	120	4.80	2.96
45	96	10	7.00	700	672.00	414.62
46	32	10	4.30	430	137.60	84.90
47	4	8	10.20	1020	40.80	16.12
48	18	8	4.30	430	77.40	30.57
49	40	12	1.09	75	43.60	38.72
50	7	8	3.15	315	22.05	8.71

STAHL: Tempcore TC55		
STABDURCHMESSER	LÄNGE [m]	MASS [kg]
De = 8 mm	2302.04	909.3
De = 10 mm	891.24	549.9
De = 12 mm	2927.32	2599.5
De = 14 mm	14.00	16.9
De = 16 mm	200.40	316.6
De = 20 mm	485.00	1198.0
GESAMTMASS		5590.2 Kg
DURCHMESSERGRUPPEN		
De bis 8 mm		909.3 Kg
De bis 14 mm		3166.3 Kg
De größer 14 mm		1514.6 Kg
SCHNEIDEN UND BIEGEN		613.6 Kg
NUR SCHNEIDEN		4976.5 Kg
HAKENANZAHL		320 Stk
STÜCKANZAHL		1711 Stk
ZUSATZBEWEHRUNG: Distanzstreifen		
Bezeichnung	Stück	Gewicht
DS90	130	92.30
Gesamtgewicht:		92.30

FOLGENDE POS. SIND ÖRTLICH ABZULÄNGEN (ÜBERGRIFF MIND. 60 CM):

① 21x12 Lg=14.00

② 3x8 Lg=14.00

Distanzstreifen d=20

STÜCK: 130

TYPE: DS 90

BIEGEANWEISUNG NACH ÖNORM B 4700

D=5ds


2R=20ds

Alle Biegebögen sind von außen nach außen gemessen.


MATERIALGÜTEN:		BETONDECKUNG	
(WENN NICHT ANDERS ANGEZEIGT)		PLANNIEBESTIMMT GEM. ÖNORM B4700-WENN NICHT ANDERS ANGEZEIGT	
BETON:	C30/37		2,5CM
STABSTAHL:	BSt 550	MATTENÜBERGRIFFE (WENN NICHT ANDERS ANGEZEIGT)	
MATTEN:	M 55	IN LÄNGSRICHTUNG:	40 cm
LAGENSCHHEMA F. DECKENBEWEHRUNG:		IN QUERRICHTUNG:	40 cm
BEZEICHNUNG DER BEWEHRUNGSLAGEN:		! UNFALLSCHUTZ !	
VERLEGERICHTUNG:		GERADE NACH OBEN ENDE: STÄBE (STÜCKE) WISSEN ABGERÜCKT ODER ZUSÄTZLICH HAKENFÖRMIG (OHNE VERRINGERUNG DER MATTLÄNGE) ANGEBOGEN WERDEN.	
PILANDARSTELLUNG		BETRIELET AUSGEFÜHRT!!!	
LEGENDE:		① STABSTAHL-POSITION	② MATTEN-POSITION
BEMERKUNGEN:			
1. BIEGEMASSE SIND AUSSEMASSE			
2. VORSTELLER: WENN NICHT ANDERS ANGEZEIGT, STÖSSE BEI EINHALTUNG DER ANGEZEIGTEN ÜBERGRIFFE VERSETZEN.			
3. KRÜMMEN, AUFBIEGEN, WINKELHAKEN, SCHLEIFEN UND SCHLINGEN SIND NACH ÖNORM B4700 TEIL 8 BZW. ÖNORM B4700 AUSZUFÜHREN.			
4. NICHT HERAUSGEFÖRMTE EISEN SIND BIEGEFORM A			

LEGENDE	
	STAHLBETON
	MAUERWERK DARÜBER
	MAUERWERK
	STAHLBETON DARÜBER


AUFLAGERNISCHEN AN1

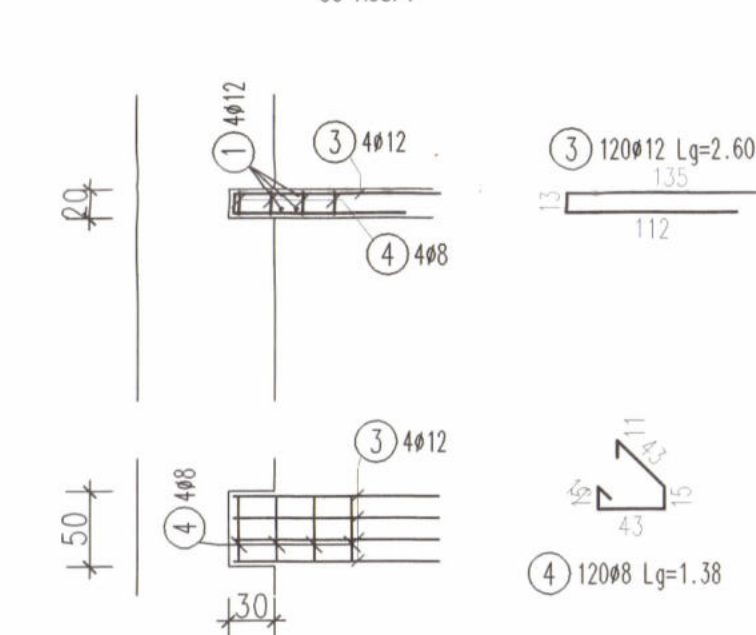


RANDEINFASSUNG RF1 / d=20

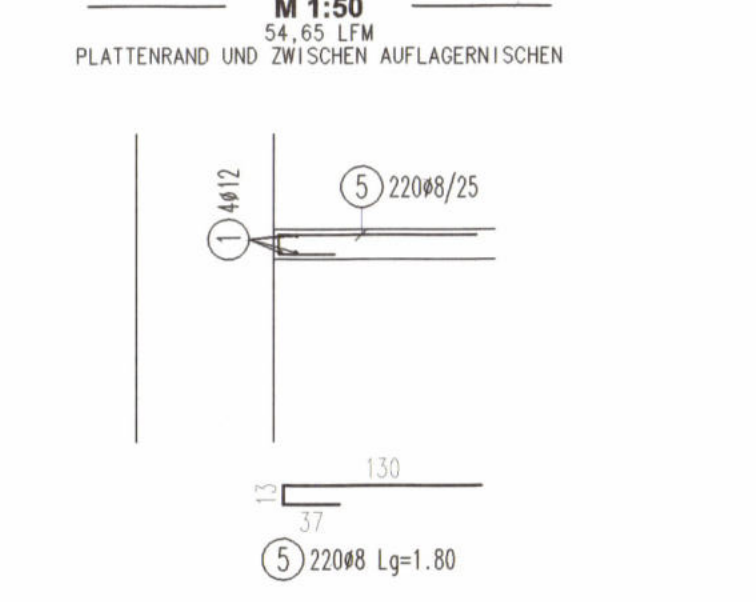

STÜTZENSTECKER S01

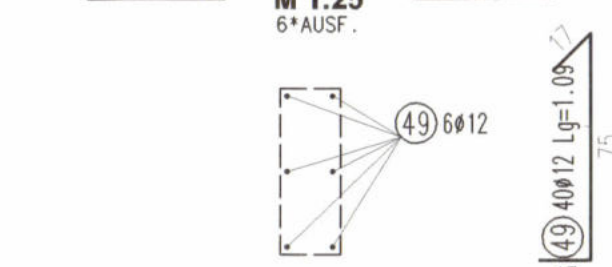

STÜTZENSTECKER S02

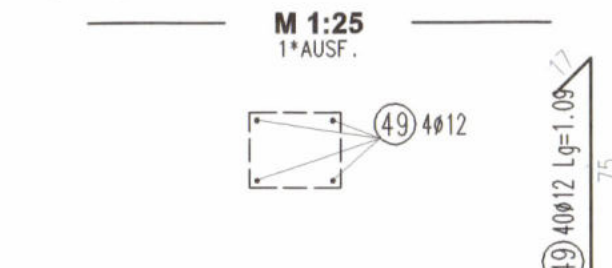

3	-	-	-
2	-	-	-
1	-	-	-
0	STB	10.05.05	Erstausgabe
Index	gez.	Datum	Inhalt

Zum Konsens

Diese Unterlagen bestätigen sich auf die zur ZL

MA 37/1-2269-1/2004

bezeichnete Pläne / angeforderte Fortschrittsanforderungen

Jägerb

JÄGERB

Datum 10.05.2005	Massstab 1 : 50	Plangröße	Dateiname	gezeichnet STB
Planinhalt Bewehrungsplan Decke über 4.OG				Plannummer B -001/0
Projekt Dachgeschossausbau Landesgerichtsstr. 6				Geschäftszahl 2004/33
Planverfasser D.I. ANDRZEJ GLOGOWSKI ZIVILINGENIEUR F. BAUWESEN OTHELLOGASSE 17/19 A-1200 WIEN TELEFON +43 (0)1-615 39 93 FAX +43 (0)1-615 39 93				