PLANGRÖSSE 0,43 x 2,14 = 0,92m²

unterliegt dem § 119 A d. BO f. Wien

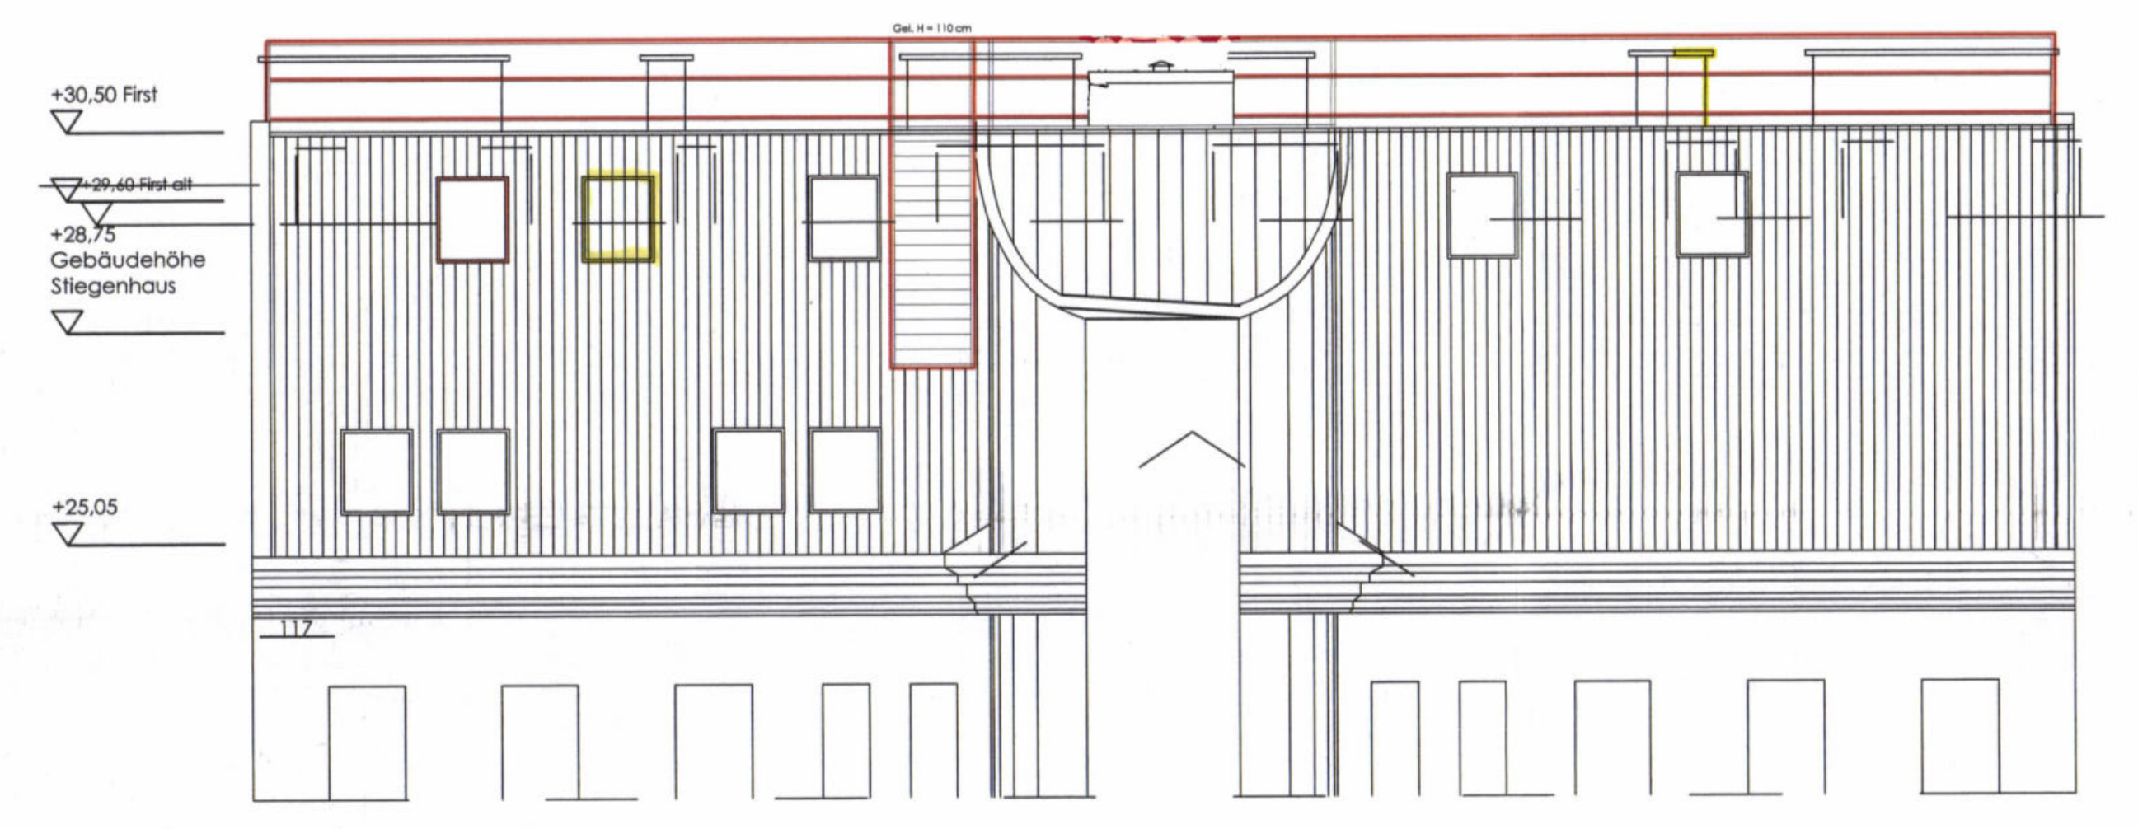
+30,50 First
+29,40 First alt
+28,15 Gebäudehöhe Stiegenhaus
+25,05
Gel. H = 110 cm

HOFANSICHT

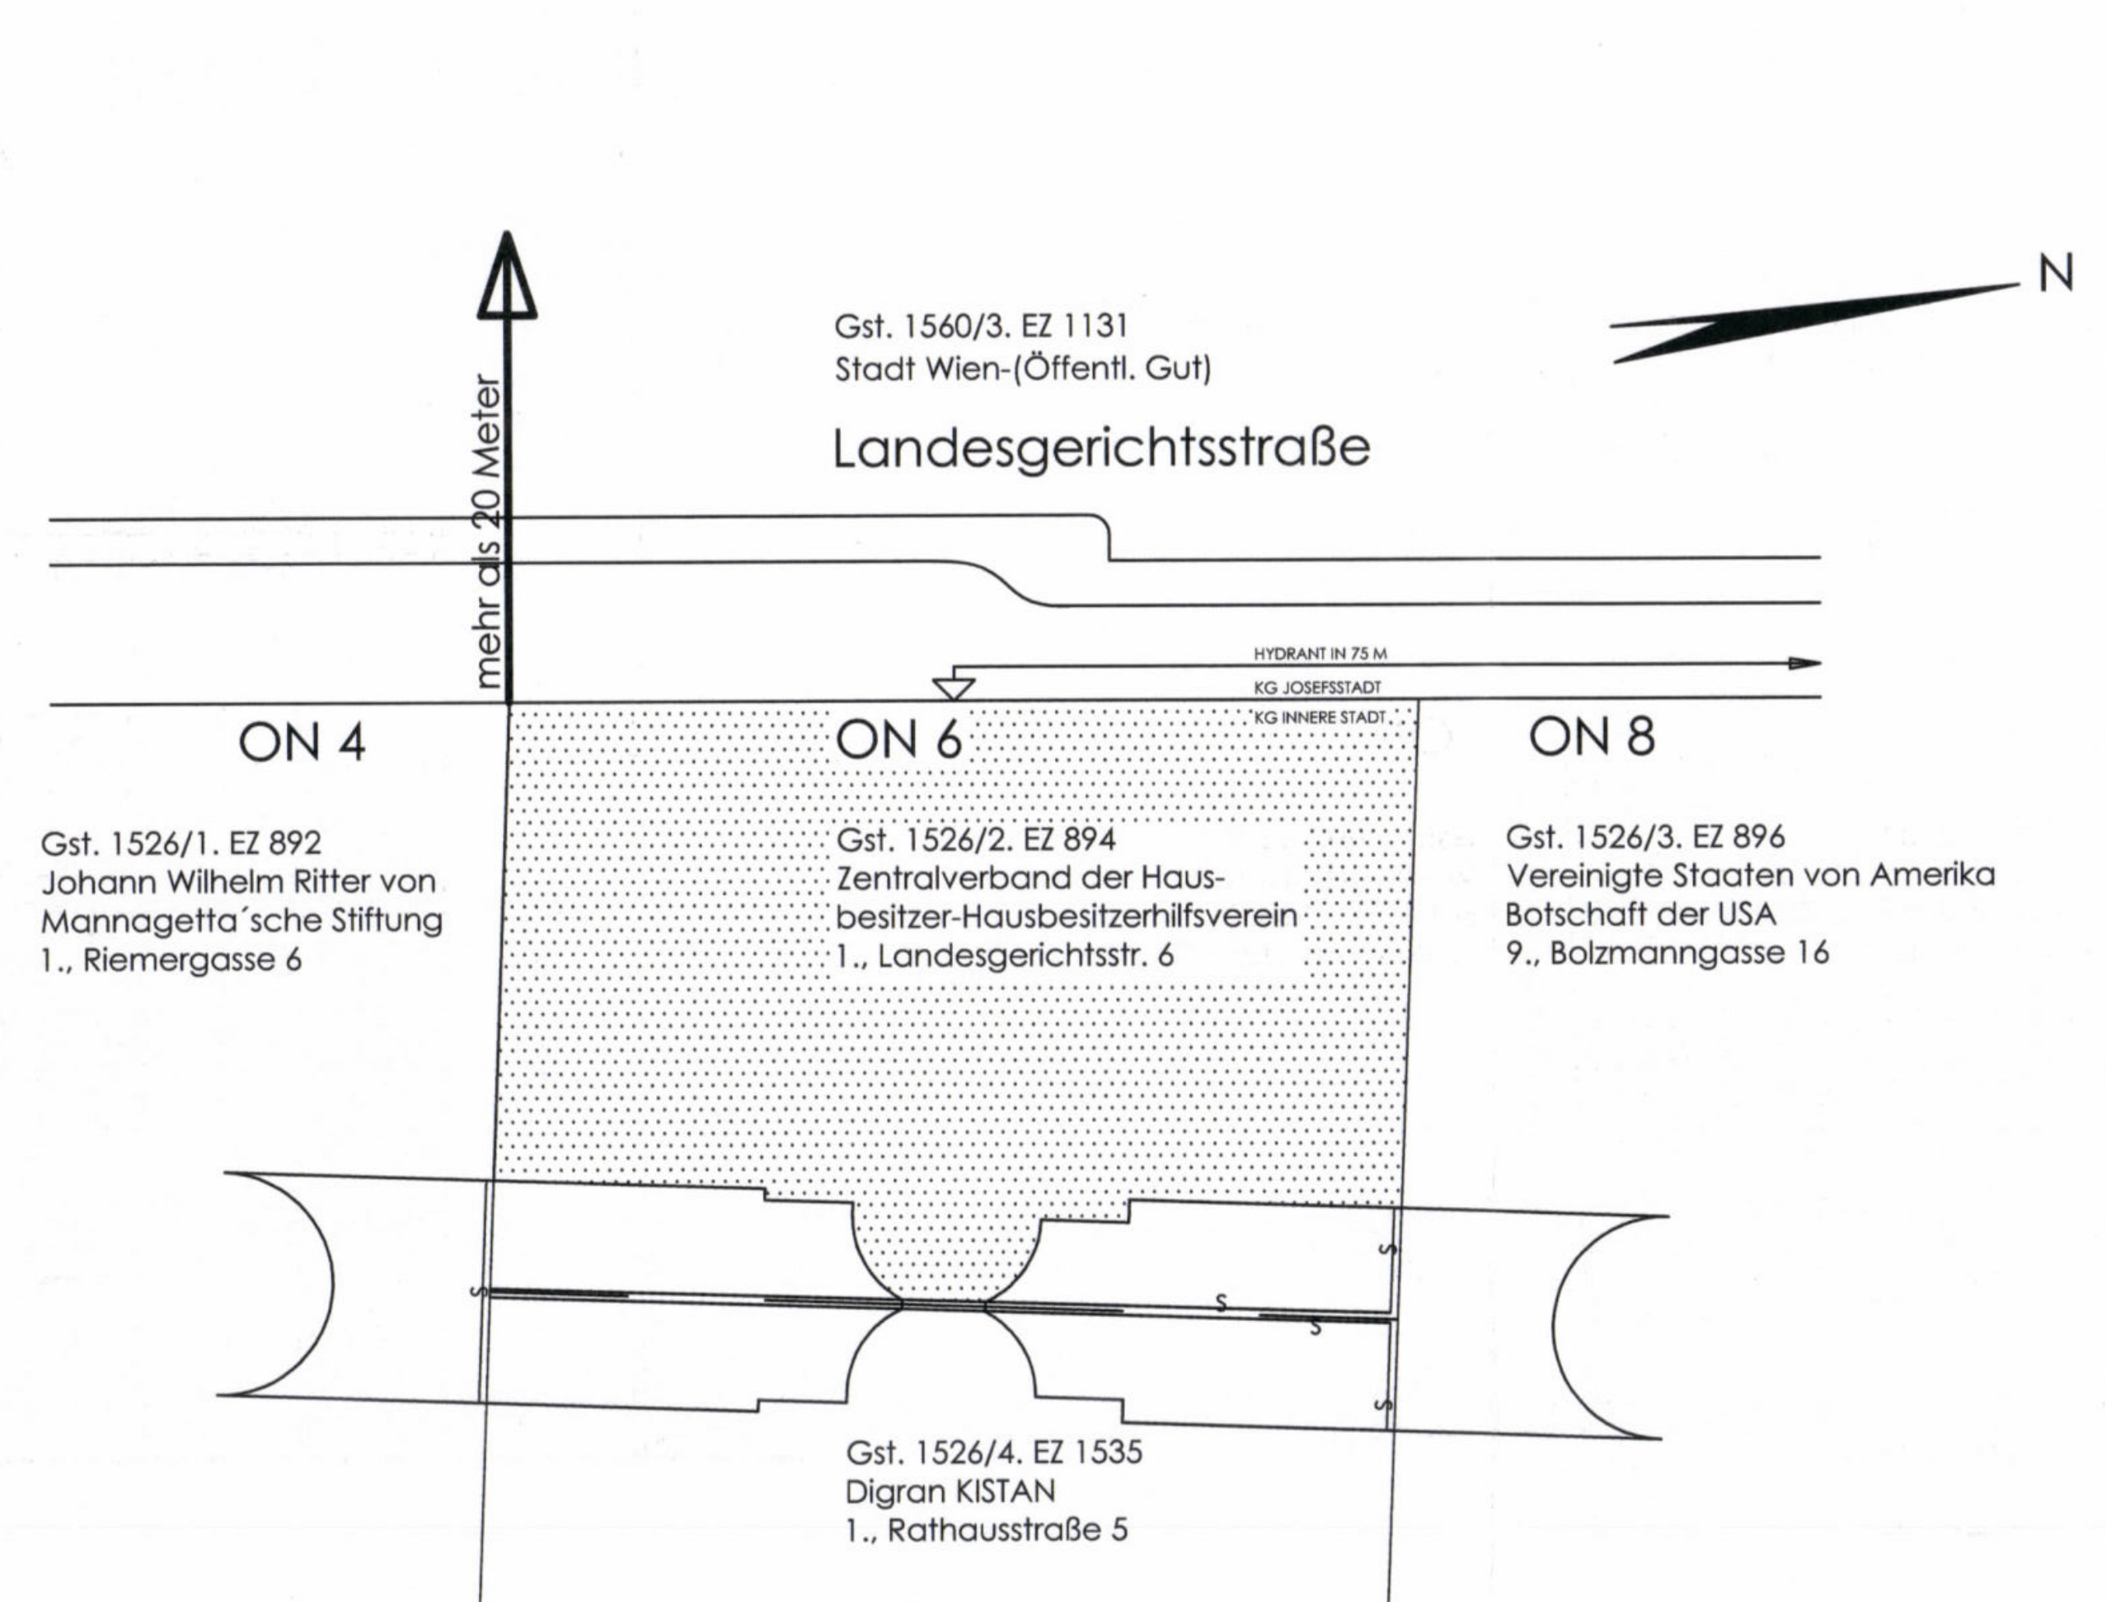
N
mehr als 20 Meter
Gst. 1560/3, EZ 1131
Stadt Wien-(Öffentl. Gut)
Landesgerichtsstraße
HYDRANT IN 75 M
KG JOSEFSTADT
KG INNERE STADT
ON 4
ON 6
ON 8
Gst. 1526/1, EZ 892
Johann Wilhelm Ritter von Mannagetta'sche Stiftung
1., Riemergasse 6
Gst. 1526/2, EZ 894
Zentralverband der Hausbesitzer-Hausbesitzerhilfsverein
1., Landesgerichtsstr. 6
Gst. 1526/3, EZ 896
Vereinigte Staaten von Amerika
Botschaft der USA
9., Bolzmanngasse 16
Gst. 1526/4, EZ 1535
Digran KISTAN
1., Rathausstraße 5

LAGEPLAN 1:250

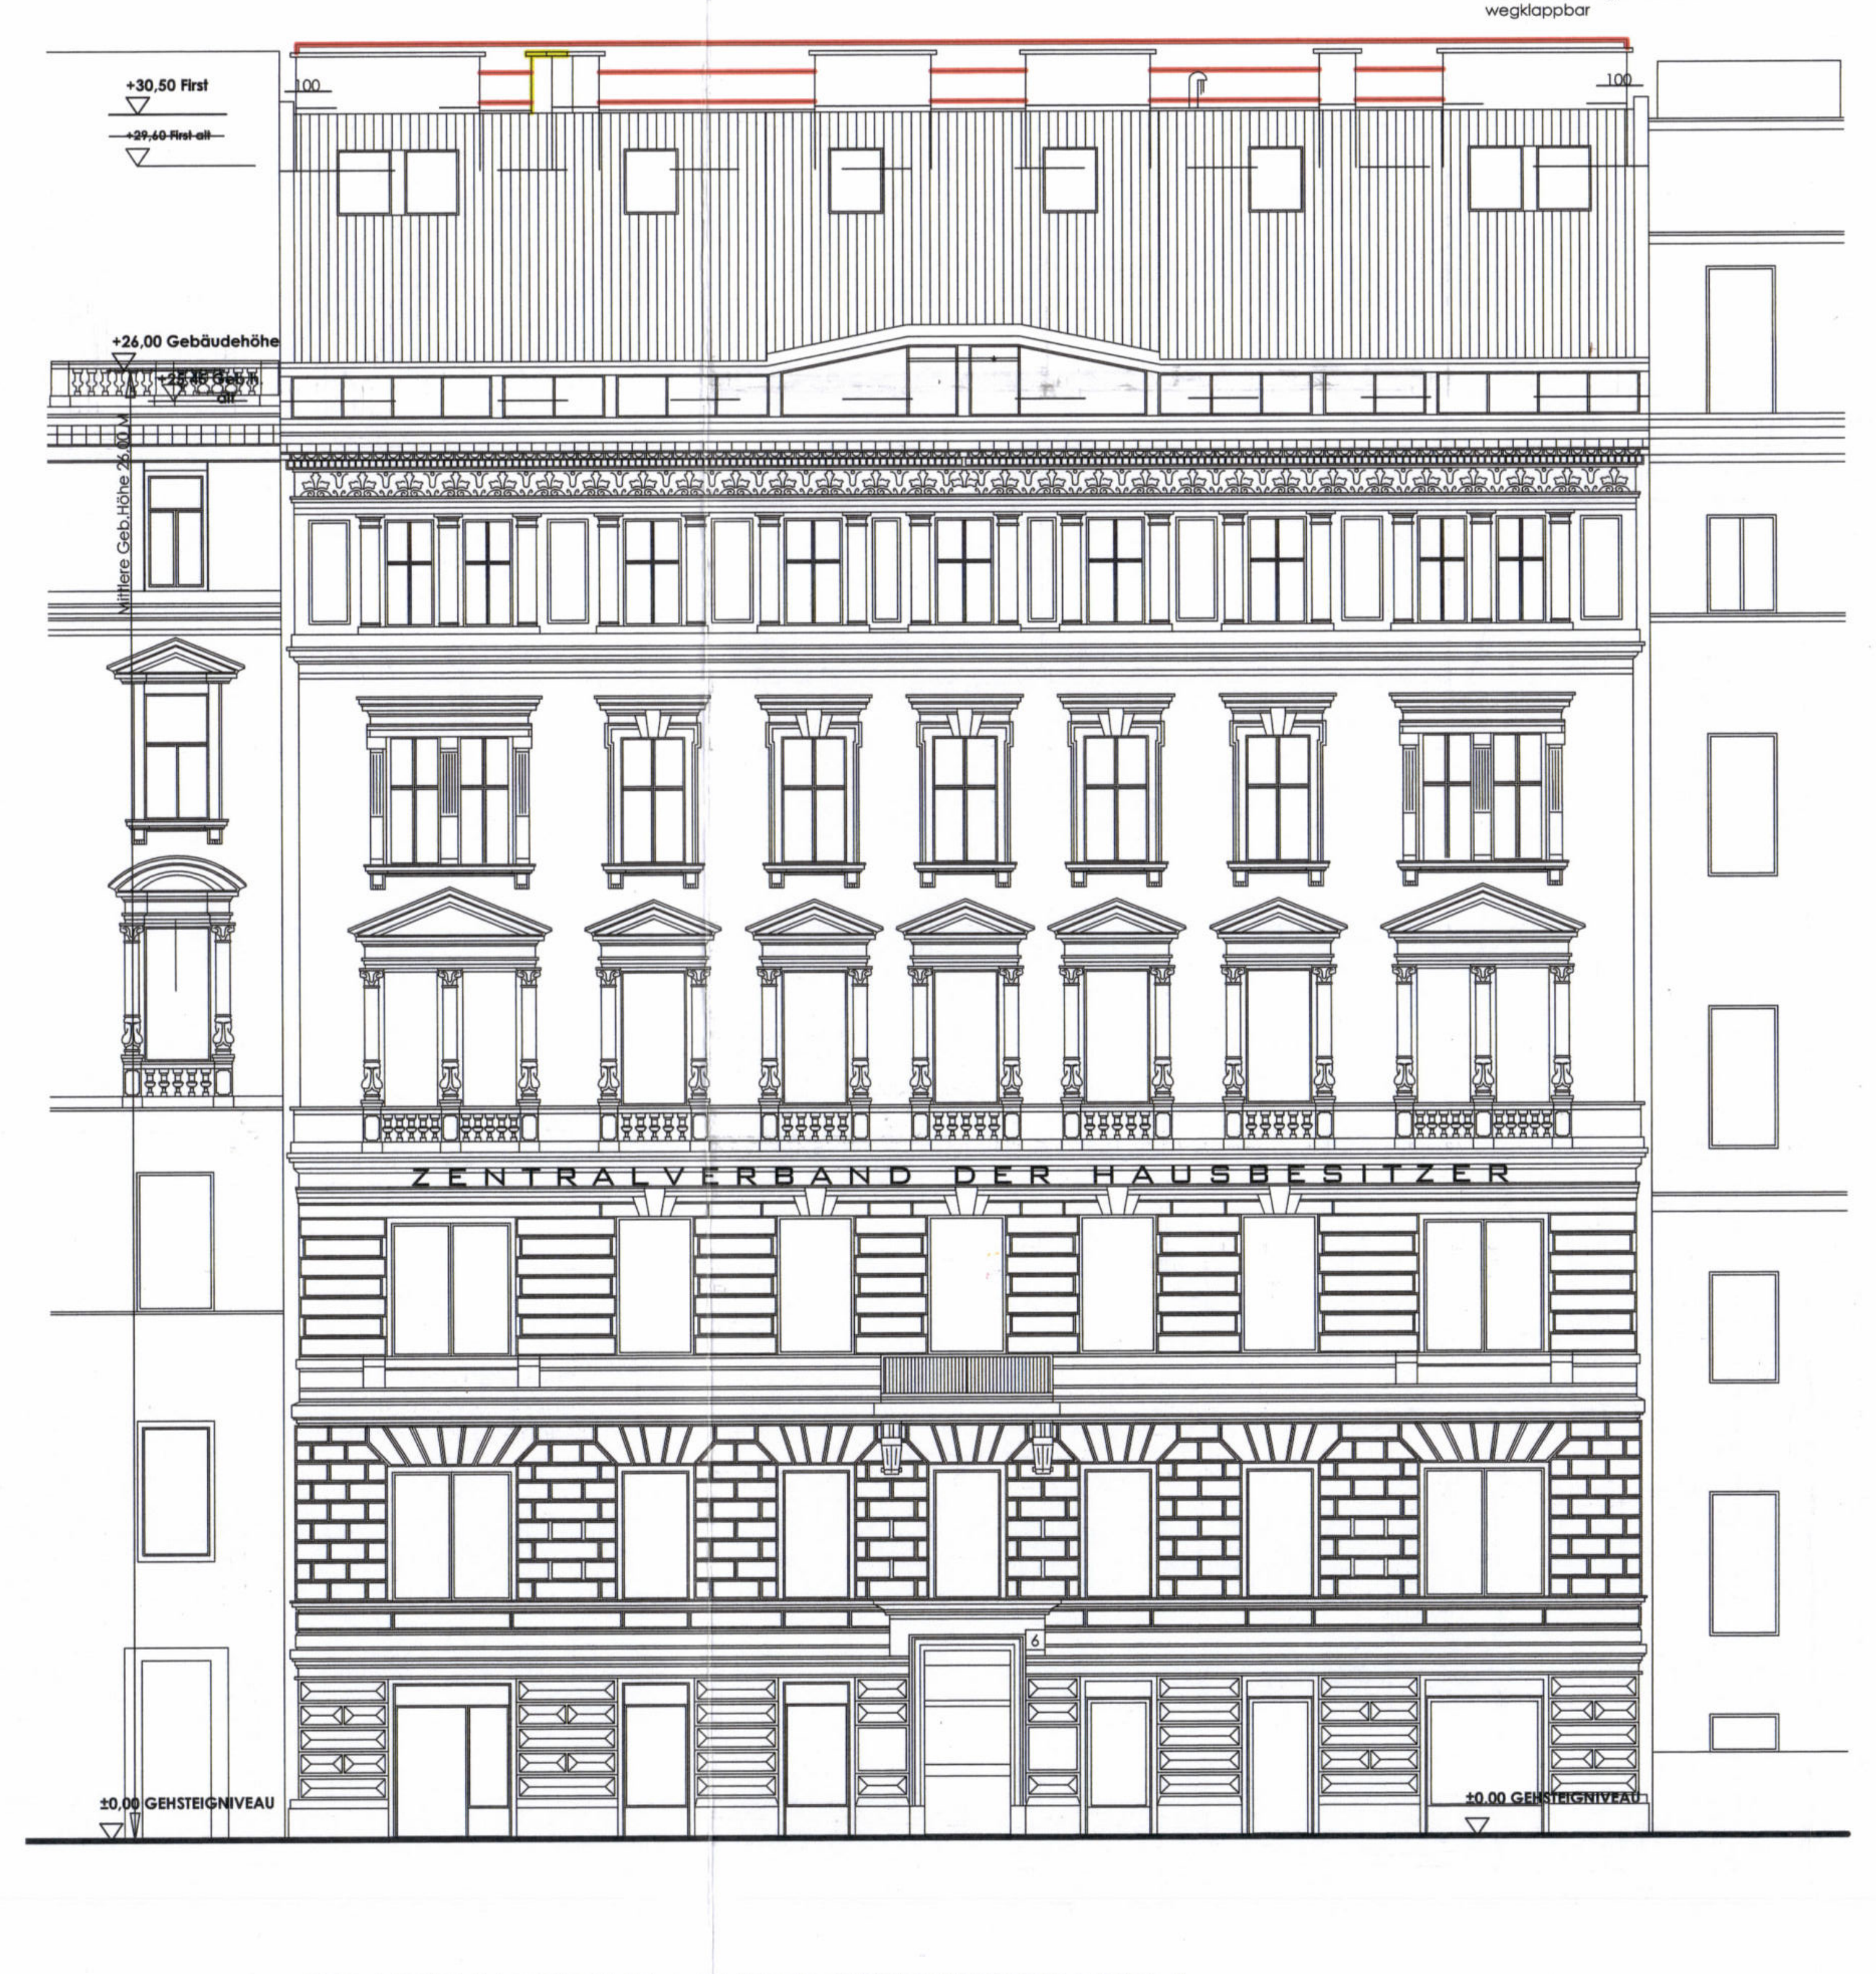
* Absturzsicherung h= 105 cm wegklappbar
+30,50 First
+29,40 First alt
+26,00 Gebäudehöhe
Mittlere Geb.Höhe 26,60 M
ZENTRALVERBAND DER HAUSBESITZER
±0,00 GEHSTEIGNIVEAU
6

STRASSENANSICHT LANDESGERICHTSSTRASSE 6

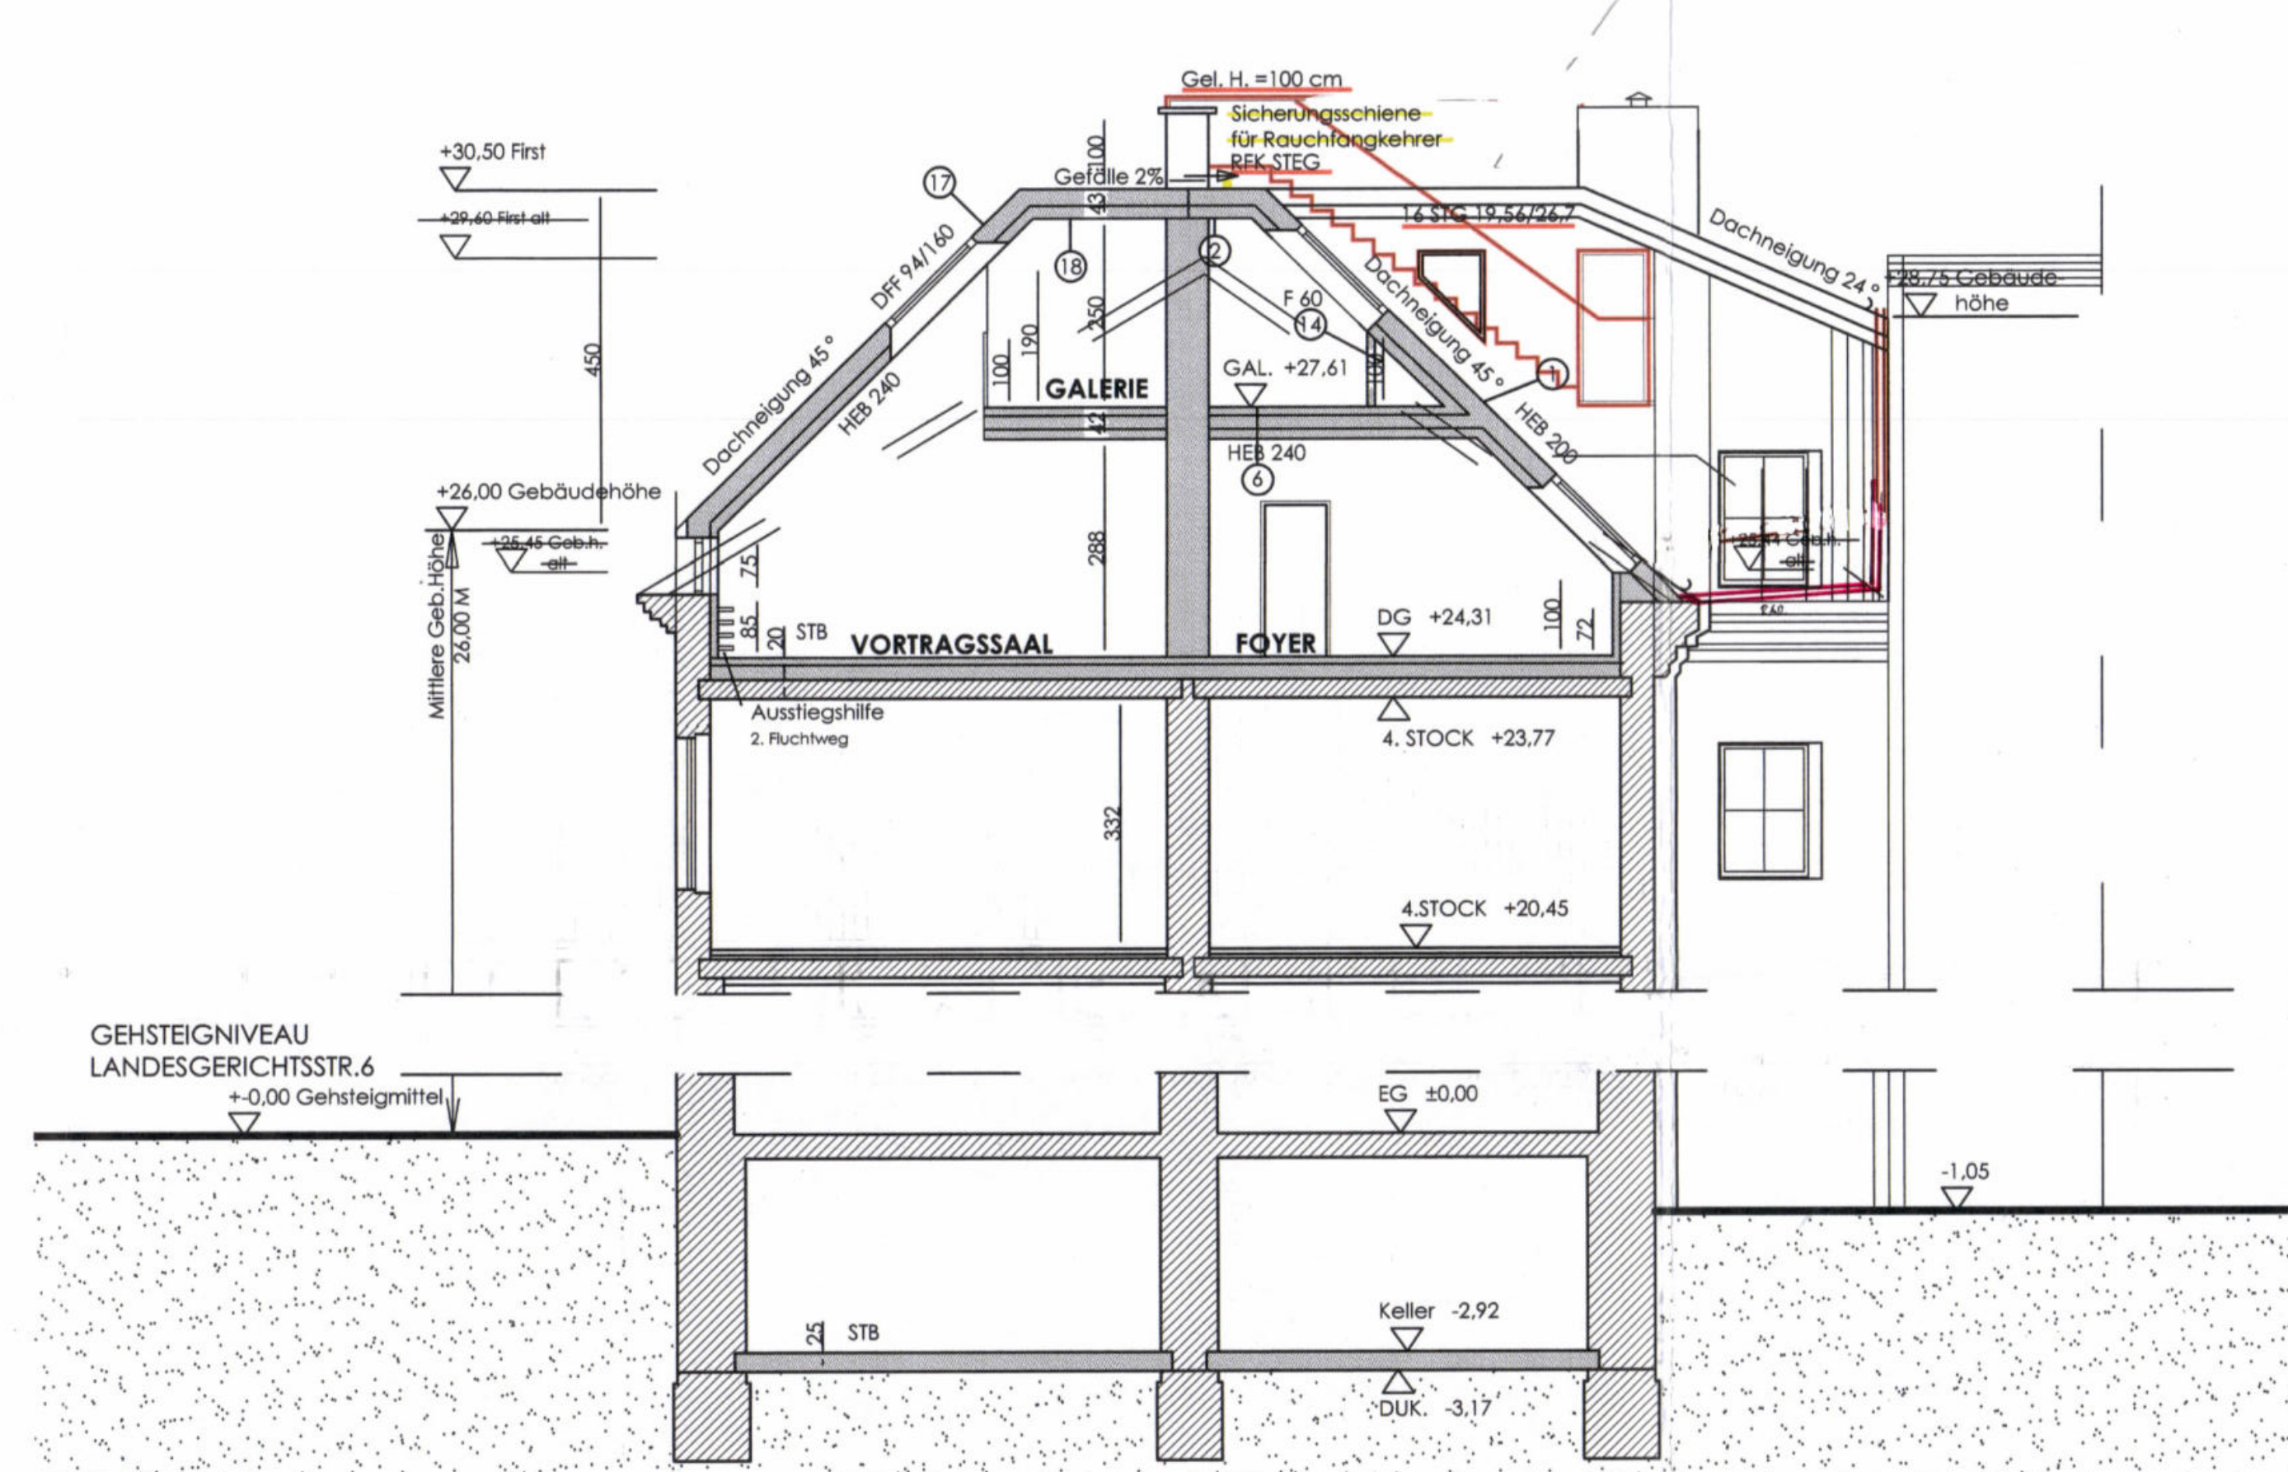
Gel. H. =100 cm
Sicherungsschiene für Rauchfangkehrer
RFK STEG
Gefälle 2%
Dachneigung 45°
Dachneigung 24°
HEB 200
HEB 240
DFF 94/160
GALERIE
GAL. +27,61
VORTRAGSSAAL
FOYER
Ausstiegshilfe 2. Fluchtweg
STB
+30,50 First
+29,40 First alt
+26,00 Gebäudehöhe
Mittlere Geb.Höhe 26,00 M
GEHSTEIGNIVEAU LANDESGERICHTSSTR.6 +0,00 Gehsteigmittel
DG +24,31
4. STOCK +23,77
4.STOCK +20,45
EG ±0,00
Keller -2,92
DUK. -3,17
-1,05
450
332
288

SCHNITT A - A

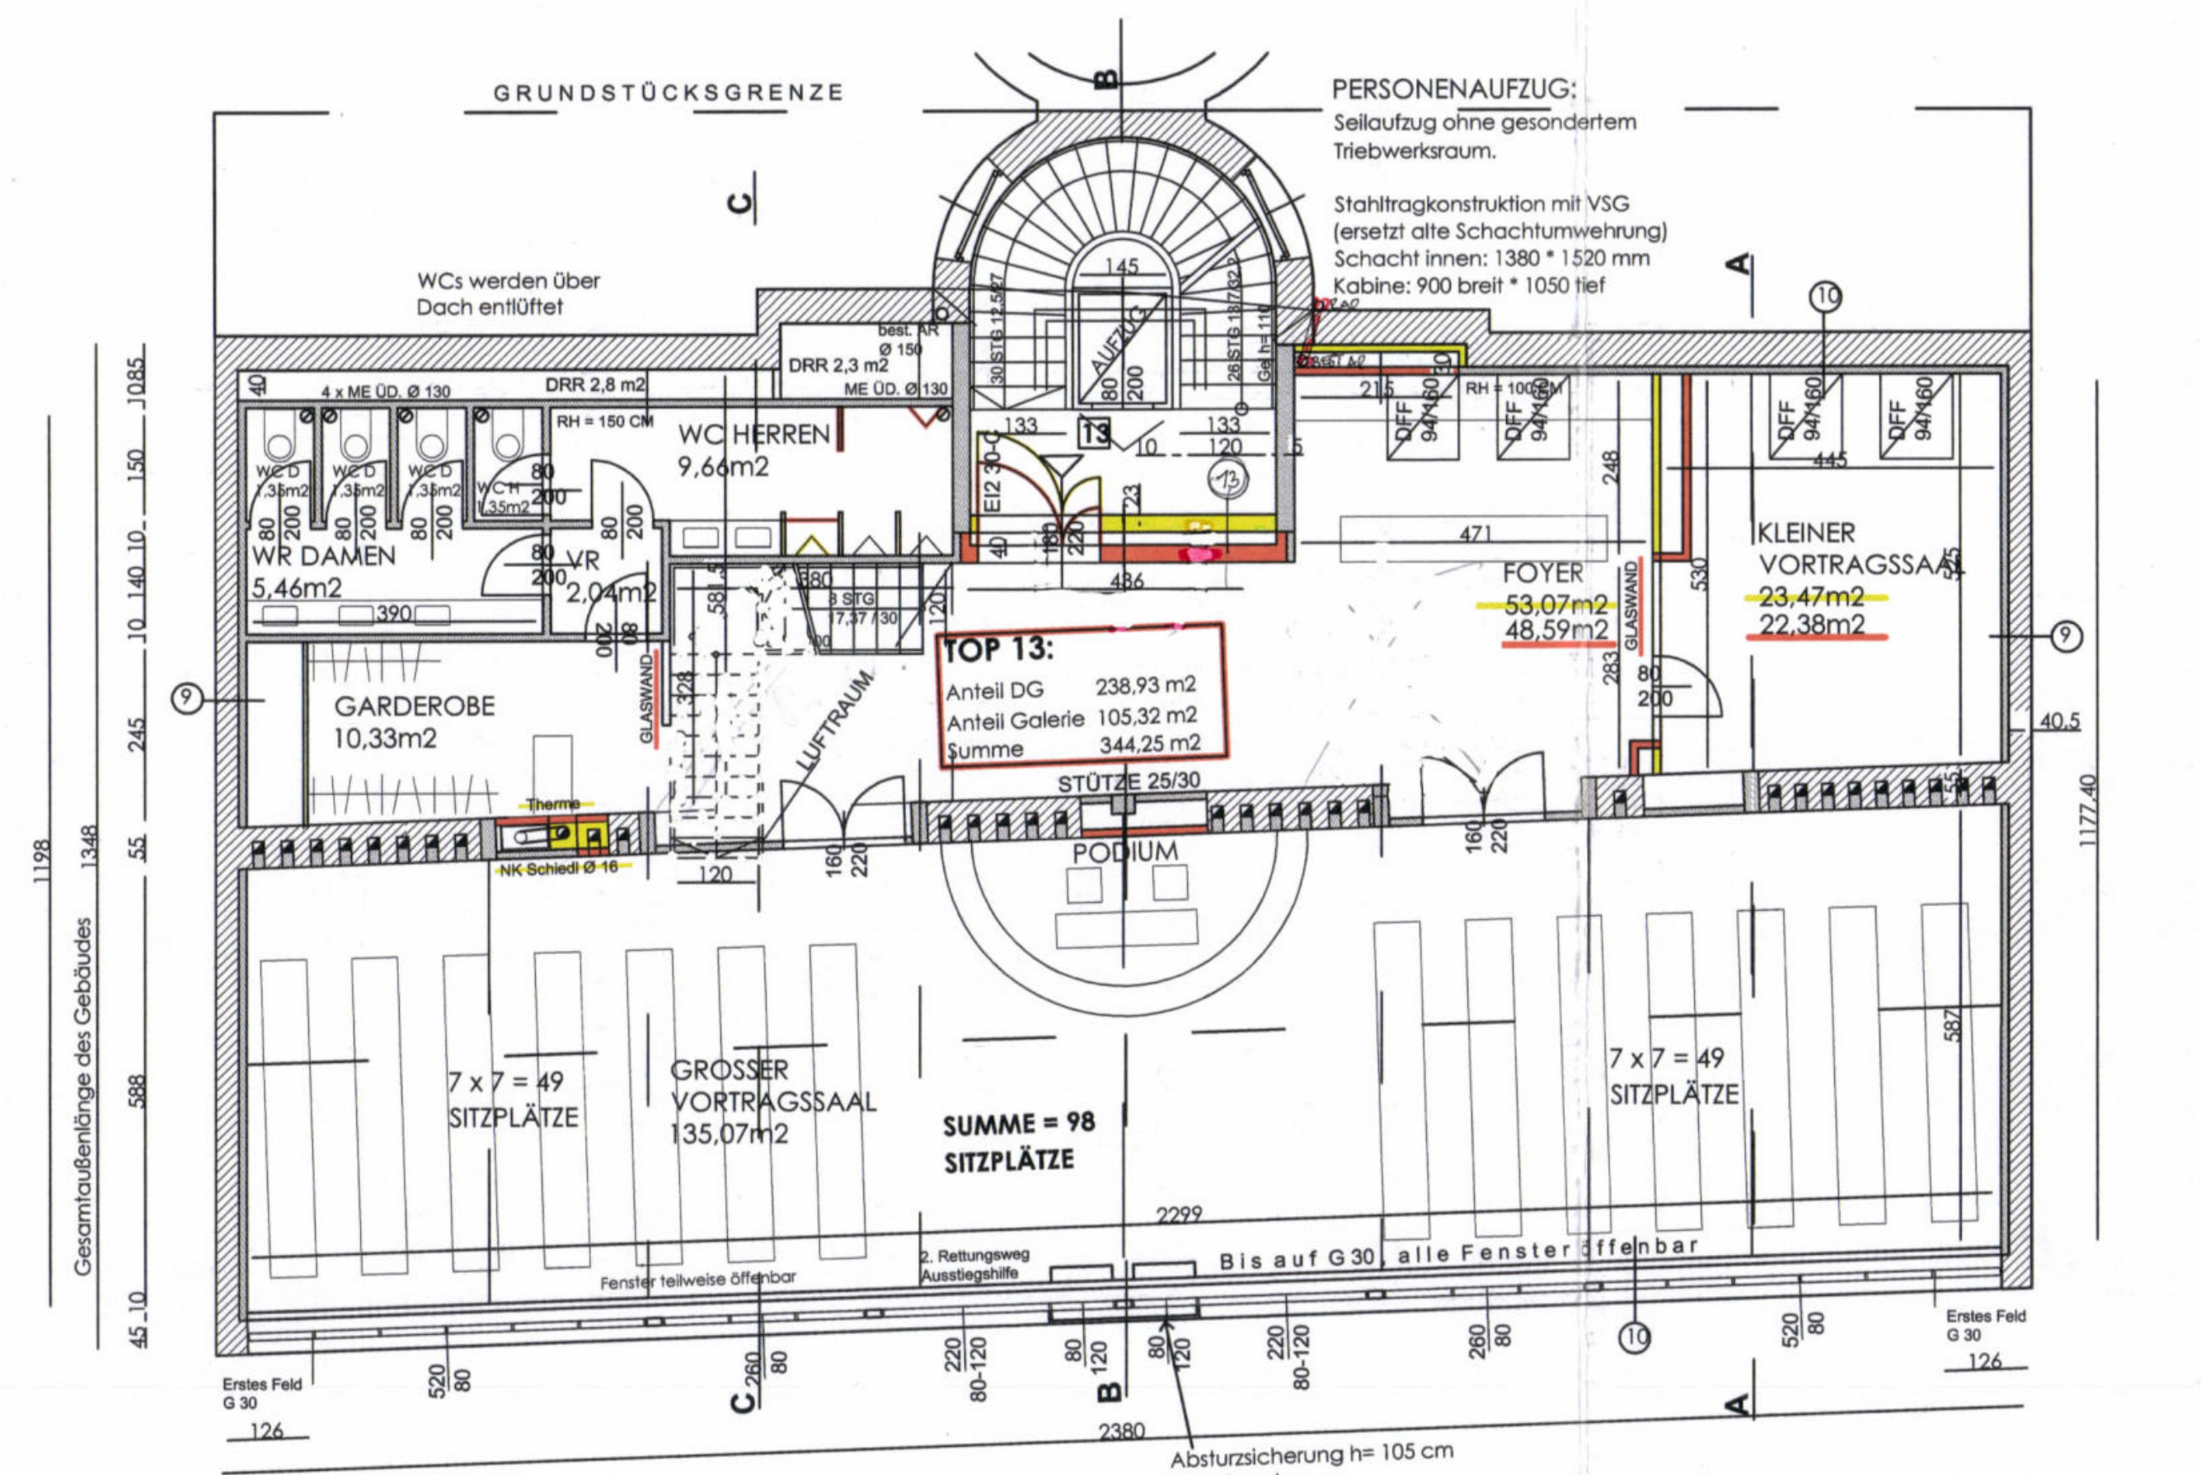
GRUNDSTÜCKSGRENZE
PERSONENAUFZUG:
Seilaufzug ohne gesonderten Triebwerksraum.
Stahlkonstruktion mit VSG (ersetzt alte Schachtumwehrung)
Kabine: 900 breit x 1050 tief
WCs werden über Dach entlüftet
WC HERREN 9,66m2
WC DAMEN 5,46m2
VR 2,74m2
GARDEROBE 10,33m2
FOYER 53,09m2 48,79m2
KLEINER VORTRAGSSAAL 23,47m2 22,38m2
GROSSER VORTRAGSSAAL 135,07m2
TOP 13:
Anteil DG 238,93 m2
Anteil Galerie 105,32 m2
Summe 344,25 m2
STÜTZE 25/30
PODIUM
LUFTRAUM
GLASWAND
7 x 7 = 49 SITZPLÄTZE
7 x 7 = 49 SITZPLÄTZE
SUMME = 98 SITZPLÄTZE
Bis auf G 30 alle Fenster öffenbar
Absturzsicherung h= 105 cm wegklappbar
Gesamtaußenlänge des Gebäudes
1348
1198

GRUNDRISS DG

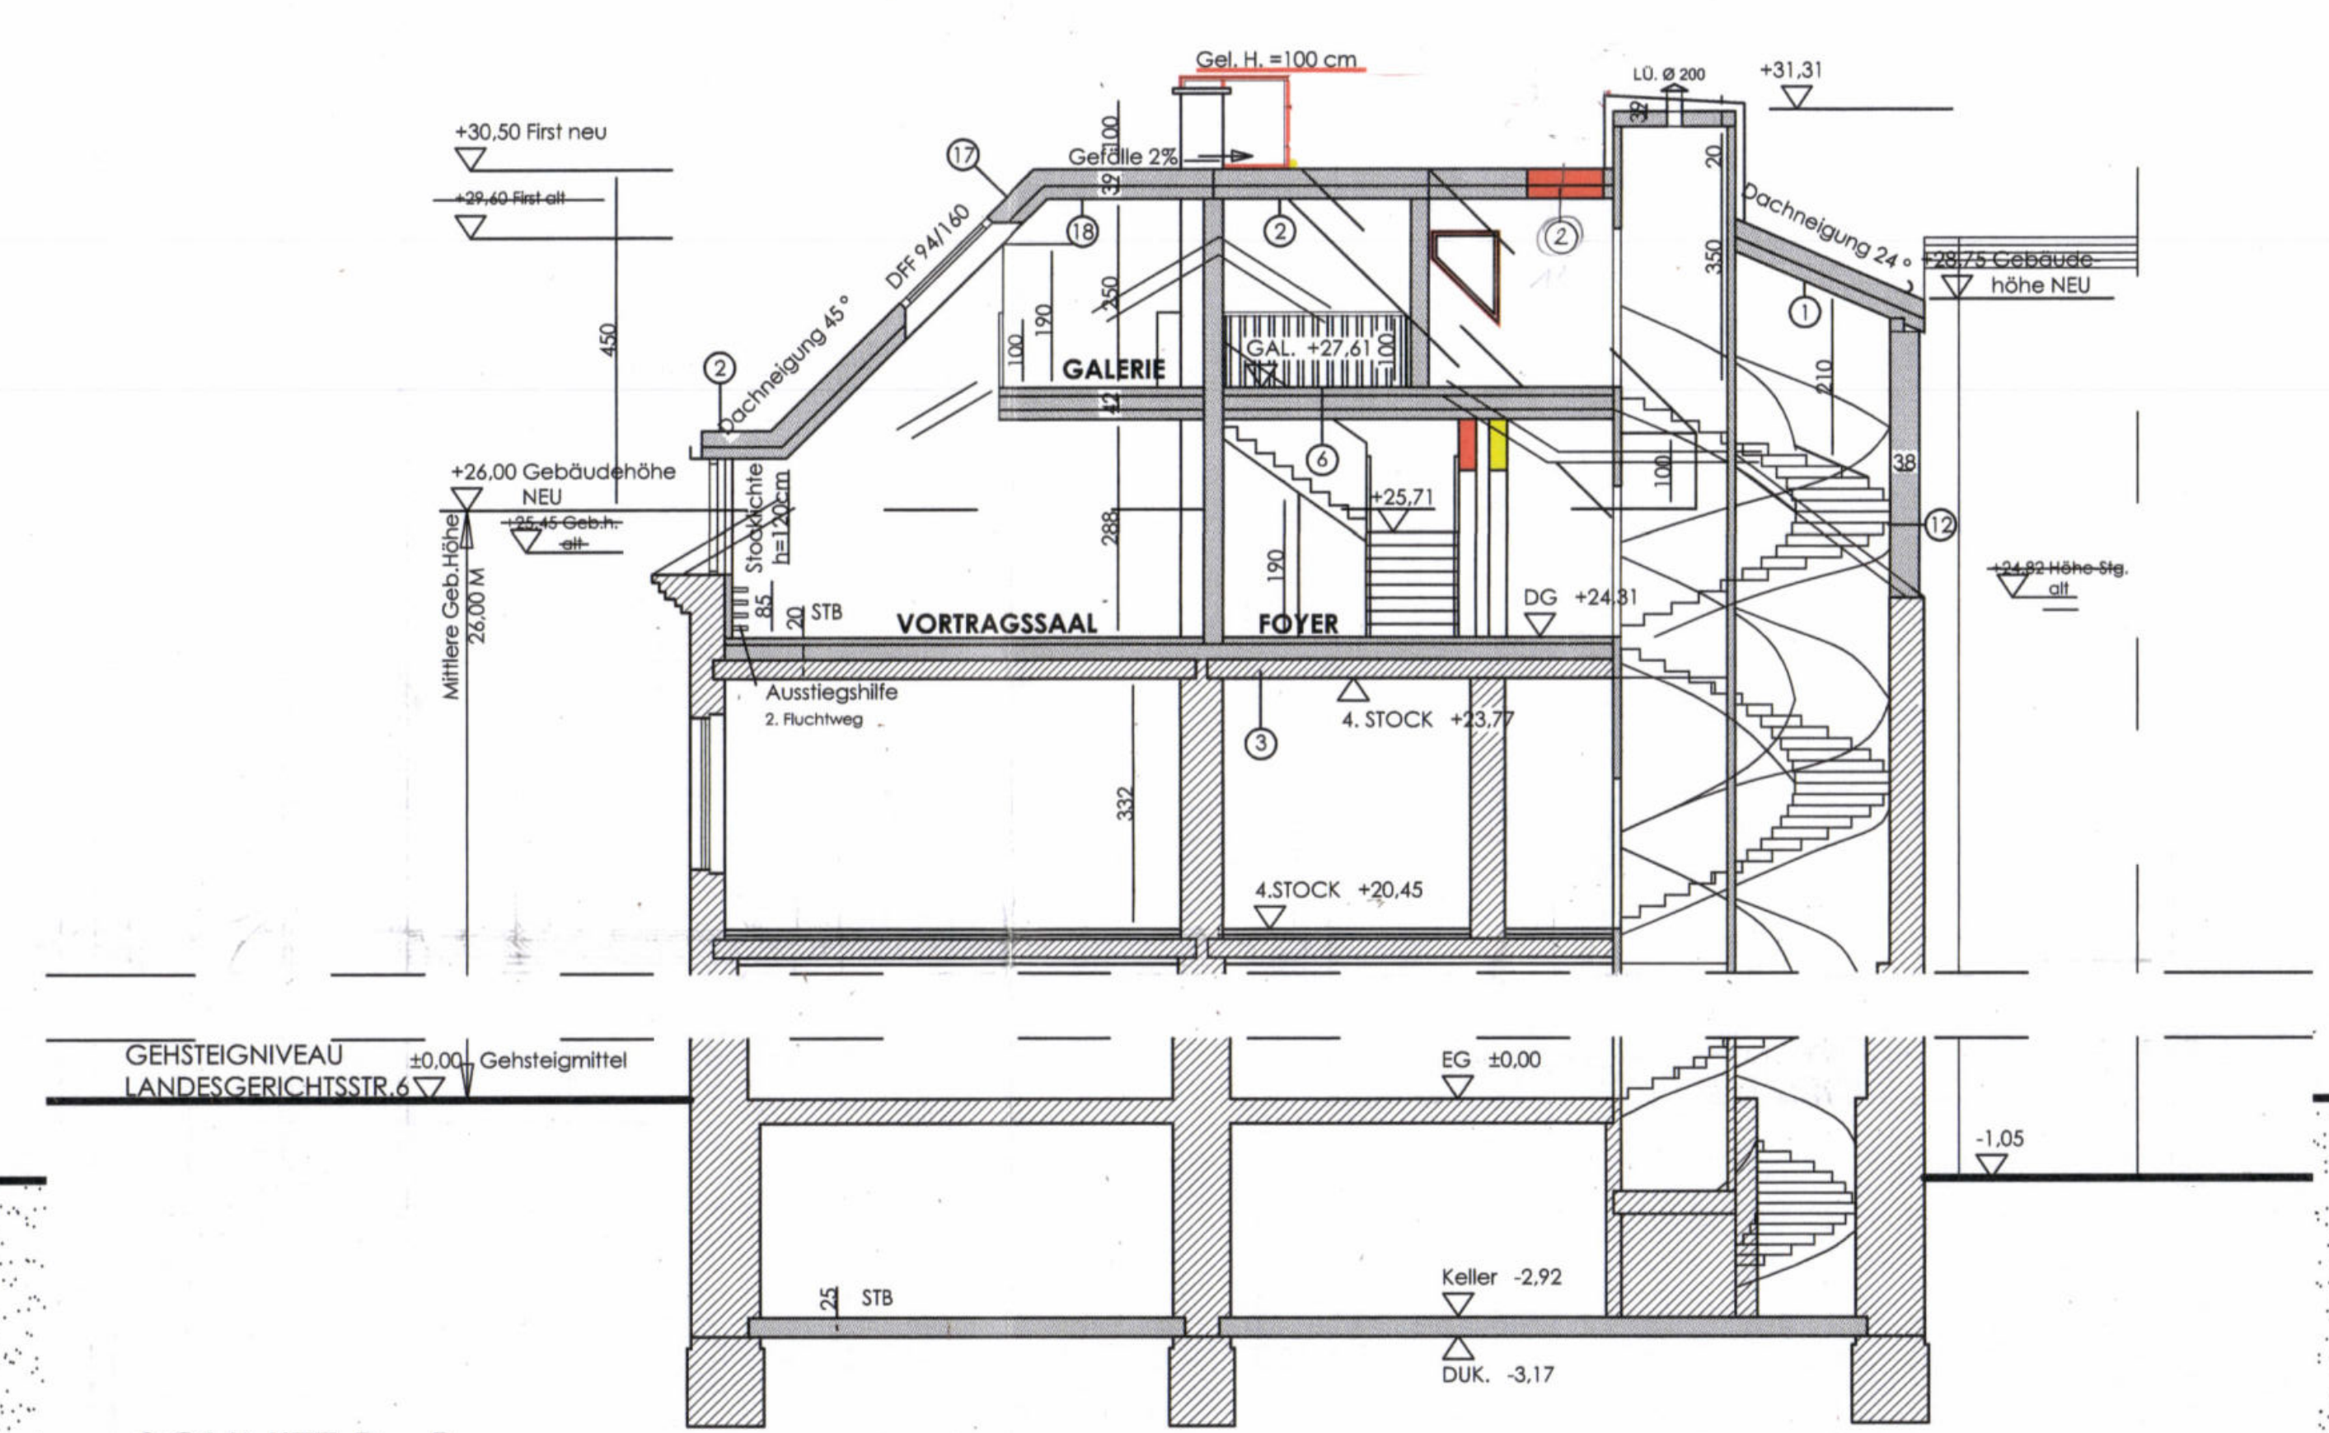
Gel. H. =100 cm
Gefälle 2%
Dachneigung 45°
Dachneigung 24°
GALERIE
GAL. +27,61
VORTRAGSSAAL
FOYER
Ausstiegshilfe 2. Fluchtweg
+30,50 First neu
+26,00 Gebäudehöhe NEU
Mittlere Geb.Höhe 26,00 M
GEHSTEIGNIVEAU LANDESGERICHTSSTR.6 ±0,00 Gehsteigmittel
DG +24,31
4. STOCK +23,77
4.STOCK +20,45
EG ±0,00
Keller -2,92
DUK. -3,17
+31,31
-1,05

SCHNITT B - B

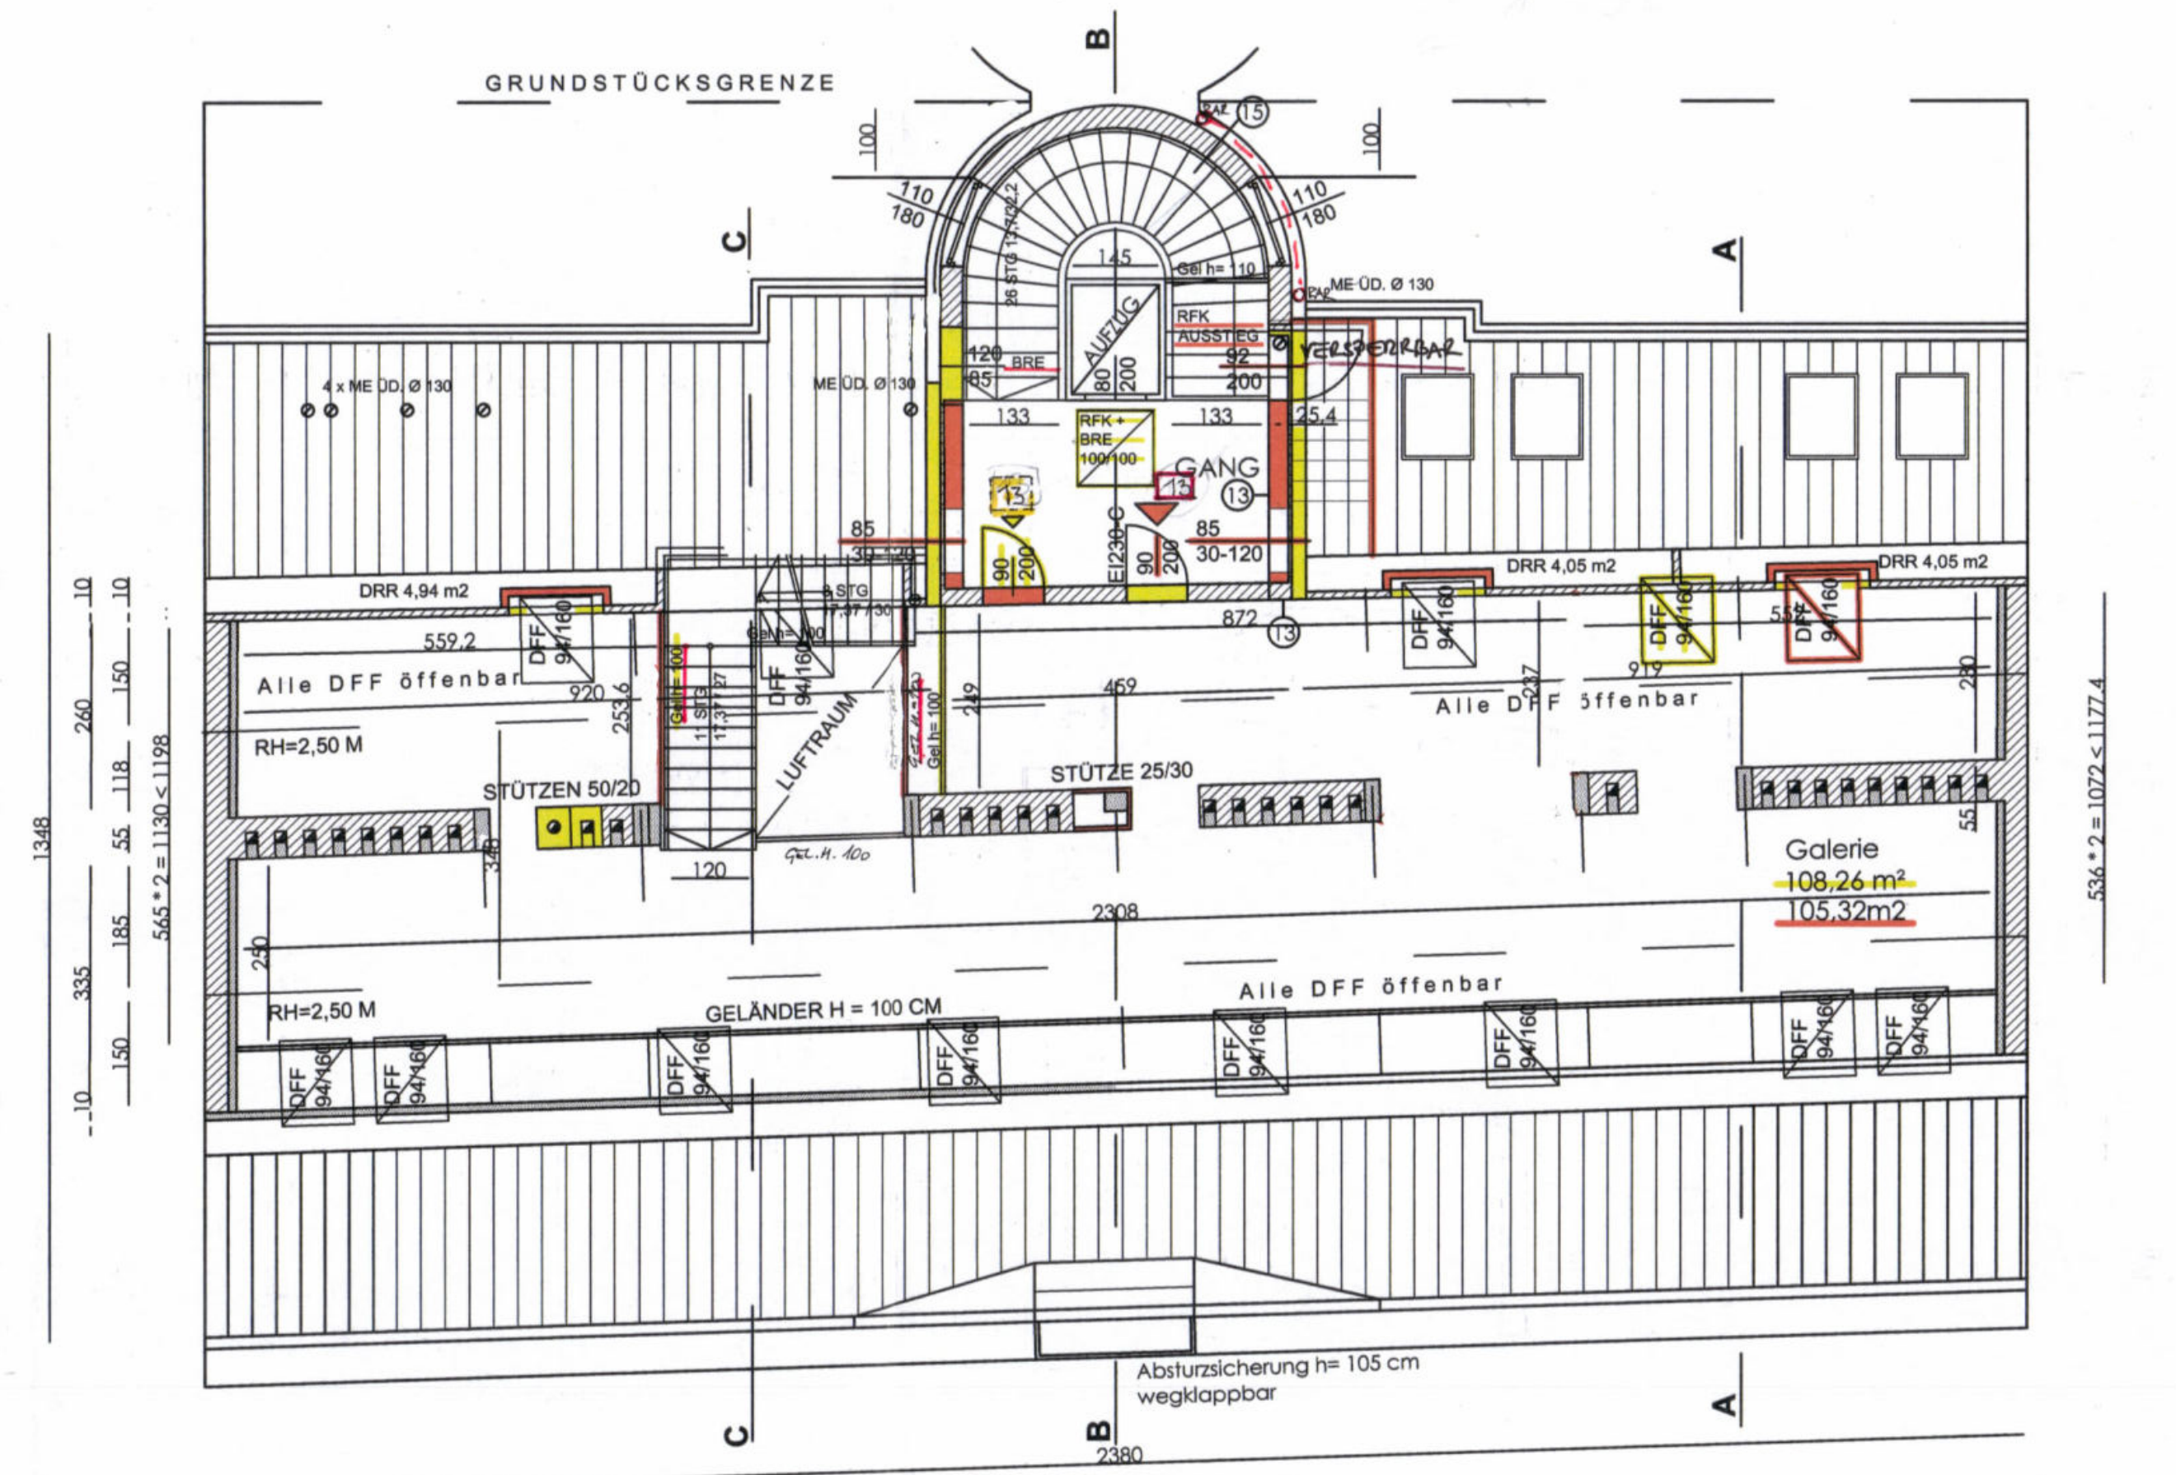
GRUNDSTÜCKSGRENZE
GANG
LUFTRAUM
Galerie 108,26 m2 105,32m2
Alle DFF öffenbar
GELÄNDER H = 100 CM
STÜTZE 25/30
STÜTZE 50/20
RH=2,50 M
Absturzsicherung h= 105 cm wegklappbar
Gaupenbreite=660 (<2380/3 = 793)
1348

GALERIE

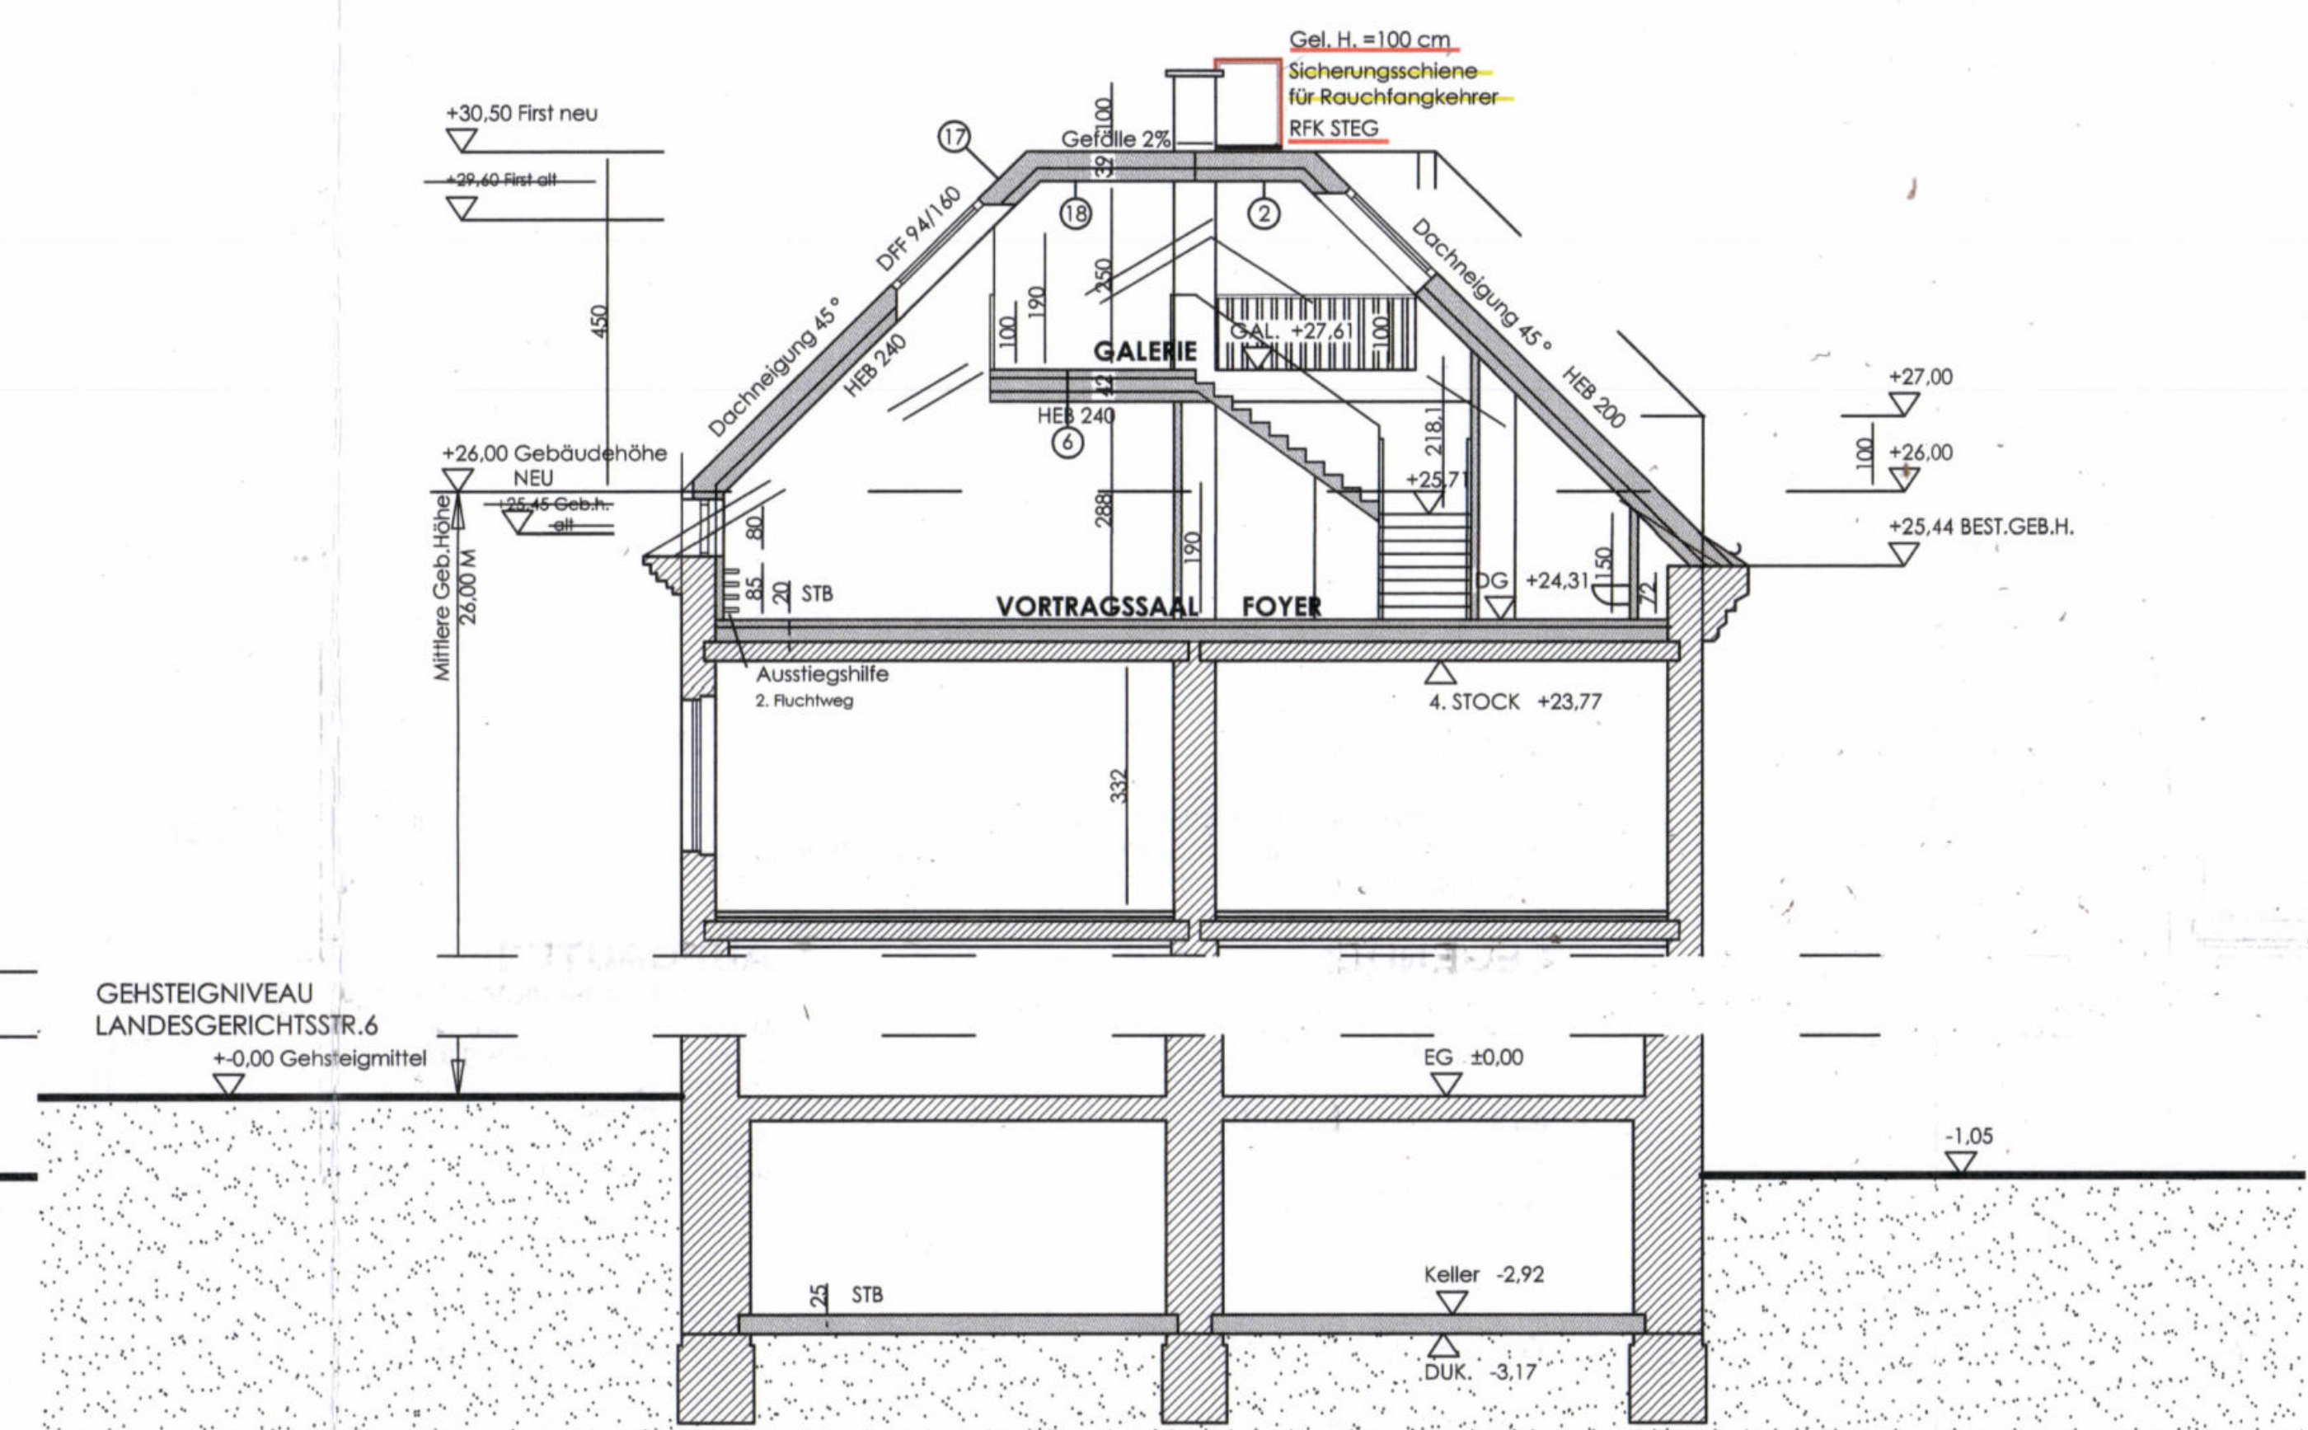
Gel. H. =100 cm
Sicherungsschiene für Rauchfangkehrer
RFK STEG
Gefälle 2%
Dachneigung 45°
HEB 200
HEB 240
DFF 94/160
GALERIE
GAL. +27,61
VORTRAGSSAAL
FOYER
Ausstiegshilfe 2. Fluchtweg
STB
+30,50 First neu
+26,00 Gebäudehöhe NEU
Mittlere Geb.Höhe 26,00 M
GEHSTEIGNIVEAU LANDESGERICHTSSTR.6 +0,00 Gehsteigmittel
+27,00
+26,00
+25,44 BEST.GEB.H.
DG +24,31
4. STOCK +23,77
EG ±0,00
Keller -2,92
DUK. -3,17
-1,05
450
332

SCHNITT C-C

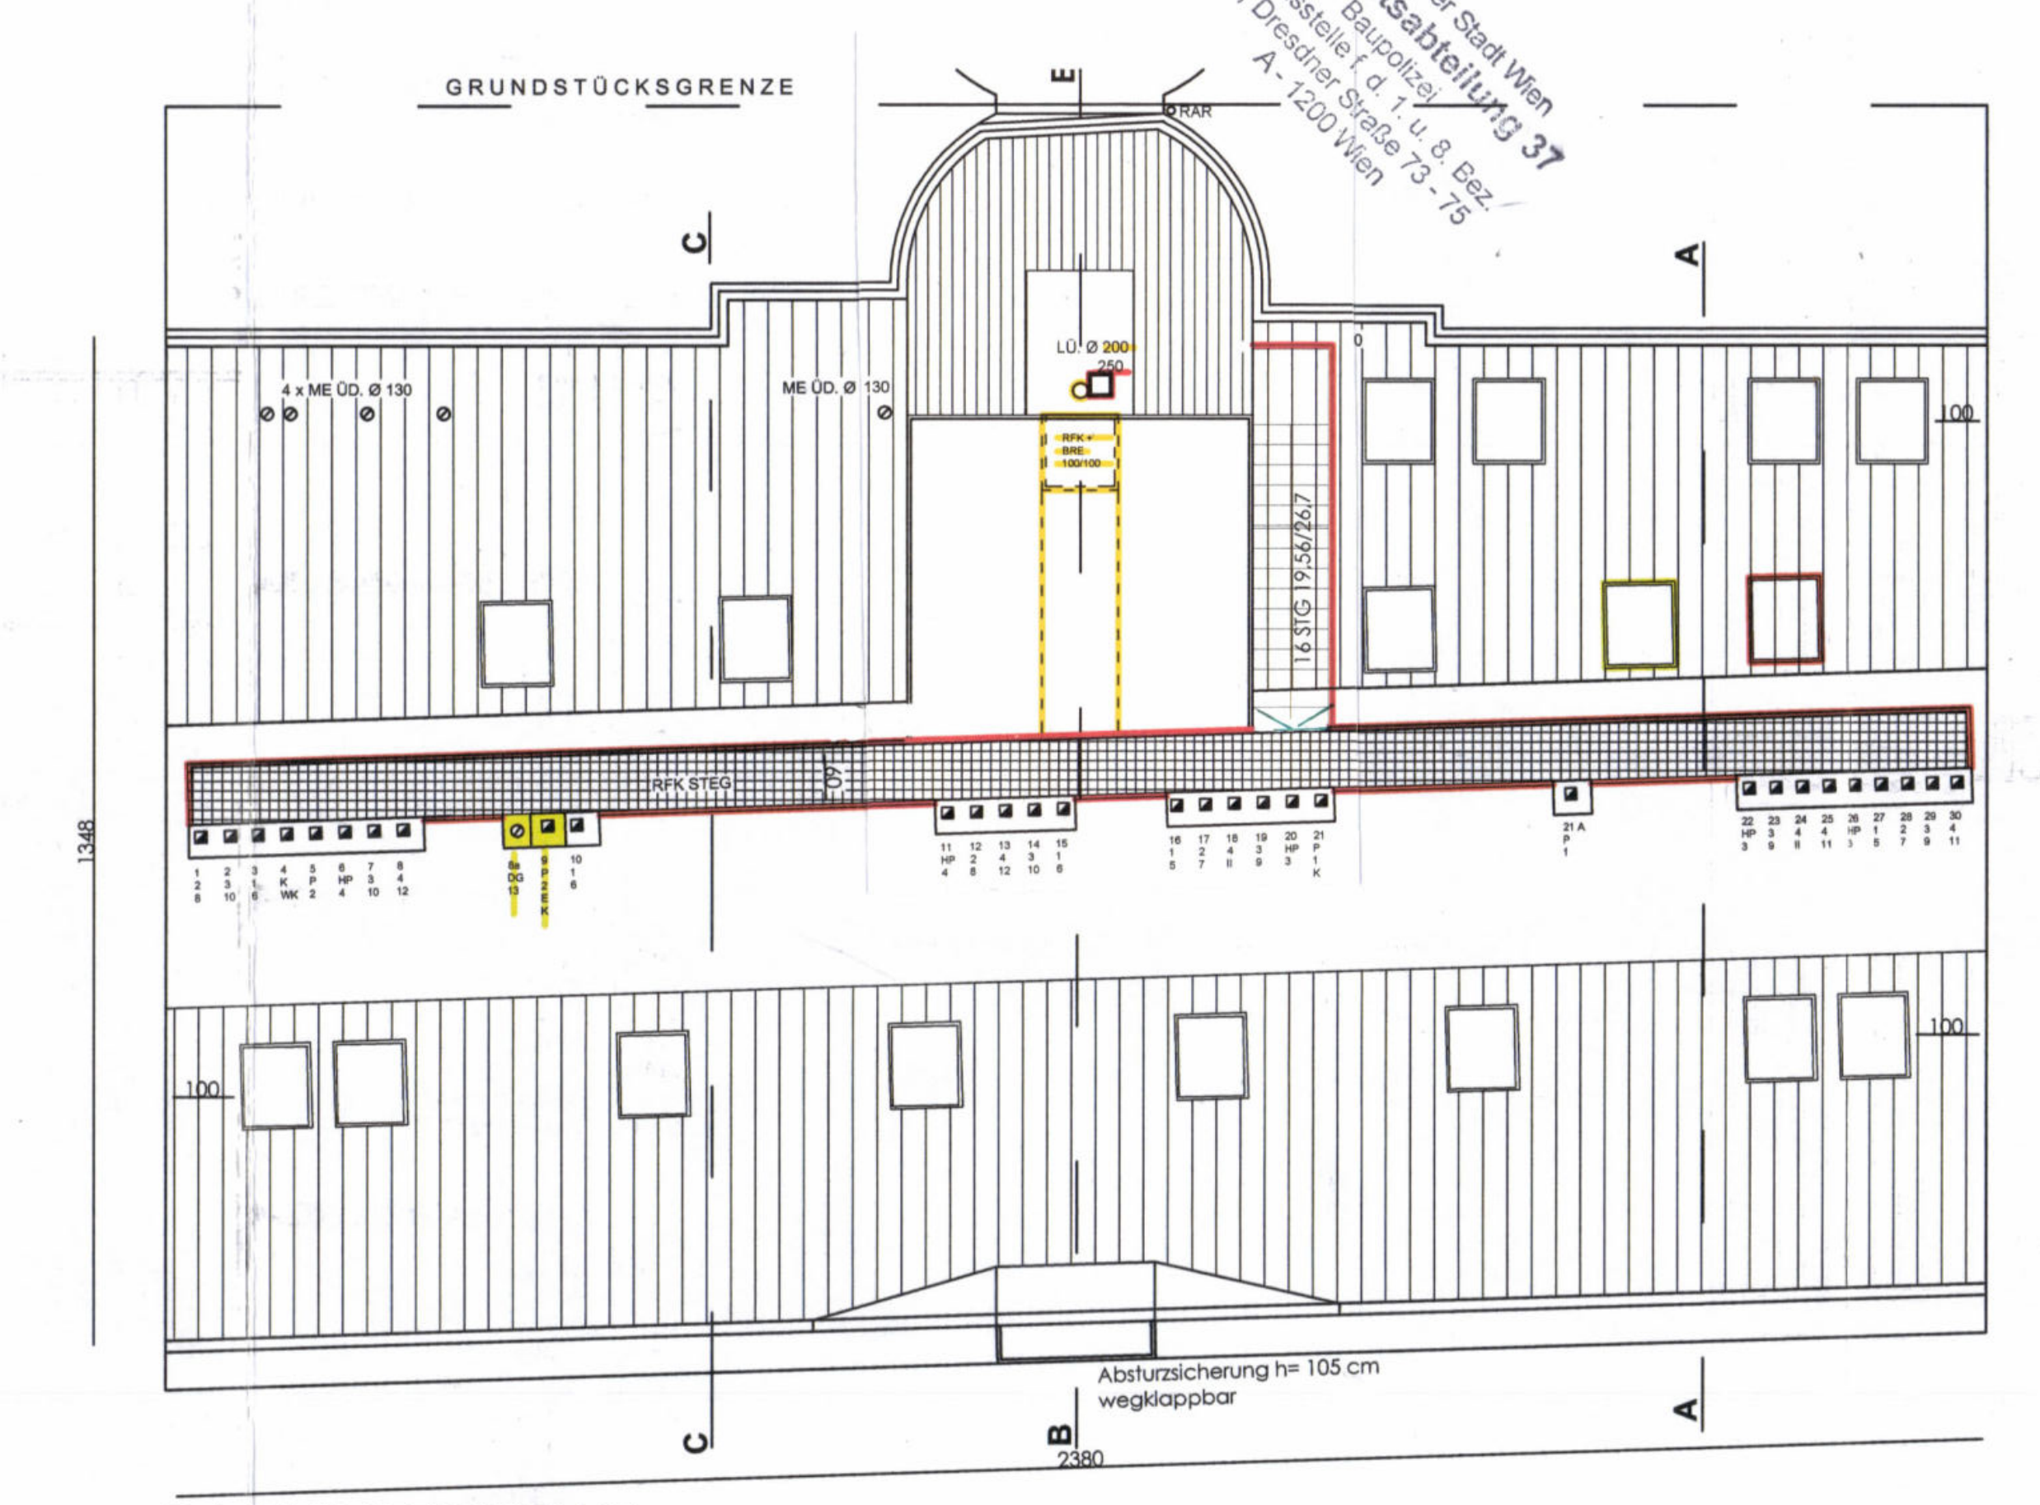
GRUNDSTÜCKSGRENZE
LÜ Ø 200
ME DD Ø 130
RFK STEG
Absturzsicherung h= 105 cm wegklappbar
1348

DACHDRAUFSICHT

Magistrat der Stadt Wien
Magistratsabteilung 37
Baupolizei
Bezirksstelle f. d. 1. u. 8. Bez.
20, Dresdner Straße 73 - 75
A - 1200 Wien

Personenaufzug:

Seilaufzug ohne gesonderten Triebwerksraum.
Stahlkonstruktion mit VGS. (Ersetzt alte Schachtumwehrung).
Kabine: 900 breit x 1050 tief.

LEGENDE:

- **BESTAND** ▆
- **NEUERSTELLUNG** 🟥
- **ABBRUCH** 🟨

Technische Erläuterungen:

- VZM = Vollziegelmauerwerk

- Alle neuen 10 cm dicken Zwischenwände sind in Gipskartonbauweise auszuführen

- Alle neuen Eingangstüren und Abstellraumtüren am Gang sind El$_2$'30 auszuführen

- Alle innenliegenden Stiegen sind elastisch gelagert. Geländerhöhe 1.0m, vertikale Sprossen, Sprossenabstand: 12 cm

- Die Beheizung der Räumlichkeiten erfolgt mit Gas-Kombi-Thermen

- Wände im Bereich von Kaminen werden bis zu einem Abstand von 25 cm aus unbrennbaren Materialien hergestellt.

- Alle WC Schalen sind abnehmbar

- Die Dachflächenfenster sind bündig mit der Dachhaut zu versetzen

- Die mechanischen Entlüftungen sind Pot Ø 130 aus verzinktem Stahlrohr F30 herzustellen.

- Neue WC - Anschlußleitungen Ø 100 Polokal, 2% Gefälle, in best. Abfallrohr Ø 150, an der Deckenunterkante abgehängt. Lüftung über Dach

- Feuermauern werden 15cm über Dach geführt.

- Tragende Teile des Dachstuhls werden F60 ummantelt.

Fenster
U = 1,9 W / m2 K
Rw = 40 dB
g = 0,67
z = 0,27 (Außenjalousien)

AUFBAUTEN:

1 DACHSCHRÄGE DACHAUSBAU

Dacheindeckung (keramische Dachziegel)		
Lattung 3/5 + Konterlattung 5/5		8,00 cm
Dachpappe		0,02 cm
Vollholzschalung		2,50 cm
Stahlrahmen HEB 200		20,00 cm
dazw. Sparren 10/14	14 cm	
dazw. TEL UNI	14 cm	
Staffel 6/10	6 cm	
dazw. TEL UNI	6 cm	
Dampfsperre		
Montagelattung 3/5		3,00 cm
GKF 1,5 2fach		3,00 cm
		36,50 cm

2 FLACHDACH

GFK 1,5 2 Fach		3,00 cm
Montagelattung		3,00cm
Dampfsperre		
20 cm - Stahlrahmen HEB 200		20,00 cm
dazw. Sparren 10/14	14 cm	
dazw. TEL UNI	14 cm	
Staffel 6/10	6 cm	
dazw. TEL UNI	6 cm	
Holzvollschalung		2,50 cm
Dachpappe		
Lattung 3/5 cm		3,00 cm
Dacheindeckung - Blechfalzdeckung		0,30 cm
		39,80 cm

3 DIPPELBAUMDECKE KLEBEPARKETT

Klebeparkett	0,60 cm
Zementestrich	5,00 cm
Dampfsperre	0,01 cm
TDP S 35/30	3,00 cm
Stahlbeton	20,00 cm
best. Dippelbaumdecke	22,00 cm
best. Putz u. Putzträger	3,00 cm
	54,00 CM

4 DIPPELBAUMDECKE FLIESEN

Fliesen	0,80 cm
Dünnbett	0,20 cm
Zementestrich	5,00 cm
Dampfsperre	0,01 cm
TDP S 35/30	3,00 cm
Stahlbeton	20,00 cm
best. Dippelbaumdecke	22,00 cm
best. Putz u. Putzträger	3,00 cm
	54,00 CM

5 DIPPELBAUMDECKE NASSRAUM

Fliesen	0,80 cm
Abdichtung	0,20 cm
Zementestrich	5,00 cm
Dampfsperre	0,01 cm
TDP S 35/30	3,00 cm
Stahlbeton	20,00 cm
best. Dippelbaumdecke	22,00 cm
best. Putz u. Putzträger	3,00 cm
	54,00 CM

6 TRAMDECKE KLEBEPARKETT GALERIE

Klebeparkett		0,80 cm
Zementestrich		5,00 cm
Dampfsperre		0,01 cm
TDP S 35/30		3,00 cm
Holzspanplatte V100		2,50 cm
Stahlrahmen HEB 240		24,00 cm
dazw. Träme	18 cm	
TEL UNI	14 cm	
dazw. Luft	4 cm	
Lattung auf Schwingbügel		3,50 cm
GKF 1,5 2fach		3,00 cm
		42,00 cm

9 FEUERMAUER VORSATZSCHALE

GKF 1,5 2fach	3,00 cm
Dampfsperre PAE-Folie	0,01 cm
Metallständer CW 75	
dazw. WDF 7,5	7,50 cm
Luft/Gespärre	15,00 cm
best. Vollziegelmauerwerk	15,00 cm
	40,50 cm

10 AUSSENWAND KNIESTOCKWAND 10 CM VORSATZSCHALE

GKF 1,25 2fach	2,50 cm
Dampfsperre PAE Folie	0,01 cm
Metallständer CW 75	7,50 cm
dazw. TEL WDF 6,0	
Luft 1,5 cm	
best. Ziegelwand	45,00 cm
best. Putz	2,50 cm
	55,00 cm

11 AUSSENWAND MONTAGEWAND

Dünnputz		0,50 cm
Heraklith EPV		5,00 cm
Spanplatte V100		1,00 cm
Holzsteher 5/10		10,00 cm
dazw. Luft	3 cm	
Mineralwolle	7 cm	
waagrechte Lattung		2,20 cm
PAE Folie		
Spanplatte V100		1,00 cm
GKF 1,25 2fach		2,50 cm
		22,00 cm

12 AUSSENWAND POROTHERM 38

Putz	2,50 cm
Porotherm	38,00 cm
Gipsputz	1,50 cm
	38,00 cm

13 TRENNWAND METALLSTÄNDERKONSTRUKTION

GKF 1,25 2fach	2,50 cm
Metallständer	7,50 cm
dazw. TEL WDF 8	
GKF 1,25 1fach	1,25 cm
Metallständer	7,50 cm
dazw. TEL WDF 8	
GKF 1,25 2fach	2,50 cm
	21,50 cm

14 ZWISCHENWAND

GKF 1,25 2 Fach	2,50 cm
Metallständer	
dazw. WDF	5,00 cm
GKF 1,25 2 Fach	2,50 cm
	10,00 cm

15 AUSSENWAND QUADRO 30

Putz	2,00 cm
Quadro 30	30,00 cm
Thermo Putz	2,00 cm
	30,00 cm

16 STB-DECKE, ehemaliger Stiegenaufgang

Fliesen	0,80 cm
Dünnbett	0,20 cm
Zementestrich	5,00 cm
Dampfsperre	0,01 cm
TDP S 35/30	3,00 cm
STB selbsttragend	20,00 cm
Abgehängte Decke / 4cm WDF	22,50 cm
GKF 1,25 2fach	2,50 cm
	54,00 cm

17 DACHSCHRÄGE DACHAUSBAU

Dacheindeckung (keramische Dachziegel)		
Lattung 3/5 + Konterlattung 5/5		8,00 cm
Dachpappe		0,02 cm
Vollholzschalung		2,50 cm
Stahlrahmen HEB 240		24,00 cm
dazw. Sparren 10/14	14 cm	
dazw. TEL UNI	14 cm	
Staffel 6/8	10 cm	
dazw. TEL UNI	10 cm	
Montagelattung 3/5		3,00 cm
GKF 1,5 2fach		3,00 cm
		40,50 cm

18 FLACHDACH

GFK 1,5 2 Fach		3,00 cm
Montagelattung		3,00cm
Dampfbremse		
20 cm - Stahlrahmen HEB 240		
TEL UNI 16+Luft 4 cm		24,00 cm
dazw. Sparren10/14	14 cm	
dazw. TEL UNI	14 cm	
Staffel 10/8	10 cm	
dazw. TEL UNI	10 cm	
Holzvollschalung		2,50 cm
Dachpappe		
Lattung 3/5 cm		3,00 cm
Dacheindeckung - Blechfalzdeckung		0,30 cm
		35,80 cm

PARIE	A	B	C	1	2	3	4

7,20 24/3

AUSWECHSLUNGSPLAN
ÜBER DEN DACHGESCHOSSAUSBAU
DES HAUSES

LANDESGERICHTSSTRASSE 6
1010 WIEN

EZ	GST	KATASTRALGEM.
894	1526/2	Innere Stadt

BAUWERBER

Zentralverband der Hausbesitzer von Wien
und den Ländern Österreichs
Landesgerichtsstraße 6
1010 Wien

IMMOBILIENVERW. / MAKLER
Dr. FRIEDRICH NOSZEK GmbH
1030 Wien, Unt. Viaduktg. 11/6

GRUNDEIGENTÜMER

Zentralverband der Hausbesitzer von Wien
und den Ländern Österreichs
Landesgerichtsstraße 6
1010 Wien

IMMOBILIENVERW. / MAKLER
Dr. FRIEDRICH NOSZEK GmbH
1030 Wien, Unt. Viaduktg. 11/6

PLANVERFASSER | **BAUFÜHRER**

Architekt Dipl.Ing. ADOLF WOHANKA
MILLERGASSE 21, 1060 WIEN
Tel.: 597 13 68 Fax: 596 24 30

ARCH. DIPL. ING. ADOLF WOHANKA

Jägerbau
JÄGER GESELLSCHAFT m.b.H.
LEHRBACHGASSE 4
1120 WIEN, Tel. 0222/813 40 72-0
BAULEITUNG

DATUM	PLANNR.	BAUTEIL	Maßstab
November 2006			M = 1:100

BEHÖRDE

Magistratsabteilung 19
Zahl B1/6063/07
Beilagen
EING.: 13. JUNI 2007
AUSGANG 18. JUNI 2007

Magistrat der Stadt Wien
Magistratsabteilung 37
Baupolizei
MA 37/1-22695-6/2004
Hierauf bezieht sich der Bescheid
Für den Abteilungsleiter:
Dipl.-Ing. Fischer
Wien, 21.6.2007
Fischer

BauBehörde
StaDt Wien