




UMGEBUNG ERDGESCHOSS
(UNTERSTE HALTESTELLE + HAUPTHALT)

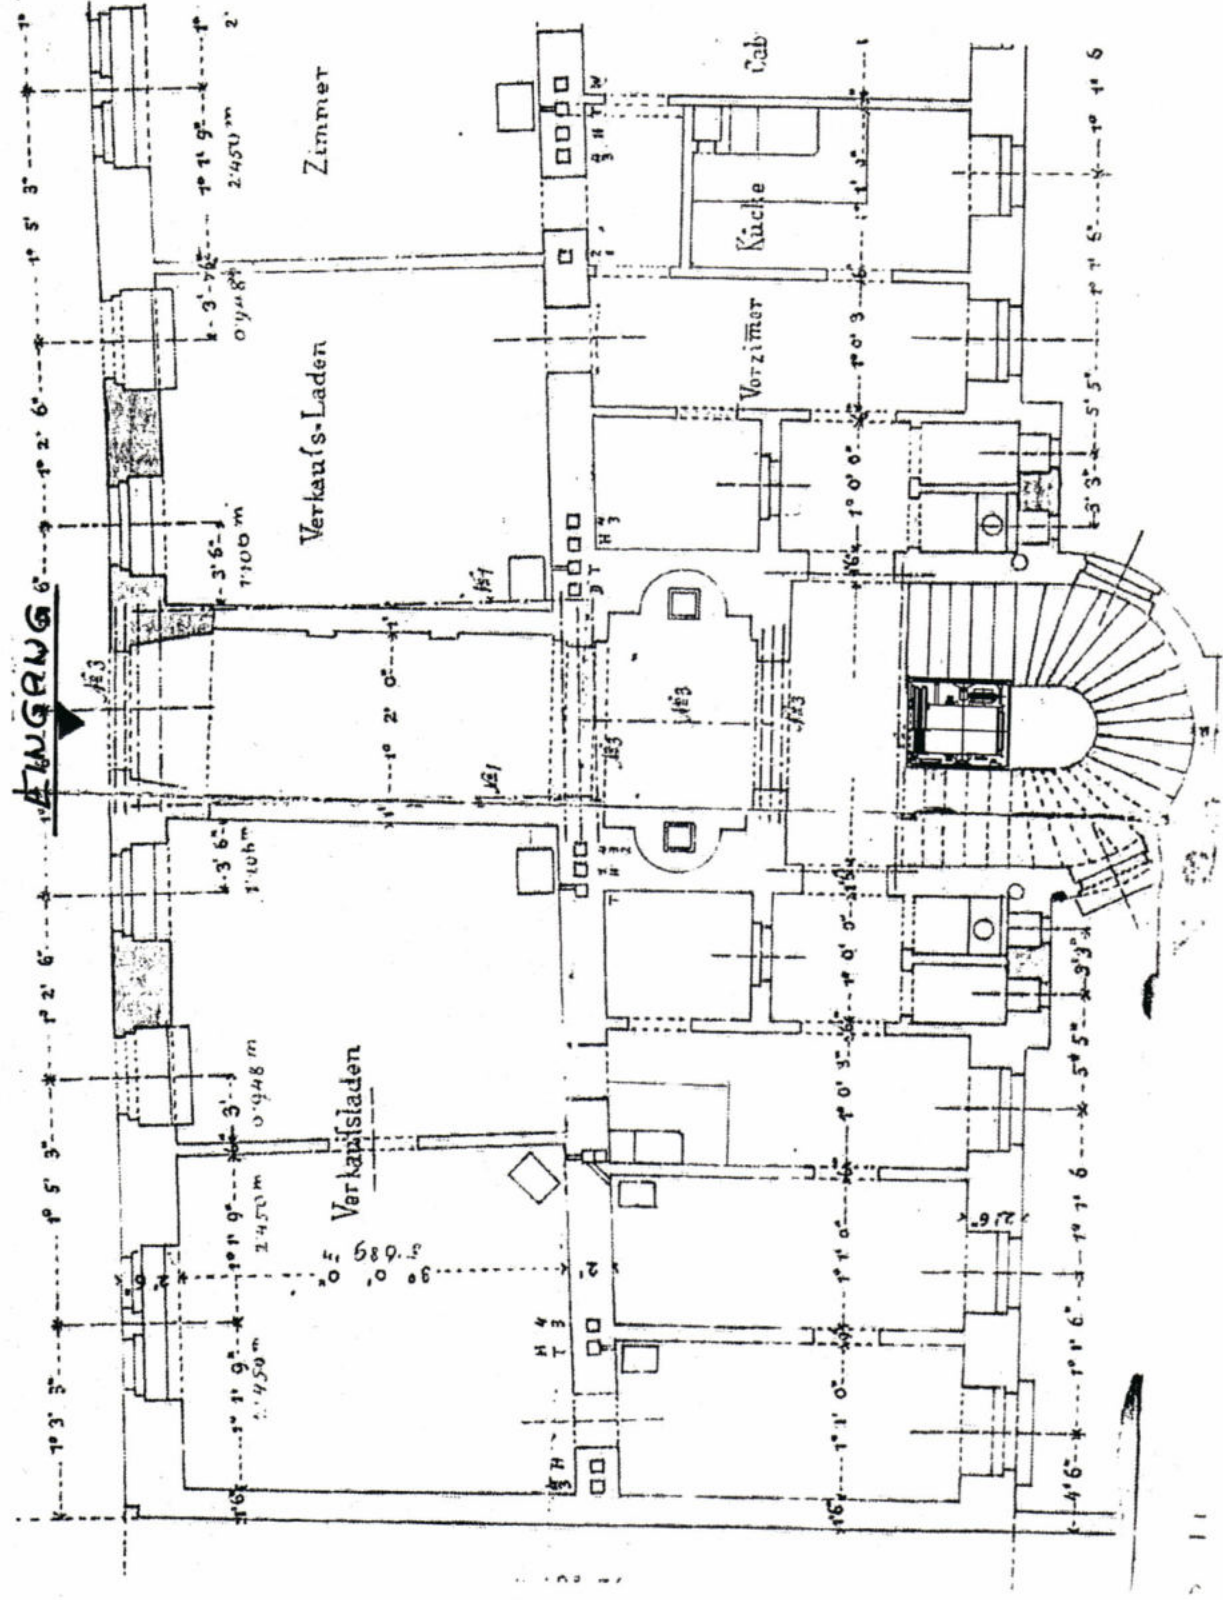


UMGEBUNG HALT „HP“ BIS HALT „4“
(REGELGESCHOSS)

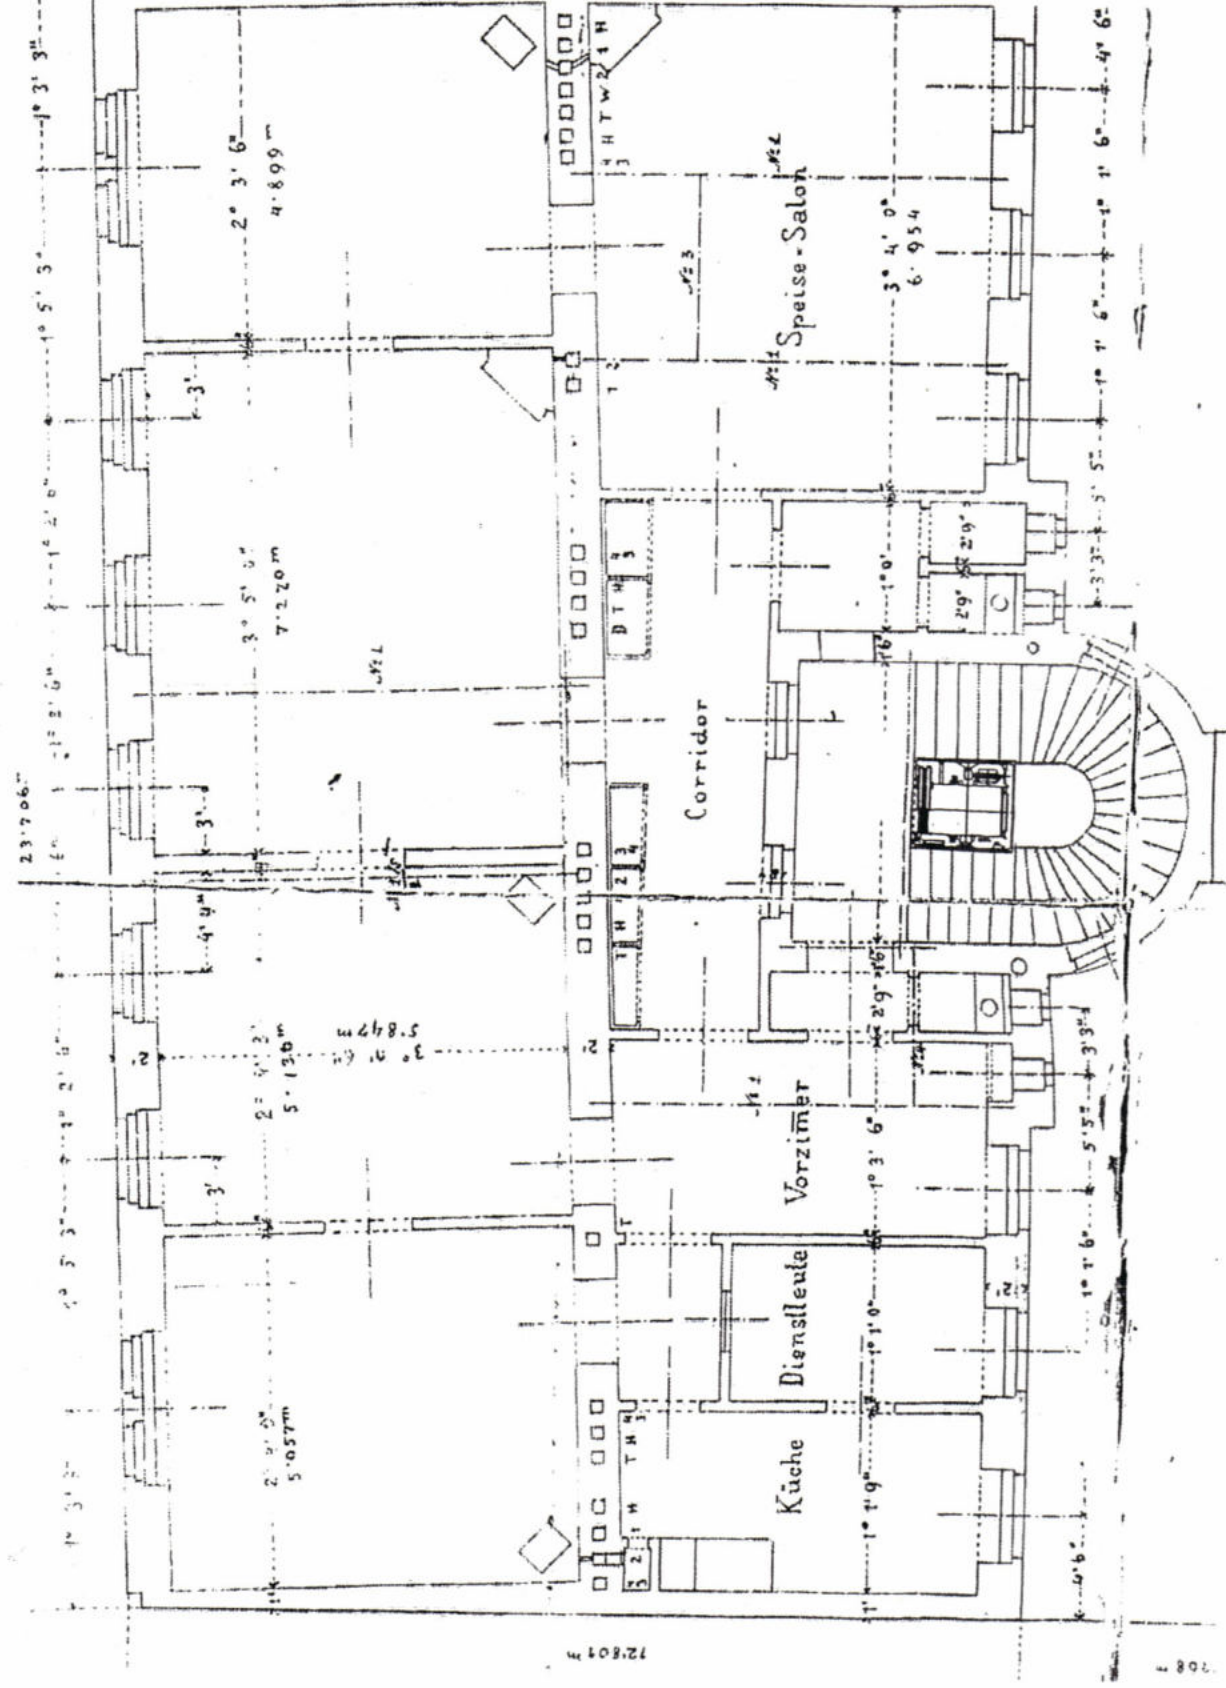

UMGEBUNG HALT „2D“
(OBERSTE HALTESTELLE + NOTBEFREIUNGSPANEEL)

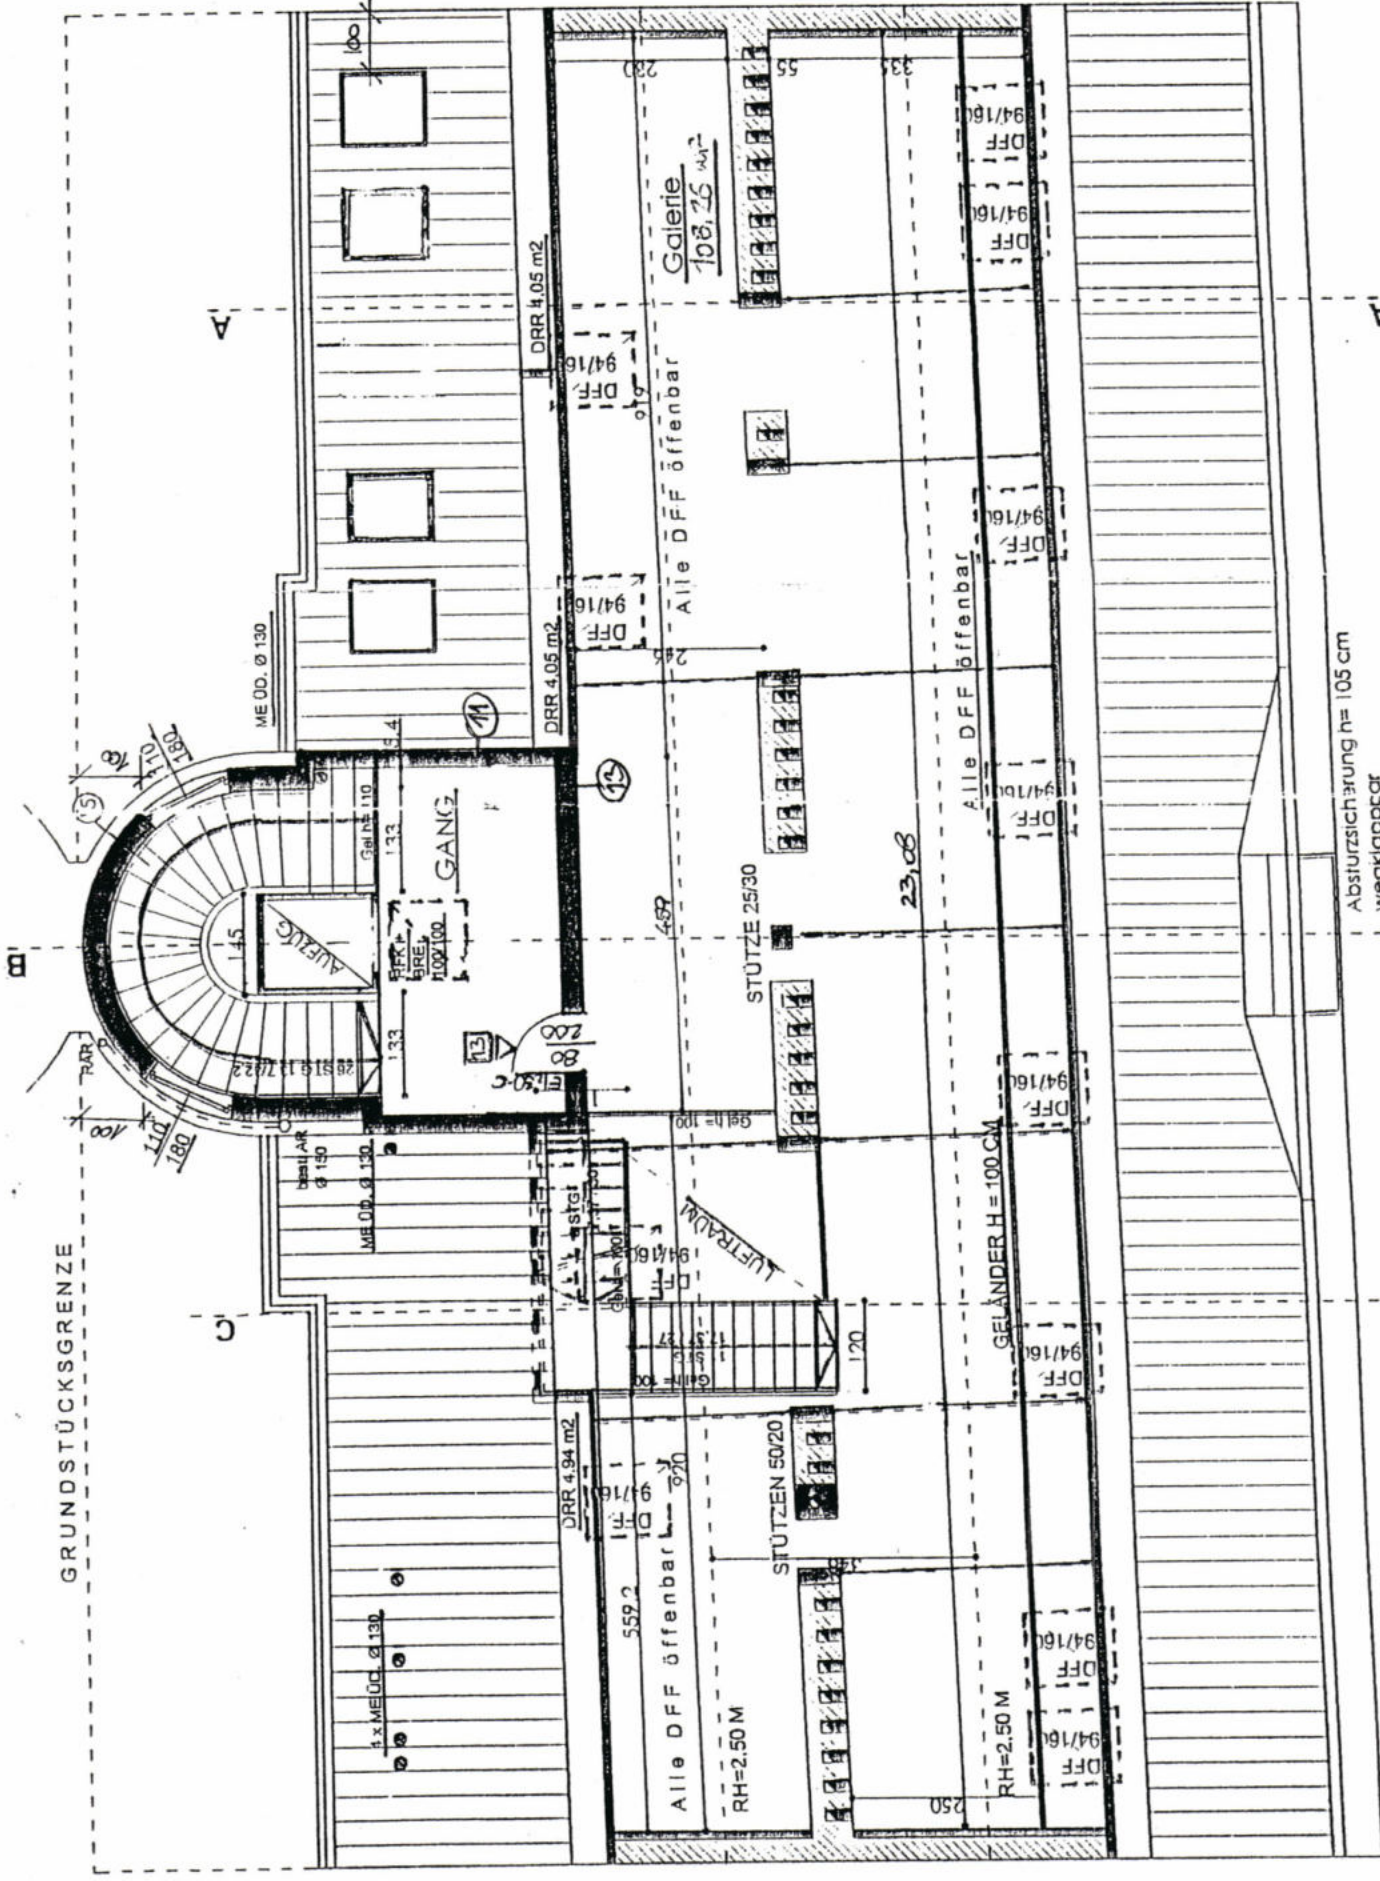

UMGEBUNG HALT „1D“

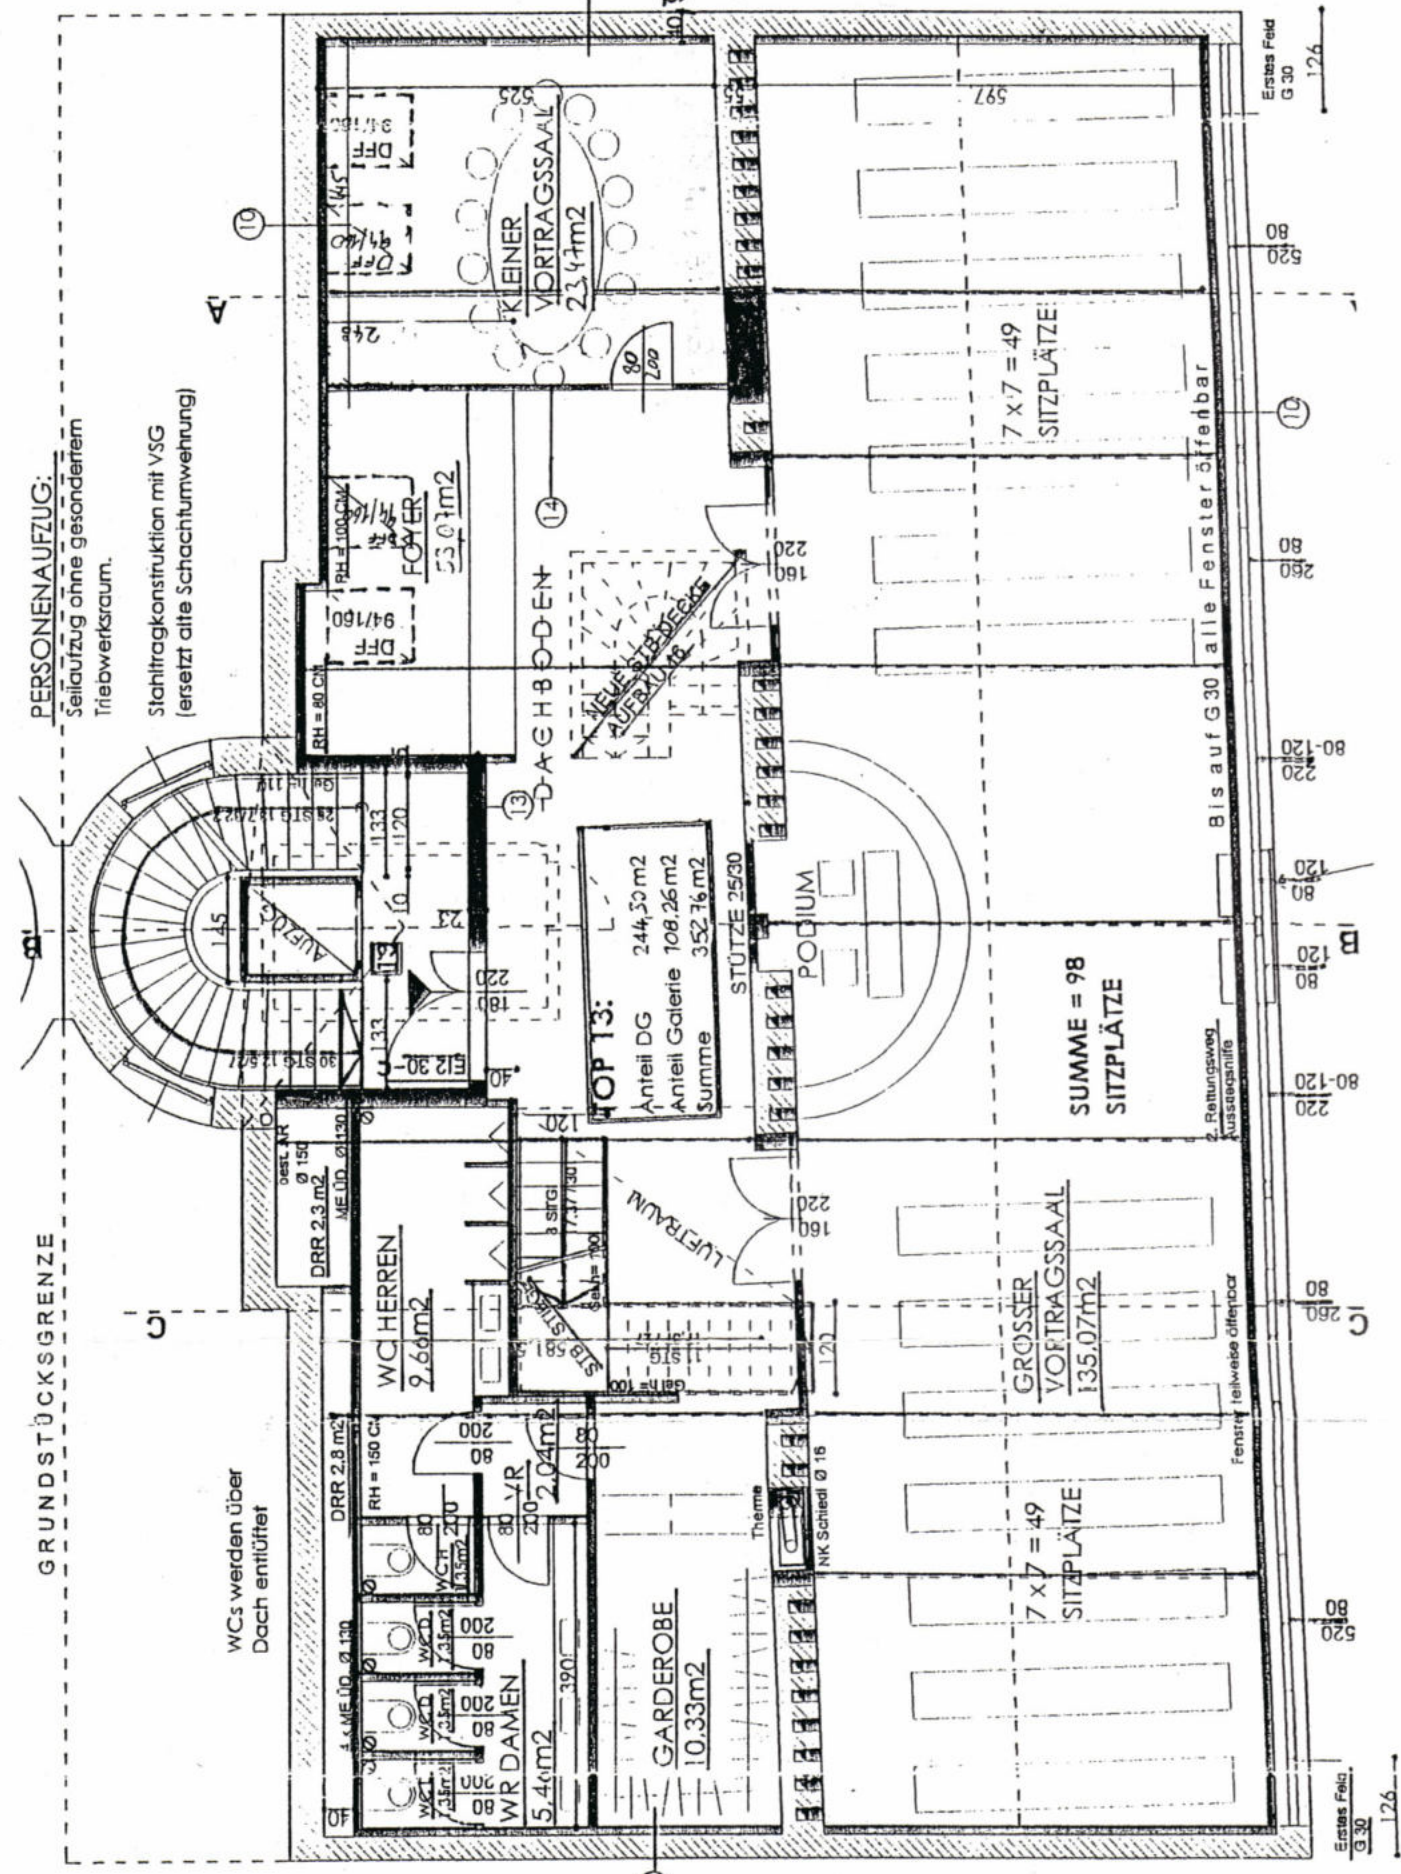

Magistrat der Stadt Wien
Magistratsabteilung 37

Baupolizei

Hierauf bezieht sich der Bescheid

MA 37- A/ 1 60 5 9 - 0 1 / 2006

Wien

12. MAI 2006

Für den Abteilungsleiter:

Mag. Ing. Dr. Eder

Landesbauverwaltung

VERGEBT MIT 720 EUR

Gemäß § 14 i.V. mit § 3

Abs. 2 Gebührengesetz 1997



EINREICHPLAN

DER BAUKRÄFTIGER: IMMOBILIENVERW./MAKLER DR. FRIEDRICH MÖSELER 1030 Wien, Untere Donaulände 118	DER PLANVERFASSTER UND BEFUGTE AUFZUGSBEREITER: KONE Aktiengesellschaft 1220 Wien, Untere Donaulände 118
DER HAUS- UND GRUNDEIGENTUMER: IMMOBILIENVERW./MAKLER DR. FRIEDRICH MÖSELER 1030 Wien, Untere Donaulände 118	DER BAUFÜHRER FÜR DIE BAUWEITERARBEITEN: Jäger Gesellschaft m.b.H. Kremsier Landstrasse 24 3100 St. Pölten
EINREICHUNG UND GENEHMIGUNG	
INDEX	ART DER ANWENDUNG
BETRIEBSART:	BÜROHAUS LANDESGERICHTSSTRASSE 6 1010 WIEN
AUFZUGSEIGENTUMER:	ZENTRALVERBAND DER HAUSEIGENTUMER HILFENBERG LANDESGERICHTSSTRASSE 6 1010 WIEN
PLANTHALT	LAGEPLAN, UMGEBUNGEN IN DEN GESCHOSSEN
FPW05/10-19	
DATUM	NAME
20.02.2006	GP
TESTST.	ERZEUGERNUMMER
29357	29357
CEPR.	PLANNUMMER (CAD)
17.03.06	29357.LAGE

