

Beschau gemäß §§125 Abs.2 und
127 Abs.3 der Bauordnung für Wien

BEFUND

STAHLKONSTR. beschau GZZT 2004/33

für die Baubewilligung vom

Zi. MA

genehmigte Bauführung

Datum

27.09.2005

Baustellenadresse

Anwesende: Bevollmächtigter des ZT Büros

D. I. T. JANICKI

Bauführer

vertreten durch:

Gegenstand der Beschau (Bauteile usw.):

STAHLKONSTRUKTION IN DB

Vorliegende Konstruktionspläne:

TL NR 1, 2, 3

Abweichungen vom bewilligten Bauplan (Einreichplan):

Abweichungen in der technischen Ausführung:

GUTACHTLICHE FESTSTELLUNG

Technische Ausführung plan- und fachgemäß: ja ☒

nein ☐

Mängel:

Weiterarbeit wird – ~~nicht~~ – unter folgenden Bedingungen – gestattet

Unterschrift und Stempel
des Bauführers



Unterschrift und Rundsiegel
des Ziviltechnikers



Mit dieser Unterschrift bestätigt der Bauführer auch, dass die dem Befund zugrunde liegenden Baupläne identisch sind mit denen, die bei der Baubehörde aufliegen.

Beschau gemäß §§125 Abs.2 und
127 Abs.3 der Bauordnung für Wien

BEFUND

EISEN beschau GZZT 2004/33
für die Baubewilligung vom

Zi.MA genehmigte Bauführung

Datum 27.05.2005

Baustellenadresse

Anwesende: Bevollmächtigter des ZT Büros D. L. T. JANICKI

Bauführer

vertreten durch:

Gegenstand der Beschau (Bauteile usw.): DECKE Ü. BESTAND. (406)

Vorliegende Konstruktionspläne: BEWEHRUNGSPL. B - 001/0

Abweichungen vom bewilligten Bauplan (Einreichplan): /

Abweichungen in der technischen Ausführung: /

GUTACHTLICHE FESTSTELLUNG

Technische Ausführung plan- und fachgemäß: ja ☒ nein ☐

Mängel: /

Weiterarbeit wird – ~~nicht~~ – unter folgenden Bedingungen – gestattet:

Unterschrift und Stempel
des Bauführers


JÄGER & CO. GMBH
LIEBIGFISCHGASSE 4
1120 WIEN, Tel. 0222/813 46 72-0
BAULEITUNG

Unterschrift und Rundsiegel
des Ziviltechnikers



Mit dieser Unterschrift bestätigt der Bauführer auch, dass die dem Befund zugrunde liegenden Baupläne identisch sind mit denen, die bei der Baubehörde aufliegen.

Beschau gemäß §§125 Abs.2 und
127 Abs.3 der Bauordnung für Wien

BEFUND

EISEN beschau GZZT 2004/33
für die Baubewilligung vom
Zi.MA genehmigte Bauführung
Datum 16.09.2005
Baustellenadresse
Anwesende: Bevollmächtigter des ZT Büros D. L. T. JANICKI
Bauführer
vertreten durch:

Gegenstand der Beschau (Bauteile usw.): BODENPLATTE
Vorliegende Konstruktionspläne: B-002/A
Abweichungen vom bewilligten Bauplan (Einreichplan):
Abweichungen in der technischen Ausführung:

GUTACHTLICHE FESTSTELLUNG

Technische Ausführung plan- und fachgemäß: ja ☒ nein ☐
Mängel: /

Weiterarbeit wird – ~~nicht~~ – unter folgenden Bedingungen – gestattet:

Unterschrift und Stempel
des Bauführers



Unterschrift und Rundstempel
des Ziviltechnikers



Mit dieser Unterschrift bestätigt der Bauführer auch, dass die dem Befund zugrunde liegenden Baupläne identisch sind mit denen, die bei der Baubehörde aufliegen.

Beschau gemäß §§125 Abs.2 und
127 Abs.3 der Bauordnung für Wien

B E F U N D

GEBÄUDE beschau GZZT 2004/33
für die Baubewilligung vom 5.10.2004
Zi.MA 37/1 - LANDESGERICHTSSTR. 6/22695-1/2004 genehmigte Bauführung
Datum 23.05.2006
Baustellenadresse LANDESGERICHTSSTR. 6 ; 1010 WIEN
Anwesende: Bevollmächtigter des ZT Büros D. J. T. JANICKI
Bauführer
vertreten durch:

Gegenstand der Beschau (Bauteile usw.): GEBÄUDE BESCHAU - VERSCHLIEßUNGEN
..... ALLE VERSCHLIEßUNGEN ERHALTEN SIND
Vorliegende Konstruktionspläne:
.....
Abweichungen vom bewilligten Bauplan (Einreichplan):
.....
Abweichungen in der technischen Ausführung:
.....

GUTACHTLICHE FESTSTELLUNG

Technische Ausführung plan- und fachgemäß: ja ☒ nein ☐
Mängel: /

Weiterarbeit wird – nicht – unter folgenden Bedingungen – gestattet:
.....

Unterschrift und Stempel
des Bauführers



Unterschrift und Rundsiegel
des Ziviltechnikers



Mit dieser Unterschrift bestätigt der Bauführer auch, dass die dem Befund zugrunde liegenden Baupläne ident sind mit denen, die bei der Baubehörde aufliegen.

Beschau gemäß §§125 Abs.2 und
127 Abs.3 der Bauordnung für Wien

BEFUND

ROHBAU beschau GZZT 2004/33
für die Baubewilligung vom
Zi.MA genehmigte Bauführung.
Datum 23.05.06
Baustellenadresse LANDESGERICHTSSTR 6 / 1010 WIEN
Anwesende: Bevollmächtigter des ZT Büros D.I.T. JANICKI
Bauführer
vertreten durch:

Gegenstand der Beschau (Bauteile usw.):
Vorliegende Konstruktionspläne: EINREICHPLAN
Abweichungen vom bewilligten Bauplan (Einreichplan):
Abweichungen in der technischen Ausführung:

GUTACHTLICHE FESTSTELLUNG

Technische Ausführung plan- und fachgemäß: ja ☒ nein ☐
Mängel:
Weiterarbeit wird – nicht – unter folgenden Bedingungen – gestattet:

Unterschrift und Stempel
des Bauführers


JÄGER & SEELENSCH GMBH
LEHRBACHGASSE 4
1120 WIEN, Tel. 0222/813 46 72-0
BAULEITUNG

Unterschrift und Rundsiegel
des Ziviltechnikers



Mit dieser Unterschrift bestätigt der Bauführer auch, dass die dem Befund zugrunde liegenden Baupläne ident sind mit denen, die bei der Baubehörde aufliegen.

BEFUND und GUTACHTEN

über die vorhandenen Rauch- und Abgasfänge gemäß Bauordnung für Wien § 128, Abs 2, Z4 -
dient als Beilage zur Fertigstellungsanzeige für die MA 37;

Architekturbüro
Arch. DI Adolf Wohanka
z.H. Herrn Arch. Heiss
Millergasse 21
1060 Wien
per FAX: 5962430

Befund-Nr.: 5/2006
Datum: 13.02.2007
Zeichen:
DVR: 1071025

für die im Hause 1010, Landesgerichtsstraße 6 befindlichen

Rauch- und Abgasfänge

sowie Luft- und Systemfänge

Bauwerber:

Bauführer:

Befundaufnahme

	Anzahl:		Art - System
a)	30	Enge Rauch- und Abgasfänge	gemauert
b)	0	Mittl. Rauch- und Abgasfänge	XXXXX
c)	0	Abluftfänge	XXXXX
d)	0	Abgassammler	XXXXX
e)	0	Rauchsammler	XXXXX
f)	0	Enge Rauch- und Abgasfänge	XXXXX

Gutachten

In Bezug auf die bestehenden Vorschriften ergab die durchgeführte Untersuchung oben angeführter Fänge:
Die Fänge unter Punkt a) - siehe Anmerkungen - können lt. ihrer bauordnungsgemäßen Bestimmung
verwendet werden.

Anton ESTERAK
Rauchfangkehrerbetrieb
Dornbacherstraße 29
1170 Wien
Tel. 485 36 94, Fax 587 02 66

25
2

BESTANDSPLAN

ÜBER DEN DACHGESCHOSSAUSBAU DES HAUSES

LANDESGERICHTSSTRASSE 6 1010 WIEN

EZ	GST	KATASTRALGEM.
894	1526/2	Innere Stadt

BAUWERBER

Zentralverband der Hausbesitzer von Wien
und den Ländern Österreichs
Landesgerichtsstraße 6
1010 Wien

GRUNDEIGENTÜMER

Zentralverband der Hausbesitzer von Wien
und den Ländern Österreichs
Landesgerichtsstraße 6
1010 Wien

PLANVERFASSTER

Architekt Dipl.Ing. ADOLF WOHANKA
MILLERGASSE 21, 1060 WIEN
Tel.: 597 13 68 Fax: 596 24 30



BAUFÜHRER



DATUM

PLANNR.

BAUTEIL

Maßstab

Mai 2007

M = 1:100

BEHÖRDE

Magistrat der Stadt Wien
Magistratsabteilung 37
Baupolizei

MA 37/1-22695-5/2004

Dieser Plan lag der Fertigstellungsanzeige zu Grunde.


Der grau dargestellte Bestand bildet keinen Konsens!

Für den Abteilungsleiter:
OWKM Kopitar

Wien, 4.12.2007

[Handwritten signature]



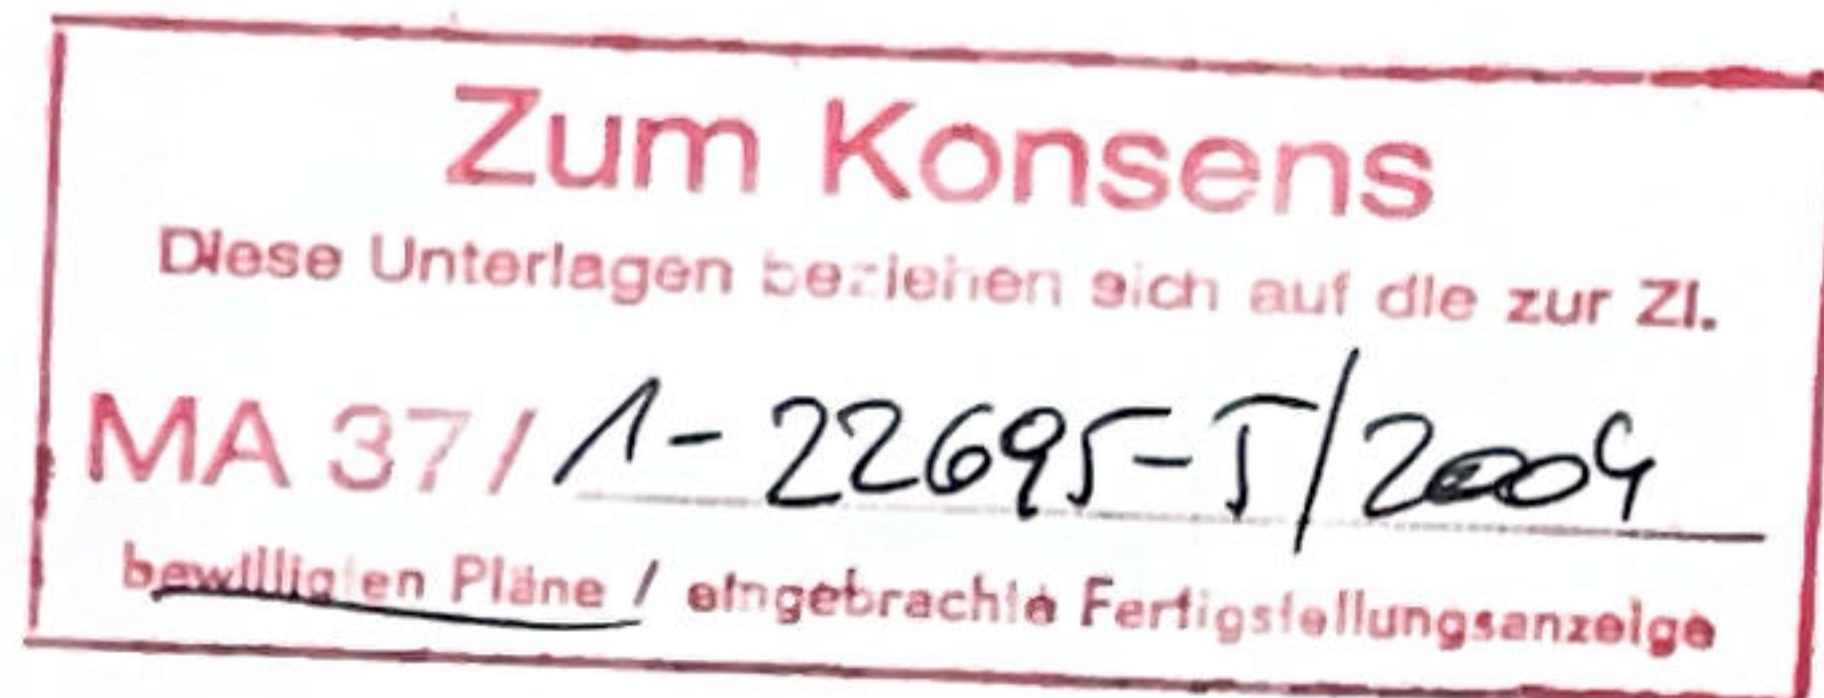

Datum 10.05.2005	Massstab 1 : 50	Plangrösse	Dateiname -	gezeichnet STB
----------------------------	---------------------------	-------------------	-----------------------	--------------------------

Planinhalt Bewehrungsplan Decke über 4.OG -	Plannummer B -001/0
---	--

Projekt Dachgeschossausbau Landesgerichtsstr. 6	Geschäftszahl 2004/33 -
--	---------------------------------------

Planverfasser



D.I. ANDRZEJ GLOGOWSKI

ZIVILINGENIEUR F. BAUWESEN
OTHELLOGASSE 17/19
A-1230 WIEN
TELEFON +43 (0)1-615 39 93
FAX +43 (0)1-615 39 93



25
3

Zum Konsens Diese Unterlagen beziehen sich auf die zur Zl. MA 37 / 1-226PS-5/2004 Bewilligte Pläne / eingebrachte Fertigstellungsanzeige
--



Datum 10.05.2005	Massstab 1 : 50	Plangrösse	Dateiname -	gezeichnet STB
---------------------	--------------------	------------	----------------	-------------------

Planinhalt Schalungsplan Decke über 4.OG -	Plannummer S -001/0
---	----------------------------

Projekt Dachgeschossausbau Landesgerichtsstr. 6	Geschäftszahl 2004/33 -
---	--------------------------------

Planverfasser  D.I. ANDRZEJ GLOGOWSKI ZIVILINGENIEUR F. BAUWESEN OTHELLOGASSE 1/7/19 A-1230 WIEN TELEFON +43 (0)1-615 39 93 FAX +43 (0)1-615 39 93	
--	---