

**Magistrat der Stadt Wien
Magistratsabteilung 37**

Baupolizei
Bezirksstelle f. d. 1. u. 8. Bez.
20, Dresdner Straße 73 - 75
A - 1200 Wien

Einlegen

EZ 894

KG unser Stadt

BEARBEITUNGSBOGEN

FERTIGSTELLUNGSANZEIGE

MA 37/1-Landesgerichtshaus 6/37447-2/2007

Fertigstellungsanzeige zu **MA 37/1-Landesgerichtshaus 6/37447-1/2007**

Belege :

	vorgelegt	nachgereicht am:
- Bestätigung des/der Ziviltechnikers/in	☒	☐
- Erklärung des/r Bauführers/in	☐	☐
- Ausführungsplan/pläne ☐ grau ☐ mit Änderungen	☐	☐
- Überprüfungsbefunde des/der Prüfsachverständigen/in	☐	☐
- Konstruktionspläne	☐	☐
- Gutachten über Rauch- und Abgasfänge	☐	☐
- Gutachten über Kanal bzw. Senkgrube mit Ausführungsplan	☐	☐
- Gutachten über sicherheitstechn. Einrichtungen	☐	☐
- Nachweis über den Wärme- u. Schallschutz	☐	☐
- Bestätigung ü. Maßnahmen z. Schutz v. Emissionen	☐	☐
- <u>Nachweis Erhaltung in Ziv. Best.</u>	☒	☐

Gesetzliche Erfordernisse:

	nicht erford.	erforderlich
- grundbücherliche Durchführung der Abteilung	☒	☐ → ☐ Mitt. an MA 64
- Gehsteigerstellung	☒	☐ → ☐ Mitt. an Gehsteigref.
- Garagenlüftungsanlage FS-Meldung vollständig erstattet	☒	☐ ja ☐ nein

Fertigstellungsanzeige

☐ Unvollständig belegt - Mitteilung erfolgt am:	Nachreichung erfolgte am:
---	--

☒ Vollständig belegt am 12.6.2008 (Tag ab dem das Gebäude / die Baulichkeit benutzt werden darf)

- ☒ Das Bauvorhaben ist daher als abgeschlossen zu beurteilen
- | | | |
|---|--|--|
| → GWR - Meldung erfolgt | ☐ JA | ☒ NICHT ERFORDERLICH |
| → Kanalplan an MA 14-GDV und MA 30 | ☐ JA | ☒ NICHT ERFORDERLICH |
| → Kostenersatz für Gehsteig vorzuschreiben | ☒ NEIN | ☐ JA → Ä.A. |
| → Stellplatzsicherstellung außerhalb des Bauplatzes | ☒ NEIN | ☐ JA → protokollieren u. Kopie einlegen |

☐ 22,00 / 50,00 VA bereits entrichtet

☒ 22,00 / 50,00 VA mittels eBezahlen vorschreiben / vorgeschrieben am :

Der/Die Sachbearbeiter/innen: Kopp.

Für den Abteilungsleiter:

Datum: 13. JUNI 2008

Verfasser (ZiviltechnikerIn):

Wien, 12. VI. 2008

ARCHITEKT DIPL. ING.
ADOLF WOHANKA
STAATL. BEF. U. BEEIDETER
ZIVILTECHNIKER
MILLER GASSE 21
1060 WIEN TEL. 597 13 68

Mit EUR 3,60
Bundesgebühr
zu vergebühren!

Bauvorhaben:

1010 WIEN LANDESGERICHTSTR. 6

(Gegenstand)

MA 39/1 - 37447-1/2007
(Geschäftszahl der ursprünglichen Baubewilligung)

HERSTELLEN EINER KLIMAAULAGE

(Adresse)

Z.V. d. HAUSBESITZER

(BauwerberIn)

Bestätigung

zur Fertigstellungsanzeige gem. § 128 BO

Es wird bestätigt, dass das o.a. Bauvorhaben bewilligungsgemäß und den Bauvorschriften entsprechend ausgeführt wurde.

Pflichtstellplätze:

- ☐ es wurden Pflichtstellplätze
 - ☐ auf dem Bauplatz
 - ☐ außerhalb des Bauplatzesordnungsgemäß hergestellt
- ☐ es waren keine Stellplätze zu schaffen
- ☐ **Weiters wird die Vollständigkeit der Unterlagen bestätigt**

Folgende Unterlagen werden beigelegt:

- ☐ da während der Bauausführung Abänderungen erfolgt sind, wird ein / werden der Ausführung entsprechende/r Plan / Pläne vorgelegt
- ☐ da ein Prüfenieur zu bestellen war, werden die von ihm aufgenommenen Überprüfungsberichte samt Konstruktionsplänen vorgelegt
- ☐ es wird ein positives Gutachten über die vorhandenen Rauch- und Abgasfänge vorgelegt
- ☐ es wird ein positives Gutachten über

- ☐ den Kanal
- ☐ die Senkgrube
- ☐ die Hauskläranlage

sowie ein Plan über diese Anlagen vorgelegt (sofern diese Anlagen nicht im Ausführungsplan dargestellt sind)

- ☐ da besondere sicherheitstechnische Einrichtungen vorzusehen waren, wird ein / werden Gutachten über

- ☐ die Brandmeldeanlage
- ☐ die Sprinkleranlage
- ☐ die Notstromanlage
- ☐

vorgelegt

- ☐ da bauliche Maßnahmen zur Vermeidung von Emissionen gemäß § 134a Abs. 3 vorzusehen waren, wird bestätigt, dass diese Maßnahmen in Form durchgeführt wurden
- ☐ da der Bau hinsichtlich des Wärme- und Schallschutzes anders, als ursprünglich bewilligt ausgeführt wurde, wird ein Nachweis über die Erfüllung des baulichen Wärmeschutzes (Wärmepass) sowie des Schallschutzes vorgelegt

- ☐ Die Endprüfung ergab, dass die Anlage betrieben werden kann.

Magistratsabteilung 37	
Außenstelle f. d. 1. u. 8. Bezirk	
Eing.:	12. JUNI 2008
MA 37/ -	
Zahl	Blg.

ARCHITEKT DIPL. ING.
ADOLF WOHANKA
STAATL. BEF. U. BEEIDETER
ZIVILTECHNIKER
MILLER GASSE 21
1060 WIEN TEL. 597 13 68

(Unterschrift des/der ZiviltechnikerIn)

MAGISTRAT DER STADT WIEN

Magistratsabteilung 37

Baupolizei

Bezirksstelle für den 1. und 8. Bezirk

Dresdner Straße 73-75 1. Stock

A - 1200 Wien

DVR:0000191

UID: ATU36801500

Fax: 4000 99 01500

Tel.: 4000 01500

e-mail: 01.08@ma37.wien.gv.at

Zugestellt am: 17. JAN. 2008

MA 37/1 - Landesgerichtsstraße 6/37447-1/2007

Wien, 14. Jänner 2008

1. Bezirk, Landesgerichtsstraße ONr. 6
EZ 894 der Kat.-Gemeinde Innere Stadt

Erliegt mit Planwechsel

**Zl. MA 37 /
Fertigstellung Zl. MA 37 / 1-37447-2/2007
Plankammer zur Ablage in EZ: 894/I**

Herstellung einer Klimaanlage

Baubewilligung

13 JUNI 2008

BESCHEID

Nach Maßgabe der mit dem amtlichen Sichtvermerk versehenen Pläne und Beschreibungen wird gemäß § 61 der Bauordnung für Wien (BO) die teilweise nachträgliche Bewilligung erteilt, auf der im Betreff genannten Liegenschaft die nachstehend beschriebene Bauführung vorzunehmen:

Auf dem Stiegenhausdach der oben genannten Liegenschaft soll eine Klimaanlage zur Klimatisierung des Dachgeschosses hergestellt werden.

Vorgeschrieben wird:

Die Klimaanlage darf ausschließlich zur Tagzeit (6:00 - 22:00 Uhr) betrieben werden.

- 1.) Luftleitungen müssen aus nicht brennbaren Baustoffen betriebsdicht hergestellt sein ÖNORM B 3800.
- 2.) Die Luftleitungen sind an der luftführenden Seite regelmäßig, mindestens einmal jährlich auf Verschmutzung zu überprüfen und erforderlichenfalls zu reinigen bzw. zu erneuern. Die Nachweise über die vorgenommenen Reinigungen sind in der Betriebsanlage aufzubewahren und den Organen der Behörde auf Verlangen vorzulegen.
- 3.) Durch schalldämmende Maßnahmen, wie z. B. Einbau von elastischen Zwischenstücken an der Saug- und Druckstelle des Ventilators, schwingungsfreie Halterungen bei Rohreinbauventilatoren, Aufstellen der Ventilatoren auf schalldämmende Unterlagen, Einbau von Schalldämpfern in Saug- und Druckrohren ist sicherzustellen, dass durch den Betrieb der Lüftungsanlage keine Unzumutbare Belästigung der Nachbarn erfolgt.
- 4.) Nach Fertigstellung der Lüftungsanlage ist gem. § 128 Abs. 1 BO bei der Baubehörde vom Bauwerber, vom Eigentümer (einem Miteigentümer) der Baulichkeit oder vom Grundeigentümer (einem Grundeigentümer) eine Fertigstellungsanzeige zu erstatten, der gemäß § 128 Abs. 2 BO folgende Unterlagen anzuschließen sind:
 - eine Bestätigung eines Ziviltechnikers über die bewilligungsgemäße und den Bauvorschriften entsprechende Bauausführung

- wenn während der Bauausführung Abänderungen erfolgt sind, ungeachtet der hierfür erwirkten Bewilligung oder Kenntnisnahme, ein der Ausführung entsprechender Plan, der von einem/r hierzu Berechtigten verfasst und von ihm/ihr sowie vom/von der Bauführer/in der Lüftungsanlage unterfertigt sein muss
- den Nachweis über die Ersterprobung der Lüftung.

Auf die Vorlage der übrigen im § 128 Abs. 2 BO genannten Unterlagen wird gemäß § 128 Abs. 3 BO verzichtet.

B e g r ü n d u n g

Der dem Bescheid zu Grunde gelegte Sachverhalt ist den eingereichten Plänen und technischen Beschreibungen und dem Ergebnis des durchgeführten Ermittlungsverfahrens entnommen. Die Bauführung ist nach den bestehenden Rechtsvorschriften zulässig. Die vorgeschriebenen Auflagen sind in der BO für Wien und den einschlägigen Nebengesetzen begründet. Etwaige privatrechtliche Vereinbarungen waren im Baubewilligungsverfahren nicht zu prüfen.

R e c h t s m i t t e l b e l e h r u n g

Gegen diesen Bescheid kann binnen zwei Wochen nach Zustellung bei diesem Amt schriftlich Berufung eingebracht werden. Die Berufung hat den Bescheid zu bezeichnen, gegen den sie sich richtet und einen begründeten Berufungsantrag zu enthalten. Bewilligungswerber/innen (Antragsteller/innen) haben die Berufung mit EUR 13,20 Bundesgebühr zu vergebühren. Die Gebühr ist durch Barzahlung oder mittels Bankomatkarte (auch mit Quickfunktion) in unserem Amt oder in einer der Kassen der Stadt Wien (diese befinden sich u.a. in jedem Magistratischen Bezirksamt) zu entrichten. Bei Bezahlung ist der Verwendungszweck und die Aktenzahl anzugeben und der Einzahlungsbeleg dem Berufungsantrag anzuschließen.

Die telefonische oder mündliche Einbringung der Berufung ist nicht zulässig.

Nur bei eBezahlen

Ausstehende Gebühren und Abgaben werden gesondert vorgeschrieben. Sie erhalten in den nächsten Tagen einen Zahlschein. Sie können aber auch unter Vorlage des Zahlscheines bei einer Kassa der Stadt Wien bar oder mittels Bankomat einzahlen. Weiters haben Sie die Möglichkeit die Bezahlung mittels Internet, über das „Bezahlservice“ der Stadt Wien (www.wien.at/bezahlen) vorzunehmen.

Ergeht als Bescheid an:

- 1.)2.) Zentralverband der Hausbesitzer von Wien und den Ländern Österreich, als Bauwerberin und Grundeigentümerin zu Händen Immobilienverwaltung Dr. Friedrich Noszek GmbH, Untere Viaduktgasse 11/6, 1030 Wien, unter Anschluss der Pläne A und B, der technischen Beschreibungen A und B sowie der Formulare „Fertigstellungsanzeige“ und „Bestätigung zur Fertigstellungsanzeige“
- 3.) Wiener Umweltschlichtung

In Abschrift an:

- 4.) Icebear Entfeuchtung & Klima GmbH, Himberger Straße 2, 1100 Wien, als Bauführerin

- 5.) Herrn Architekt Dipl.-Ing. Adolf Wohanka, Millergasse 21, 1060 Wien, als Planverfasser
- 6.) MA 37/1 - unter Anschluss des Planes C und der technischen Beschreibung C
- 7.) Finanzamt für Gebühren und Verkehrsteuern
- 8.) zum Akt

Die Sachbearbeiterin:
Ing. Staeger Gabriele
Tel. 4000/08513 DW

Für den Abteilungsleiter:
Dipl.-Ing. Fischer
Oberstadtbaurat

Wichtige Informationen und Formulare im Internet:
www.bauen.wien.at

26
2

7.20

PARIE	A	B	C	1	2	3	4
-------	---	---	---	---	---	---	---

EINREICHPLAN

ÜBER DIE ERRICHTUNG EINER KLIMAAANLAGE
AM DACH DES HAUSES

**LANDESGERICHTSSTRASSE 6
1010 WIEN**

EZ	GST	KATASTRALGEM.
894	1526/2	Innere Stadt

BAUWERBER

Zentralverband der Hausbesitzer von Wien
und den Ländern Österreichs
Landesgerichtsstraße 6
1010 Wien

IMMOBILIENVERW. / MAKLER
Dr. FRIEDRICH NOSZEK GmbH
1030 Wien, Unt. Viaduktg. 11/6

GRUNDEIGENTÜMER

Zentralverband der Hausbesitzer von Wien
und den Ländern Österreichs
Landesgerichtsstraße 6
1010 Wien

IMMOBILIENVERW. / MAKLER
Dr. FRIEDRICH NOSZEK GmbH
1030 Wien, Unt. Viaduktg. 11/6

PLANVERFASSTER

Architekt Dipl.Ing. ADOLF WOHANKA
MILLERGASSE 21, 1060 WIEN
Tel.: 597 13 68 Fax: 596 24 30



AUSFÜHRENDE FIRMA

Icebear Entfeuchtung & Klima GmbH
Himberger Straße 2 1100 Wien
Tel.: 889 36 40... Fax.: 889 36 75



DATUM	PLANNR.	BAUTEIL	Maßstab
Juni 2007			M = 1:100

BEHÖRDE

Magistrat der Stadt Wien
Magistratsabteilung 37
Baupolizei

MA 37/1-37447-1/2007

Hierauf bezieht sich der Bescheid

Für den Abteilungsleiter:
Dipl.-Ing. Fischer

Wien, 14.1.2008

Fischer



Magistratsabteilung 19
Zahl: B1/10621/07
Beilagen: Plan
EING.: 16. OKT. 2007
AUSGANG: 22. OKT. 2007

Franz

BESCHREIBUNG:

Das Klimagerät wurde innen so weit möglich zur Gänze mit einer Schallschutzmatte ausgekleidet.

Der Motorschutzschalter und der Druckkessel wurden noch zusätzlich ummantelt.

Das gesamte Gerät wurde voll elastisch auf Gummipuffern aufgelagert.

Eine technische Beschreibung der Firma eisbär (Icebear Entfeuchtung & Klima GmbH) liegt bei.
Ansprechpartner: Ing. Thomas Aussprung 01/8893640

Das Klimagerät dient der Beheizung sowie Kühlung des neu ausgebauten Dachgeschosses.

Betriebszeiten: Montag- ~~Freitag~~ 6:00 - 20:00


Fenster

U = 1,9 W / m² K

R_w = 40 dB

g = 0,67

z = 0,27 (Außenjalousien)

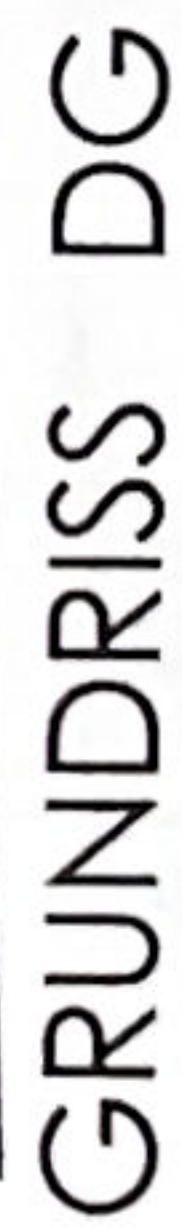


Stahltragkonstruktion mit VSG
(ersetzt alte Schachturnwehrung)
Schacht innen: 1380 * 1520 mm
Kabine: 900 breit * 1050 tief

TOP 13:

Anteil DG	238,93 m2
Anteil Galerie	105,32 m2
Summe	344,25 m2


SUMME = 98
SITZPLÄTZE

Absturzicherung h= 105 cm
wegklappbar

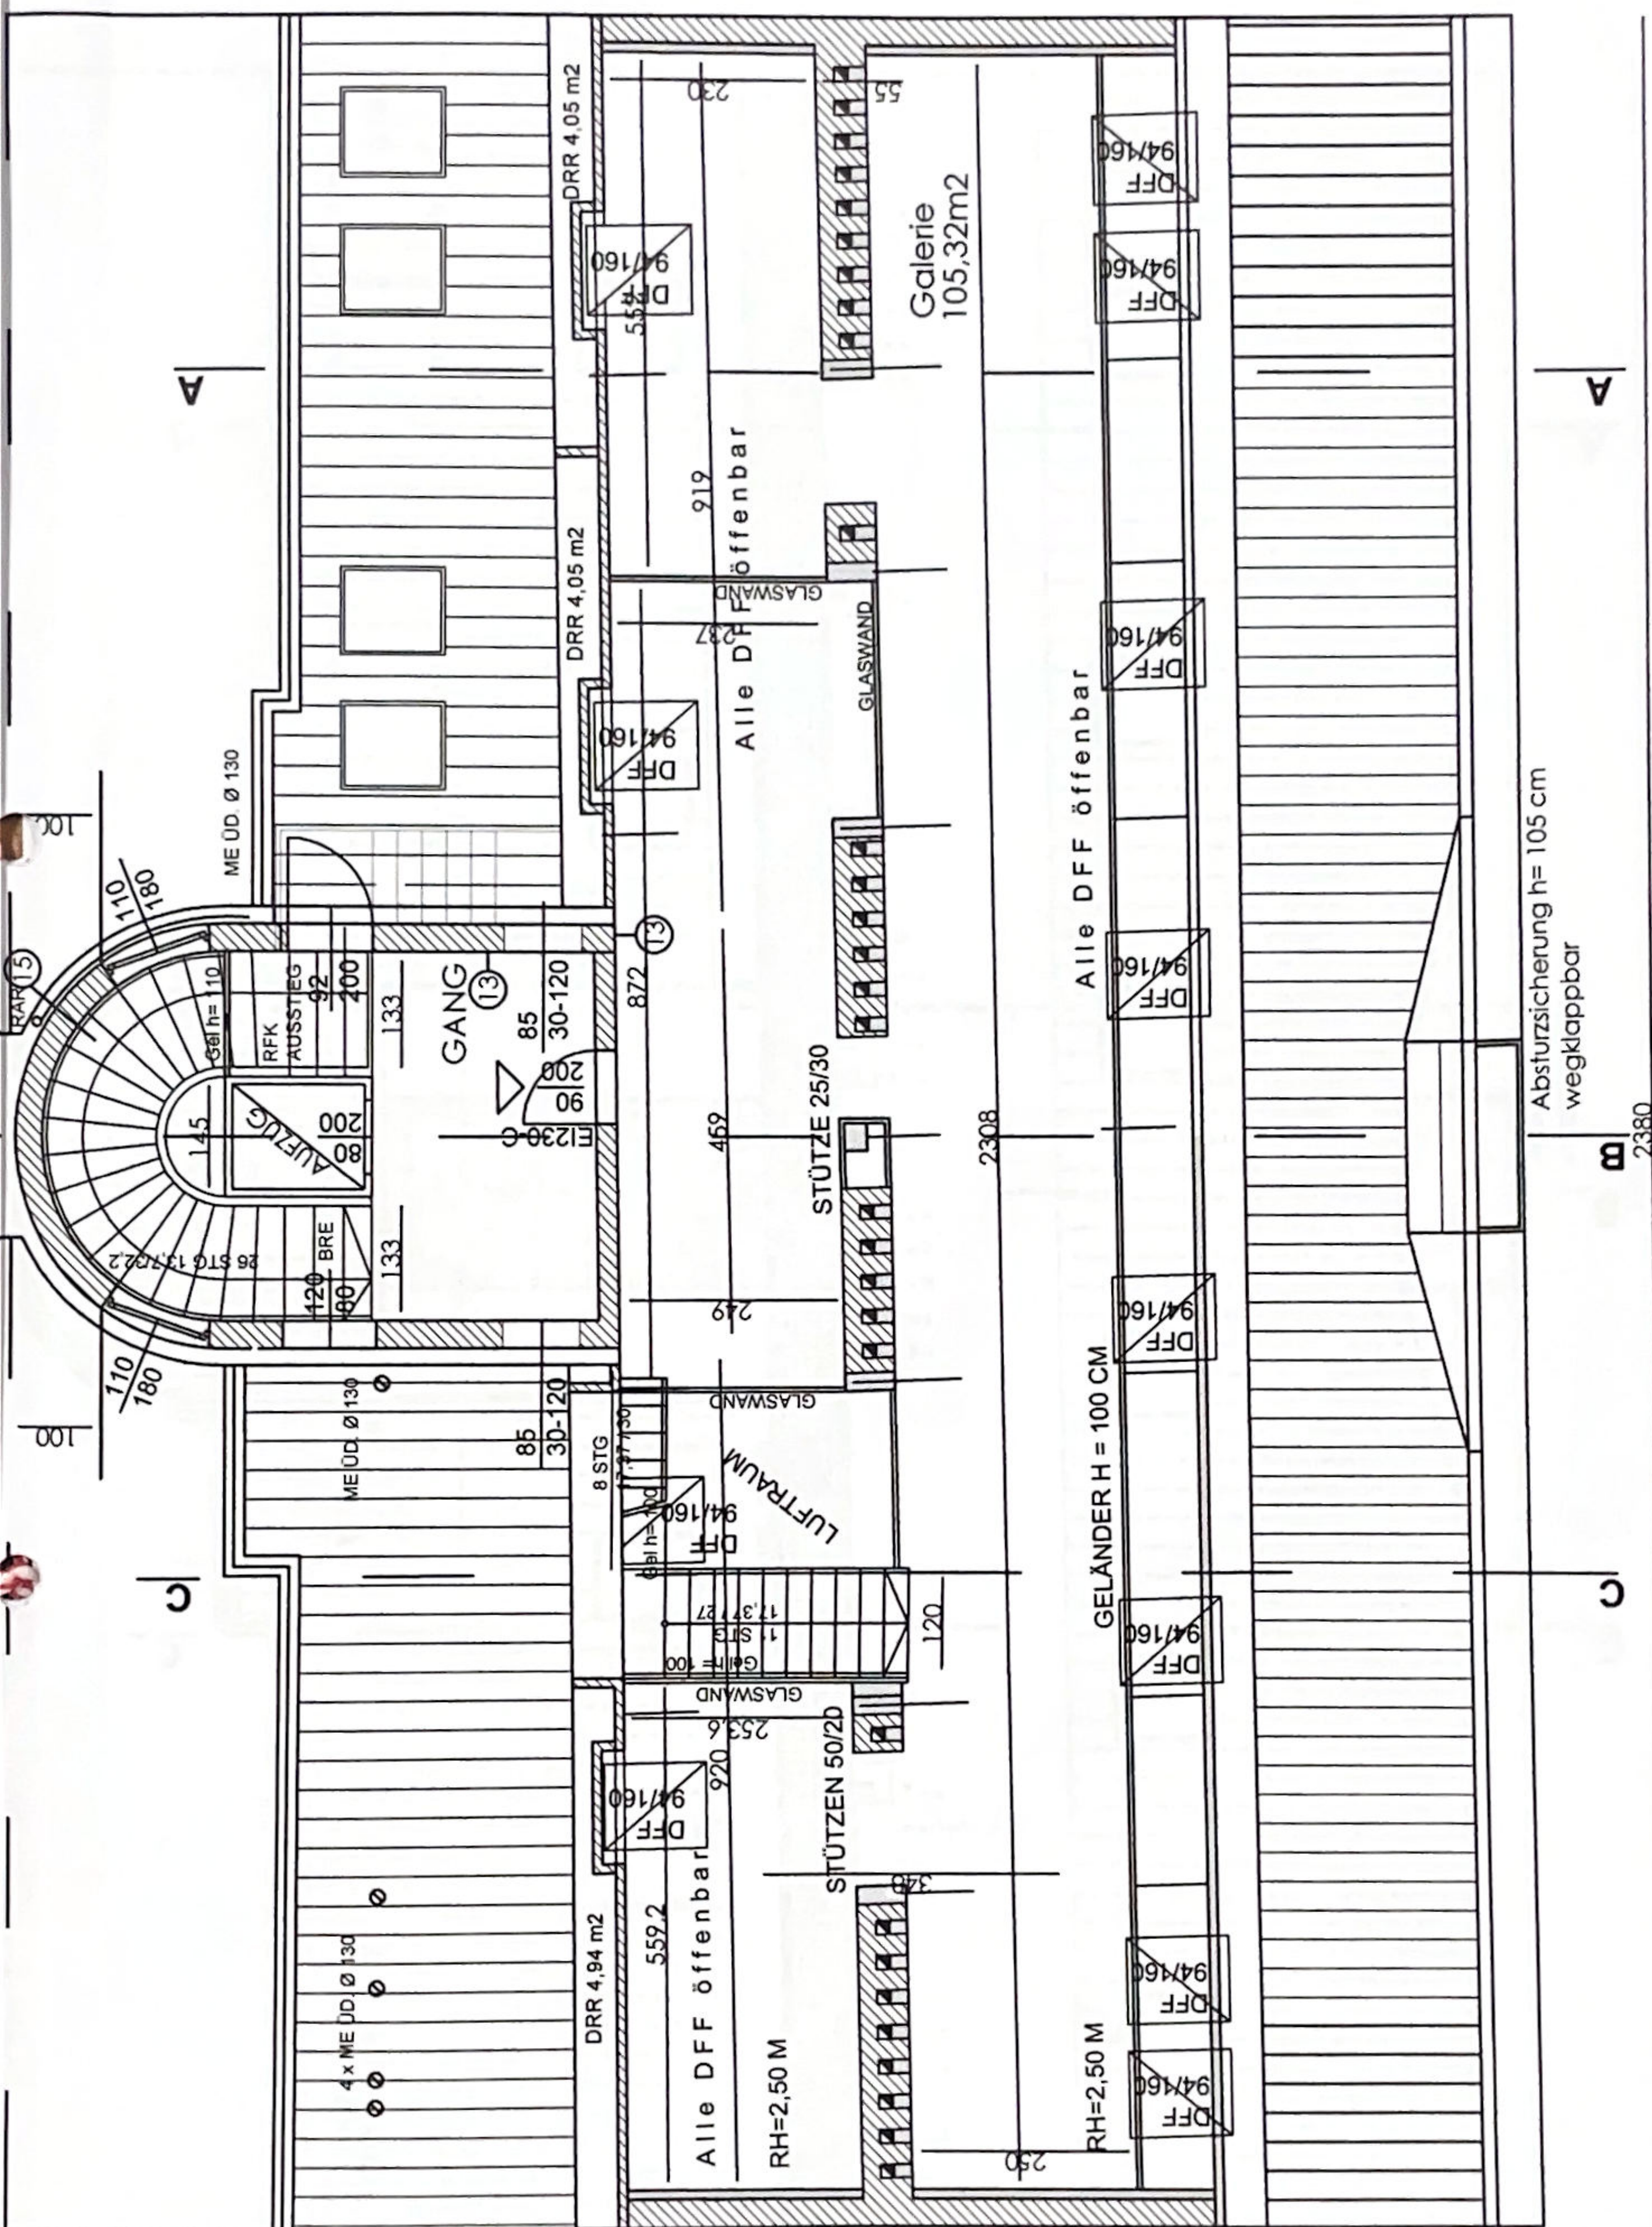


GALERIE

Gauppenbreite=660 ($<2380/3 = 793$)

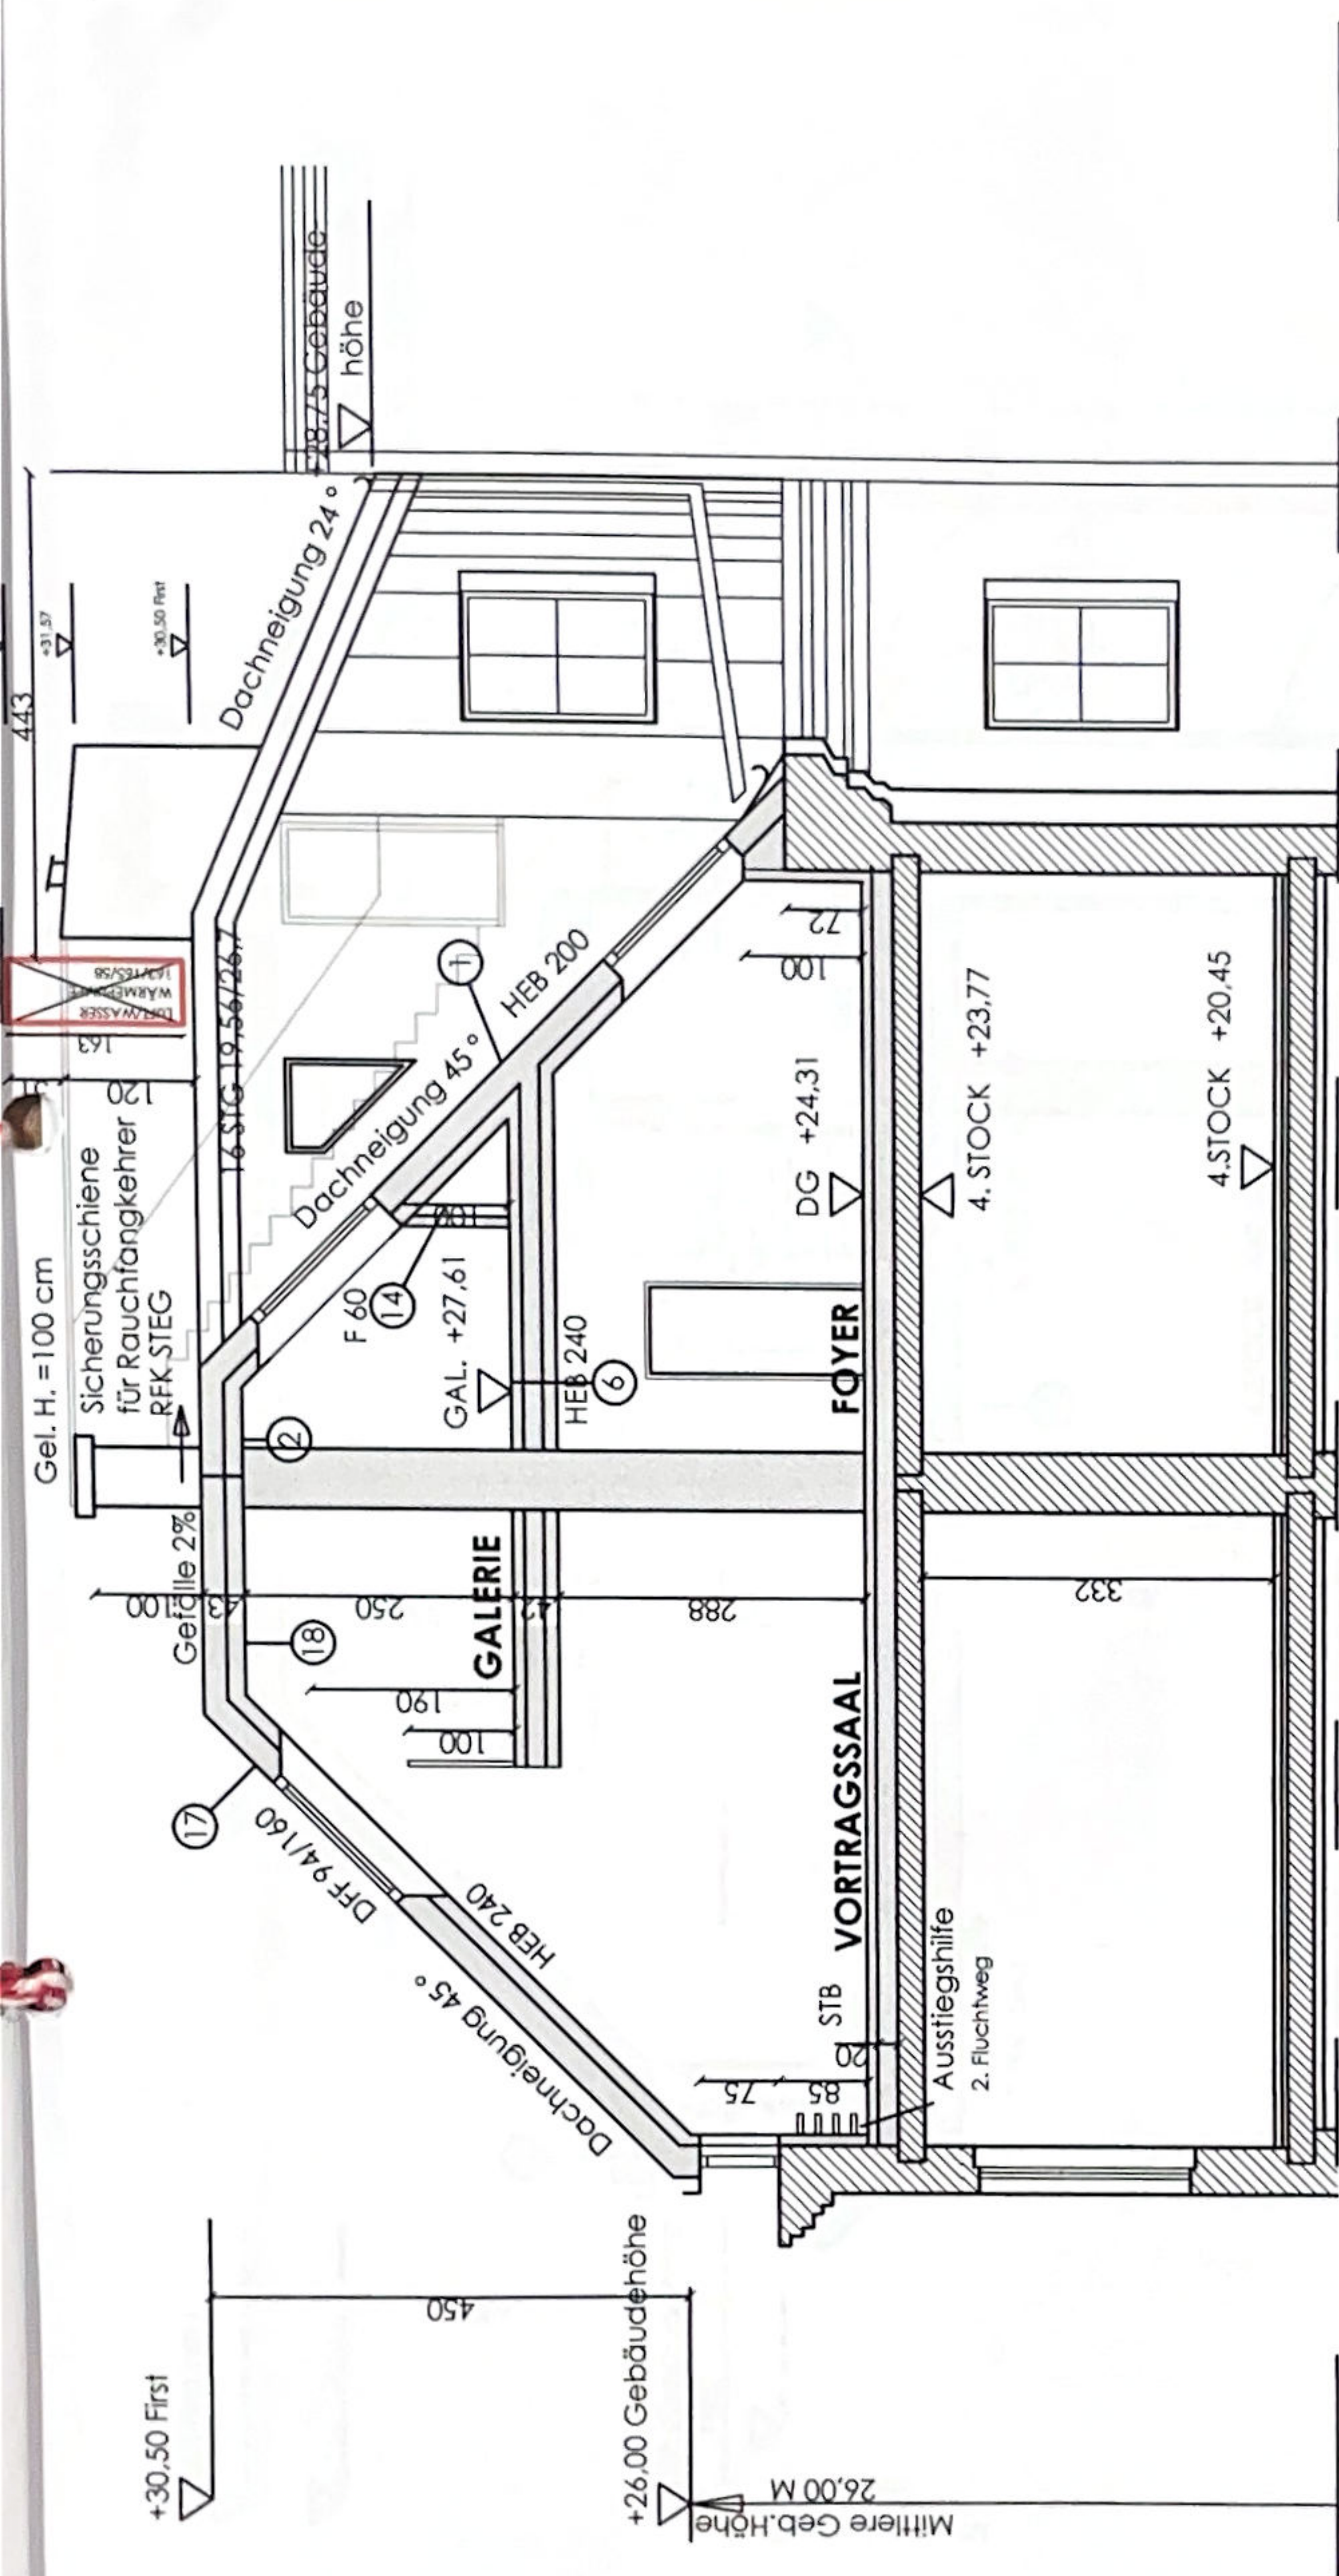

GEHSTEIGNIVEAU
LANDESGERICHTSSTR.6

+0,00 Gehsteigmittel

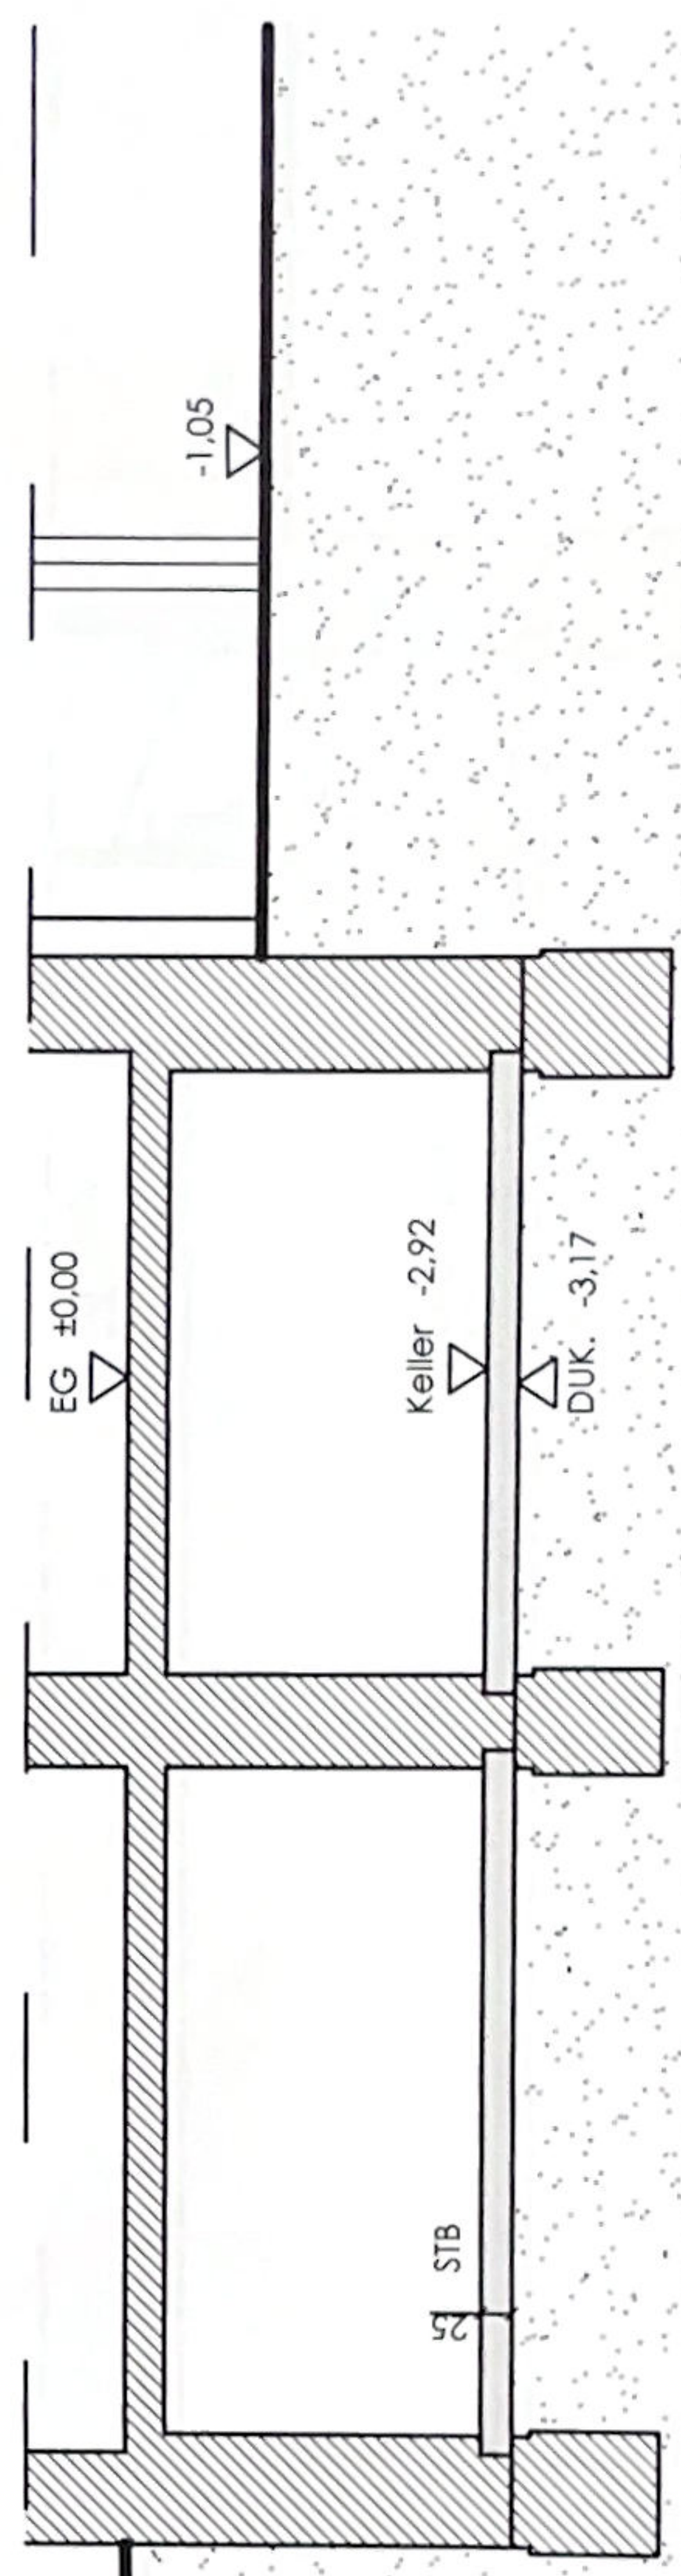

SCHNITT A - A

2380

1110,1

165

1104,9

* = Absturzsicherung h= 105 cm
wegklappbar

+30,50 First










100


173

100

+26,00 Gebäudehöhe

Mittlere Geb.Höhe 26,00 m

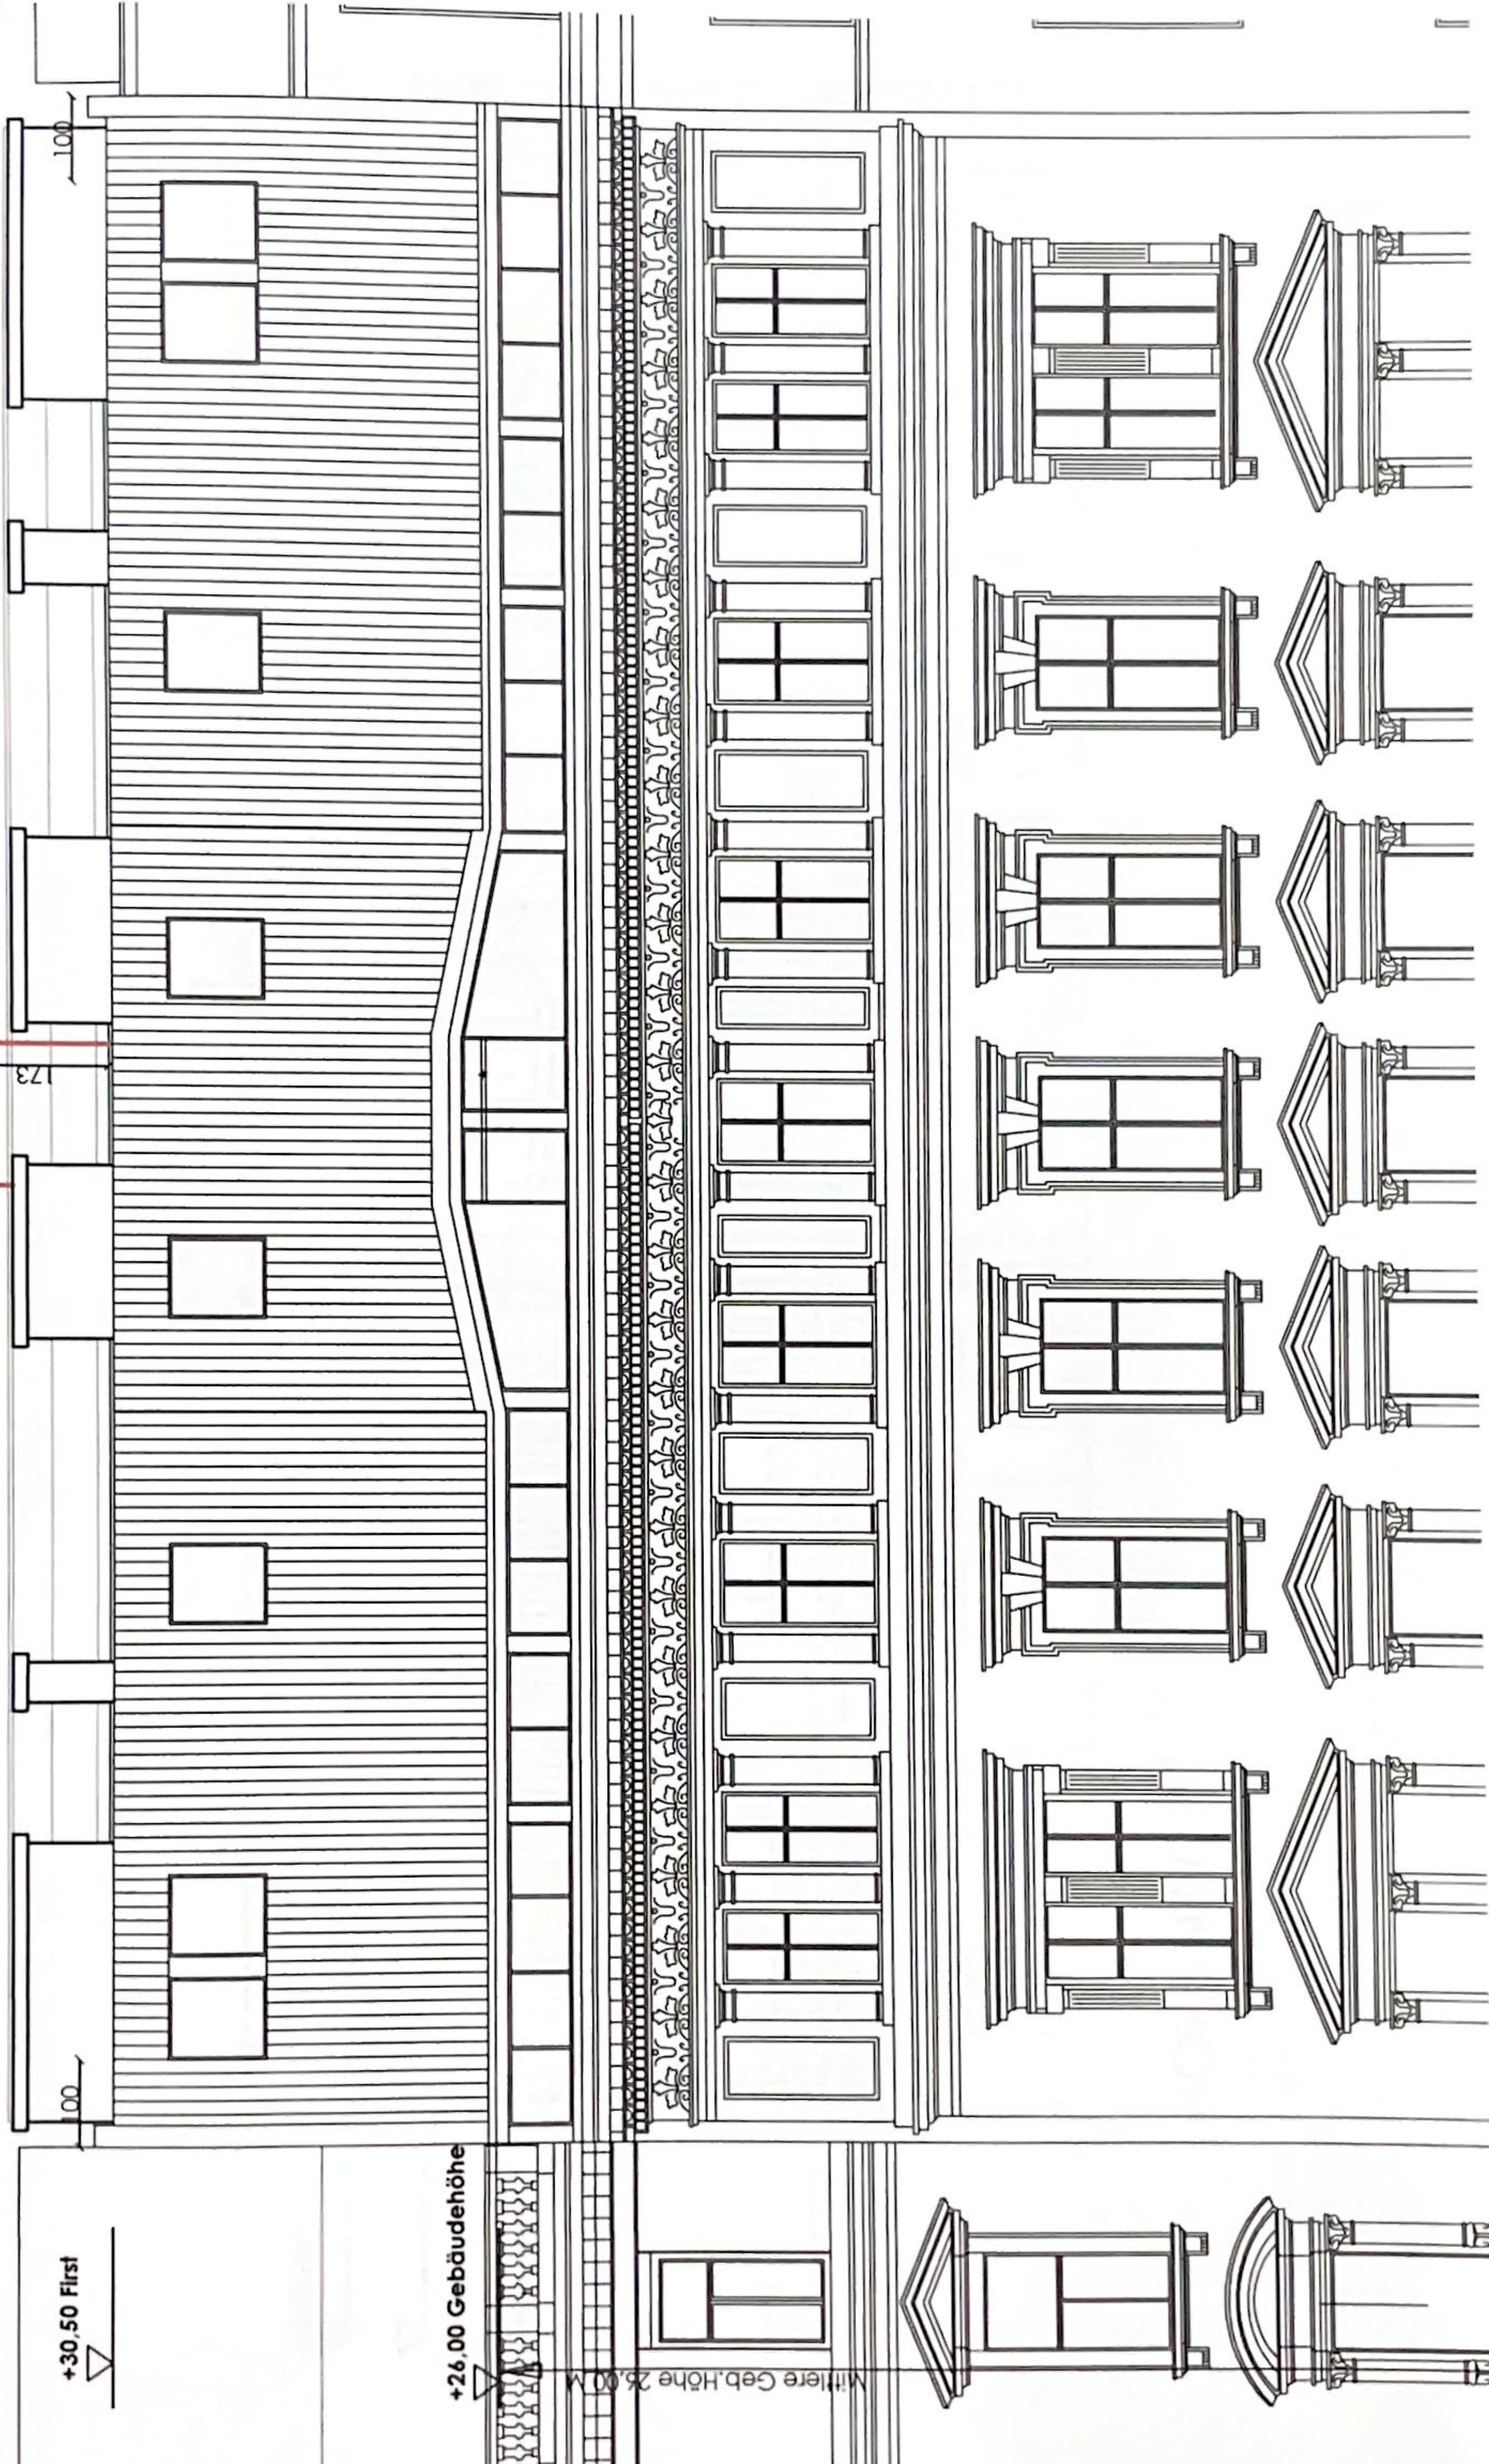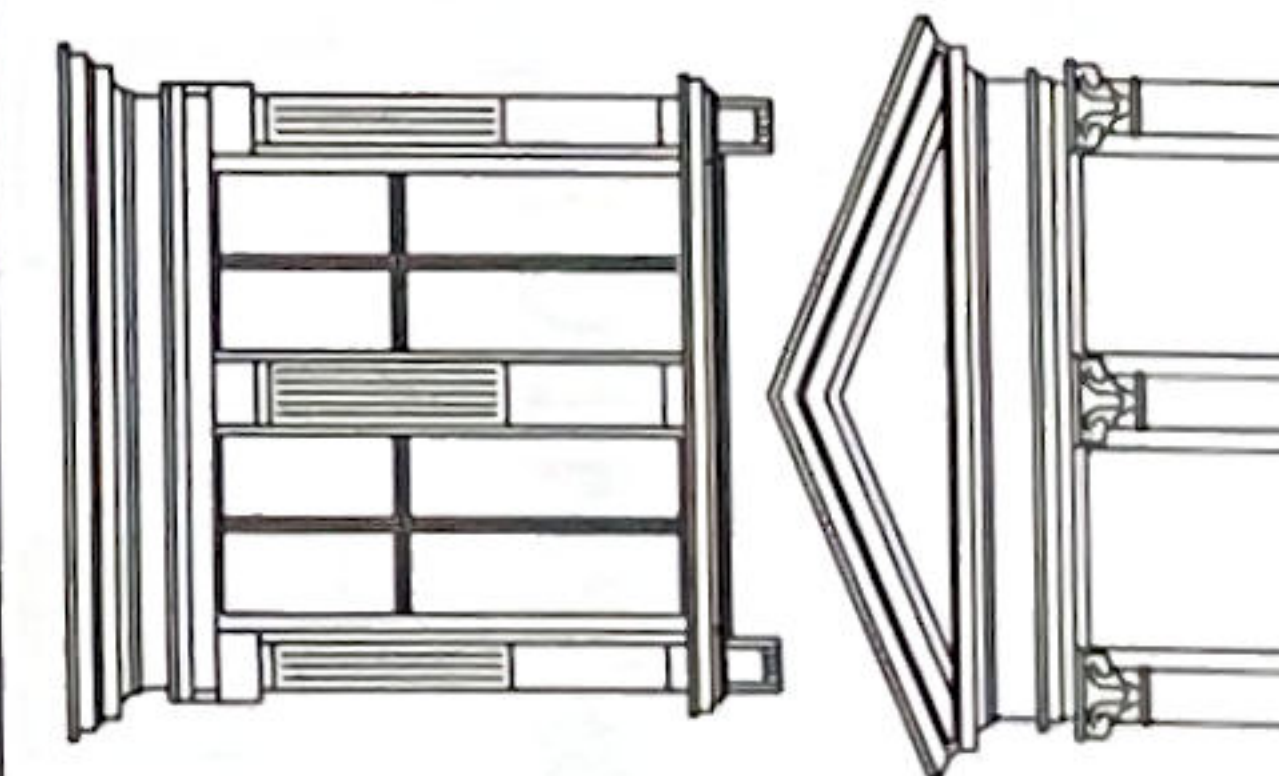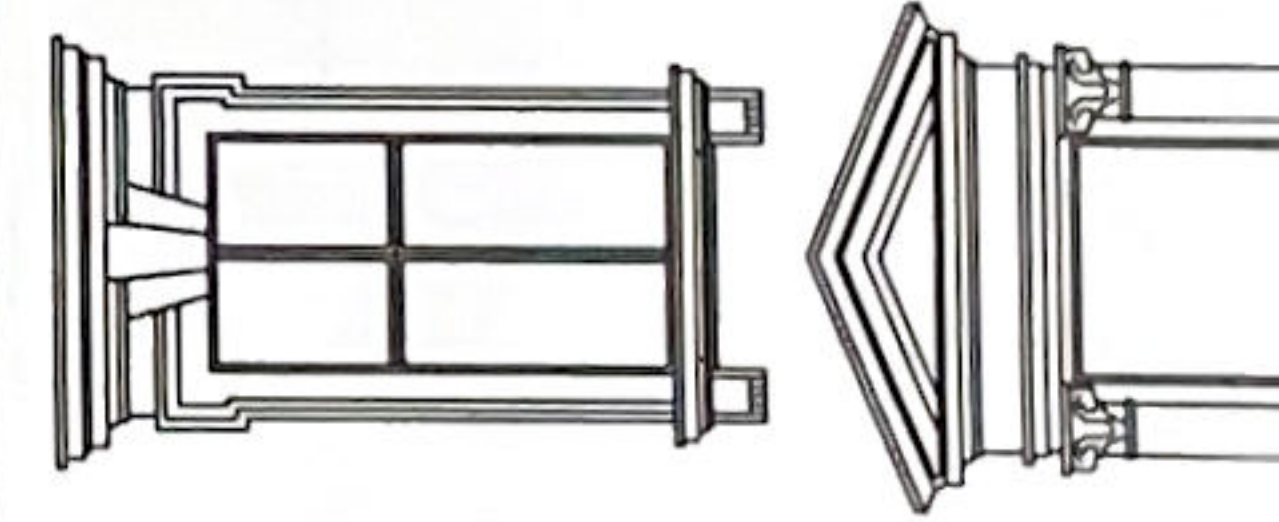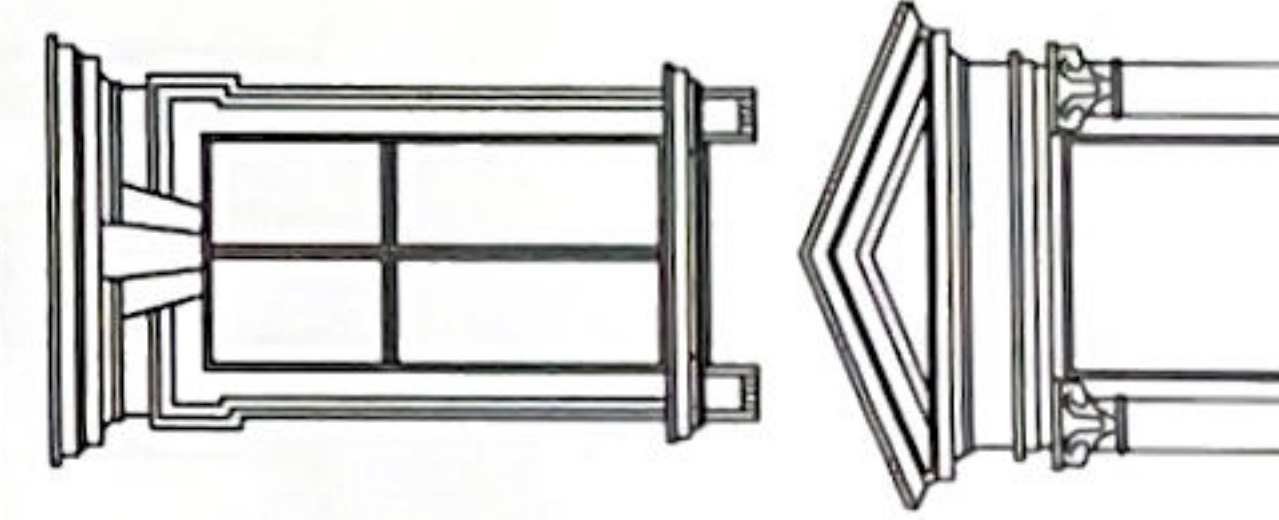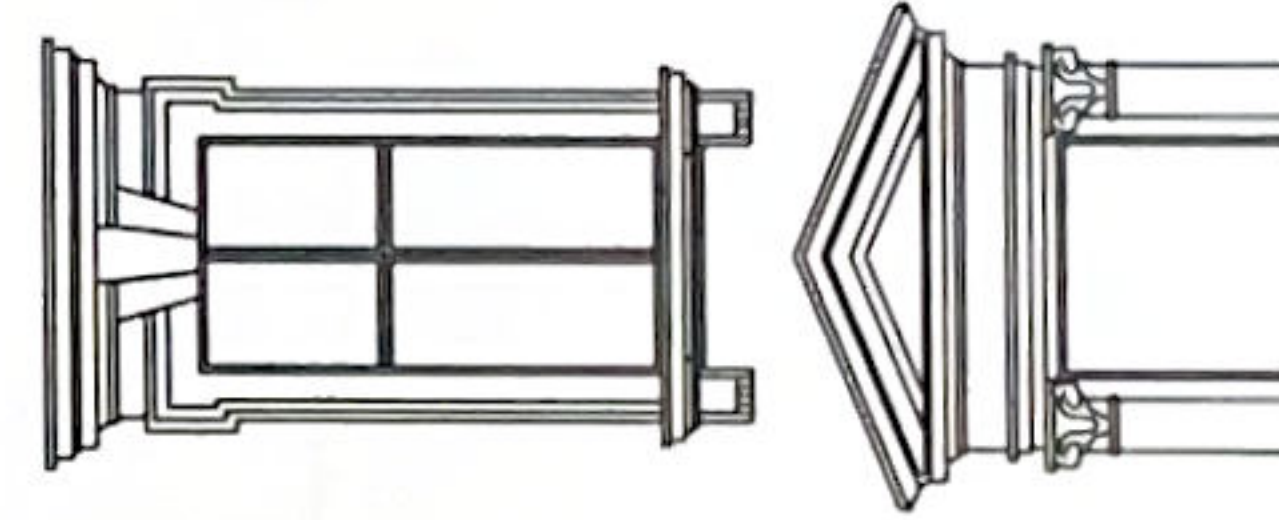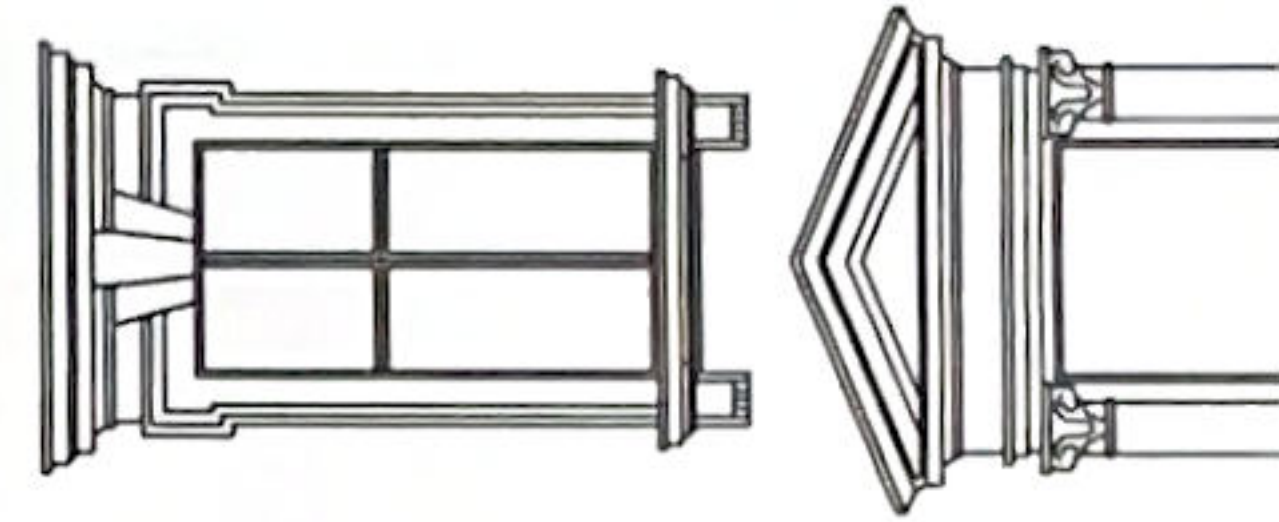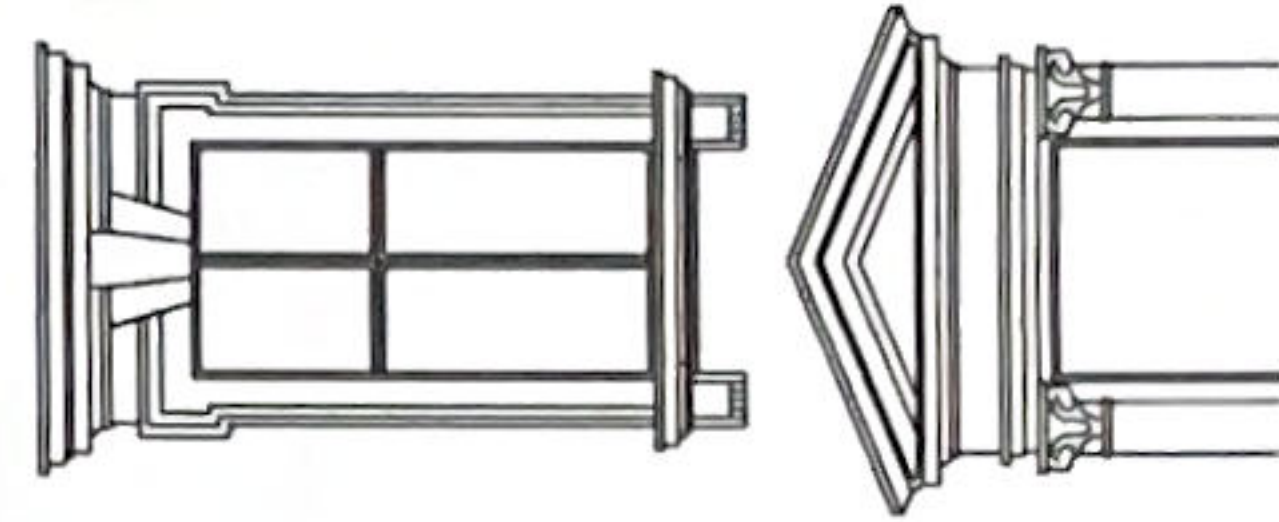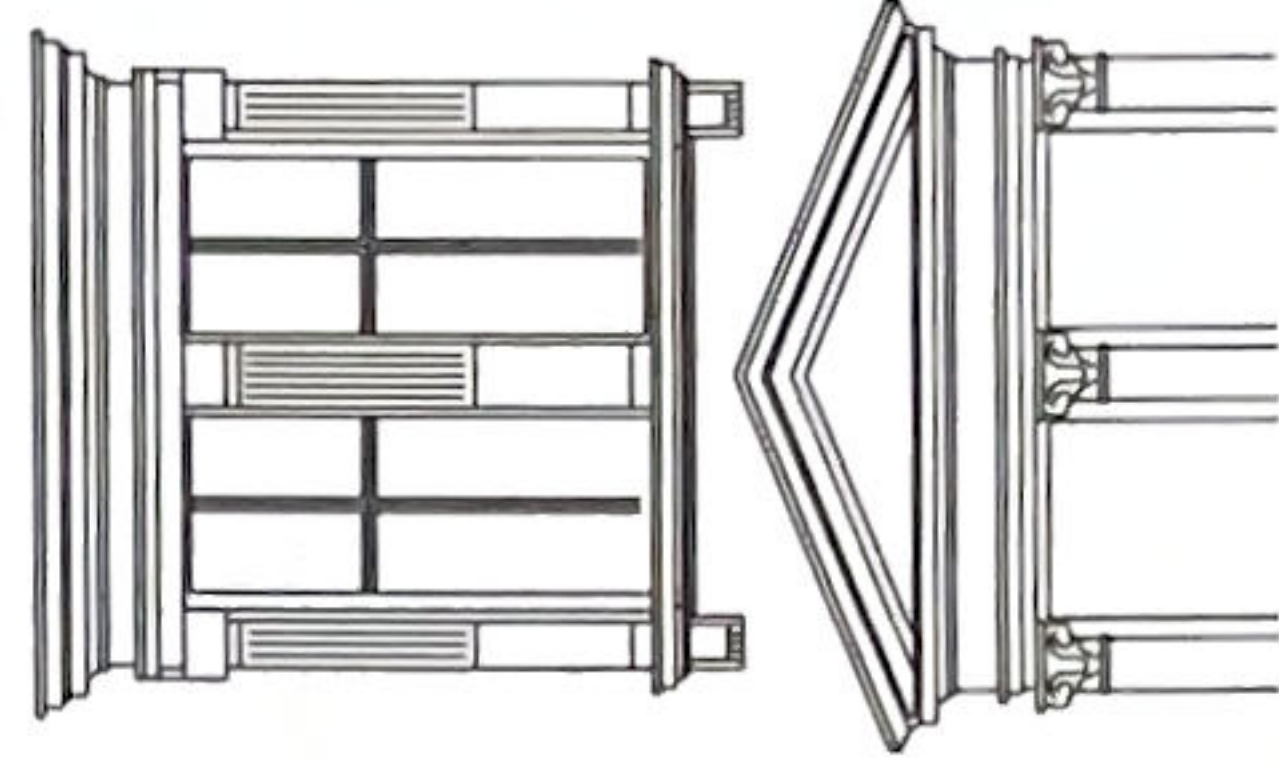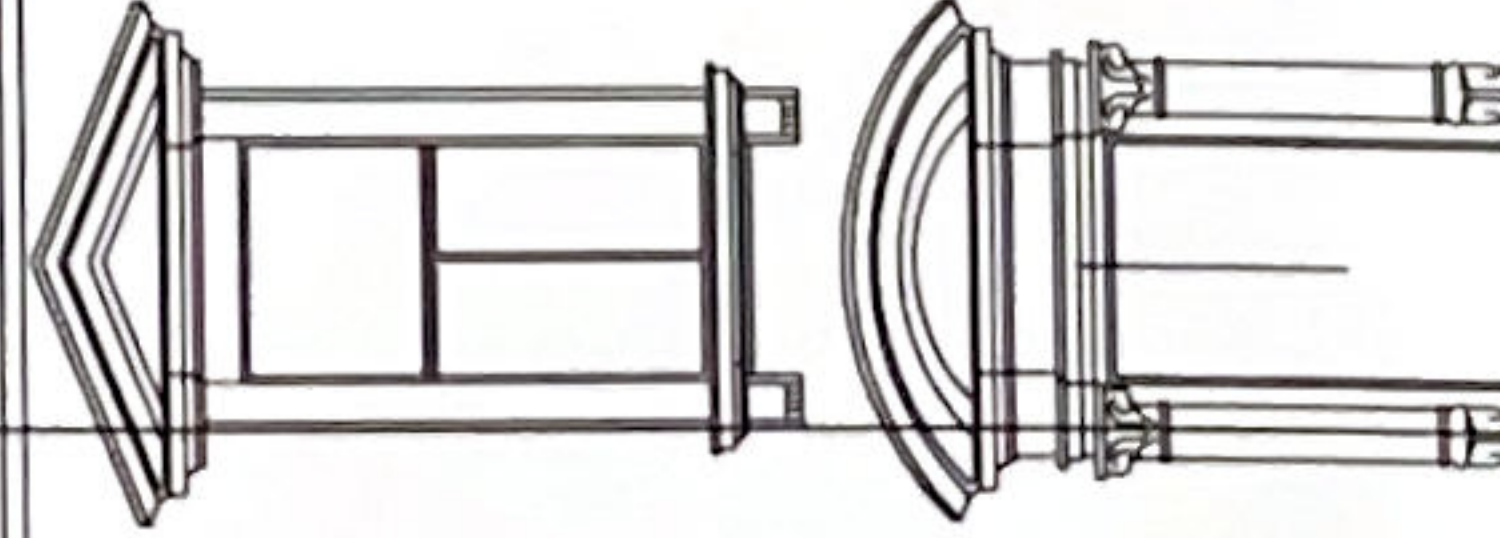

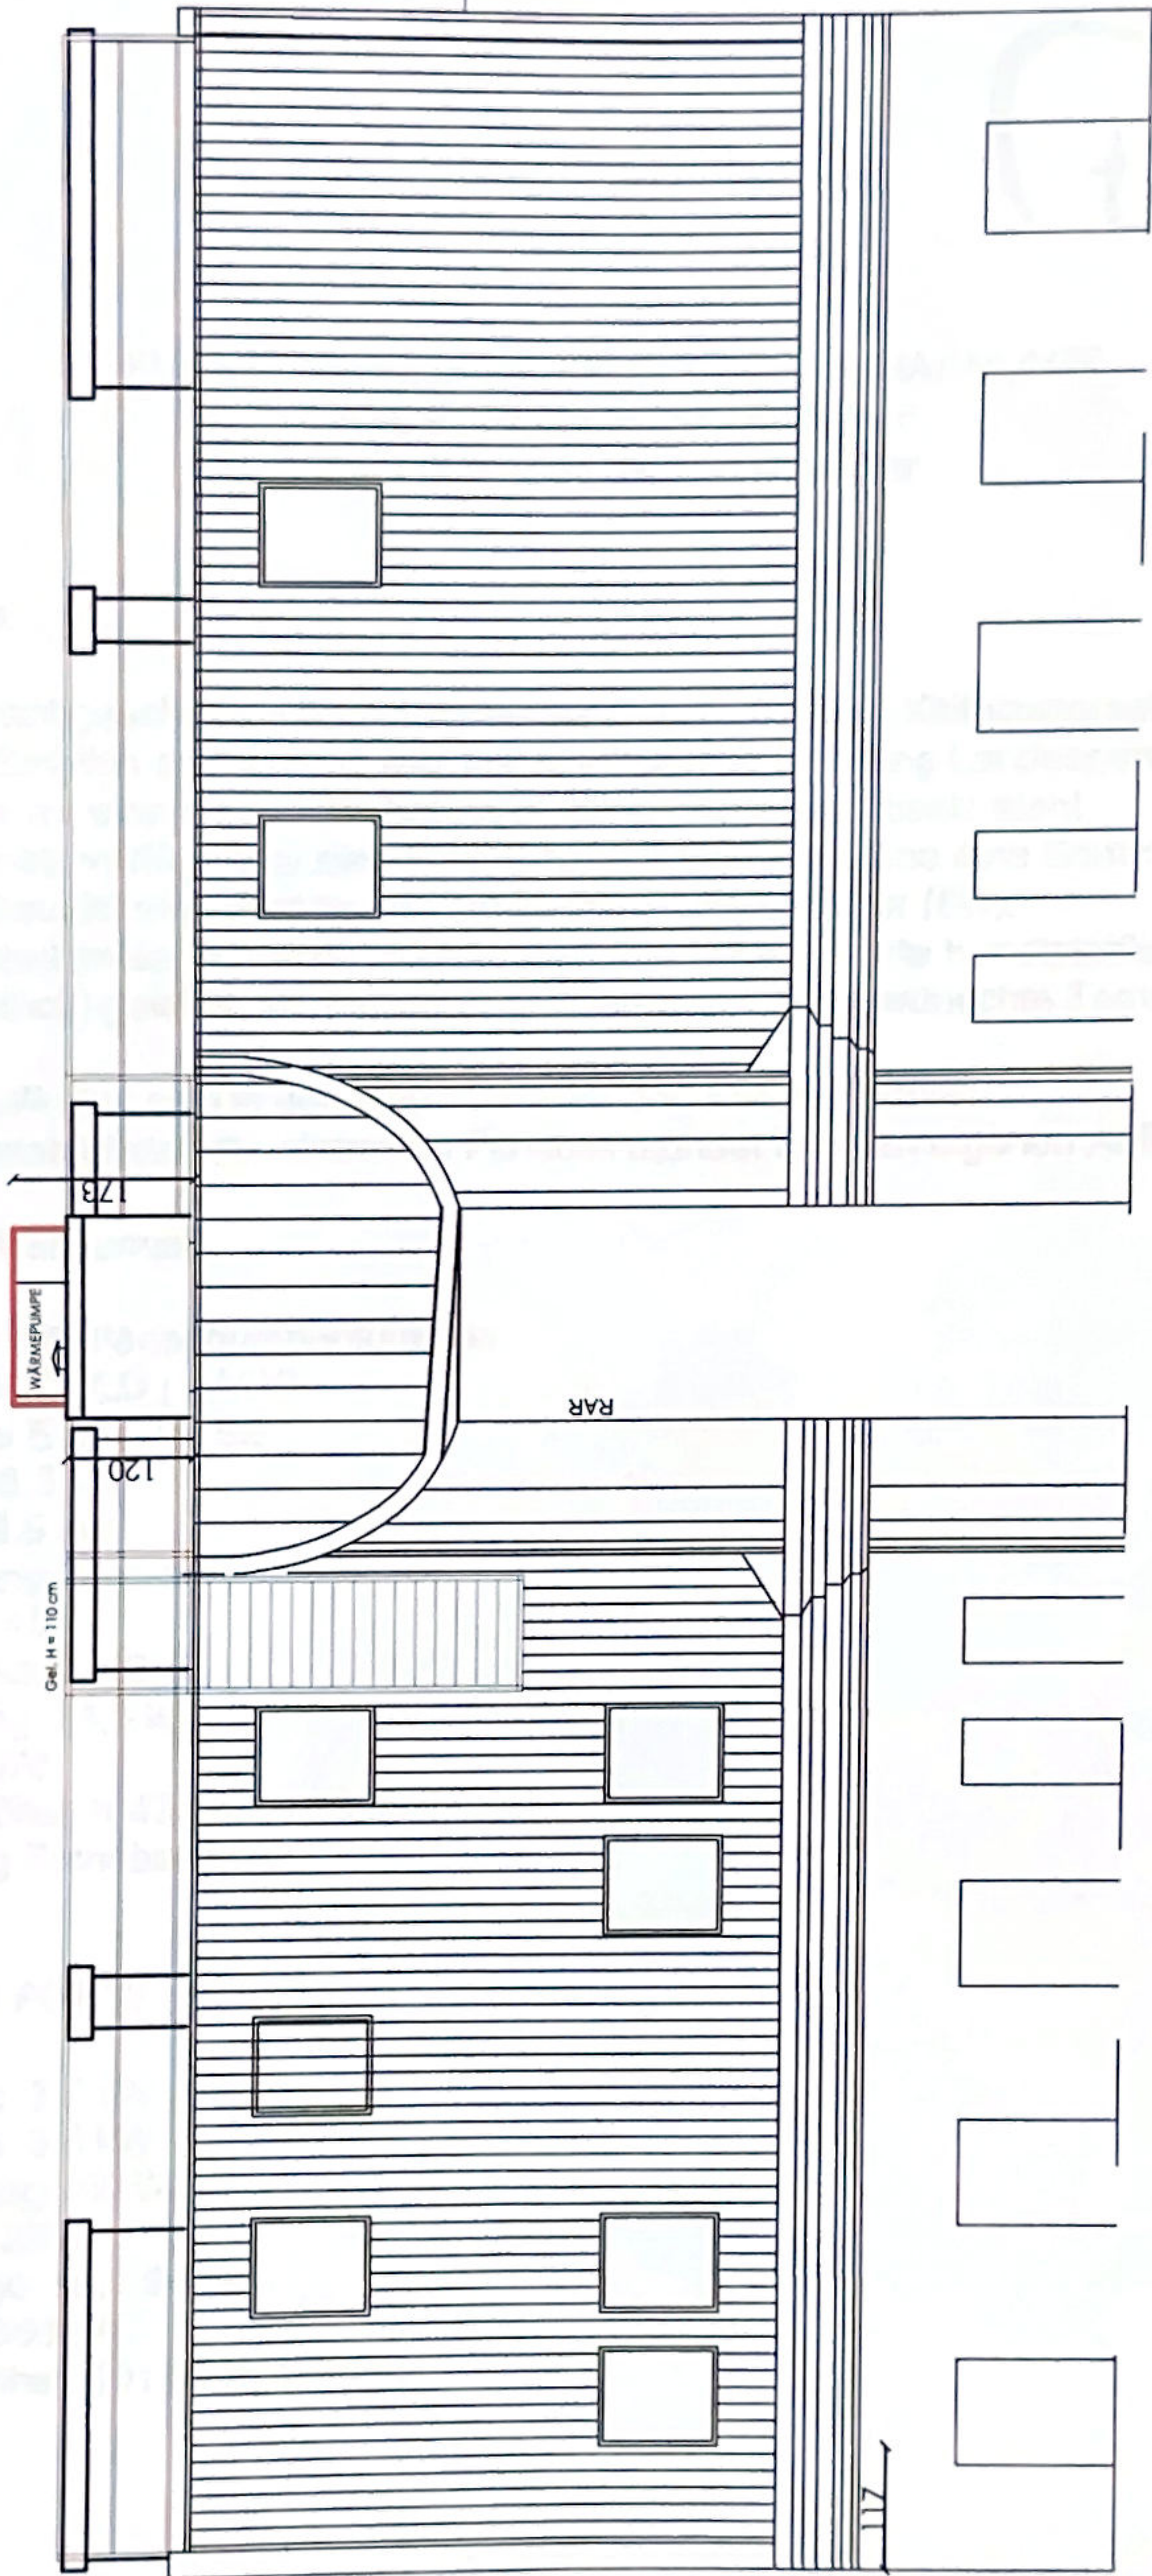

HOFANSICHT

+30,50 First

+28,75
Gebäudehöhe
Stiegenhaus

+25,05

FUNKTIONSBESCHREIBUNG DER KLIMAANLAGE
LANDESGERICHTSSTRASSE 6
Zentralverband der Hausbesitzer

1. Allgemeines

Am Dach des Dachgeschoßausbaus Landesgerichtsstr. 6 ist ein Kaltwassersatz mit Wärmepumpenfunktion so montiert, dass die Abluftseite in Richtung Landesgerichtsstraße weist, und die Ansaugseite vor einem ca. 1,3m hohen blechverkleidetem Absatz steht.

Der Kaltwassersatz verfügt über eine Fern EIN/AUS Schaltung und eine Sommer/Winter Schaltung. Im Gerät eingebaut ist eine Pumpe und ein kleiner Pufferspeicher (80l).

Das mit Frostschutzmittel versetzte Wasser wird über eine isolierte Kunststoffleitung zu einzelnen Fan Coils (11 Stück) geleitet, wo mittels Raumthermostat die gewünschte Temperatur eingestellt werden kann.

Die Fan Coils befinden sich in den Räumen unter den Fensterflächen

Ein Kondenswasserablauf der einzelnen Fancoils mündet in einen eigenen Abfluss.

2. Gerätespezifikationen:

Kaltwassersatz mit Wärmepumpenfunktion

Marke: THERMOCOLD (ITALY)

Type: Miniexcel E 138 ZH SE

Kälteleistung: 35,3 kW

Heizleistung: 39,5 kW

Anschlussleistung: 16,5 kW

Strom: 28,2 A / 400V

Schalldruckpegel: 53dB(A)

Kältemittelfüllung: 14,5 kg

Kältemittel: R407c

Länge/Breite/Höhe: 1647/583/1630 mm

Gewicht: 408 kg Betriebsbereit

Fan Coils

Marke: TONON FORTY

Type: VTI 40

Kühlleistung: ca. 3,2 kW

Heizleistung: ca. 3,8 kW

Anschlussleistung: 90 W

Strom: 0,39 A / 230V

Wasserfüllmenge: ca. 1,9 Liter

Schallleistung: 35db(A)

Länge/Breite/Höhe: 1012/216/445mm

Gewicht: 23 kg

3. Funktionsweise

Jeder Fan Coil wird über einen Thermostat angesteuert, bei dem die gewünschte Temperatur eingestellt werden kann. Das Klimagerät am Dach stellt im Sommer Kaltwasser mit 7°/12°C und im Winter Heizwasser mit 45°C zur Verfügung.

Die integrierte Kälteanlage arbeitet nach dem Kompressionsprinzip. Gasförmiges Kältemittel wird aus dem Verdampfer abgesaugt und vom Kompressor verdichtet. Das Heißgas wird im Kondensator verflüssigt. Die Verdampfungswärme und Kompressionswärme wird dabei über einen Ventilator ins Freie abgegeben. Das flüssige Kältemittel strömt danach zum Expansionsventil und verdampft, unter Entzug von Wärme, im Verdampfer. Somit ist der Kältekreis geschlossen.

4. Schalltechnische Maßnahmen

Um eine effiziente Dämpfung zu erzielen, wurde im Außenteil der Kompressor mit schallabsorbierendem Material gedämmt. Der Kompressor selbst ist mit Gummipuffern im Gehäuse fixiert. Um eventuellen Körperschall auszuschließen sind zwischen Gerät und Befestigungsschienen Mafundplatten unterlegt.

5. Kältetechnische Sicherheitseinrichtungen

Die Geräte verfügen über einen Hochdruckschalter, der im Falle eines zu hohen Kältemitteldruckes (z.B. verschmutzter Kondensator) den Kompressor abschaltet, damit dieser keinen Schaden nimmt. Ebenso verhält es sich mit zu wenig Kältemittel. Ein Differenzdruckschalter wasserseitig verhindert ein Anlaufen des Kompressors falls zu wenig Wasser im System ist oder die Pumpe nicht läuft.

6. Elektrische Steuerung

Die Spannungsversorgung erfolgt über eine eigene 400V Anspeisung
Die gesamte Steuerung des Klimagerätes erfolgt über einen elektronischen Regler .


7. Wartungshinweise

Dieses Gerät ist Prüfbuchpflichtig (mehr als 1,5 kg Kältemittel) und ist mindestens einmal jährlich hinsichtlich seiner Betriebssicherheit zu prüfen (§22(1) Kälteanlagenverordnung).

Die Luftansaugfilter der Fan Coils sind in regelmäßigen Abständen zu reinigen und die Kondensatoroberfläche des Kaltwassersatzes mit geeigneten Mitteln zu reinigen (Druckluft, Bürste).

LANDSBERGCHASSR-6

ch. Eisbar. 23.05.06

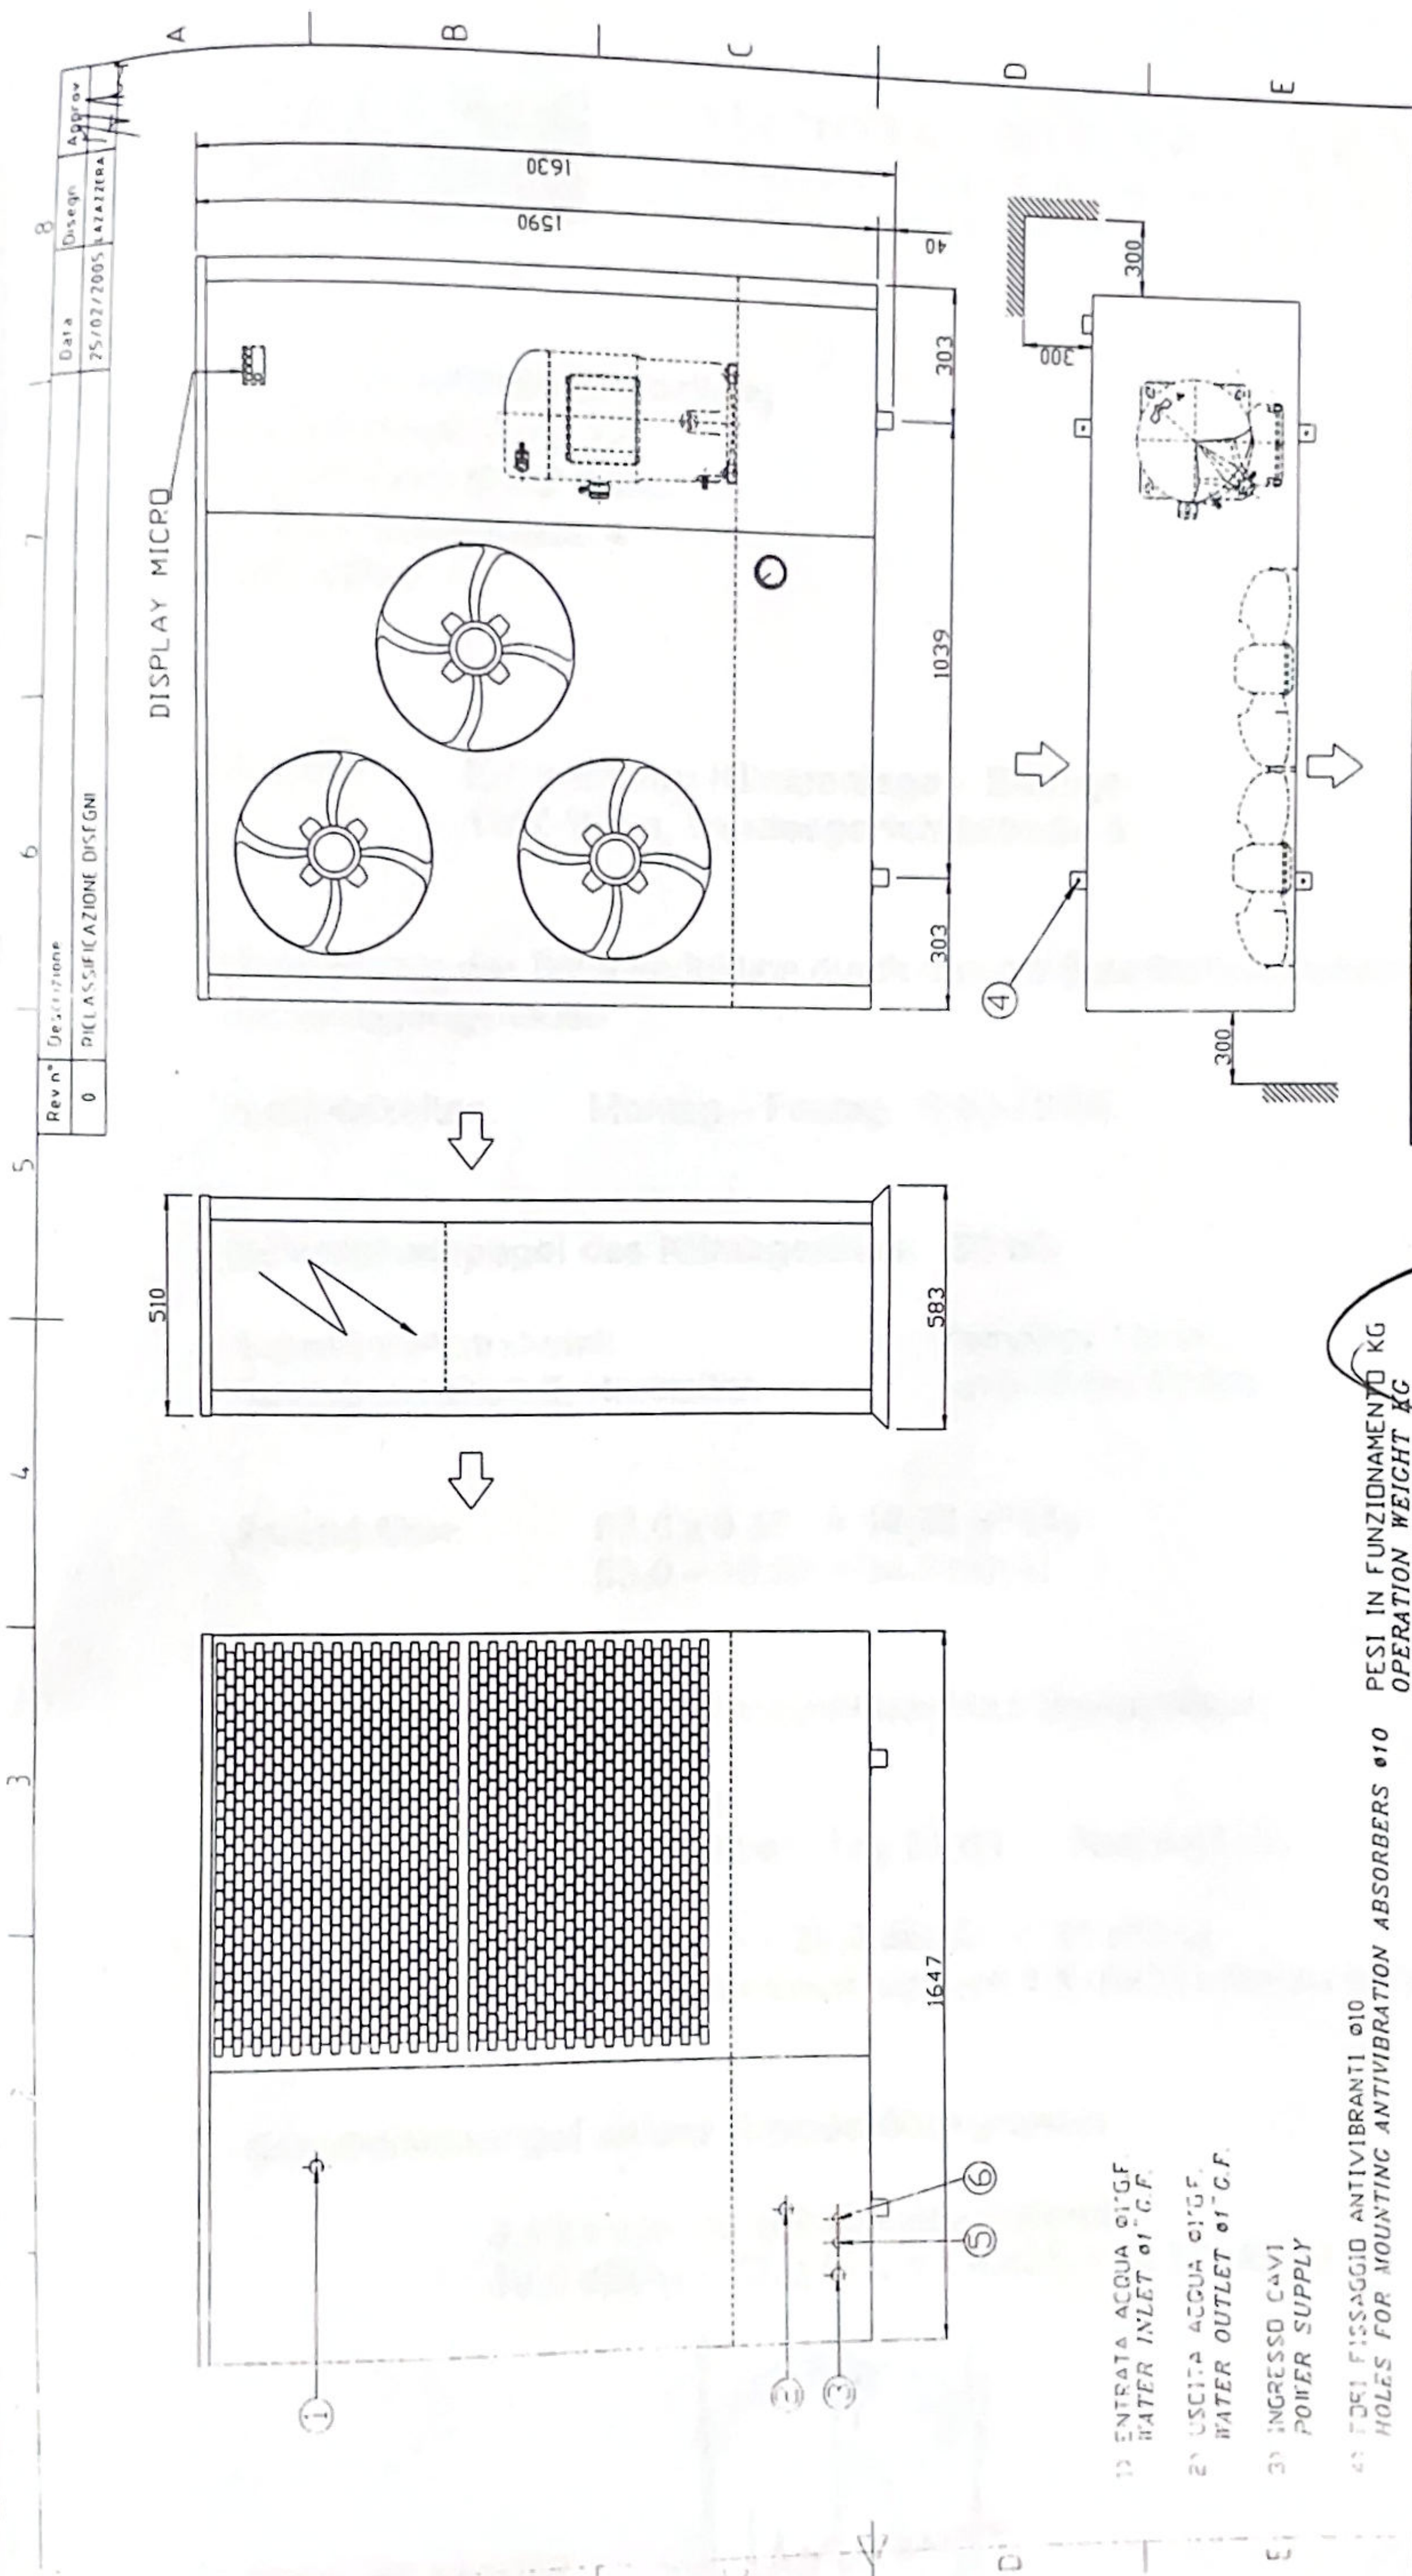

COD.	ME11D131
DISEGNO N.	ME11D131/REV.2
MATERIALE	SPESS SVILUPPO
PESO Kg.	NPEZZI F.TO PAG. A3 1/1
MODELLO - MODEL:	MINIEXCEL 130-138 ZC SE-ZH SE
FILE: ME11D131	SCALA
SOSTITUISCE	SOSTITUITO DA
Disegno di proprietà Thermocold Costruzioni S.r.l. - Diffusione e riproduzione vietate a norma di legge	

PESI IN FUNZIONAMENTO KG
OPERATION WEIGHT KG

MOD.	130ZC	138ZC
KG.	381	401
MOD.	130ZH	138ZH
KG.	391	411



ARCHITEKT DIPL.-ING. ADOLF WOHANKA
STAATLICH BEFUGTER UND BEEIDETER ZIVILTECHNIKER
1060 WIEN, MILLERGASSE 21 TEL. 597 13 68 FAX 596 24 30

Wiener Umweltschutzabteilung
Magistratsabteilung 22
Magistrat der Stadt Wien
1., Ebendorferstraße 4
1082 Wien

**Betreff: Einreichung Klimaanlage – Beilage
1010 Wien, Landesgerichtsstraße 6**

Berechnung der Schallreduktion durch das mit Schallschutzmaterial ausgekleidete Klimanlagengehäuse.

Betriebszeiten: Montag – Freitag 6:00-20:00

Schalldruckpegel des Klimagerätes: 53 dB

Schallschutzmaterial: Armaflex 15mm
Absorptionsmaß lt. Hersteller: $\alpha=0,35$ bei 500Hz

Abstobtion: $53,0 \times 0,35 = 18,55 \text{ dB(A)}$
 $53,0 - 18,55 = 34,5 \text{ dB(A)}$

Schalldruckpegel des schallgedämmten Klimagerätes:

Grenzwert lt. ÖAL-Richtlinie

Kerngebiet: Tag 51 dB, Nacht 41 dB

$34,5 + 5 = 39,5 \text{ dB(A)} < 41 \text{ dB(A)}$

Der Grenzwert wird um 1,5 dB(A) unterschritten.

Schalldruckpegel an der Grundstücksgrenze:

4,43m von der Schallquelle entfernt:

$39,5 \text{ dB(A)} - 10 \lg(4 \times \pi \times 4,43^2) = 22,04 \text{ dB(A)}$

Wien, 03.12.2007







Einlegen

EZ 894

KG Linne Stadt

BEARBEITUNGSBOGEN

FERTIGSTELLUNGSANZEIGE

MA 37/1 - Landesgerichtshof 6/22695-5/2004

Fertigstellungsanzeige zu MA 37/1 - Landesgerichtshof 6/22695-1/2004 (-BBW)

MA 37/1 - Landesgerichtshof 6/22695-6/2004 (-1. PW)

MA 37/

Belege :

	vorgelegt	nachgereicht am:
- Bestätigung des/der Ziviltechnikers/in	☒	☐
- Erklärung des/r Bauführers/in	☐	☐
- Ausführungsplan/pläne ☒ grau ☐ mit Änderungen	☒	☐
- Überprüfungsbeurteilungen des/der Prüfeningenieurs/in	☒	☐
- Konstruktionspläne	☒	☐
- Gutachten über Rauch- und Abgasfänge	☒	☐
- Gutachten über Kanal bzw. Senkgrube mit Ausführungsplan	☐	☐
- Gutachten über sicherheitstechn. Einrichtungen	☐	☐
- Nachweis über den Wärme- u. Schallschutz	☐	☐
- Bestätigung ü. Maßnahmen z. Schutz v. Emissionen	☐	☐
-	☐	☐

Gesetzliche Erfordernisse:

	nicht erford.	erforderl.
- grundbücherliche Durchführung der Abteilung	☒	☐ → ☐ Mitt. an MA 64
- Gehsteigerstellung	☒	☐ → ☐ Mitt. an Gehsteigref.

Fertigstellungsanzeige

☐ Unvollständig belegt - Mitteilung
erfolgt am:

Nachreichung

erfolgte am:

☒ Vollständig belegt am 20.12.2007 (Tag ab dem das Gebäude / die Baulichkeit benutzt werden darf)

☒ Das Bauvorhaben ist daher als abgeschlossen zu beurteilen

→ GWR - Meldung erfolgt

☐ JA

☒ NICHT ERFORDERLICH

→ Kanalplan an MA 14-GDV und MA 30

☐ JA

☒ NICHT ERFORDERLICH

→ Kostenersatz für Gehsteig vorzuschreiben

☒ NEIN

☐ JA → Ä.A.

→ Stellplatzsicherstellung außerhalb des Bauplatzes

☒ NEIN

☐ JA → protokollieren u. Kopie einlegen

☐ 22,00 / 50,00 VA bereits entrichtet

☒ 22,00 / ~~50,00~~ VA mittels eBezahlen vorschreiben / vorgeschrieben am :

Der/Die Sachbearbeiter/innen: Kor.

Für den Abteilungsleiter:

Datum: **01 APR. 2008**



ARCHITEKT DIPL.-ING. ADOLF WOHANKA
STAATLICH BEFUGTER UND BEEIDETER ZIVILTECHNIKER
1060 WIEN, MILLERGASSE 21 TEL. 597 13 68 FAX 596 24 30

An die
Magistrat der Stadt Wien
MA 37 / 1

Dresdner Straße 73-75
1200 Wien

Wien, 18.02.2007

BESTÄTIGUNG

Betreff: 1100 Wien, Landesgerichtsstraße 6

Die mit Bescheid der MA 37/1 – Landesgerichtsstraße 6 / 22695-1 / 2004 am 5. Oktober 2004 ^{T.1.P.W.} genehmigte Bauführung ist sowohl plangemäß als auch den Bestimmungen der Bauordnung für Wien und den Bauvorschriften entsprechend fertiggestellt.

Es wurde die Ausgleichsabgabe für den erforderlichen Pflichtstellplatz entrichtet.

Alle erforderlichen Unterlagen befinden sich im Bauakt. *und sind vollständig*

Wien, am 18. Februar 2007



ARCHITEKT DIPL.-ING. ADOLF WOHANKA
STAATLICH BEFUGTER UND BEEIDETER ZIVILTECHNIKER
1060 WIEN, MILLERGASSE 21 TEL. 597 13 68 FAX 596 24 30

An den
Magistrat der Stadt Wien
MA 37 / Baupolizei für den 1. Bezirk

Dresdnerstraße 73 -75
1200 Wien

Betrifft: 1010 Wien, Landesgerichtsstraße 6

Aufgrund einer Anzeige wurde die derzeit fertige Stahlkonstruktion für den Dachausbau auf obiger Liegenschaft nachgemessen.

Es haben sich gegenüber der Einreichung keinerlei Differenzen im Bezug auf die im Einreichplan angegebenen Höhen betreffend Traufenhöhe und Dachhöhe ergeben.

Mit der Bitte um Kenntnisnahme.



GUTACHTLICHE FESTSTELLUNG

Technische Ausführung stimmt mit Gutachten überein

Weiterer Nachtrag ist nicht erforderlich

Unterzeichnet und Stempel
des Sachbearbeiters

Unterzeichnet und Stempel
des Sachbearbeiters

Wien, am 27. September 2005

Beschau gemäß §§125 Abs.2 und
127 Abs.3 der Bauordnung für Wien

B E F U N D

BODEN beschau GZZT 2009/33

für die Baubewilligung vom

Zi.MA genehmigte Bauführung.

Datum

Baustellenadresse LANDESGERICHTSTR. 6; 1010 WIEN

Anwesende: Bevollmächtigter des ZT Büros D. H. T. JARVICK

Bauführer

vertreten durch:

Gegenstand der Beschau (Bauteile usw.): BODEN BESCHAU

Vorliegende Konstruktionspläne: LT. PROBESCHÄNTE LEHMIGE BODEN

Abweichungen vom bewilligten Bauplan (Einreichplan):

Abweichungen in der technischen Ausführung:


GUTACHTLICHE FESTSTELLUNG

Technische Ausführung plan- und fachgemäß: ja ☒ O nein ☐ O

Mängel:

Weiterarbeit wird – nicht – unter folgenden Bedingungen – gestattet:

Unterschrift und Stempel
des Bauführers

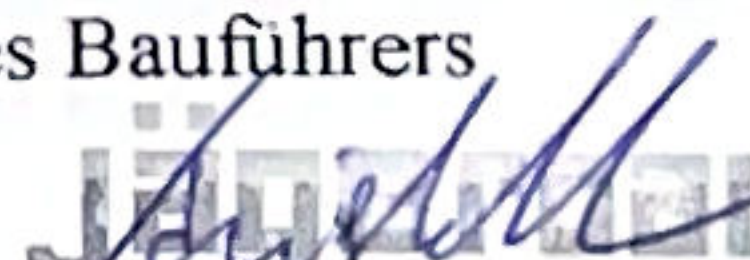
JÄGER GESELLSCHAFT m.b.H.
LEHRBACHGASSE 4
1120 WIEN, Tel. 0222/813 46 72-0
BAULEITUNG

Unterschrift und Rundsiegel
des Ziviltechnikers




Mit dieser Unterschrift bestätigt der Bauführer auch, dass die dem Befund zugrunde liegenden Baupläne ident sind mit denen, die bei der Baubehörde aufliegen.