



LAGEPLAN 1 : 250

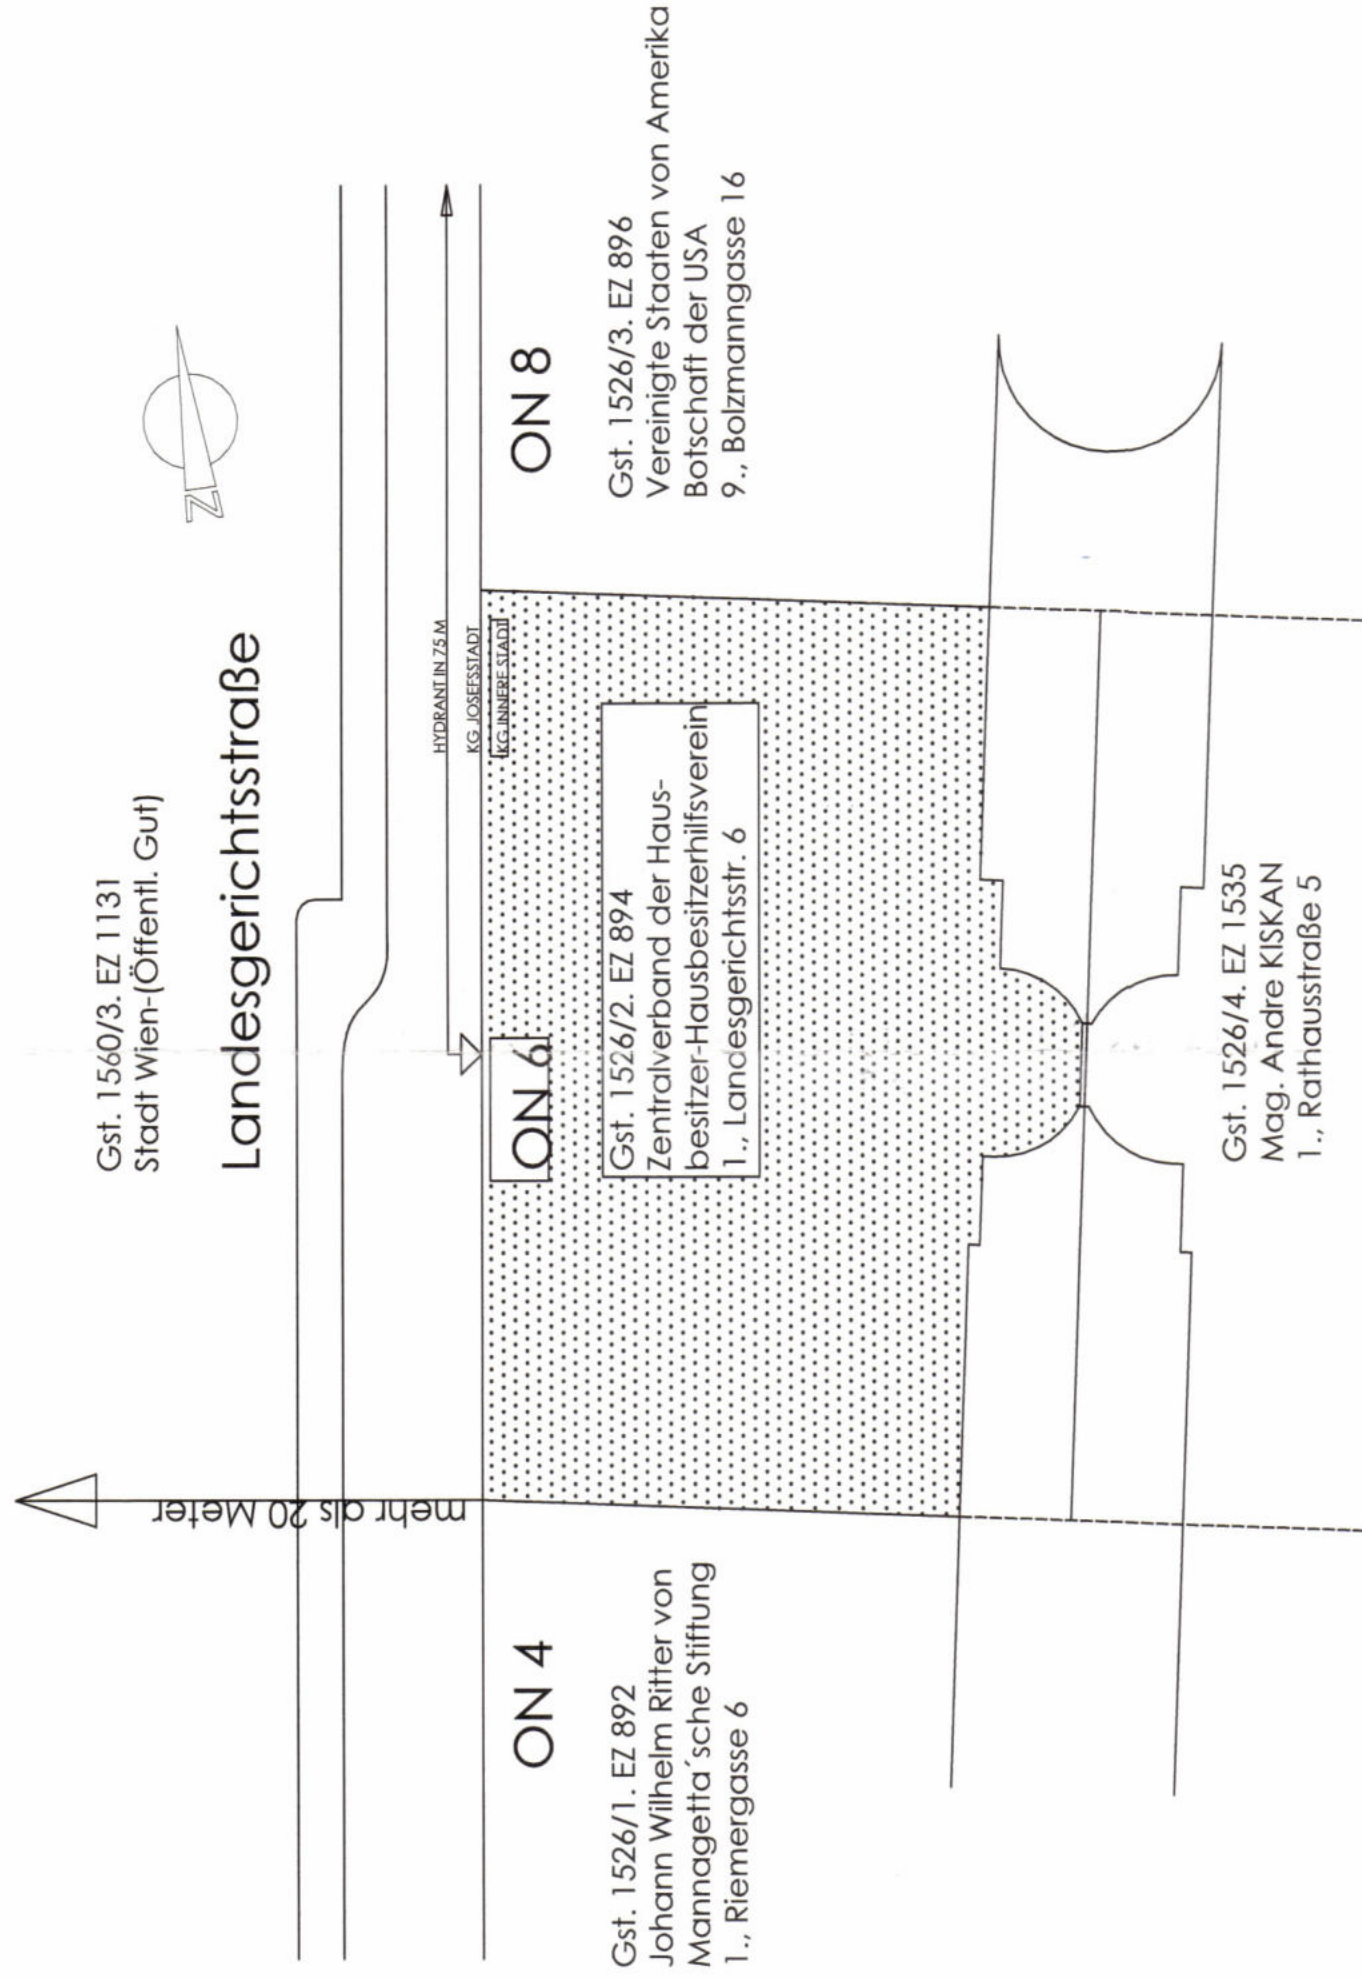


STRASSENANSICHT

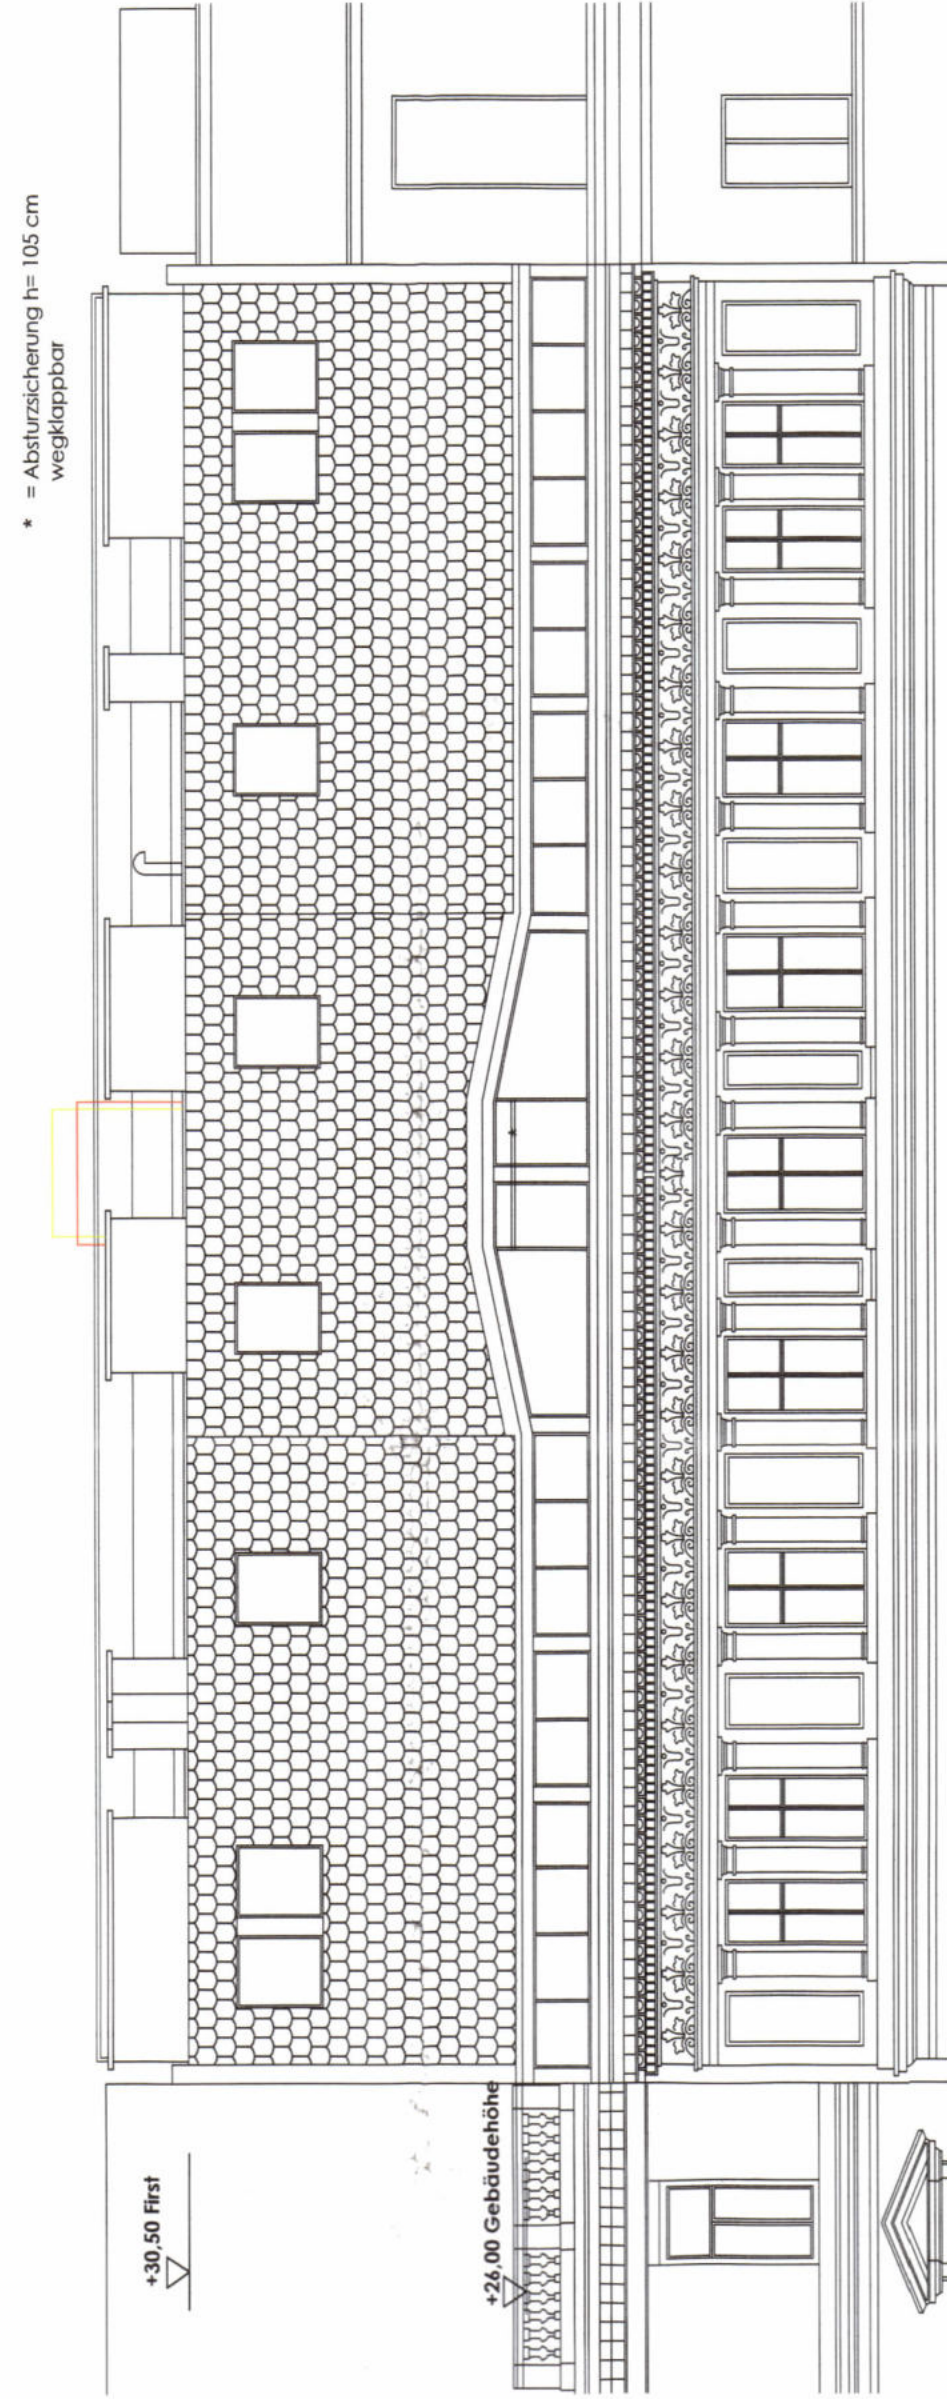


DIE ERRICHTUNG UND DER BETRIEB DER KLIMA/HEIZANLAGE (WELCHE NUMMER AUSGETAUSCHT WERDEN SOLL) WURDE MIT BESCHIED MA 37/1-ANLAGEGERICHTSSTRASSE 6/37447-1/2007 AM 14. JANUAR 2008 BAUBEHÖRDE GENEHMIGT

DACHDRAUFSICHT

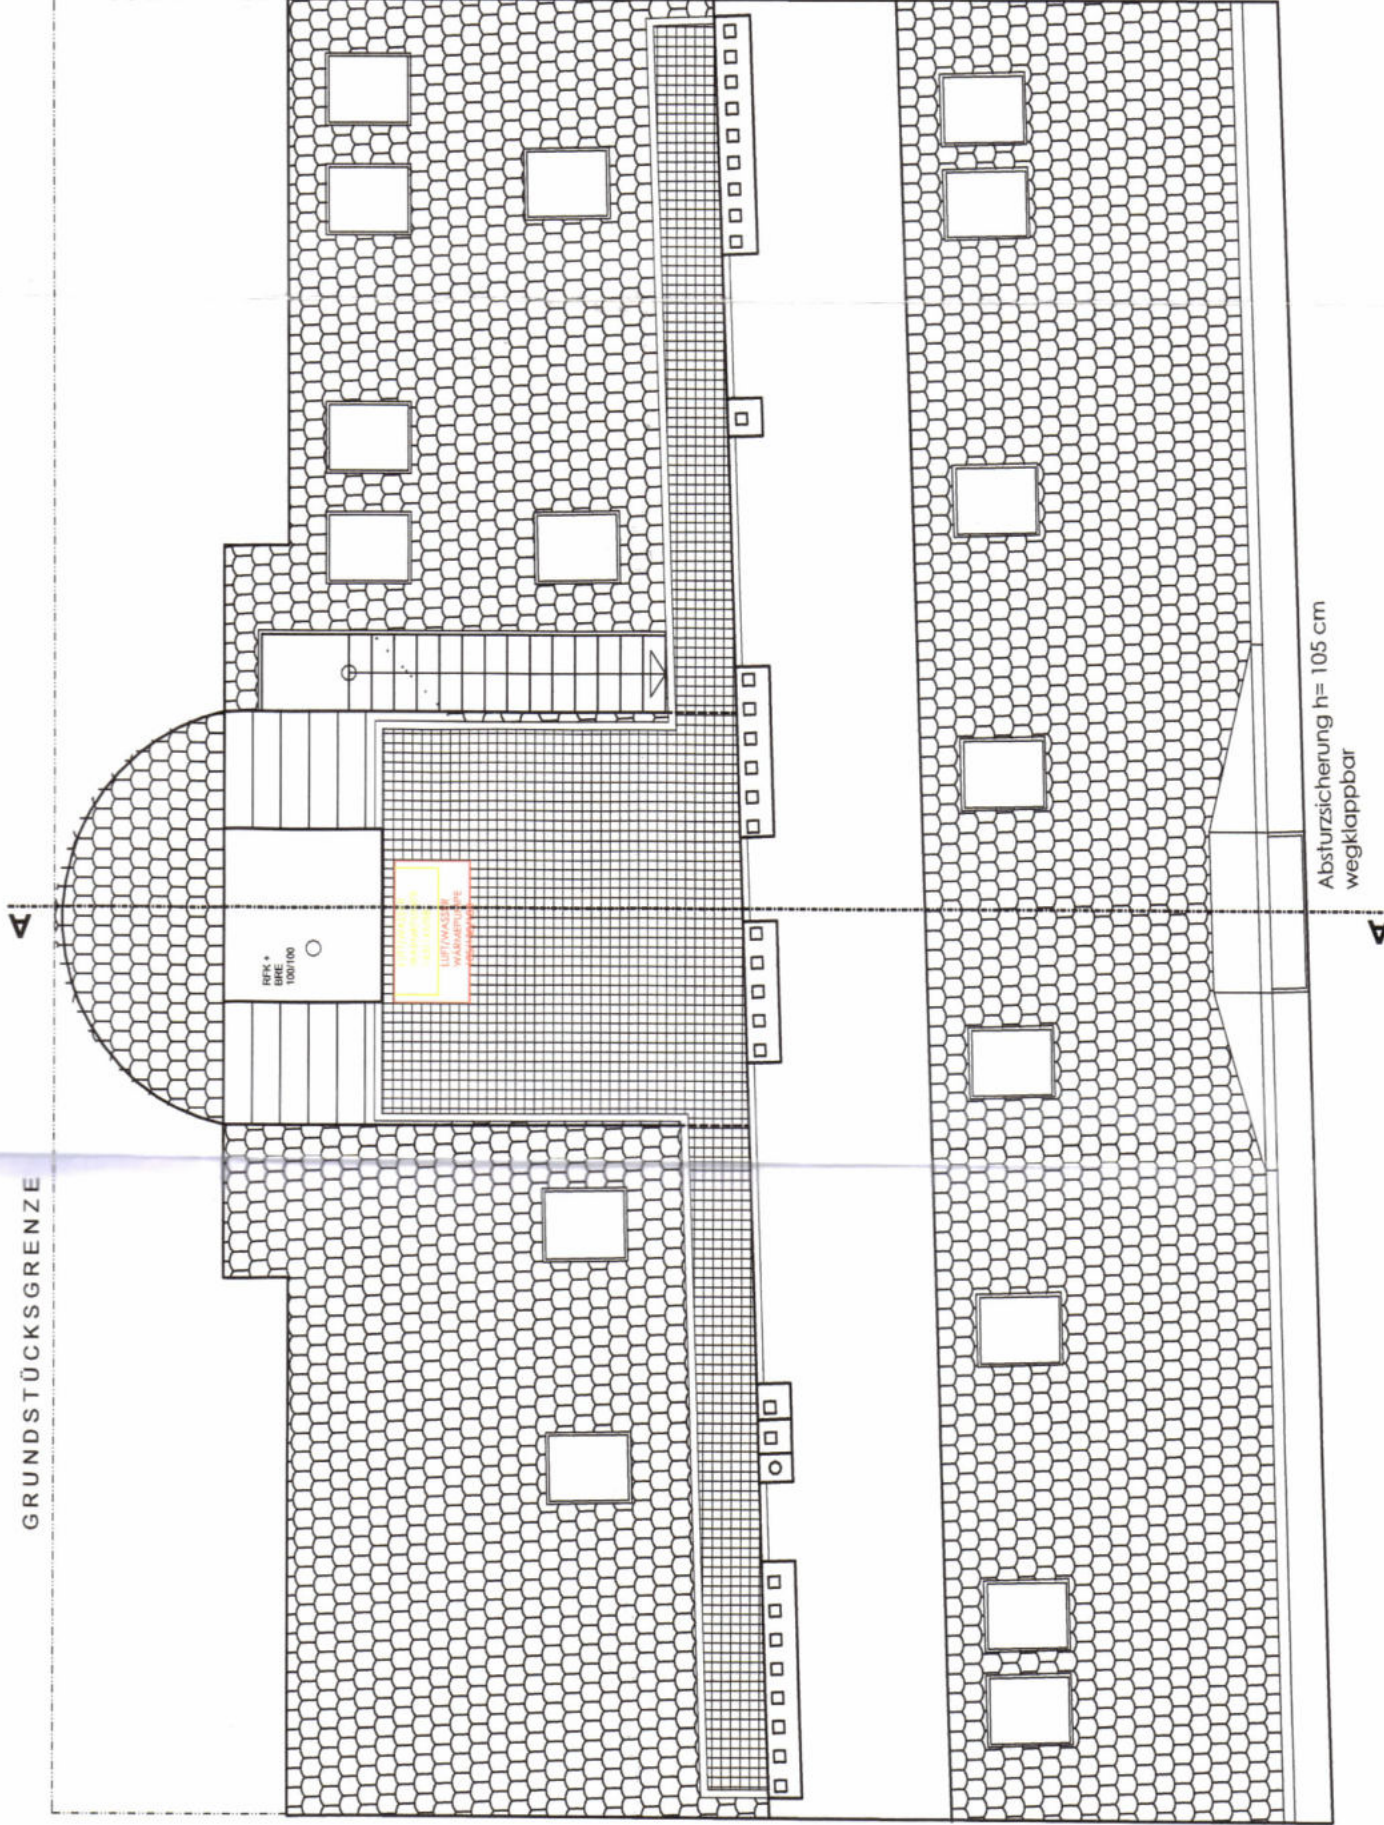

HOFANSICHT

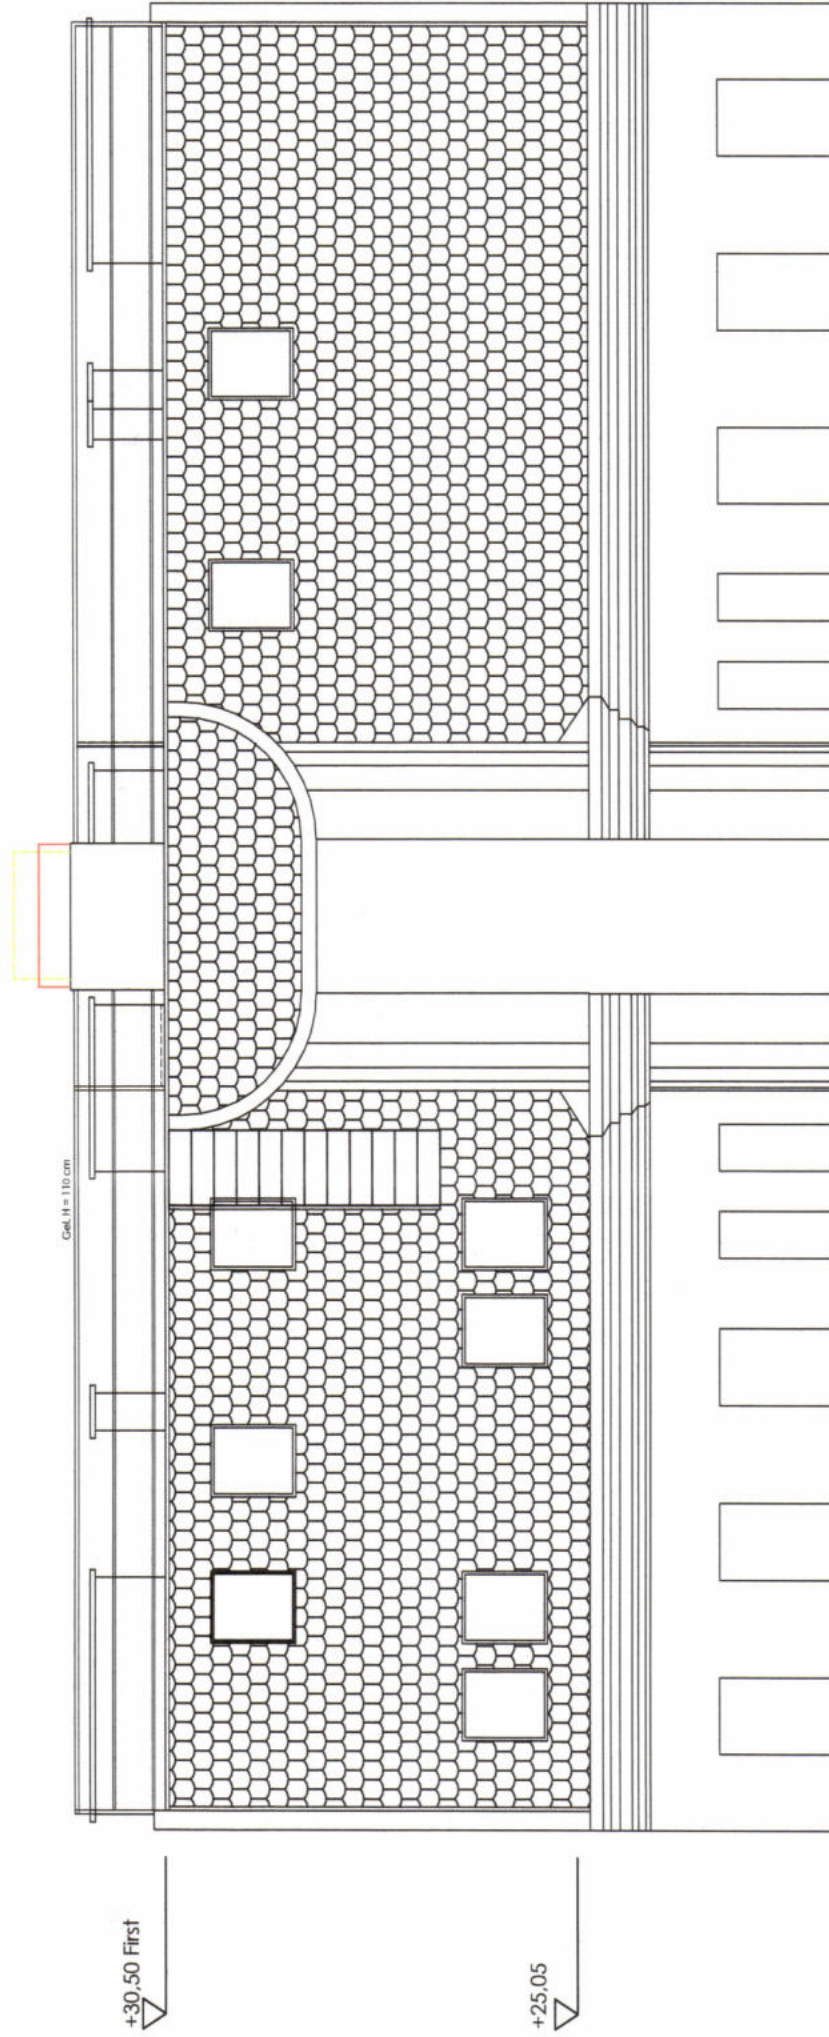

PARIE A B C D E

EINREICHPLAN

GRUNDRISS, SCHNITT, ANSICHTEN, LAGEPLAN

BAUVORHABEN
AUSTAUSCH EINER KLIMA/HEIZANLAGE
AM DACH DES HAUSES
1010 WIEN, LANDESGERICHTSSTRASSE 6

EZ. 894 **GST.NR. 1526/2** **KAT. GEM. INNERE STADT**

BAUWERBER UND GRUNDEIGENTÜMER
ZENTRALVERBAND DER HAUSBESITZER
HAUSBESITZERHILFSVEREIN
LANDESGERICHTSSTRASSE 6
1010 WIEN

BEHÖRDE
Magistrat der Stadt Wien
Magistratsabteilung 37 - Baupolizei
Gebietsgruppe Ost, Stadterneuerung 1
ZL: MA37/19181-2015-1
Hierauf bezieht sich der Bescheid

PLANVERFASSER
D. I. ANDRZEJ GLOGOWSKI
OTHELLOGASSE 17/19
A-1200 WIEN
TEL: 01 415 39 03
MAIL: at.glogowski@nied.at

BAUFÜHRER
K.B. Krieger- und Sauerwaldt
Architekturbüro
2744 LEDERDOIT

DATUM 26.02.2015 PLANNR. 0,51 M2 GZ. 2014/043