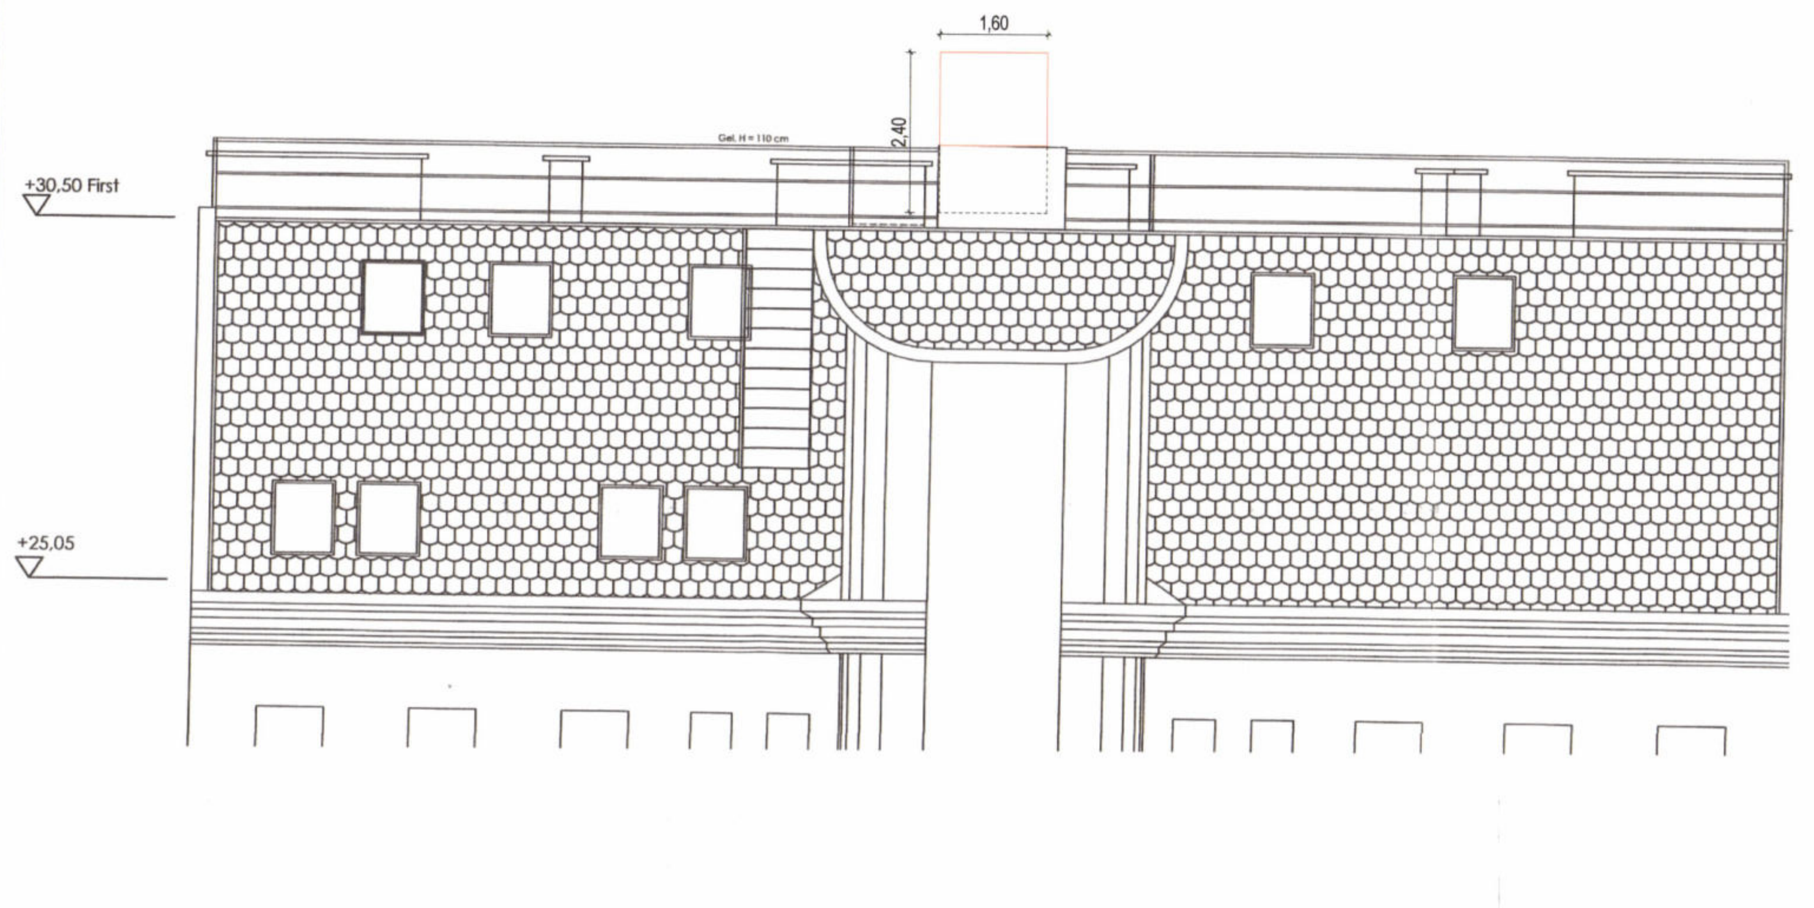

Hofansicht

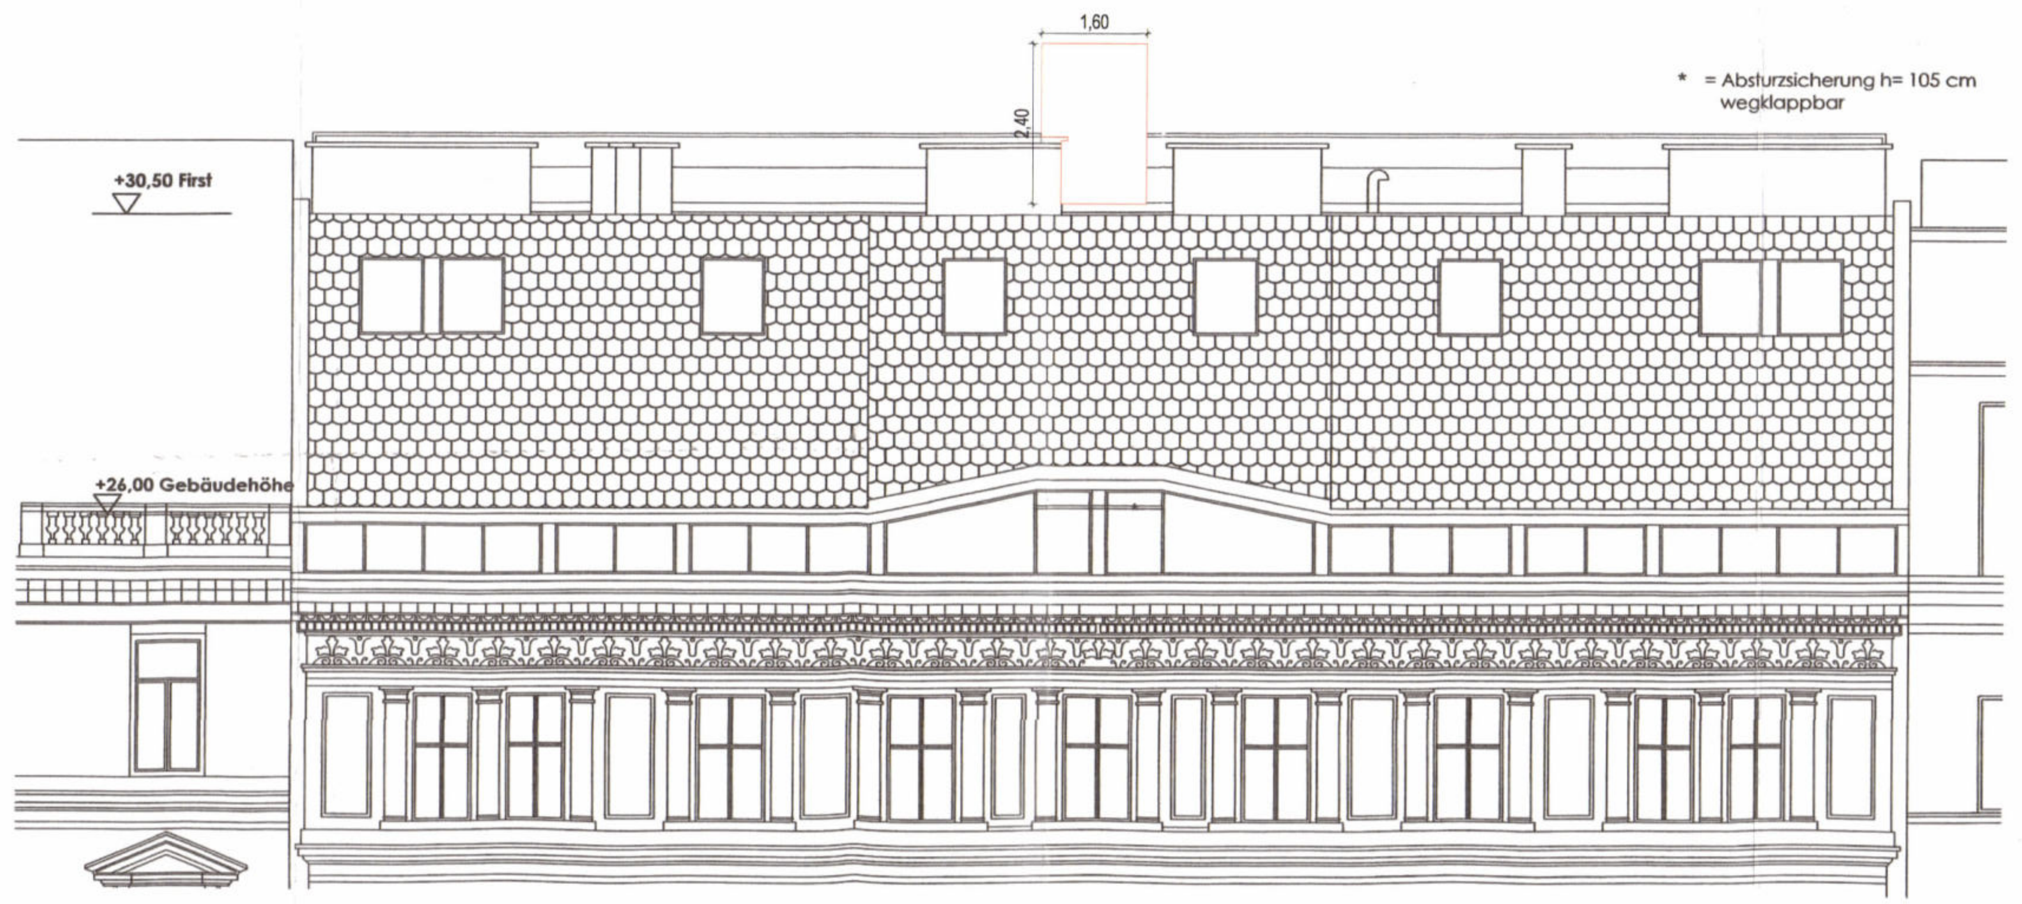

Strassenansicht

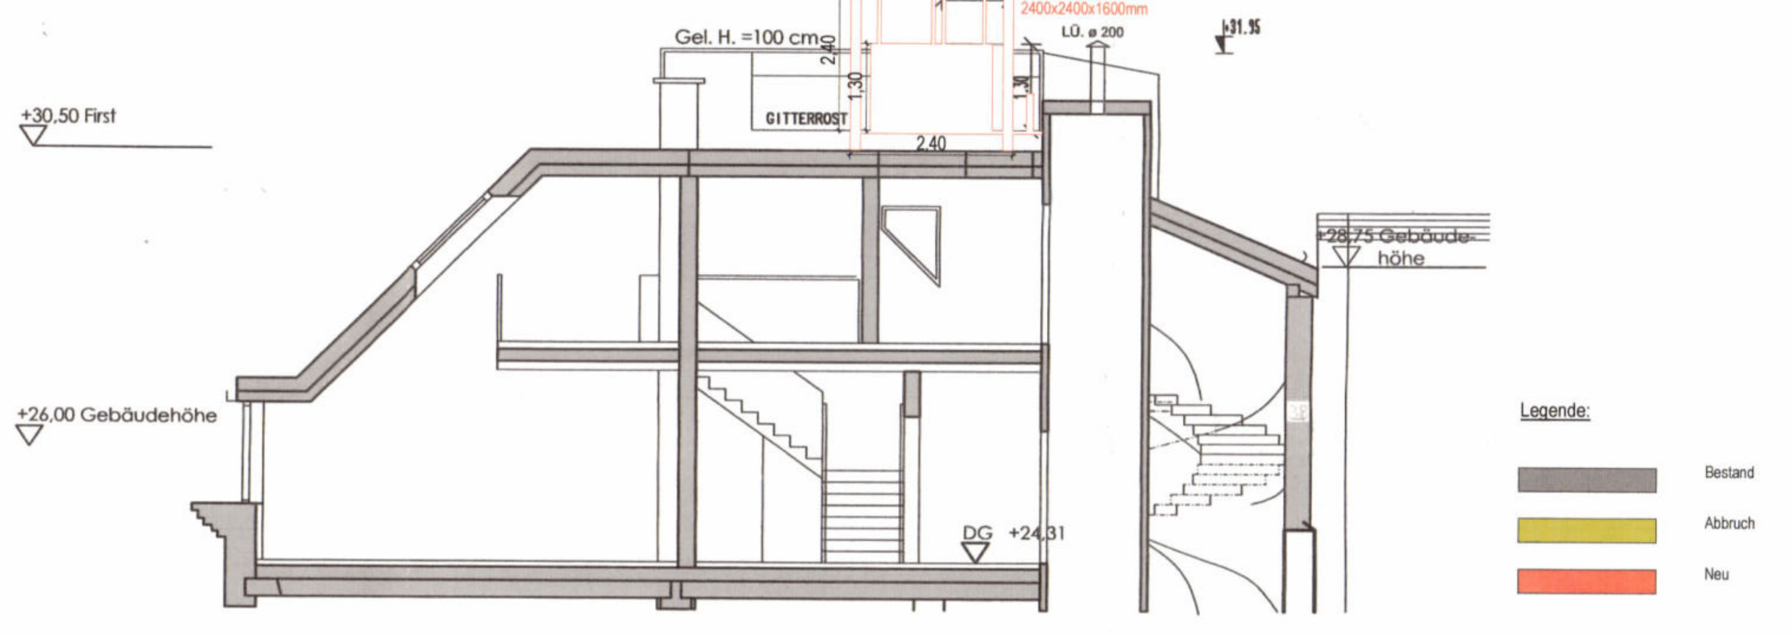

Schnitt A-A

Legende:

- Bestand
- Abbruch
- Neu

Sonderschalldammgehäuse - Super Quiet SonaSafe Schallschutzgehäuse für den Einbau von Kälte-, Klima-, und Wärmepumpen-Außengeräten mit horizontaler Luftansaugung und vertikaler Luftausblasung mit insgesamt 2 Lüfter. Gehäuse-Abmessungen (HXBXT): 2400x2400x1600mm Gewicht: ca.750 kg. Ausführung: Außenflächen aus Pulverbeschichtetes RAL9010 (Reinweiß) und verzinktes Stahlblech, Innenflächen aus Lochblech mit 50x50x10mm Lochung in verzinkter Ausführung. Nominale Schlaldämmleistung: >20 dB, mit Sonderrohrschalldämpfer inkl. Anschlußkanal mit Druckverlust ca. 8 Pa bei Luftdruchfluss 4,4 m³/s. inkl. Zubehör: Gummistreifen unterhalb der Rahmen und Schalldämmmatte flächendeckend unterhald der Wärmepumpe.

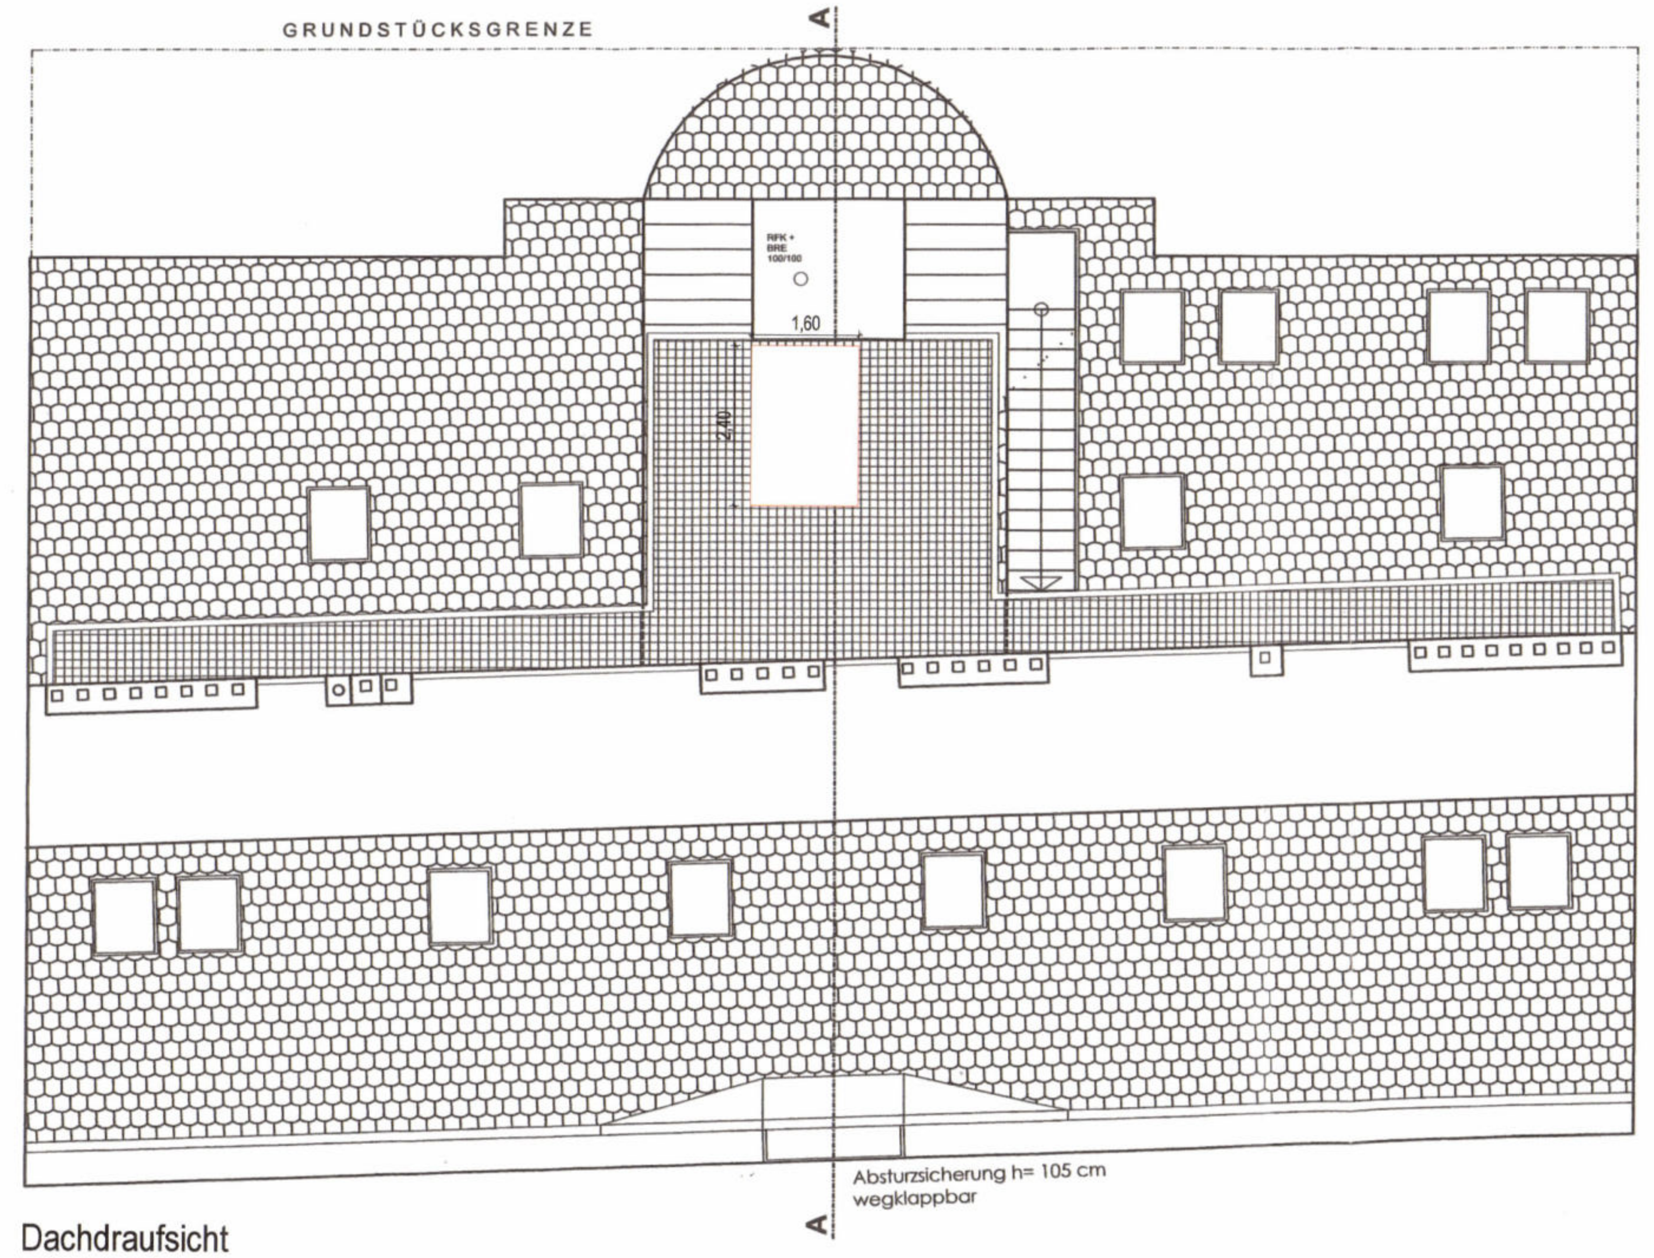

Dachdraufsicht

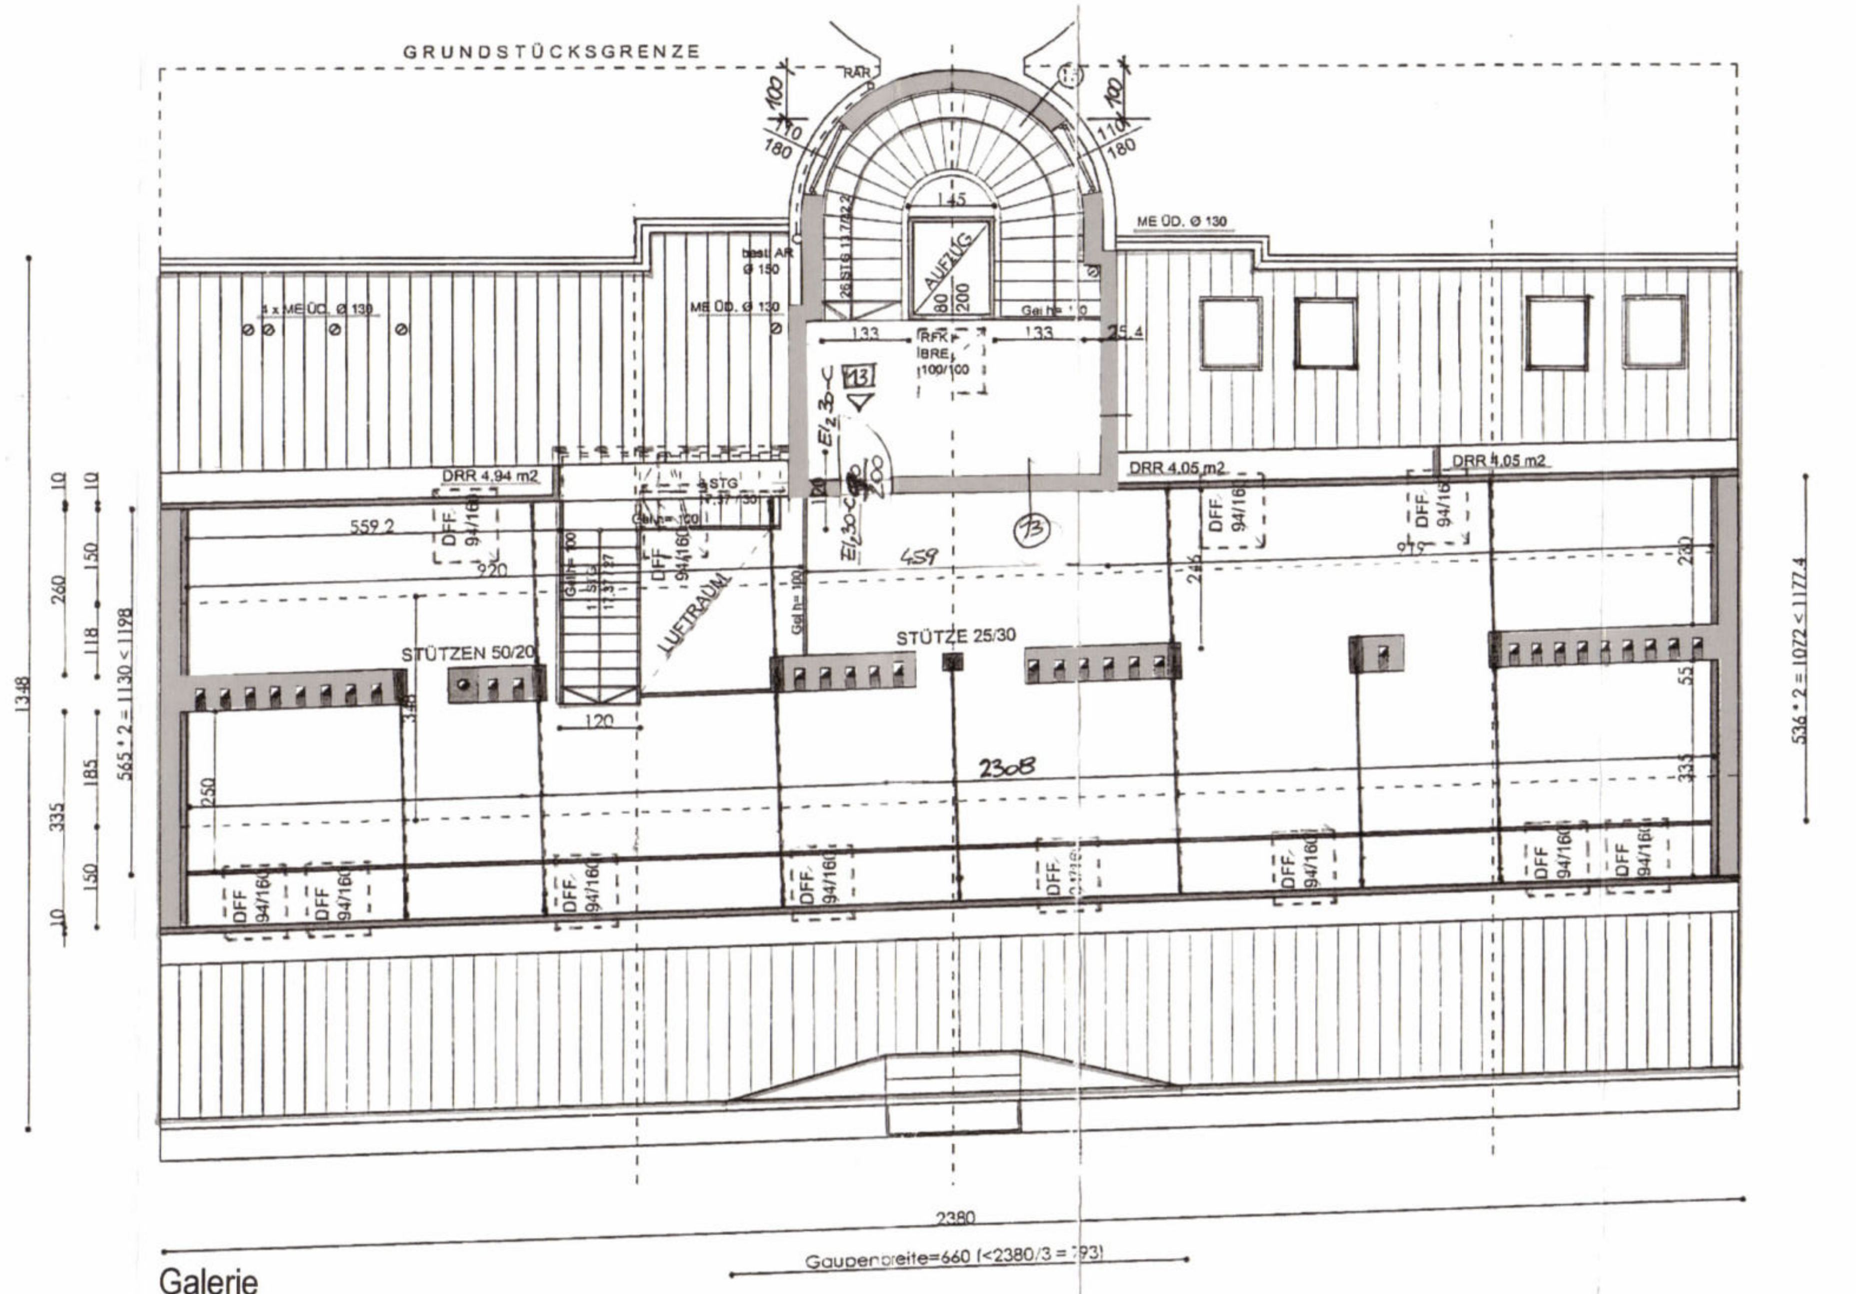

Galerie

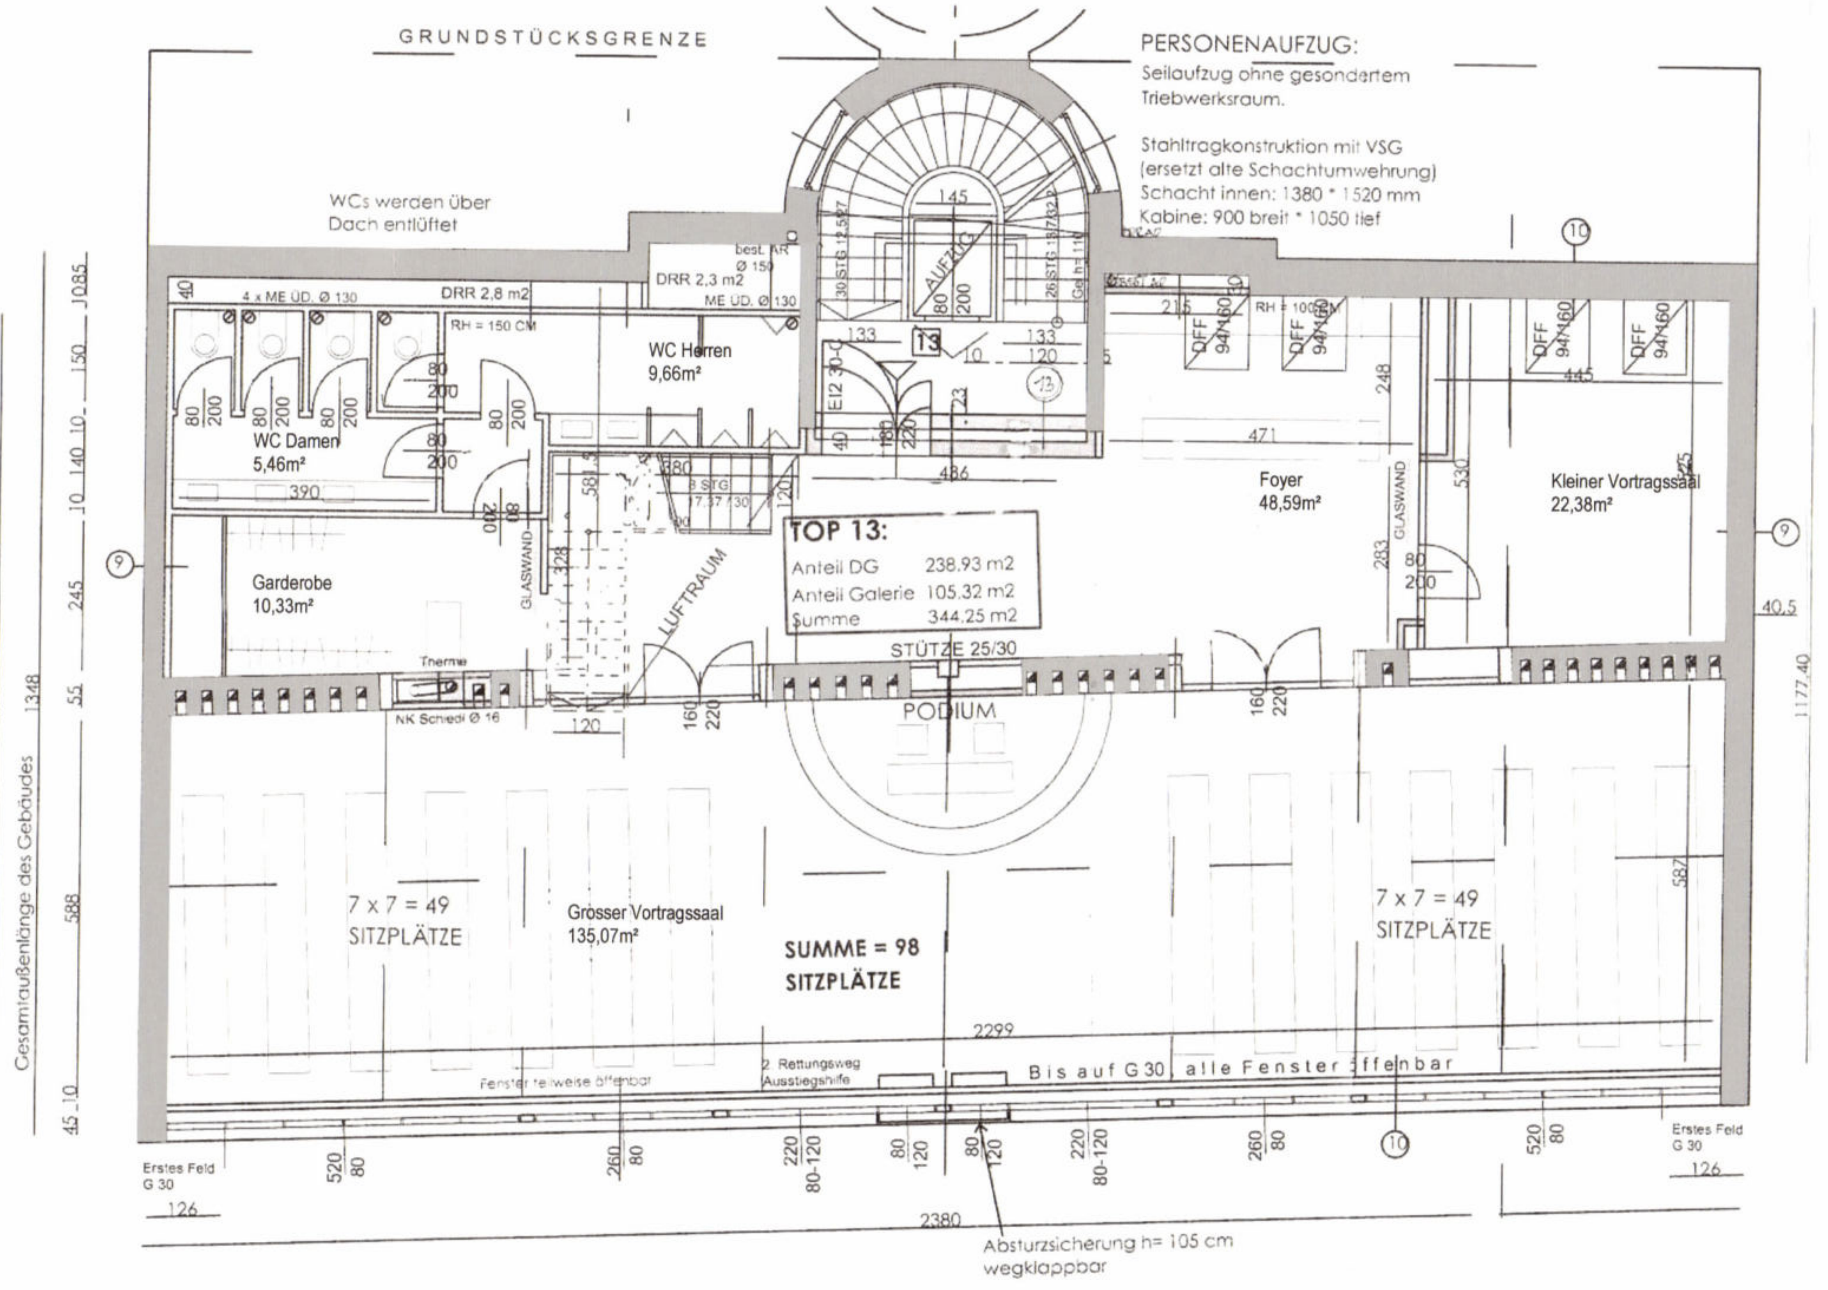

Dachgeschoß

	Schalldämmung [dB(A)] Sonderschalldämmgehäuse SQV_MAXA HWA-A 0133H	HWA-A 0133H	Bewertung HWA-A 0133H mit SQV_MAXA HWA-A 0133H
Schalldruckpegel in ein bestimmte Richtung auf 1m	-20,0 dB(A)	62,9 dB(A)	42,9 dB(A)

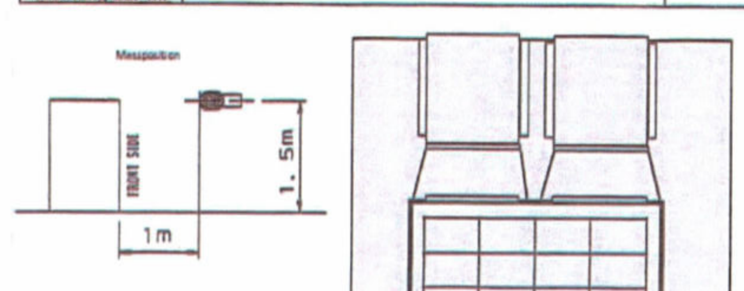

Entfernung	Schalldruckpegelabnahme*	mit zahlreichen Schallreflexionen der Wände **
R = 2m	37,9 dB(A)	39,9 dB(A)
R = 3m	35,0 dB(A)	38,1 dB(A)
R = 4m	32,9 dB(A)	36,9 dB(A)
R = 5m	31,3 dB(A)	35,9 dB(A)
R=8m	27,9 dB(A)	33,9 dB(A)
R=10m	26,3 dB(A)	32,9 dB(A)

Einreichplan

EZ: 894 GST.NR.: 1526/2, KG: 01004 Innere Stadt

Objekt / Ansuchen um:
Errichtung Schallschutzhaube

Landesgerichtsstr.6
1010 Wien

Planinhalt
Grundriss DG und DD
Grundriss Galerie
Schnitt, Ansichten
Lageplan

Plannummer
P0420-LAN- EP- 002- A

Parie
A / B / C / D

Maßstab
1:100

Datum
01.08.2017

Plangröße
107 cm x 38 cm

Magistratsabteilung 19
Zahl 650990/2017
EING. 09. Aug. 2017
AUSGANG

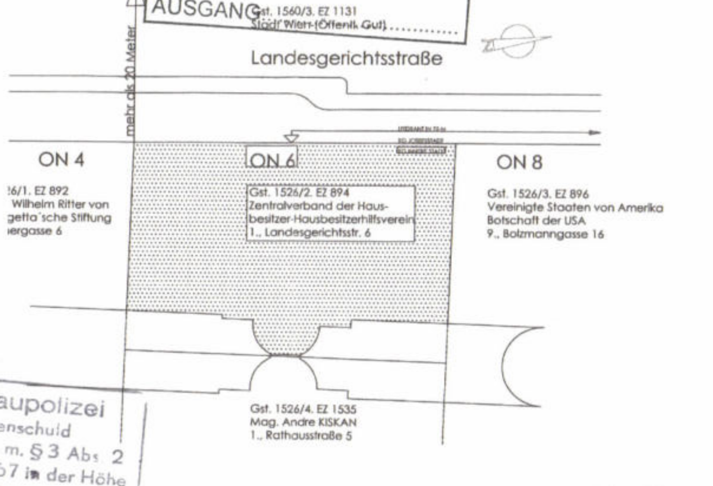

MA 37 – Baupolizei
Die Gebührenschuld gem. § 4 iVm § 3 Abs. 2 Gebührengesetz 1957 in der Höhe von EUR 7,80 wurde
entrichtet
bekanntgegeben, siehe Akt
Wien, 28. Aug. 2017
U.:

Bauwerber/in

Zentralverband der Hausbesitzer
Hausbesitzerhilfsverein
1010 Wien, Landesgerichtsstraße 6
Tel. 01/406 33 18 Fax 01/406 53 49
ZVR 187843163 ATU 59082708

Grundstückseigentümer/in

Zentralverband der Hausbesitzer
Hausbesitzerhilfsverein
1010 Wien, Landesgerichtsstraße 6
Tel. 01/406 33 18 Fax 01/406 53 49
ZVR 187843163 ATU 59082708

Bauführer/in

KTB Klima und Sonnenschutztechnik GmbH
A-1230 Wien, Lemböckgasse 47
Tel: 02259 / 2101, Fax: 02259 / 2101-440
E-Mail: office@ktbklima.at

Magistrat der Stadt Wien
Baubehörde
Magistratsabteilung 37 - Baupolizei
Gebietsgruppe Ost, Stadterneuerung 1
Zl.: MA37/650990-2017-1
Hierauf bezieht sich der Bescheid
Wien, 28.8.2017
Für den Abteilungsleiter:
Dipl.-Ing. Fischer
Oberstadtbaurat

MA37 BAUPOLIZEI SICHER BAUEN
StadtWien

Planverfasser/in

baukult ... der stoff aus dem realitäten sind!

baukult ZT GmbH
Architektin DI Regina M. Leitner
1070 wien . halbgasse 3-5 / stg. 2
fn 459264p . tel + 43 1 9247867 10
www.baukult.at . www.parifizieren.at