

Einreichplan

EZ: 894 GST.NR.: 1526/2, KG: 01004 Innere Stadt

Objekt / Ansuchen um:

bauliche Änderungen

Landesgerichtsstr.6
1010 Wien

Planinhalt

Lageplan

Grundrisse KG, TP,
HP, 1.Stock, 2.Stock,
3.Stock, DG, Galerie

Plannummer

P0420-LAN-EP-001-A

Parie

A / B / C / D

Maßstab


1:100

Datum

15.03.2018

Plangröße

155 cm x 43 cm

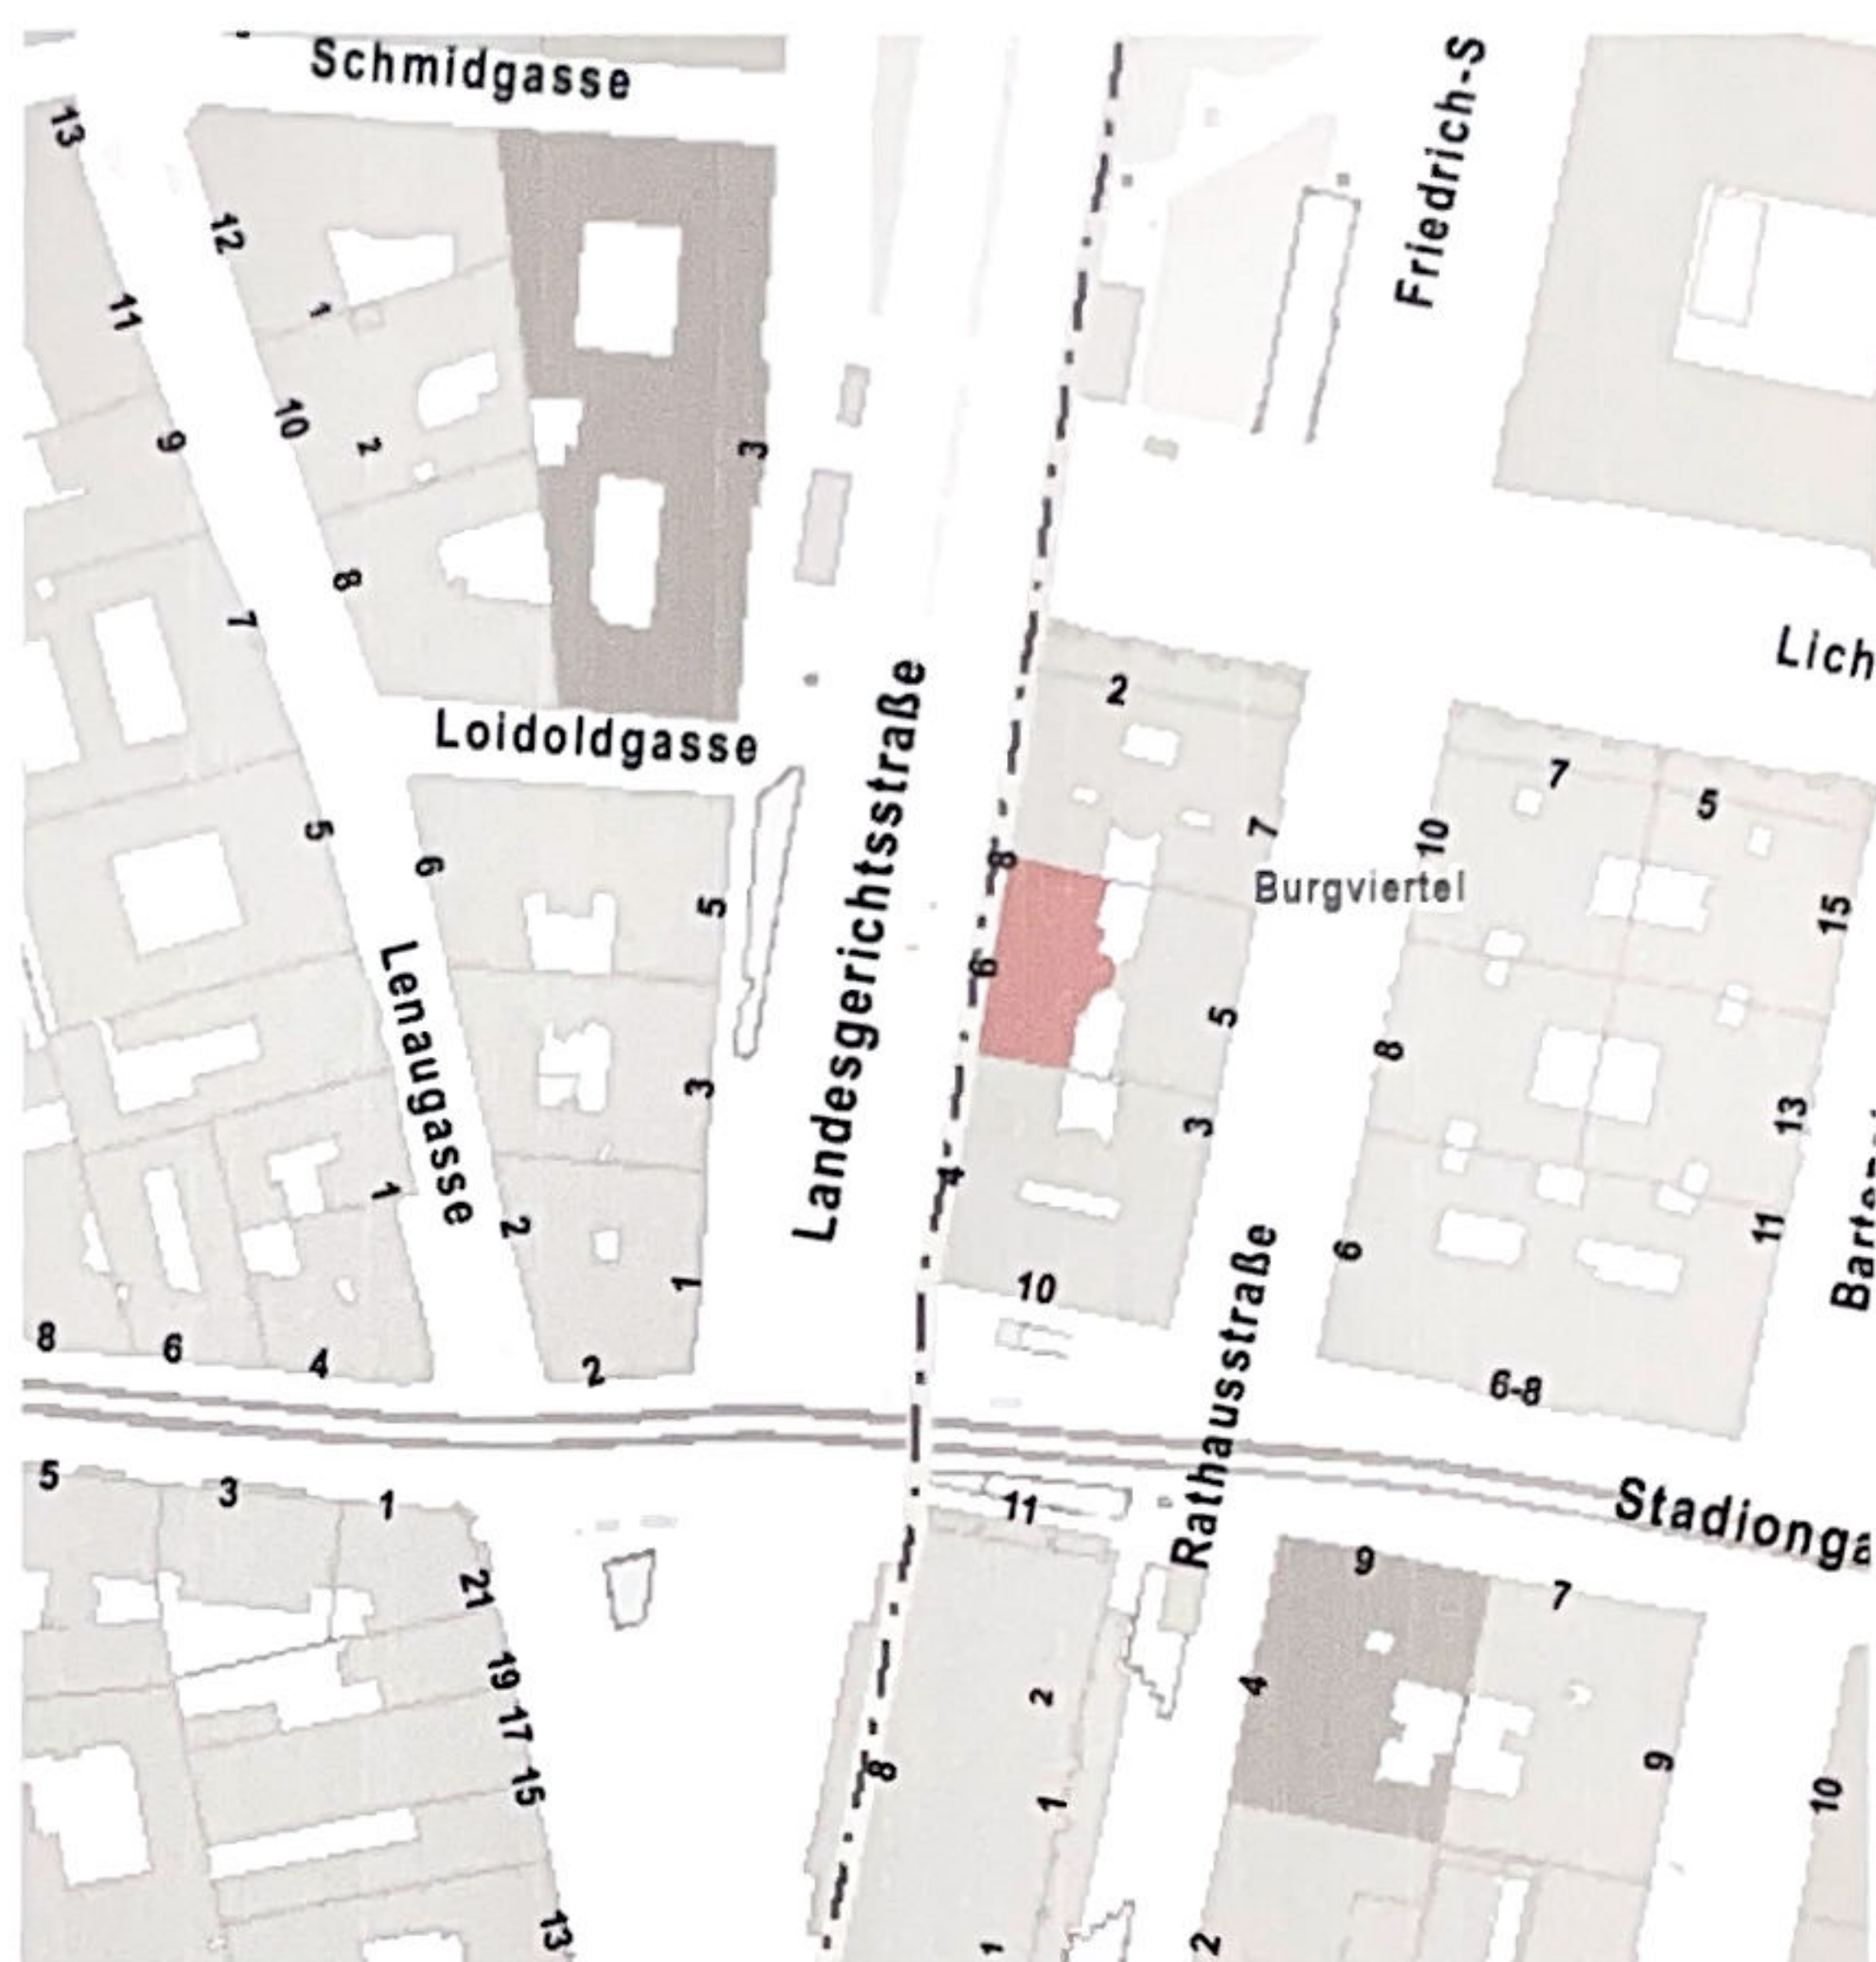

N
Lageplan

Bauwerber/in

Zentralverband der Hausbesitzer
Hausbesitzerhilfsverein
1010 Wien, Landesgerichtsstraße 6
Tel. 01/406 33 18 Fax 01/406 53 49
ZVR 187843163 ATU 59082708

Grundstückseigentümer/in

Zentralverband der Hausbesitzer
Hausbesitzerhilfsverein
1010 Wien, Landesgerichtsstraße 6
Tel. 01/406 33 18 Fax 01/406 53 49
ZVR 187843163 ATU 59082708

Bauführer/in

B & C Baubetriebs GmbH

BAUMEISTER

A - 1110 Wien, Fuchsbodengasse 7
Telefon: 01/767 68 07 Fax DW 10
office@bc-bau.at www.bc-bau.at
FN 276814 d. NG Wien, AT 187843163

Bimoba Hoch und Tiefbau
Handels Ges.m.b.H

1170 Wien, Kärntnerberggasse 12/2
office@bimoba.at Tel./Fax: 01/406 64 79
www.bimoba.at

Planverfasser/in

Bauverwaltung der Stadt Wien

Magistratsabteilung 37 - Baupolizei
Gebietsgruppe Ost, Stadterneuerung 1

Zl.: MA37/438141-2018-1

Dieses Bauvorhaben gilt als gem. § 70 BO bewilligt.

MA37
BAUPOLIZEI
SICHER BAUEN

Stadt Wien

Für den Abteilungsleiter:

Dipl.-Ing. Fischer
Oberstadtbaurat

Wien, 15.6.2018

baukult ZT GmbH
Architektin Dipl. Regina M. Lettner
1070 wien, halbgasse 3-5 / stg. 2
fn 459264p tel + 43 1 9247867 10
www.baukult.at www.parifizieren.at

baukult

... der stoff aus dem realitäten sind!

BAUINSPEKTION - BEARBEITUNGSBOGEN (§ 62 BO)

MA 3711-438141-2018-3

Adresse: 1, LANDESGERICHTSSTRASSE

ONr. 6

AV - Baubeginn:

- ☒ Bauführer bekanntgegeben
☒ baurechtl. GF erforderlich und benannt
☐ Prüfenieur erforderlich und bekanntgegeben

- ☐ Mitteilung am: _____
☐ Mitteilung am: _____
☐ Mitteilung am: _____

Baubeginn am: 04.06.2018

Spätestmög. Bauvollendung 04.06.2018

- ☒ Erhebung vor Ort nicht erforderlich (wegen Geringfügigkeit, Unbedenklichkeit, etc.)
☐ Ortserhebung am: _____

- ☐ Baupläne liegen auf _____ ☐ Statik erforderlich und liegt auf _____
☐ Überprüfungsnachweise erforderlich und liegen auf _____

Anmerkung/Maßnahme (z.B. Baueinstellung/Kontaktaufnahme): _____

[Signature]

Sachbearbeiter/in

[Signature]

Leiter/in

☒ *[Signature]*

Einlegen: Überwachungsarchiv

AV - Fertigstellung:

- ☒ Fertigstellungsmeldung und BF-Bestätigung erforderlich (Bauvorhaben gem. Abs. 1 Ziff. 1, 2 oder 3)
☒ Fertigstellungsanzeige und BF-Bestätigung erforderlich (Bauvorhaben gem. Abs. 1 Ziff. 4 ohne Prüfenieur)
☐ Fertigstellungsanzeige und ZT-Bestätigung erforderlich (Bauvorhaben gem. Abs. 1 Ziff. 4 mit Prüfenieur)

- ☐ eingebrachte Fertigstellungsmeldung bzw. -anzeige unvollständig belegt:

Mitteilung erfolgt am: _____

Frist: _____

☐ Einlegen: Überwachungsarchiv

- ☒ eingebrachte Fertigstellungsmeldung bzw. -anzeige vollständig belegt:

24.09.2018

Datum

VA mittels eBezahlen vorschreiben

☒ 22,00 Euro

☐ 50,00 Euro

Der/Die Sachbearbeiter/in:

08.09.2018

Für den Abteilungsleiter:

Datum:

26. SEP. 2018

Datum:

[Signature]

Überwachung abgeschlossen - Einlegen:

EZ 894

KG INNERE STAAT

EZ

29

Einlegen

EZ

894

KG

Innere Stadt

BEARBEITUNGSBOGEN

FERTIGSTELLUNGSANZEIGE

MA 37/ 1 - LANDESGERICHTSSTRASSE 6 / 650.990 - 2017 - 1

Fertigstellungsanzeige MA 37/ 1 - 650.990 - 2017 - 9

Belege :

	vorgelegt	nachgereicht am:
- Bestätigung des/der Ziviltechnikers/in	☐	☐
- Erklärung des/r Bauführers/in	☒	☐
- Ausführungsplan/pläne ☐ grau ☐ mit Änderungen	☐	☐
- Überprüfungsbeefunde des/der Prüfengeurs/in	☐	☐
- Gutachten über Abgasanlagen (bei Abgassammlern mit Hinweis, dass eine Strömungs-berechnung nach ÖNORM EN 13384-2 vorliegt)	☐	☐
- Gutachten über Kanal bzw. Senkgrube	☐	☐
- Gutachten über sicherheitstechn. Einrichtungen	☐	☐
- Nachweis über den Wärme- u. Schallschutz	☐	☐
- Bestätigung ü. Maßnahmen z. Schutz v. Emissionen	☐	☐
-	☐	☐

Gesetzliche Erfordernisse:

nicht erford.

erforderlich

- grundbücherliche Durchführung der Abteilung	☒	☐ →	☐ Mitt. an MA 64
- Gehsteigerherstellung	☒	☐ →	☐ Mitt. an Gehsteigref.
- Garagenlüftungsanlage FS-Meldung vollständig erstattet	☒	☐ ja	☐ nein

Fertigstellungsanzeige

Nachreichung

☐ Unvollständig belegt - Mitteilung

erfolgt am:

erfolgte am:

☒ Vollständig belegt am 09.10.2017 (Tag ab dem das Gebäude / das Bauwerk benutzt werden darf)

- ☒ Das Bauvorhaben ist daher als abgeschlossen zu beurteilen
- GWR - Meldung (Webformular) erfolgt (nur bei Neubau) ☐ JA ☒ NICHT ERFORDERLICH
- Kostenersatz für Gehsteig vorzuschreiben ☒ NEIN ☐ JA → Ä.A.
- Stellplatzsicherstellung außerhalb des Bauplatzes ☒ NEIN ☐ JA → protokollieren u. Kopie einlegen

☐ 22,00 / 50,00 VA bereits entrichtet☒ 22,00 / 50,00 VA mittels eBezahlen vorschreiben / vorgeschrieben am 11. OKT. 2017

Der Sachbearbeiter:

Für den Abteilungsleiter:

Wkm. Paezelt

Datum: 9. OKT. 2017

Bauführer/in:

KTB Klima und Sonnenschutztechnik
GmbH
Lemböckgasse 47
1230 Wien

Wien, 08.09.2017

Bauvorhaben:

Errichtung einer Schallschutzhaube

(Gegenstand)

Landesgerichtsstraße 6, 1010 Wien

(Adresse)

Zentralverband Haus und Eigentum

(BauwerberIn)

MA37/650990-2017-1

(Geschäftszahl der ursprünglichen Baubewilligung)

Erklärung des/r Bauführers/in zur Fertigstellung

- ☐ **Gemäß § 62 Abs. 7 BO**
(nach Bauanzeige gem. § 62 Abs. 1 Z 1 bis 3)
- ☒ **Gemäß § 128 Abs. 3 bzw. 3a BO**
(nach Baubewilligung bzw. Bauanzeige gem. § 62 Abs. 1 Z 4)

Es wird erklärt, dass das o.a. Bauvorhaben der Baubewilligung/
Bauanzeige und den Bauvorschriften entsprechend ausgeführt
wurde.

- ☐ ~~Weiters wird bestätigt, dass die vorgenommenen Ab-
änderungen, die nun im Rahmen der Fertigstellungsanzeige/
-meldung durch farbliche Ersichtlichmachung in den Aus-
führungsplänen bekannt gegeben werden, den Umfang des
§ 73 Abs. 3 nicht überschreiten.~~
- ☐ ~~Darüber hinaus wird das Erreichen der erforderlichen
Zuverlässigkeit der Tragwerke gemäß § 128 Abs. 2 Z 2 und Z 2a
bestätigt.~~



KTB Klima und Sonnen-
schutztechnik GmbH

A-1230 Wien, Lemböckgasse 47

Tel: 02259 / 2101, Fax: 02259 / 2101-440

E-Mail: office@ktbklima.at

(Bauführer/in, Stempel / Unterschrift)

Wichtige Hinweise umseitig!

1. Bezirk, Landesgerichtsstraße ONr. 6
EZ 894 der Kat. Gem. Innere Stadt



RK 01.09.2017

Magistrat der Stadt Wien
Magistratsabteilung 37
Baupolizei – Gebietsgruppe Ost
Stadterneuerung I
Dresdner Straße 82, 1. Stock
A – 1200 Wien
Telefon: (+43 1) 4000-37410
Telefax: (+43 1) 4000-99-37410
E-Mail: ggo.stadterneuerung1@ma37.wien.gv.at
www.bauen.wien.at

Aktenzahl	Sachbearbeiter/in:	Durchwahl	Datum
MA37/650990-2017-1	DI Schinner Bsc.	01/4000-37413	Wien, 28.8.2017

Errichtung einer Schallschutzhaube

Baubewilligung

B E S C H E I D

Nach Maßgabe der mit dem amtlichen Sichtvermerk versehenen Pläne, die einen wesentlichen Bestandteil dieses Bescheides bilden, wird gemäß § 61 der Bauordnung für Wien (BO), die Bewilligung erteilt, auf der im Betreff genannten Liegenschaft die nachstehend beschriebene Bauführung vorzunehmen:

Für das sich auf dem Dach befindliche Außengerät der bestehenden Klimaanlage für die Einheit Top 13 im Dachgeschoß wird eine Schallschutzhaube errichtet.

Vorgeschrieben wird:

- 1.) Der/Die Bauführer/in hat gemäß § 124 Abs. 2 BO den Beginn der Bauführung mindestens drei Tage vorher der MA 37/Bauinspektion und weiters dem Arbeitsinspektorat für Bauarbeiten (Fichtegasse 11, 1010 Wien) anzuzeigen.
- 2.) Gemäß § 127 Abs. 2 BO sind der/die Bauwerber/in und der/die Bauführer/in verpflichtet, auf der Baustelle die Baupläne, nach denen gebaut werden darf, die nach dem Fortschritt des Baues erforderlichen statischen Unterlagen aufzulegen.
- 3.) Der Bauwerber hat bei Baubeginn eine von der öffentlichen Verkehrsfläche bzw. dem Aufschließungsweg deutlich und dauernd sicht- und lesbare Tafel an der von der Bauführung betroffenen Liegenschaft anzubringen, aus der hervorgeht,
 1. um welches Bauvorhaben es sich handelt,
 2. das Datum des Baubeginns und
 3. die zuständige Behörde.

Diese Tafel muss mindestens drei Monate ab Baubeginn belassen werden. Grenzt die von der Bauführung betroffene Liegenschaft an mehrere öffentliche Verkehrsflächen oder Aufschließungswege, ist an jeder dieser Verkehrsflächen eine solche Tafel anzubringen.

- 4.) Auf die Bestellung eines/r Prüfsachverständigen/in und auf die Erstattung der Beschauanzeigen zur Ermöglichung der behördlichen Überprüfung der Bauausführung wird gemäß § 127 Abs. 6 BO verzichtet.
- 5.) Nach Fertigstellung der Bauarbeiten ist gemäß § 128 Abs. 1 BO bei der Behörde von dem/der Bauwerber/in, von dem/r Eigentümer/in (einem/r Miteigentümer/in) der Baulichkeit oder von dem/r Grundeigentümer/in (einem/r Grundmiteigentümer/in) eine Fertigstellungsanzeige zu erstatten, der folgende Unterlagen anzuschließen sind:
- eine Erklärung der/des Bauführer/in über die bewilligungsgemäße und den Bauvorschriften entsprechende Bauausführung;
 - wenn während der Bauausführung Abänderungen erfolgt sind, ungeachtet der hierfür erwirkten Bewilligung, ein der Ausführung entsprechender Plan, der von einem/r hierzu Berechtigten verfasst und von ihm/ihr sowie vom/von der Bauführer/in unterfertigt sein muss;

Auf die Vorlage der übrigen im § 128 Abs. 2 genannten Unterlagen wird gemäß § 128 Abs. 3 BO verzichtet.

B e g r ü n d u n g

Der dem Bescheid zu Grunde gelegte Sachverhalt ist den eingereichten Plänen und dem Ergebnis des Ermittlungsverfahrens entnommen. Die Bauführung ist nach den bestehenden Rechtsvorschriften zulässig. Die Auflagen sind in der Bauordnung für Wien und den einschlägigen Nebengesetzen begründet. Etwaige privatrechtliche Vereinbarungen waren im Baubewilligungsverfahren nicht zu prüfen.

R e c h t s m i t t e l b e l e h r u n g

Sie haben das Recht gegen diesen Bescheid Beschwerde an das Verwaltungsgericht zu erheben.

Die Beschwerde ist innerhalb von vier Wochen nach Zustellung dieses Bescheides schriftlich bei uns einzubringen. Sie hat den Bescheid, gegen den sie sich richtet, und die Behörde, die den Bescheid erlassen hat, zu bezeichnen. Weiters hat die Beschwerde die Gründe, auf die sich die Behauptung der Rechtswidrigkeit stützt, das Begehren und die Angaben, die erforderlich sind, um zu beurteilen, ob die Beschwerde rechtzeitig eingebracht ist, zu enthalten. Bewilligungswerber/innen (Antragsteller/innen) haben die Beschwerde mit EUR 30,00 Bundesgebühr zu vergewähren. Die Gebühr ist auf das Konto des Finanzamtes für Gebühren, Verkehrsteuern und Glücksspiel (IBAN: AT83 0100 0000 0550 4109, BIC: BUNDATWW) zu entrichten, wobei als Verwendungszweck das jeweilige Beschwerdeverfahren (Geschäftszahl des Bescheides) anzugeben ist.

Bei elektronischer Überweisung der Beschwerdegebühr mit der „Finanzamtszahlung“ ist als Empfänger das Finanzamt für Gebühren, Verkehrsteuern und Glücksspiel (IBAN wie zuvor) anzugeben oder auszuwählen. Weiters sind die Steuernummer/Abgabenkontonummer 109999102, die Abgabenart „EEE - Beschwerdegebühr“, das Datum des Bescheides als Zeitraum und der Betrag anzugeben.

Als Nachweis der Entrichtung der Gebühr ist der Zahlungsbeleg oder ein Ausdruck über die erfolgte Erteilung einer Zahlungsanweisung anzuschließen.

Für jede gebührenpflichtige Eingabe ist vom Beschwerdeführer (Antragsteller) ein gesonderter Beleg vorzulegen.

Die Beschwerde samt Einzahlungsnachweis kann in jeder technisch möglichen Form übermittelt werden. Bitte beachten Sie, dass die Absenderin bzw. der Absender die mit jeder Übermittlungsart verbundenen Risiken (z. B. Übertragungsverlust, Verlust des Schriftstückes) trägt.

Die telefonische oder mündliche Einbringung der Beschwerde ist nicht zulässig.

Hinweis auf Rechtsvorschriften

Es wird darauf aufmerksam gemacht, dass die einschlägigen baurechtlichen Vorschriften (Gesetze, Verordnungen und die darin verbindlich erklärten Normen), sofern im Baubewilligungsbescheid nicht anders bestimmt, auch dann auf den Bau Anwendung finden, wenn sie im Bescheid nicht angeführt oder in den Einreichunterlagen anders dargestellt sind. Im Einzelnen wird auf die Bestimmungen der BO und auf die Richtlinien des Österreichischen Instituts für Bautechnik (OIB) verwiesen. Weiters stellen grundsätzlich die ÖNORMen den Stand der Technik im Sinne des § 88 Abs. 1 BO dar.

Während der Bauführung ist jede unnötige, das zumutbare Maß übersteigende Lärm- und Staubbelästigung zu vermeiden und insbesondere im Hinblick auf die Einhaltung der Bestimmungen des Baulärmgesetzes, LGBl. für Wien Nr. 16/1973 in der dzt. geltenden Fassung in Verbindung mit der Verordnung der Wiener Landesregierung vom 30. Apr. 1973, LGBl. für Wien Nr. 20/1973 zu achten.

Auf die Bestimmungen des Bundesbehindertengleichstellungsgesetzes wird hingewiesen.

Auf die Verpflichtung zur Einhaltung der Bestimmungen des Arbeitnehmerschutzes und des Bauarbeitenkoordinationsgesetzes - BauKG wird hingewiesen. Auskünfte zum BauKG erhalten Sie zum Beispiel bei der Landesinnung Bau Wien, Wolfengasse 4, 1010 Wien.

Bei Baubeginn ist jedenfalls zu überprüfen, ob die der Berechnung zugrundeliegenden statischen Sachverhalte den Tatsachen vor Ort entsprechen. Die Auswirkungen aller früheren und/oder gleichzeitigen Baumaßnahmen sind zu berücksichtigen.

Handelt es sich um ein Bauvorhaben mit geringfügiger Auswirkung gemäß ÖNORM B 1998-3 darf das rechtmäßig bestehende Sicherheitsniveau zum Zeitpunkt der Errichtung um nicht mehr als 3 % verschlechtert werden.

Gebührenhinweis

Ausstehende Gebühren und Abgaben werden gesondert vorgeschrieben. Sie erhalten in den nächsten Tagen einen Zahlschein. Sie können aber auch unter Vorlage des Zahlscheines bei einer Kassa der Stadt Wien bar oder mittels Bankomat einzahlen. Weiters haben Sie die Möglichkeit die Bezahlung mittels Internet, über das „Bezahlservice“ der Stadt Wien (www.wien.at/bezahlen) vorzunehmen.

Ergeht an: siehe Verteilerliste im Anhang

Für den Abteilungsleiter:

DI Fischer
Oberstadtbaurat

Wichtige Informationen und Formulare im Internet:

www.bauen.wien.at

Anhang**Verteilerliste zur Zahl 650990-2017-1****Ergeht an:**

EinbringerIn/BauwerberIn, Grund(mit)eigentümerIn	Zentralverband der Hausbesitzer - Hausbesitzerhilfsverein Landesgerichtsstraße 6, A-1010 Wien unter Anschluß der Pläne A und B
---	--

In Abschrift an:

PlanverfasserIn	Baukult ZT GmbH Halbgasse 3-5/2, A-1070 Wien
BauführerIn	KTB Klima und Sonnenschutztechnik GmbH Lemböckgasse 47, A-1230 Wien

Behörden/Verwaltung:

Finanzamt für Gebühren, Verkehrsteuern und Glücksspiel
MA 37 - Bauinspektion, Überwachungsarchiv mit Plan C
Wiener Umweltanwaltschaft



Dieses Dokument wurde amtssigniert.

Information zur Prüfung des elektronischen Siegels
bzw. der elektronischen Signatur finden Sie unter:
<https://www.wien.gv.at/amtssignatur>

Einreichplan

EZ: 894 GST.NR.: 1526/2, KG: 01004 Innere Stadt

Objekt / Ansuchen um:

Errichtung Schallschutzhaube

Landesgerichtsstr.6
1010 Wien

Planinhalt

Grundriss DG und DD
Grundriss Galerie
Schnitt, Ansichten
Lageplan

Plannummer

P0420-LAN- EP- 002- A

Parie

A / B / C / D

Maßstab

1:100

Datum

01.08.2017

Plangröße

107 cm x 38 cm

Bauwerber/in

Zentralverband der Hausbesitzer
Hausbesitzerhilfsverein
1010 Wien, Landesgerichtsstraße 6
Tel. 01/406 33 18 Fax 01/406 53 49
ZVR 187843163 ATU 59082708

Bauführer/in

ktb KTB Klima und Sonnen-
schutztechnik GmbH
A-1230 Wien, Lemböckgasse 47
Tel: 02259 / 2101, Fax: 02259 / 2101-440
E-Mail: office@ktbklima.at

Planverfasser/in

baukult

... der stoff aus dem realitäten sind!



MA 37 - Baupolizei
Die Gebährenschild
gem. § 14 in Verb. m. § 3 Abs 2
Gebührengesetz 1957 in der Höhe
von EUR 7,80 wurde
☐ entrichtet
☒ bekanntgegeben, siehe Akt
28. Aug. 2017
Wien,
U.:

Grundstückseigentümer/in

Zentralverband der Hausbesitzer
Hausbesitzerhilfsverein
1010 Wien, Landesgerichtsstraße 6
Tel. 01/406 33 18 Fax 01/406 53 49
ZVR 187843163 ATU 59082708

Magistrat der Stadt Wien
Baubehörde
Magistratsabteilung 37 - Baupolizei
Gebietsgruppe Ost, Stadterneuerung 1

ZI.: MA37/650990-2017-1


Hierauf bezieht sich der Bescheid

Wien, 28.8.2017

Für den Abteilungsleiter:
Dipl.-Ing. Fischer
Oberstadtbaurat

MA37
BAUPOLIZEI
SICHER BAUEN

Stadt Wien

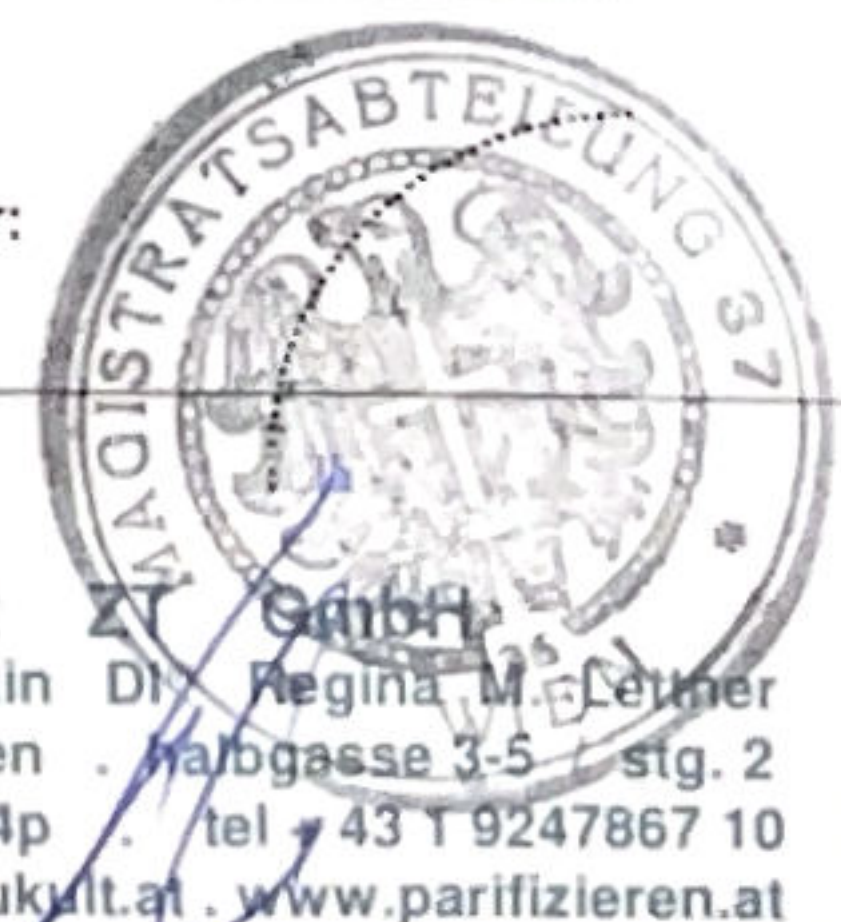

baukult ZT GmbH
Architektin DI. Regina M. Lechner
1070 wien, Halbtaggasse 3-5, stg. 2
tn 459264p tel. 43 1 9247867 10
www.baukult.at www.parifizieren.at

28

Einlegen
EZ 894
KG Innere Stadt

BEARBEITUNGSBOGEN

FERTIGSTELLUNGSANZEIGE

MA 371 1 - LANDESGERICHTSSTRASSE 6/191161-2015-1

Fertigstellungsanzeige MA 371 1 -

Belege :

	vorgelegt	nachgereicht am:
- Bestätigung des/der Ziviltechnikers/in	☐	☐
- Erklärung des/r Bauführers/in	☒	☐
- Ausführungsplan/pläne ☐ grau ☐ mit Änderungen	☐	☐
- Überprüfungsberichte des/der Prüfsachverständigen/in	☐	☐
- Gutachten über Abgasanlagen (bei Abgassammlern mit Hinweis, dass eine Strömungs-berechnung nach ÖNORM EN 13384-2 vorliegt)	☐	☐
- Gutachten über Kanal bzw. Senkgrube	☐	☐
- Gutachten über sicherheitstechn. Einrichtungen	☐	☐
- Nachweis über den Wärme- u. Schallschutz	☐	☐
- Bestätigung ü. Maßnahmen z. Schutz v. Emissionen	☐	☐
-	☐	☐

Gesetzliche Erfordernisse:

	nicht erford.	erforderlich
- grundbücherliche Durchführung der Abteilung	☒	☐ → ☐ Mitt. an MA 64
- Gehsteigerstellung	☒	☐ → ☐ Mitt. an Gehsteigref.
- Garagenlüftungsanlage FS-Meldung vollständig erstattet	☒	☐ ja ☐ nein

Fertigstellungsanzeige

☐ Unvollständig belegt - Mitteilung
erfolgt am:

Nachreichung

erfolgte am:
.....
.....

☒ Vollständig belegt am 09.10.2015 (Tag ab dem das Gebäude / das Bauwerk benutzt werden darf)

- ☒ Das Bauvorhaben ist daher als abgeschlossen zu beurteilen
- | | | |
|--|--|--|
| → GWR - Meldung (Webformular) erfolgt (nur bei Neubau) | ☐ JA | ☒ NICHT ERFORDERLICH |
| → Kostenersatz für Gehsteig vorschreiben | ☒ NEIN | ☐ JA → Ä.A. |
| → Stellplatzsicherstellung außerhalb des Bauplatzes | ☒ NEIN | ☐ JA → protokollieren u. Kopie einlegen |

☐ 22,00 / 50,00 VA bereits entrichtet
☒ 22,00 / 50,00 VA mittels eBezahlen vorschreiben / vorgeschrieben am :

Der Sachbearbeiter:
Wkm. Paczelt
Datum: 13. OKT. 2015

Für den Abteilungsleiter:
lw



FERTIGSTELLUNG NACH ÖNORM A 2060, ABSCHNITT 2.26

(Aufforderung zur Übernahme)

Bauvorhaben: Zentralverband Haus und Eigentum – Landesgerichtsstraße 6, 1010 Wien

Anlage: MAXA Kältemaschine/Wärmepumpe

Auftraggeber: Zentralverband der Hausbesitzer – Hausbesitzerhilfsverein - Landesgerichtsstraße 6/3, 1010 Wien

Auftragnehmer: KTB Klima und Sonnenschutztechnik GmbH

Gewerk (Leistung): Klima / Austausch der Kältemaschine/Wärmepumpe

Auftrag vom: 05.08.2015

Mit dieser Meldung erklärt KTB Klima und Sonnenschutztechnik GmbH, dass oben angeführte Leistungen (Anlagen) fertig gestellt und zur Übernahme bereit sind. Das heißt, es sind alle Einregulierungsarbeiten erfolgt, ein allfälliger vereinbarter Probetrieb und Funktionsprüfungen durchgeführt.

Die Betriebs- und Bedienungsanleitungen werden übergeben am: 08.10.2015

Als Termin zur Einweisung des Bedienungspersonals wird vorgeschlagen:

Sollte innerhalb von vierzehn Tagen nach Erhalt dieser Aufforderung, ohne Angabe von Gründen, keine Übernahme durch den Auftraggeber gemäß Abschnitt 2.22.8 der ÖNORM A 2060 erfolgen, so gilt die förmliche Übernahme mit Fristablauf erfolgt.

Leobersdorf, am 08.10.2015



KTB Klima und Sonnenschutztechnik GmbH

A-2544 Leobersdorf, Ared Straße 16-18
Tel: 02256/20 440, Fax: 02256/20 440 40

.....E-Mail: office@ktbklima.at.....

Stempel und Unterschrift



Klima- und Sonnenschutztechnik

Oberrdorf, Aredstrasse 16-18 Tel: 02256/20 440

PRÜFPROTOKOLL lt. § 22 DER KÄLTEANLAGENVERORDNUNG

Kunde:	Zentralverband Haus und Eigentum	Adresse:	1010, Landesgerichtsstrasse 6
Standort der Anlage:	Dach	Anlagenbezeichnung:	Kaltwassersatz
Techniker:	HWi	Datum:	2015-10-06

Verdampfer		Ölabscheider auf Funktion prüfen	N
Zustand	O	Druck- u. Saugmanometer auf Funktion prüfen	N
Überprüfen der Filter	N	Magnetventil auf Funktion prüfen	O
Filterdimension		Expansionsventil u. Einspritzung auf Funktion prüfen	O
Tropfwanne und Abfluß überprüfen	N	Vibration der Kältemittelleitungen	O
Überprüfen der Abtauheizung	N	Überprüfen der Isolierung	O
Überprüfen der Abtauuhr (Einstellung)	N	Ventilator und Ventilatorenantrieb	
Kondensator wassergekühlt		Überprüfen der Ventilator- u. Motorlager	O
Überprüfen des Wasserventils	N	Überprüfen v. Motorgehäuse u. E-Anschluß	O
Verflüssiger auf Verkalkung prüfen	N	Keilriemendimension	
Überprüfen des Ablaufes	N	Überprüfen u. Ausrichten der Antriebs- u. Keilriemen	N
Kondensator luftgekühlt		Festziehen u. Ausr. der Antr.- u. Keilriemenscheibe	N
Zustand	O	Kontroll- und Steuergeräte	
Luftseitige Reinigung	O	Funktionsüberprüfung d. Thermostaten (Einstellung)	40 °C
Ventilator überprüfen	O	Frostschutzthermostatefunktionsüberprüfung (Einst.)	4 °C
Kompressor		Elektr. Schaltger.Funktion u. Kontaktabnutzung prüfen	O
Überprüfen des Betriebs- u. Allgemeinzustandes	O	Sonstige Überprüfung	
Überprüfen der Ölpumpe und des Öldruckes	N	Temperatur Kaltwasser ein	31 °C
Ölstand prüfen	N	Temperatur Kaltwasser aus	42 °C
Überprüfen des Hochdruckschalters	aus bei 35 bar	Strömungswächter auf Funktion prüfen	O
Überprüfen des Niederdruckschalters	aus bei 4,2 bar	Schmutzfänger kontrollieren	N
Überprüfen des Ölschalters	aus bei N bar	Kühlturm	
Geräusch- u. Vibrationsprüfung	O	Temperatur Kühlwasser ein	N °C
Pump-Down-Kontrolle	Ausschaltung bei N bar	Temperatur Kühlwasser aus	N °C
Überprüfen der Keilriemen od. Kupplung	N	Überprüfen des Allgemeinzustandes des Kühlturmes	N
Keilriemendimension		Wasserwanne u. Wassersiebe a. Schmutzabl. prüfen	N
Leistungsregelung auf Funktion prüfen	N	Schwimmerventil bzw. Niveauregelung Funktion prüfen	N
Heißgas-Bypass-Einrichtung auf Funktion prüfen	N	Überprüfen des Ventilatormotors	N
Verflüssigungsdruck-/ temp. eintragen	°C / BAR 25,7	Sprühdüsen auf Funktion prüfen	N
Verdampfungsdruck-/ temp. eintragen	°C / BAR 9,9	Elektr. Heizung der Wasserwanne auf Funktion prüfen	N
Stromaufnahme des Kälteverdichters prüfen	17,5 Amp	Thermostate für elektrische Heizung prüfen	N
Kältemittelkreislauf prüfen		Ventilatorsteuerung auf Funktion prüfen	N
Allseitige Dichtheitsprüfung + Ölspuren Sichtkontrolle	O	Abschlammwassermenge kontrollieren	N
Überprüfung der Kältemittelfüllung	O	gemessen bei Aussentemperatur	17 °C
ZUSÄTZLICH GELEISTETE SAISONBEDINGTE ARBEITEN		Prüfbuch bestätigt	X / nein
Einschalten der Anlage vor der warmen Saison, wenn erforderlich			N
Abschalten der Anlage nach der warmen Saison, einschl. Abpumpen des Kältemittels, wenn erforderlich			N
Entleeren der Wasserleitungen, Pumpe, Kondensator und / oder Kühlturm um Einfrieren im Winter zu vermeiden			N

PRÜFZEICHEN:

O = in Ordnung

R = Reinigung durchgeführt

N = Nicht vorhanden

Z = Zusätzliche Arbeiten erforderlich

E = Einstellung durchgeführt

S = Betriebssicherheit nicht gegeben

VERMERKE:

MAXA HWA-A/H 0133, S/N:12-251145, R410a 3,7kg

Unterschrift Kunde:

(Stempel) Name in Blockbuchstaben

Bericht

Schalltechnischer Bericht

Auftraggeber

Zentralverband Haus und Eigentum

Dokumenttitel

**Austausch einer Klima-/Heizanlage am Dach des
Gebäudes 1010 Wien, Landesgerichtsstraße 6**

Dokumentendatum

03.03.2015

Revision: 1



ic **consulenten** | a member of ic group

ic consulenten Ziviltechniker GesmbH
Schönbrunner Straße 297, 1120 Wien, Österreich
T +43 1 521 69-0, F +43 1 521 69-180
office@ic-group.org, www.ic-group.org
FN 137252 t

EN ISO 9001

Zentralverband der Hausbesitzer
Hausbesitzerhilfsverein
1010 Wien, Landesgerichtsstraße 6
Tel. 01/406 33 18 Fax 01/406 53 49
ZVR 187843163 ATU 59082708

DOKUMENTENKONTROLLBLATT

PROJEKTNUMMER: Projektnummer 13x14013.03

ERSTELLT DURCH: iC consulenten Ziviltechniker GesmbH
Schönbrunner Straße 297, A-1120 Wien
Tel: +43 1 521 69 0
Fax: +43 1 521 69 180
E-Mail: office@ic-group.org

ERSTELLT FÜR: Zentralverband Haus und Eigentum
Adresse: 1010 Wien, Landesgerichtsstr. 6
Tel: +43 (0)1 406 33 18 DW 11
Fax: +43 (0)1 406 53 49
E-Mail: bednar@zvhausundeigentum.at

DATUM: 03.03.2015

BEARBEITER: Ljiljana Maletic Josic, Ing.
Bozena Gabriel, Mag.

Datum	Revision Nr.	Bearbeiter	Geprüft durch	Genehmigt durch	Unterschrift
03.07.2014	Rev. 0	mlj	gbo	uw	
03.03.2015	Rev. 1	mlj	gbo	uw	

INHALT

1.	Allgemeines.....	1
1.1.	Aufgabenstellung.....	1
1.2.	Verwendete Normen und Richtlinien	1
1.3.	Weitere Unterlagen.....	1
1.4.	Formelzeichen und Definitionen	1
1.5.	Projektbeschreibung	2
1.6.	Untersuchungsmethode.....	3
1.7.	Ergebnisunsicherheit.....	4
1.7.1.	Immissionsmessung	4
1.7.2.	Immissionsprognose.....	4
2.	Schallmessung zur Bestimmung des Schallleistungspegels des bestehenden Gerätes	5
2.1.	Durchführung der Messung	5
2.2.	Messprinzip	5
2.3.	Berechnung des Schallleistungspegels	6
2.4.	Messergebnisse	7
3.	Umgebungsärm	8
3.1.	Messung 2013	8
3.2.	Umgebungsärmkarten.....	8
3.3.	Flächenwidmung	8
3.4.	Planungsrichtwerte	9
4.	Schalltechnische Ausbreitung.....	9
4.1.	Grundlagen	9
4.2.	Schallemissionen	9
4.3.	Schallimmissionen	10
5.	Schalltechnische Beurteilung.....	10
6.	Anhang.....	12
6.1.	Datenblatt der geplanten Kühlanlage	12
6.2.	Schallleistungspegel der geplanten anlage	13
6.3.	Rechenmodell.....	14
6.4.	Lärmrasterkarte.....	15

TABELLEN

Tabelle 1: Immissionspunkte.....	3
Tabelle 2: 95%-Vertrauensbereiche, in dB.....	4
Tabelle 3: 95%-Vertrauensbereiche für typischen Straßenverkehr, in dB.....	4
Tabelle 4: Genauigkeit Immissionsprognose (Quelle: ÖNORM ISO 9613-2).....	5
Tabelle 5: Messwerte bei Vollbetrieb "Kühlung" in 1 m Abstand.....	7
Tabelle 6: Berechnung des Schalleistungspegels	8
Tabelle 7: Messergebnisse 2013	8
Tabelle 8: Ermittlung vom Planungsrichtwert.....	9
Tabelle 9: Schallemissionen Bestand und Prognose	10
Tabelle 10: Ergebnisse.....	10
Tabelle 11: Schalltechnische Beurteilung am Tag (06:00-19:00) und Abend (19:00-22:00).....	10

ABBILDUNGEN

Abbildung 1: Luftbilddarstellung der Umgebung (Quelle: https://maps.google.at).....	2
Abbildung 2: Lageplan und Abstände zu den exponierten Anrainern	3
Abbildung 3: Messprinzip - quaderförmige Hüllfläche nach ÖNORM EN ISO 3746.....	6
Abbildung 4: Kälteanlage am Dach des Hauses Landesgerichtsstr. 6	6
Abbildung 5: Auszug Flächenwidmungsplan (Quelle: www.wien.gv.at/flaechenwidmung/public).....	8
Abbildung 6: Berechnung der Schalleistungspegel	13
Abbildung 7: Ansicht Rechenmodell	14
Abbildung 8: Lärmrasterkarte Tag 6-19Uhr, Abend 19-22 Uhr, h=25m üGOK	15

1. ALLGEMEINES

1.1. AUFGABENSTELLUNG

Die Firma iC consulenten wurde vom Zentralverband Haus und Eigentum beauftragt, eine schalltechnische Untersuchung betreffend den Austausch der Klima-/Heizanlage am Dach des Hauses Landesgerichtsstr. 6 im 1. Wiener Gemeindebezirk durchzuführen. Nach Bedarf sollten Lärminderungsmaßnahmen ausgearbeitet werden.

1.2. VERWENDETE NORMEN UND RICHTLINIEN

ÖNORM S 5004 (12/2008): Messung von Schallimmissionen

ÖAL Richtlinie 3 Blatt 1 (03/2008): Beurteilung von Schallimmissionen im Nachbarschaftsbereich

ÖAL Richtlinie 36 Blatt 1 (02/2007): Schalltechnische Grundlagen für die örtliche und überörtliche Raumplanung und Raumordnung

ÖNORM EN ISO 3746 (03/2011): Akustik – Bestimmung der Schallleistungs- und Schallenergiepegel von Geräuschquellen aus Schalldruckmessungen – Hüllflächenverfahren der Genauigkeitsklasse 3 über einer reflektierenden Ebene.

ÖNORM ISO 9613-2 (07/2008): Dämpfung des Schalls bei Ausbreitung im Freien

1.3. WEITERE UNTERLAGEN

- Bauakustische Messungen – Messungen von Schallimmissionen gemäß ÖNORM S 5004. Wohngebäude Rathausstr. 5, 1010 Wien, Vasko+Partner Ingenieure, 08.07.2013
- Schalltechnische Stellungnahme, iC consulenten Ziviltechniker GesmbH, 07.02.2014
- Datenblatt der Firma Maxa Air Conditioning
- Einreichplan, DI Andrzej Glogowski, 26.02.2015

1.4. FORMELZEICHEN UND DEFINITIONEN

p **Schalldruck [Pa]**

Differenz zwischen dem Momentanwert des Drucks und dem statischen Druck

L_p **Schalldruckpegel [dB]**

Zehnfacher dekadischer Logarithmus des Verhältnisses des Quadrates des Schalldrucks p zum Quadrat eines Bezugswertes p_0 (20 μ Pa) angegeben in Dezibel

L_{pA} **A-bewerteter Schalldruckpegel [dB]**

Der A – bewertete Schalldruckpegel ist der mit der Frequenzbewertung „A“ ermittelte Schalldruckpegel.

L_w **Schallleistungspegel [dB]**

zehnfacher dekadischer Logarithmus des Verhältnisses der Schallleistung P einer Quelle zu einem Bezugswert P_0 (1 pW), angegeben in Dezibel

L_{wA} **A-bewerteter Schallleistungspegel [dB]**

Der A – bewertete Schallleistungspegel ist der mit der Frequenzbewertung „A“ ermittelte Schallleistungspegel.

$L_{A,eq}$ **A – bewerteter energieäquivalenter Dauerschallpegel [dB]**

Der A – bewertete energieäquivalente Dauerschallpegel ist der mit der Frequenzbewertung „A“ ermittelte energieäquivalente Dauerschallpegel

L_{A,95} **Basispegel [dB]**

Der Basispegel ist der in 95 % der Messzeit überschrittene A - bewertete, mit der Anzeigedynamik „fast“ ermittelte Schalldruckpegel.

1.5. PROJEKTbeschreibung

In der Einreichplanung aus dem Jahr 2007 über die Errichtung einer Klimaanlage auf dem Dach des Hauses Landesgerichtsstr. 6 in 1010 Wien wurden schalltechnische Berechnungen durchgeführt und die Anlage wurde für die Betriebszeit 6-20 Uhr (Werktage) genehmigt. Aufgrund der Beschwerden der Anrainer wurde im Juli 2013 durch das Büro Vasko+Partner eine Messung der auftretenden Schallimmissionen bei Betrieb der Klimaanlage und bei abgeschaltetem Gerät durchgeführt. Der Messpunkt befand sich im Innenhof, an der Hausfassade Top 10, Rathausstr. 5, 1010 Wien. Bei der Messung wurde festgestellt, dass die Schallimmissionen beim Betrieb der Klimaanlage (Umgebungs-lärm + Klimaanlage) am Immissionspunkt bei $L_{pA}=48$ dB lagen und den bestehenden Umgebungs-lärm unzulässig erhöhen. Im Zuge der technischen Planung wurde als beste Maßnahme der Austausch der Anlage festgestellt. Es wird eine lärmarme Anlage (Sonderanfertigung) der Firma Maxa Air Conditioning Type HWA-A 0133 am Dach aufgestellt.

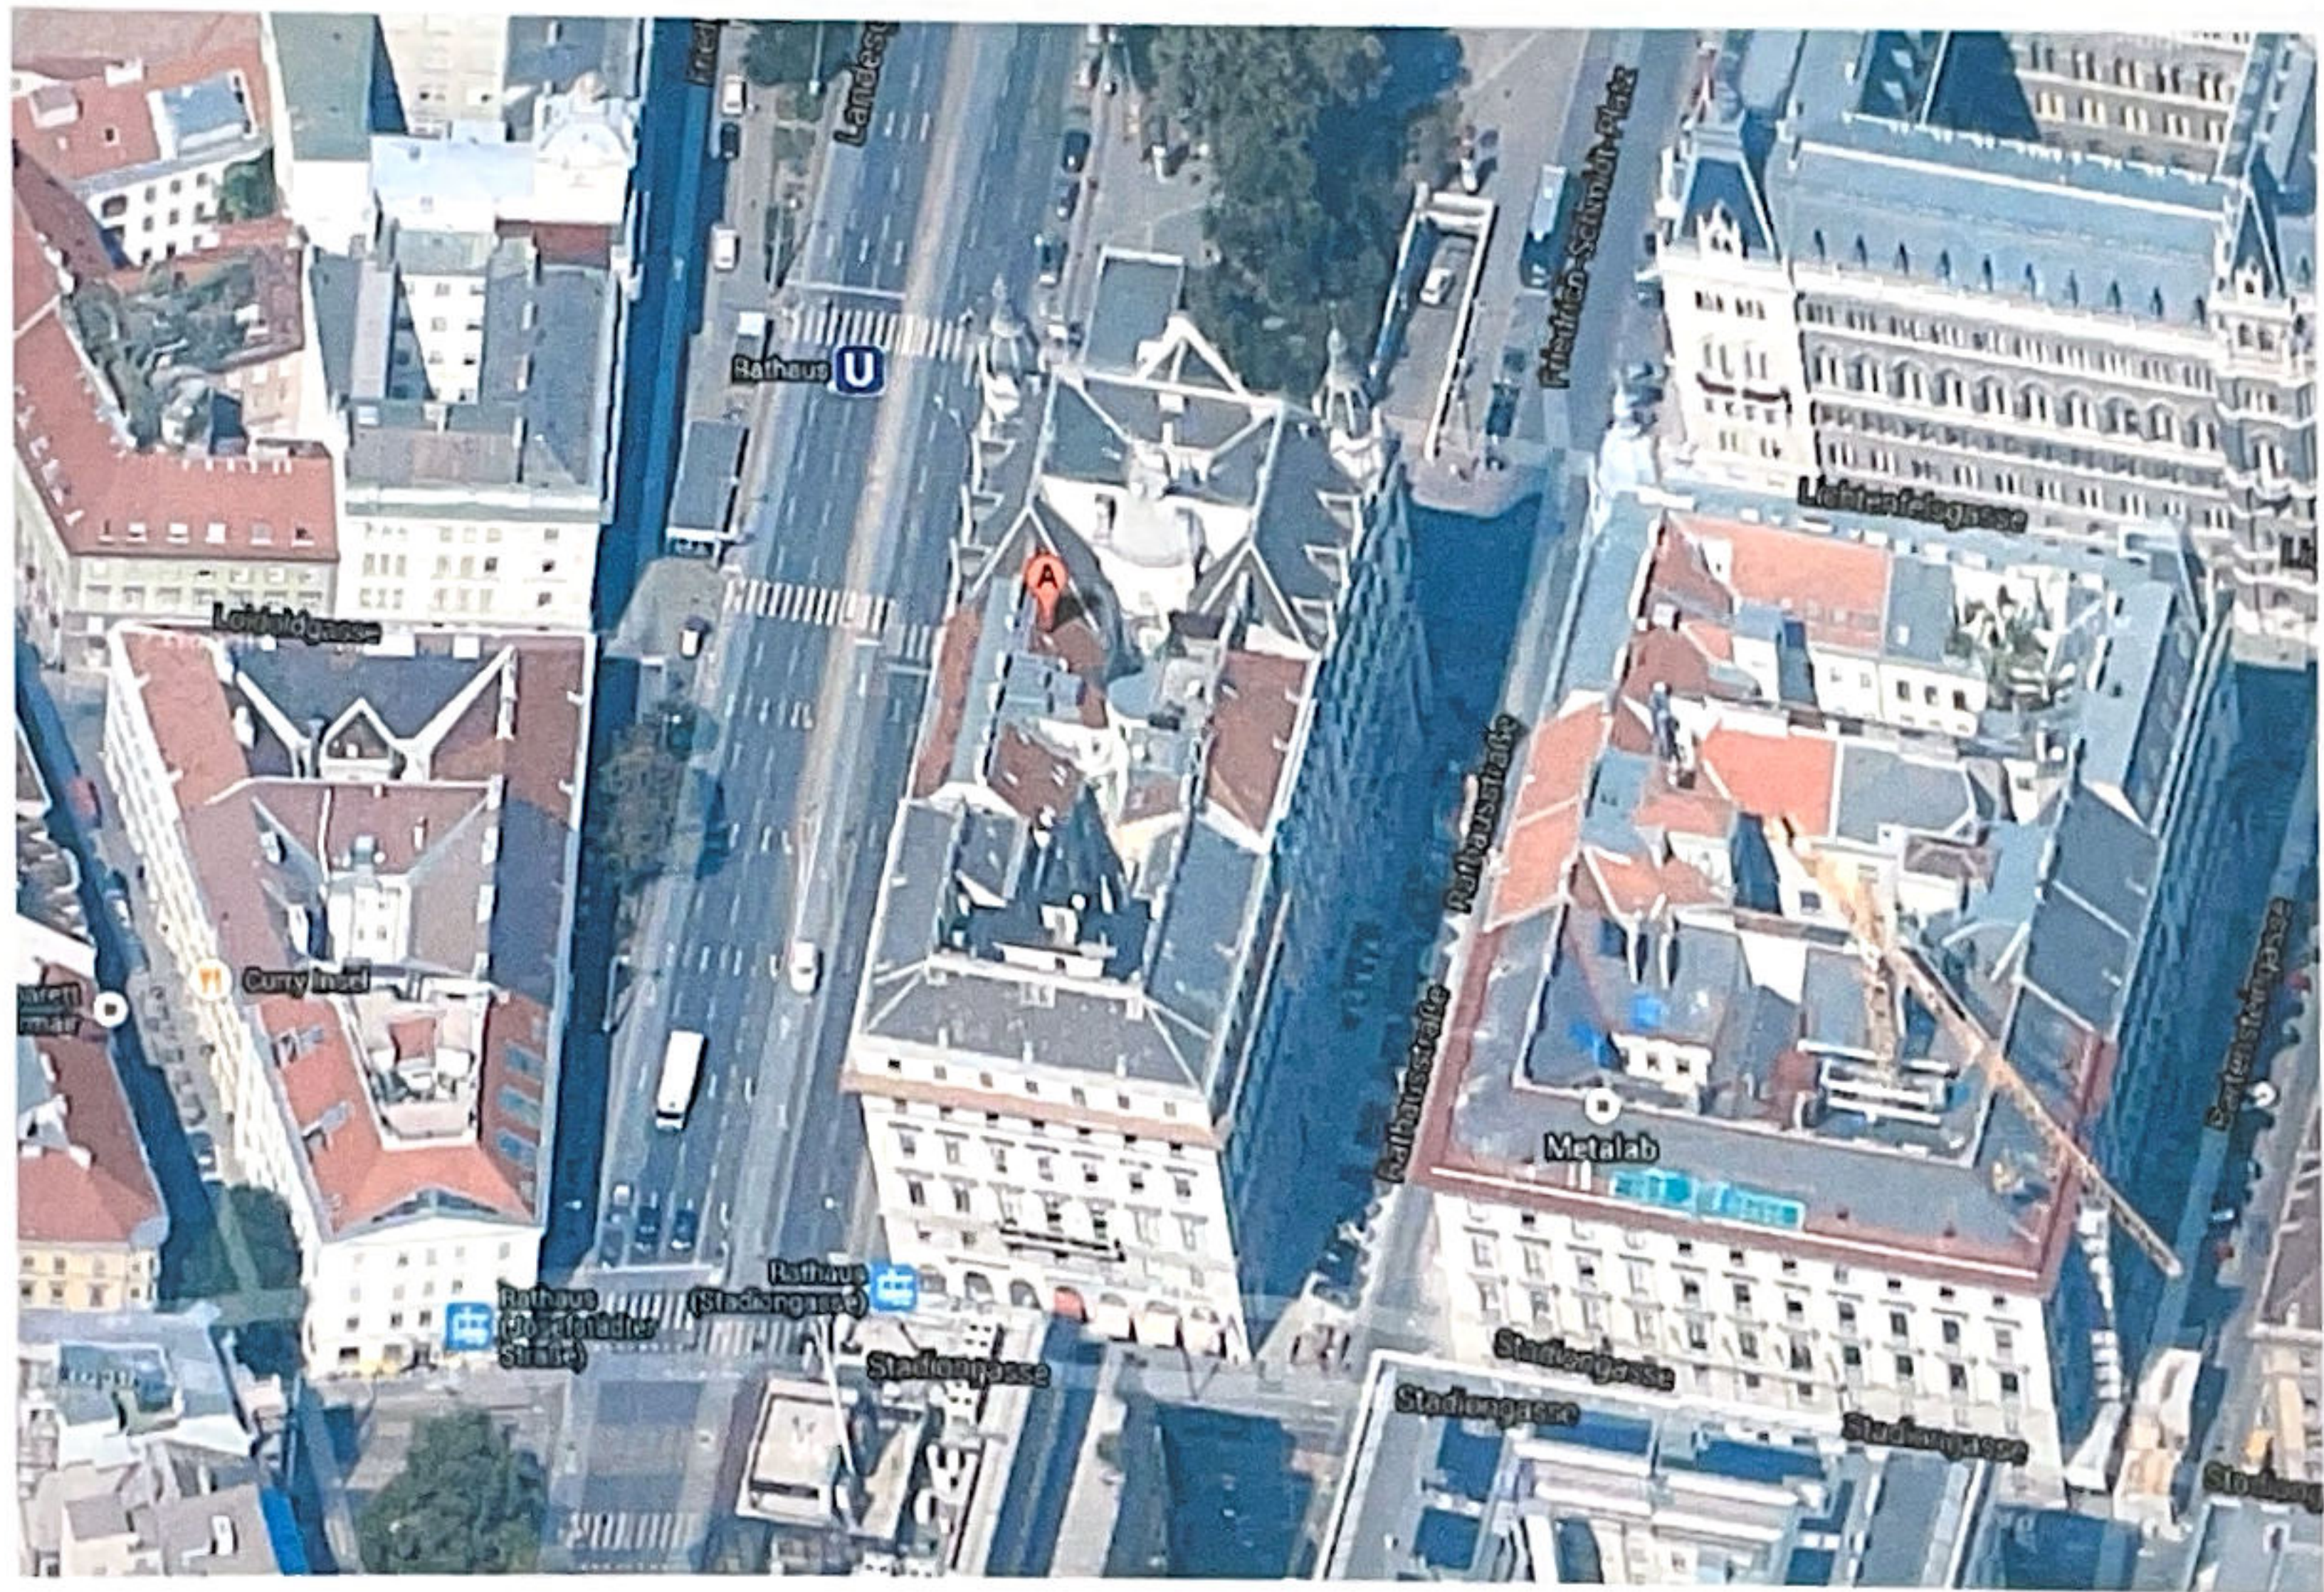


Abbildung 1: Luftbilddarstellung der Umgebung (Quelle: <https://maps.google.at>)

Wie in Abbildung 2 zu entnehmen ist, befinden sich die lärmexponiertesten Anrainerpunkte im Innenhof, Rathausstraße 5.

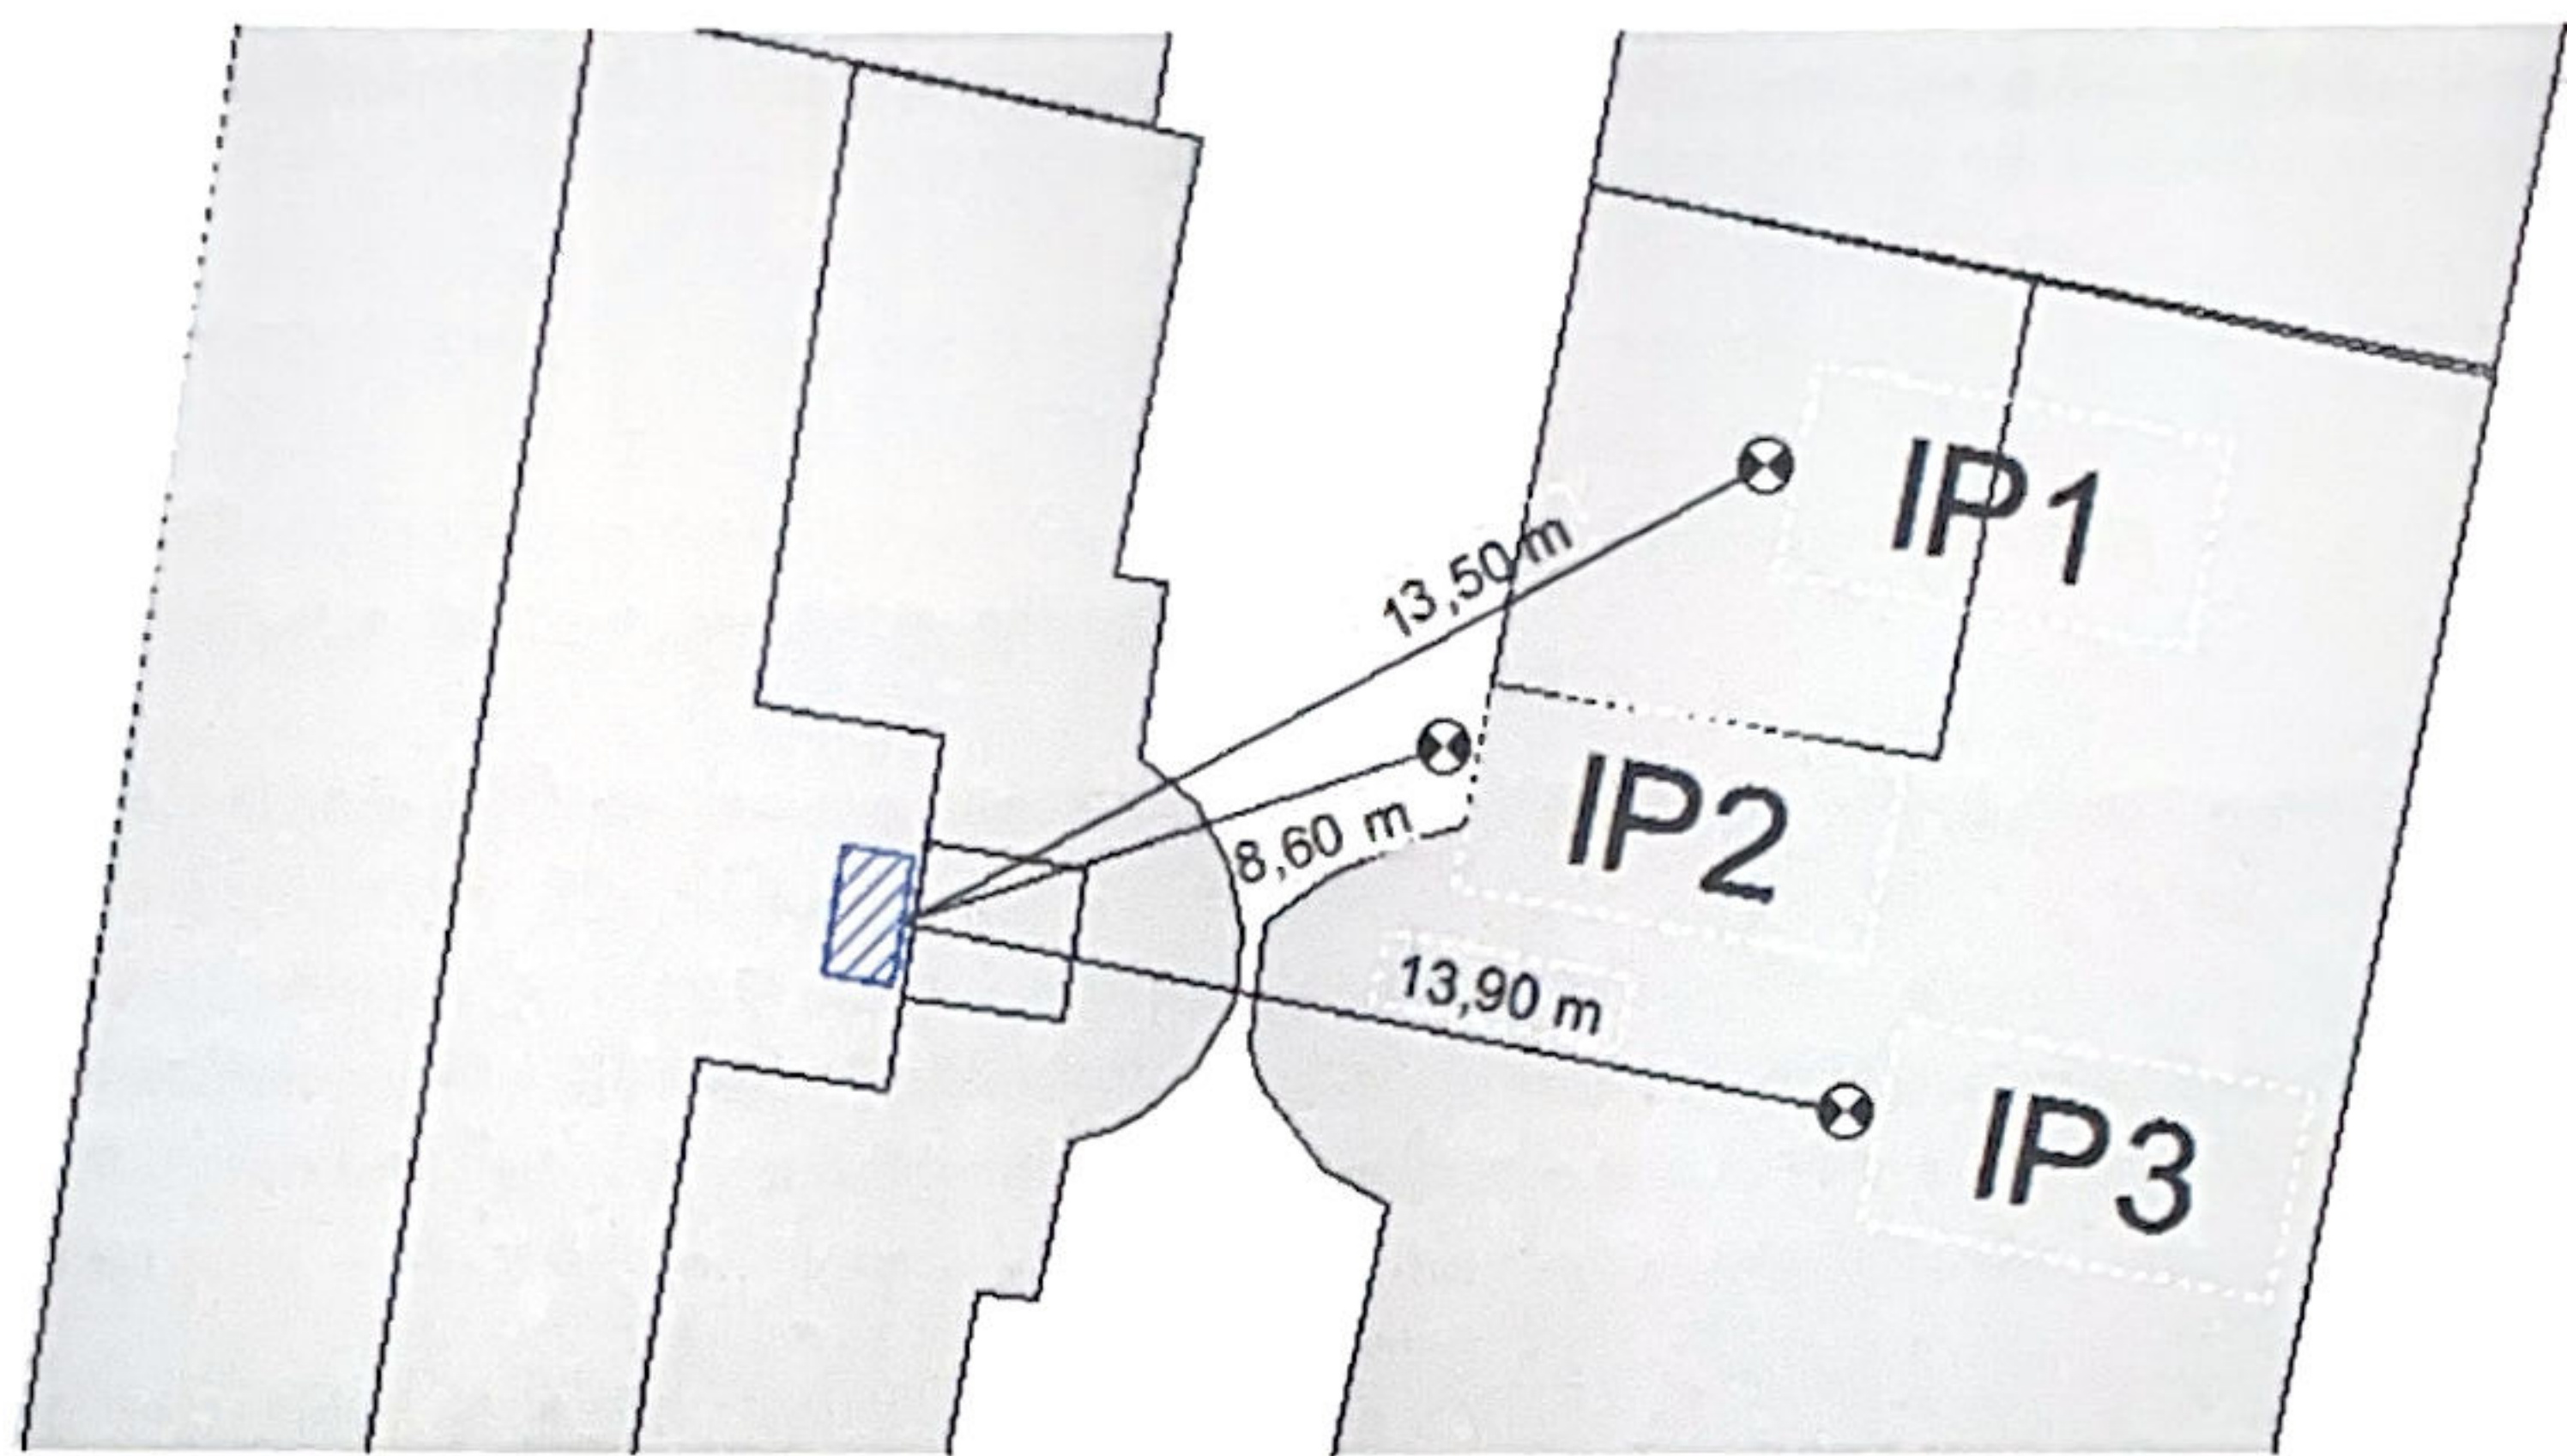


Abbildung 2: Lageplan und Abstände zu den exponierten Anrainern

Tabelle 1 gibt Aufschluss über die exponierten Immissionspunkte.

IP	Adresse	Höhe über GOK	Abstand zum Gerät
IP1	1010 Wien, Rathausstraße 5/Terrasse Nord	26,5 m	13,5 m
IP2	1010 Wien, Rathausstraße 5/Top 10, Fenster Hof, 6.OG	25,5 m	8,6 m
IP3	1010 Wien, Rathausstraße 5/Dachterrasse	29,0 m	13,9 m

Tabelle 1: Immissionspunkte

Im Dachgeschoß des Hauses Landesgerichtsstraße 6 befinden sich Räumlichkeiten des Zentralverbandes Haus & Eigentum mit Büroraumnutzung (keine Wohnungen).

1.6. **UNTERSUCHUNGSMETHODE**

Die Beurteilung der Lärmauswirkungen auf die Nachbarschaft erfolgte entsprechend der ÖAL-Richtlinie 3-1 unter Berücksichtigung des Richtwertes für die Flächenwidmung entsprechend Gebietskategorie nach ÖAL Richtlinie 36 Blatt 1 sowie der Umgebungslärmkarten des Umweltministeriums und den Messungen.

Prinzipiell definiert die ÖAL-Richtlinie 3-1 ein Irrelevanzkriterium, welches auch mögliche künftige Immissionssituationen berücksichtigt. Dieses Irrelevanzkriterium wird durch den sog. „planungstechnischen Grundsatz“ (PTG) beschrieben. Der Beurteilungspegel der spezifischen Immission aus den Betriebsanlagen soll demzufolge um mindestens MdB unterhalb des Planungsrichtwertes liegen. Der Planungsrichtwert stellt dabei das Minimum aus dem Beurteilungspegel der ortsüblichen Immission (Messung bzw. Umgebungslärmkarte) und dem Richtwert gemäß Flächenwidmung dar.

Der Beurteilungspegel der spezifischen Immission basiert auf dem energieäquivalenten Dauerschallpegel, welcher mit einem Anlagenzuschlag (+ 5dB) versehen wird. Im gegenständlichen Projekt erfolgt die Beurteilung für den Tag 6:00 – 19:00 Uhr und für

den Abend 19:00 – 22:00 Uhr. In der Nacht 22:00 – 6:00 Uhr wird die Anlage nicht betrieben.

Wird der PTG eingehalten, sind die Anlagen ohne weitere Maßnahmen aus schalltechnischer Sicht genehmigungsfähig. Bei nicht Einhaltung des PTGs ist eine individuelle Beurteilung durchzuführen. Zusätzlich wird die prognostizierte Schallimmission dem Basispegel gegenüber gestellt.

Die in der Nachbarschaft zu erwartenden Betriebslärmimmissionen wurden ausgehend von den Emissionen der projektierten Schallquellen nach ÖN ISO 9613-2 mittels der PC Software Cadna/A berechnet. Dabei wurden die Schallimmissionspegel (Tag) jeweils an lärmexponierten Punkten der Wohnnachbarschaft errechnet, sowie Rasterlärmkarten für den Zeitraum Tag in einer Rasterhöhe entsprechend der Anrainerpunkte (IP2) erstellt.

1.7. ERGEBNISUNSICHERHEIT

1.7.1. Immissionsmessung

Die ausgewiesenen Messwerte, bezogen auf den tatsächlichen Messzeitraum, beinhalten eine Toleranz von ± 1 dB für geeichte Präzisionsschallpegelmessgeräte. Für eine allgemeine Aussage sind noch die zusätzlichen Streuungen durch die Umgebungsbedingungen (maßgebliche Schallquelle, Wetterbedingungen, Bodenbeschaffenheit, usw.) zu berücksichtigen. Bei Geräuschsituationen, die durch Quellen verursacht werden und die in freien Entfernungen von <50 m liegen, können die meteorologischen Einflüsse vernachlässigt werden. Bei Geräuschsituationen mit maßgeblichen Schallquellen in größeren Entfernungen unterliegen die Messwerte größeren Streubreiten, die nur statistisch durch mehrfache Messungen eingegrenzt werden können. Gemäß ÖNORM S 5004 können anhand der Ergebnisse von Ringversuchen folgende Vertrauensbereiche für Schallmessungen im Freien angeführt werden:

Geräuschart	für $L_{A,eq}$
Straßenverkehr	1,1
Anlagengeräusche	2,0

Tabelle 2: 95%-Vertrauensbereiche, in dB

Speziell für Straßenverkehrslärmmessungen an Gebäuden werden folgende Vertrauensbereiche angeführt:

Messpunkt	für $L_{A,eq}$	für $L_{A,95}$	für $L_{A,1}$
vor dem geöffneten Fenster	0,9	1,1	1,5
im Raum bei geöffnetem Fenster	0,7	1,0	0,8
an der Grenzfläche	0,6	0,7	1,0

Tabelle 3: 95%-Vertrauensbereiche für typischen Straßenverkehr, in dB

1.7.2. Immissionsprognose

Das verwendete Rechenmodell berücksichtigt prinzipiell günstige Schallausbreitungsbedingungen bei Mitwindwetterlage. Die verwendete Berechnungsgrundlage ÖNORM ISO 9613-2 führt für diese Bedingungen folgende Genauigkeiten an:

Höhe h^a m	Entfernung d^b	
	$0 < d < 100$ m	$100 \text{ m} < d < 1\,000$ m
$0 < h < 5$	± 3 dB	± 3 dB
$5 < h < 30$	± 1 dB	± 3 dB
^a h mittlere Höhe von Quelle und Empfänger ^b d Entfernung zwischen Quelle und Empfänger		

Tabelle 4: Genauigkeit Immissionsprognose (Quelle: ÖNORM ISO 9613-2)

2. SCHALLMESSUNG ZUR BESTIMMUNG DES SCHALLEISTUNGSPEGELS DES BESTEHENDEN GERÄTES

2.1. DURCHFÜHRUNG DER MESSUNG

Ort: 1010 Wien, am Dach des Hauses Landesgerichtsstraße 6
Datum: 12.03.2014 zwischen 9:30 – 11:00 Uhr
Messbeauftragte: Mag. B. Gabriel, iC
Wetter: sonnig, leichter Wind, +10°C
Umgebungsärm: Der Schallpegel am Messort beim abgeschalteten Klimagerät war hauptsächlich durch den Verkehrslärm, entfernte Baustellengeräusche und gelegentliche Gespräche im Innenhof geprägt.

Die Messung erfolgte nach ÖNORM EN ISO 3746. Es wurde in den Phasen mit niedrigem Umgebungsärmpegel („rot“-Phase bei der Verkehrsampel) und ohne Störgeräusche durch die Baustelle gemessen.

Messgerät:

Schallpegelmesser Brüel&Kjaer Typ 2260 mit Terzfilter Präzisionsklasse 0,7,
Seriennummer: 2349974
½Zoll-Mikrofon der Fa. Brüel&Kjaer Type 4189, Seriennummer: 2339644
½Zoll-Mikrofonvorverstärker der Brüel&Kjaer Type ZC 0026, Seriennummer: 3053
Prüfschallquelle Brüel&Kjaer Kalibrator Type 4231, Seriennummer: 2342865

Alle Messgeräte hatten zum Zeitpunkt der Messung eine gültige Eichung.
Die Messkette wurde vor und nach der Messung mittels Prüfschallquelle kalibriert.

2.2. MESSPRINZIP

Die Messung wurde auf einer gedachten quaderförmigen Hüllfläche in 1 m Abstand vom Gerät durchgeführt.

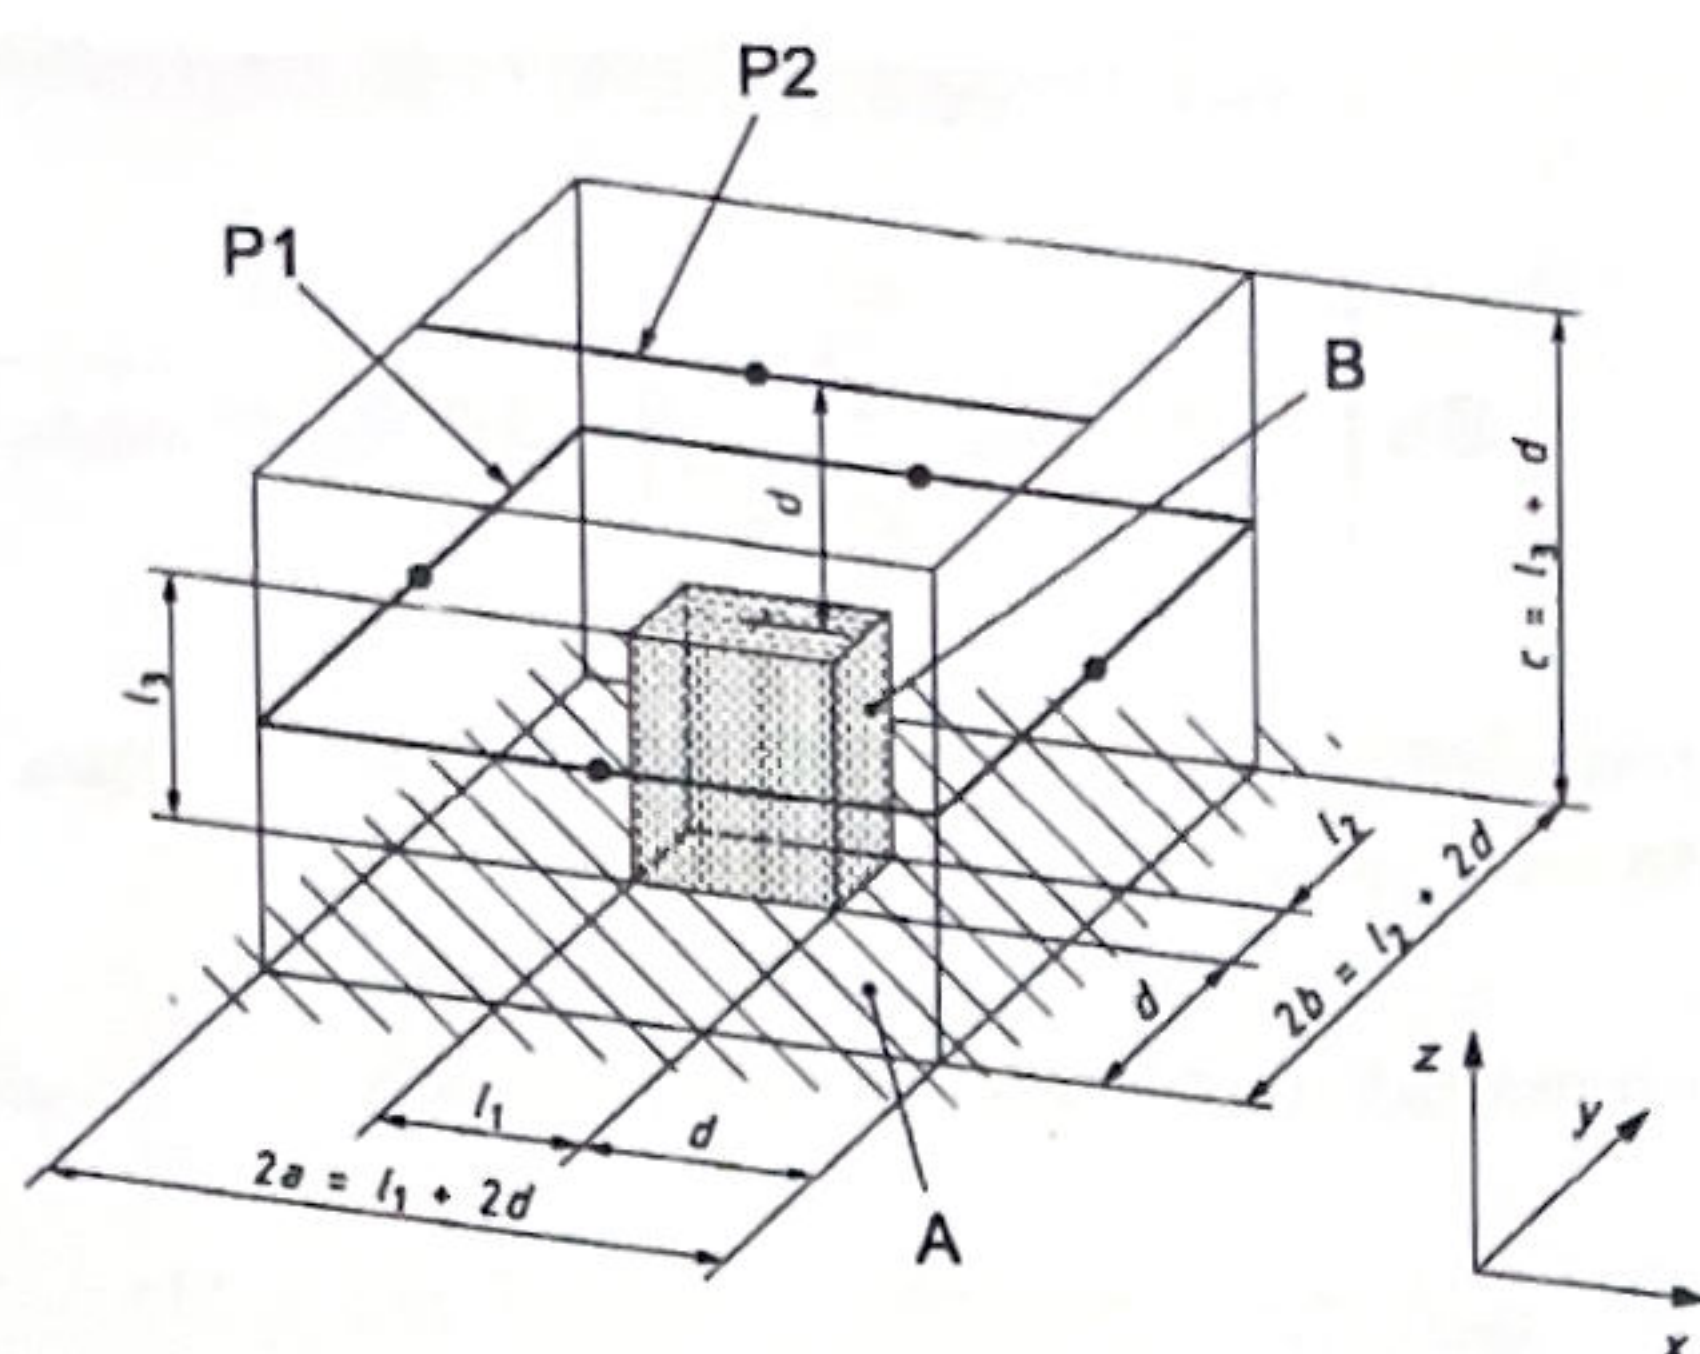


Abbildung 3: Messprinzip - quaderförmige Hüllfläche nach ÖNORM EN ISO 3746

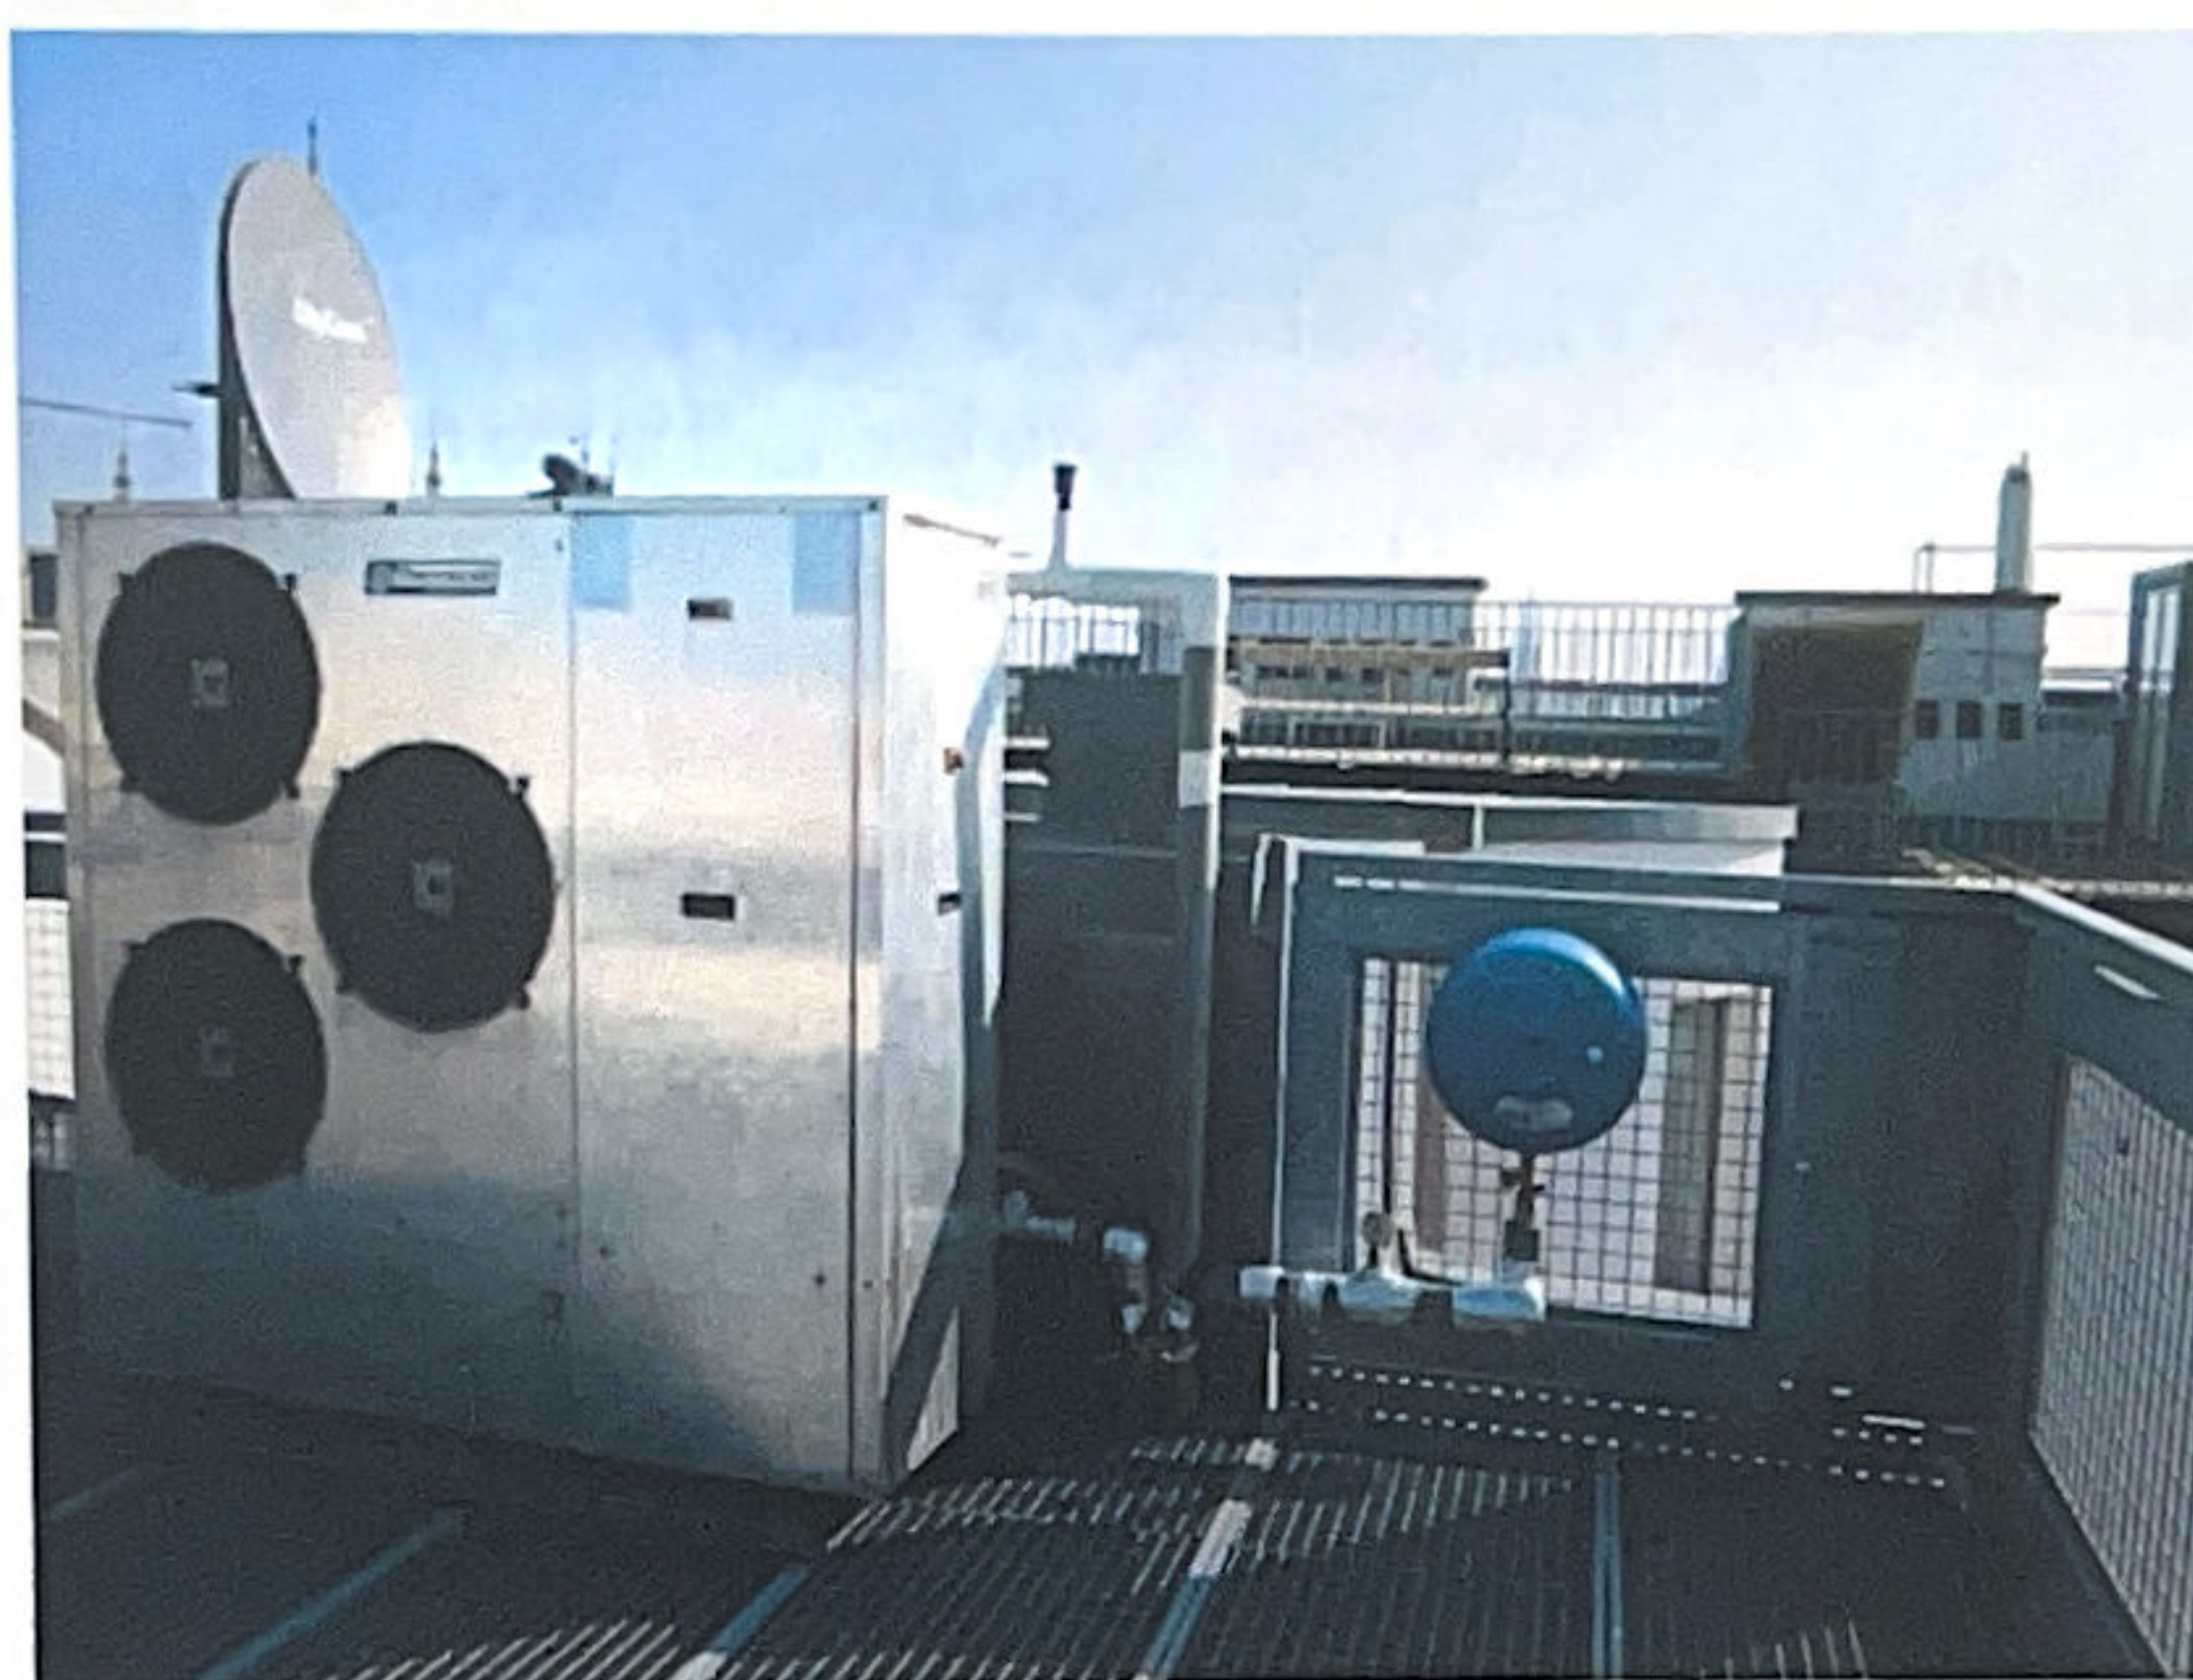


Abbildung 4: Kälteanlage am Dach des Hauses Landesgerichtsstr. 6

2.3.

BERECHNUNG DES SCHALLLEISTUNGSPEGELS

Die Ermittlung des Schallleistungspegels erfolgt in folgenden Rechenschritten:

Der gemittelte Schalldruckpegel in einem definierten Abstand $\overline{L'_{pA(ST)}}$

$$\overline{L'_{pA(ST)}} = 10 \log_{10} \left[\frac{1}{N_M} \sum_{i=0}^{N_M} 10^{0,1 L'_{pAi(ST)}} \right] \text{ dB}$$

$L'_{pAi(ST)}$ der in Dezibel angegeben zeitlich gemittelte A-bewertete Schalldruckpegel der untersuchenden Geräuschquelle (ST) an der i-ten Mikrofonposition oder für die i-te Mikrofonbahn.

N_M die Anzahl der Mikrofonpositionen oder Mikrofonbahnen

Mittelwert des Fremdgeräusches $\overline{L_{pA(B)}}$

$$\overline{L_{pA(B)}} = 10\log_{10} \left[\frac{1}{N_M} \sum_{i=0}^{N_M} 10^{0,1L_{pAi(B)}} \right] \text{dB}$$

- $L'_{pAi(B)}$

der in Dezibel angegeben zeitlich gemittelte A-bewertete Schalldruckpegel des Fremdgeräusch (B) an der i-ten Mikrofonposition oder für die i-te Mikrofonbahn.
- N_M

die Anzahl der Mikrofonpositionen oder Mikrofonbahnen

Korrektur des Fremdgeräuscheinflusses ΔL_{pA}

$$\Delta L_{pA} = \overline{L'_{pA(ST)}} - \overline{L_{pA(B)}}$$

- Für $\Delta L_{pA} > 10 \text{ dB}$:

$K_{1A} = 0 \text{ dB}$
- Für $3 \text{ dB} \leq \Delta L_{pA} \leq 10 \text{ dB}$:

$K_{1A} = -10\log_{10}(1 - 10^{-0,1\Delta L_{pA}}) \text{dB}$
- Für $\Delta L_{pA} < 3 \text{ dB}$:

$K_{1A} = 3 \text{ dB}$

- K_{1A}

Fremdgeräuschkorrekturwert

Berechnung des Messflächenschalldruckpegels nach Korrektur

$$\overline{L_{pA}} = \overline{L'_{pA(ST)}} - K_{1A} - K_{2A}$$

- K_{2A}

Umgebungskorrekturwert (Im Freifeld $K_{2A} = 0 \text{ dB}$)

Berechnung des Schallleistungspegels $L_{W,A}$

$$L_{WA} = \overline{L_{pA}} + 10\log_{10} \left(\frac{S}{S_0} \right) \text{dB}$$

- S

der Flächeninhalt der Messfläche, in Quadratmetern
- S_0

Bezugsfläche (1 m²)

2.4. MESSERGEBNISSE

Messpunkt	Messwert $L'_{pA(ST)}$ in dB
1 Südseite	62,2
2 Westseite	65,2
3 Westseite	65,2
4 Nordseite	64,9
Mittelwert $\overline{L'_{pA(ST)}}$	64,5

Tabelle 5: Messwerte bei Vollbetrieb "Kühlung" in 1 m Abstand

Parameter	Formelzeichen	Einheit	Wert
Gemittelter Messwert	$\overline{L'_{pA(ST)}}$	dB	64,5
Fremdgeräusch	$\overline{L_{pA(B)}}$	dB	49,4
Differenz Messwert und Fremdgeräusch	ΔL_{pA}	dB	15,1
Korrektur des Fremdgeräusches	K_{1A}	dB	0
Messflächenschalldruckpegel	$\overline{L_{pA}}$	dB	64,5
Messabstand	d	m	1
Hüllfläche	A	m ²	32
Schallleistungspegel	$L_{W,A}$	dB	79,6
Schallleistungspegel gerundet	$L_{W,A}$	dB	80

Tabelle 6: Berechnung des Schallleistungspegels

3. UMGEBUNGSLÄRM

3.1. **MESSUNG 2013**

Hier wird auf die Ergebnisse der schalltechnischen Untersuchung von Vasko+Partner Ingenieure vom 08.07.2013 verwiesen. In der kurzen Zeitphase bei abgeschalteter Anlage wurden folgende Pegel gemessen:

Messpunkt	Tag	
	$L_{A,eq}$ [dB]	$L_{A,95}$ [dB]
MP1 Rathausstraße 5/Innenhoffassade 6.OG/Top 10	44	40

Tabelle 7: Messergebnisse 2013

3.2. **UMGEBUNGSLÄRMKARTEN**

Da die Umgebungslärmkarten den Pegel an den Hausfassaden ausweisen und die Situation in einem Innenhof nicht ausreichend darstellen, wurden keine Lärmkarten der Beurteilung zu Grunde gelegt.

3.3. **FLÄCHENWIDMUNG**

Folgende Planungsrichtwerte wurden dem Bereich Landesgerichtsstraße 6 zugeordnet.
Flächenwidmungskategorie: Gemischtes Baugebiet:
Tag: 60 dB/A Abend: 55 dB/A Nacht: 50 dB/A



Abbildung 5: Auszug Flächenwidmungsplan (Quelle:www.wien.gv.at/flaechenwidmung/public)