



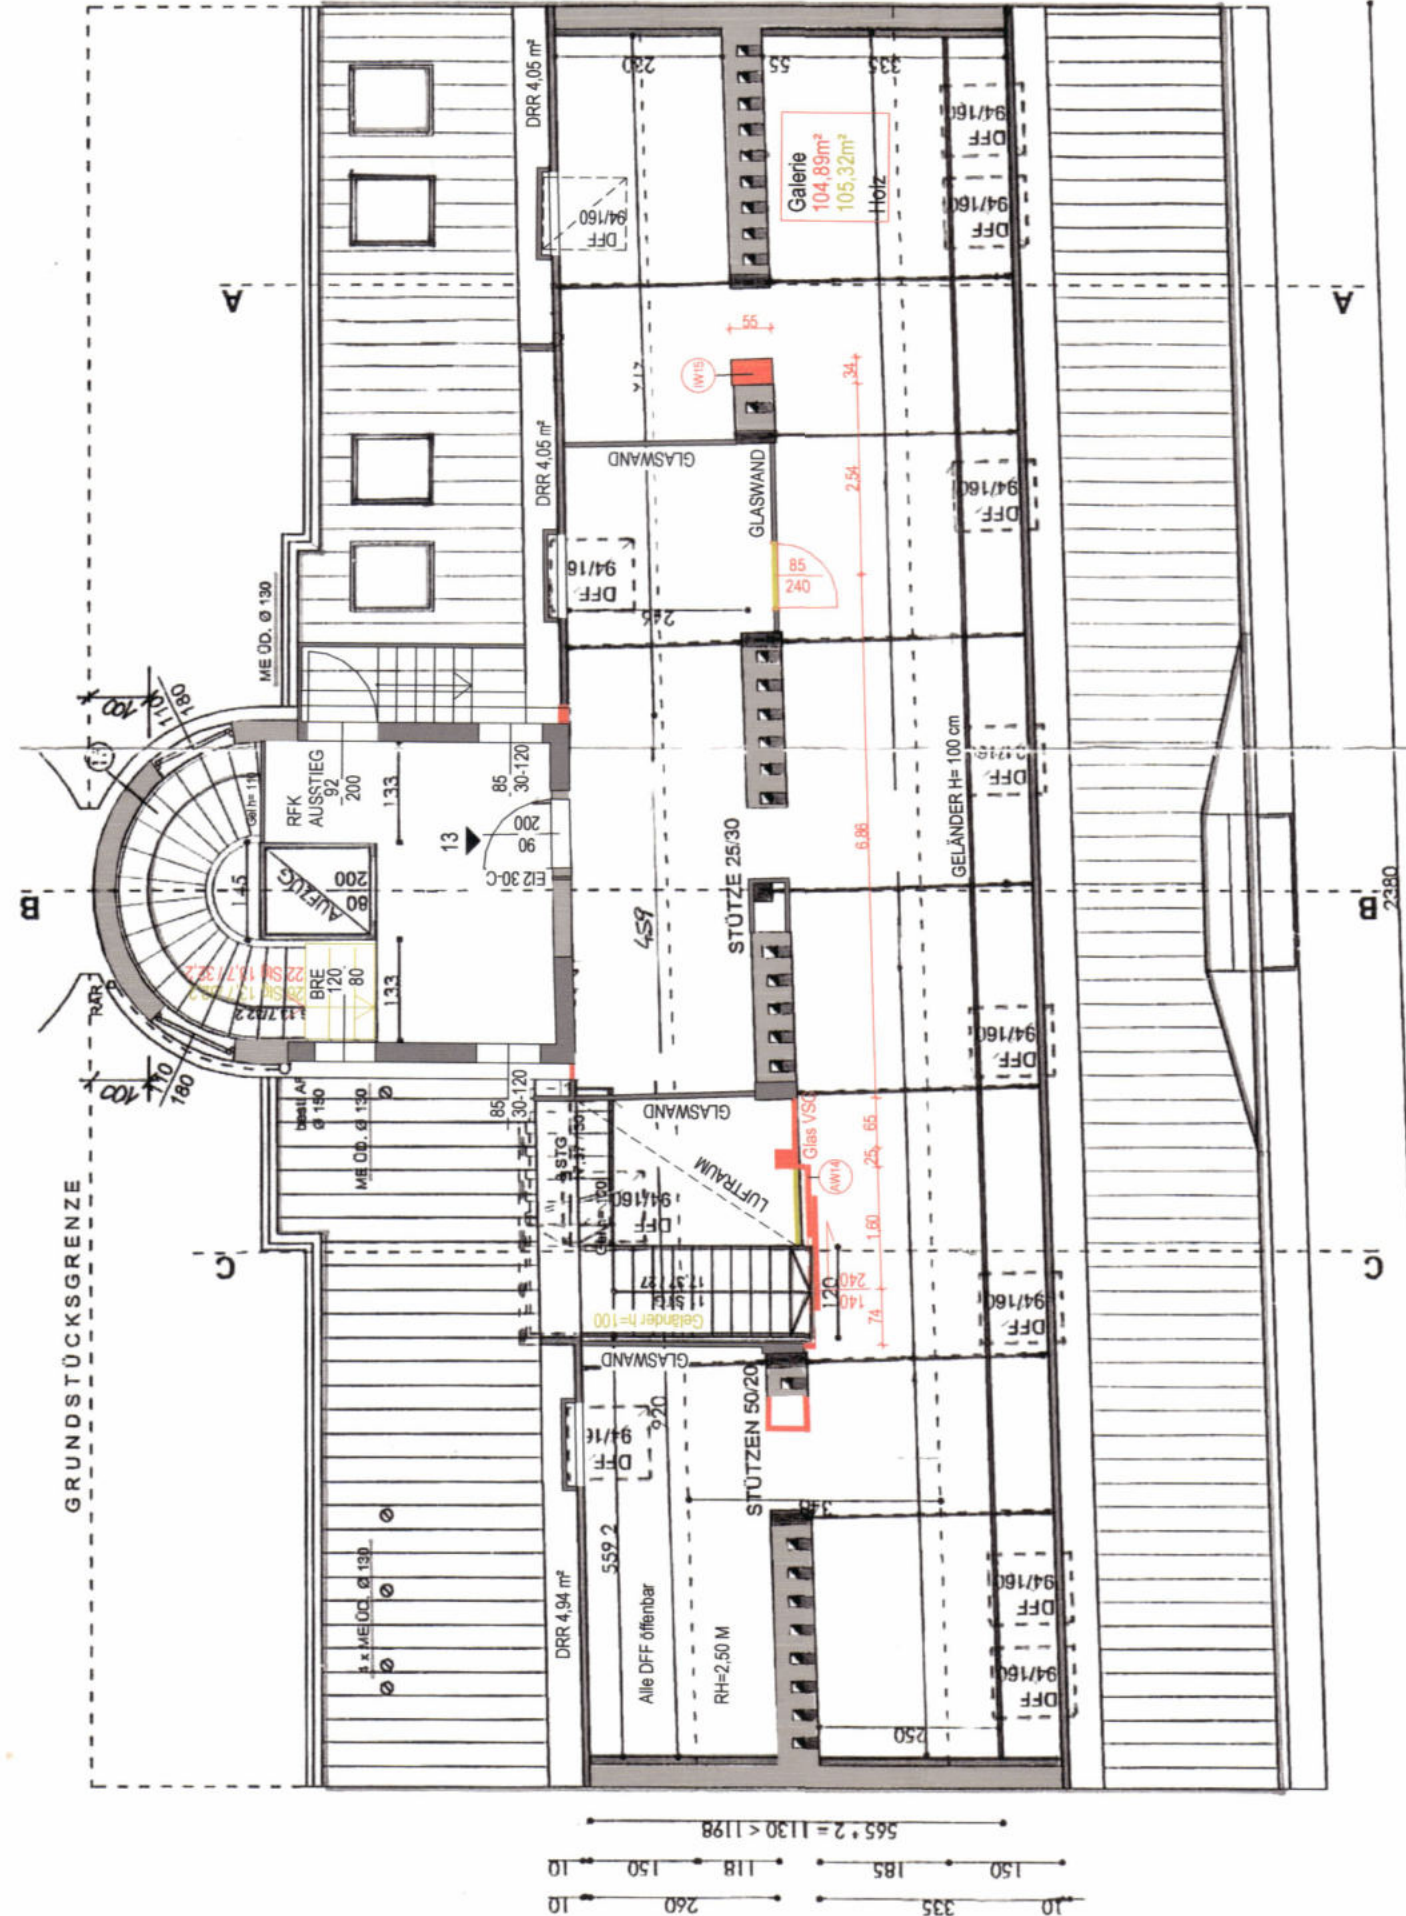

Galerie

AW14 Glas VSG	6,00 cm	IW15	Putz einlagic	24,00 cm	IW24	2,50 cm	1,25 cm
Glas	6,00 cm	Ziegel	50,00 cm	GKB	UK dazw. Mineralwolle	7,50 cm	7,50 cm
IW01	1,25 cm	Putz einlagic	55,00 cm	GKB		1,25 cm	10,00 cm
GKB	7,50 cm	IW16	Metallgitterwand	VS02	Dampfbremse	1,25 cm	1,25 cm
UK dazw. Mineralwolle	10,00 cm	IW17	Putz zwelagic	GKB	UK dazw. Mineralwolle	0,80 cm	10,00 cm
IW02	1,25 cm	NF Ziegel	73,00 cm		Gesamt	269,40	cm
GKB	1,25 cm	Putz zwelagic	2,50 cm				
UK dazw. Mineralwolle	1,25 cm	IW18	15,00 cm				
GKB	15,00 cm	Putz zwelagic	1,50 cm				
IW03	1,25 cm	Ziegel	15,00 cm				
GKB	1,25 cm	Putz zwelagic	18,00 cm				
UK dazw. Mineralwolle	1,25 cm	IW19	2,00 cm				
GKB	1,25 cm	Ziegel	17,00 cm				
IW08	20,00 cm	Putz zwelagic	2,00 cm				
Putz	2,00 cm						
Ziegel	20,00 cm						
Putz	2,00 cm						


Aufbauten

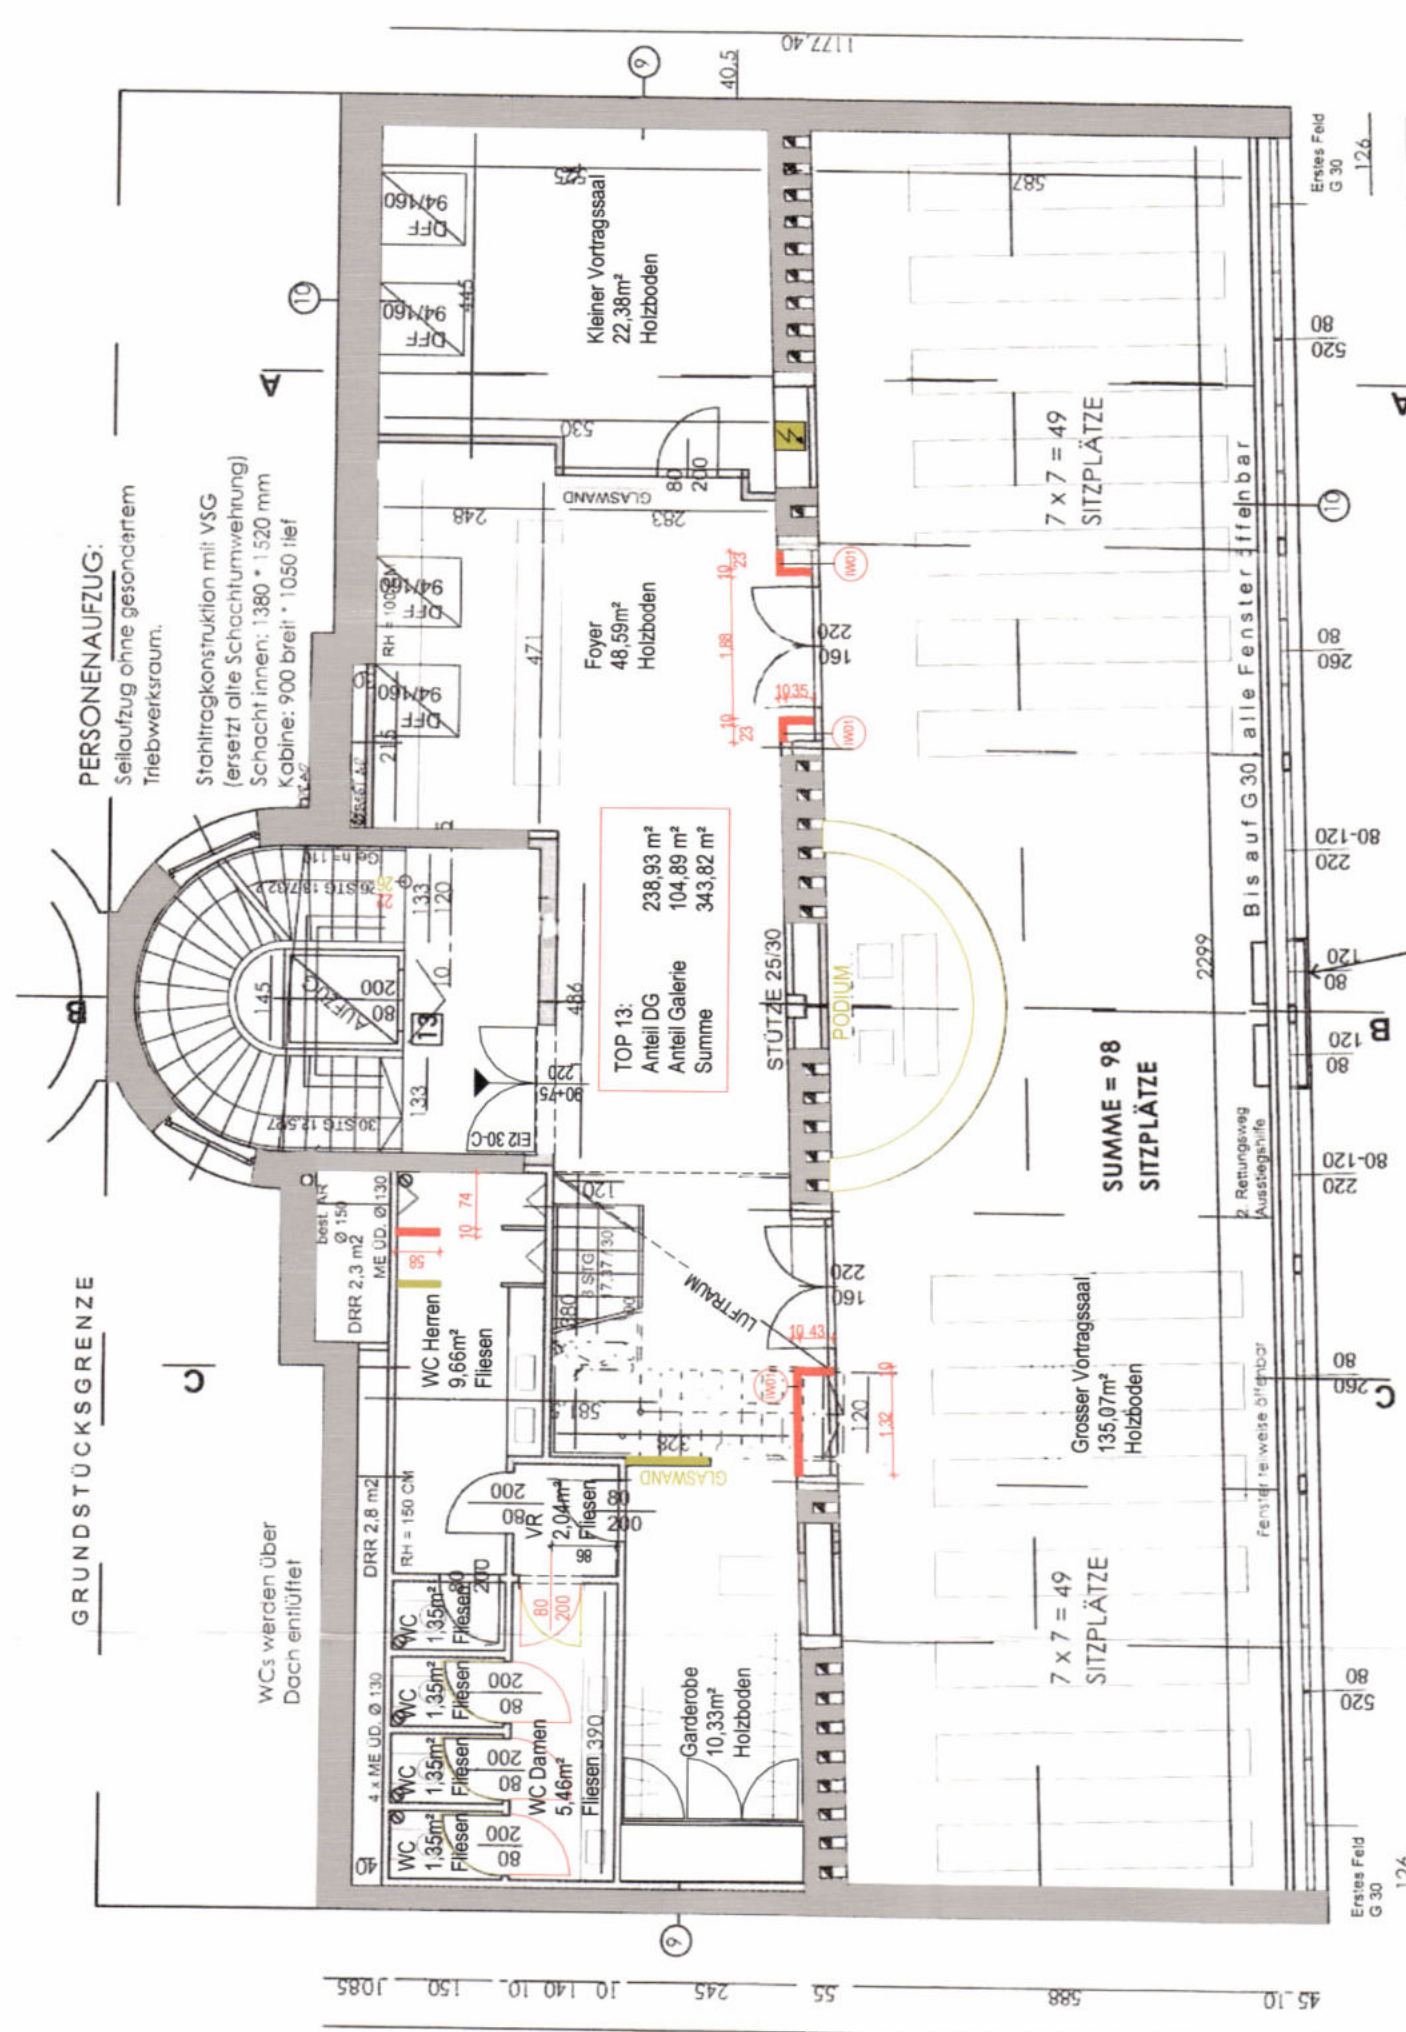


1. Stock




2. Stock

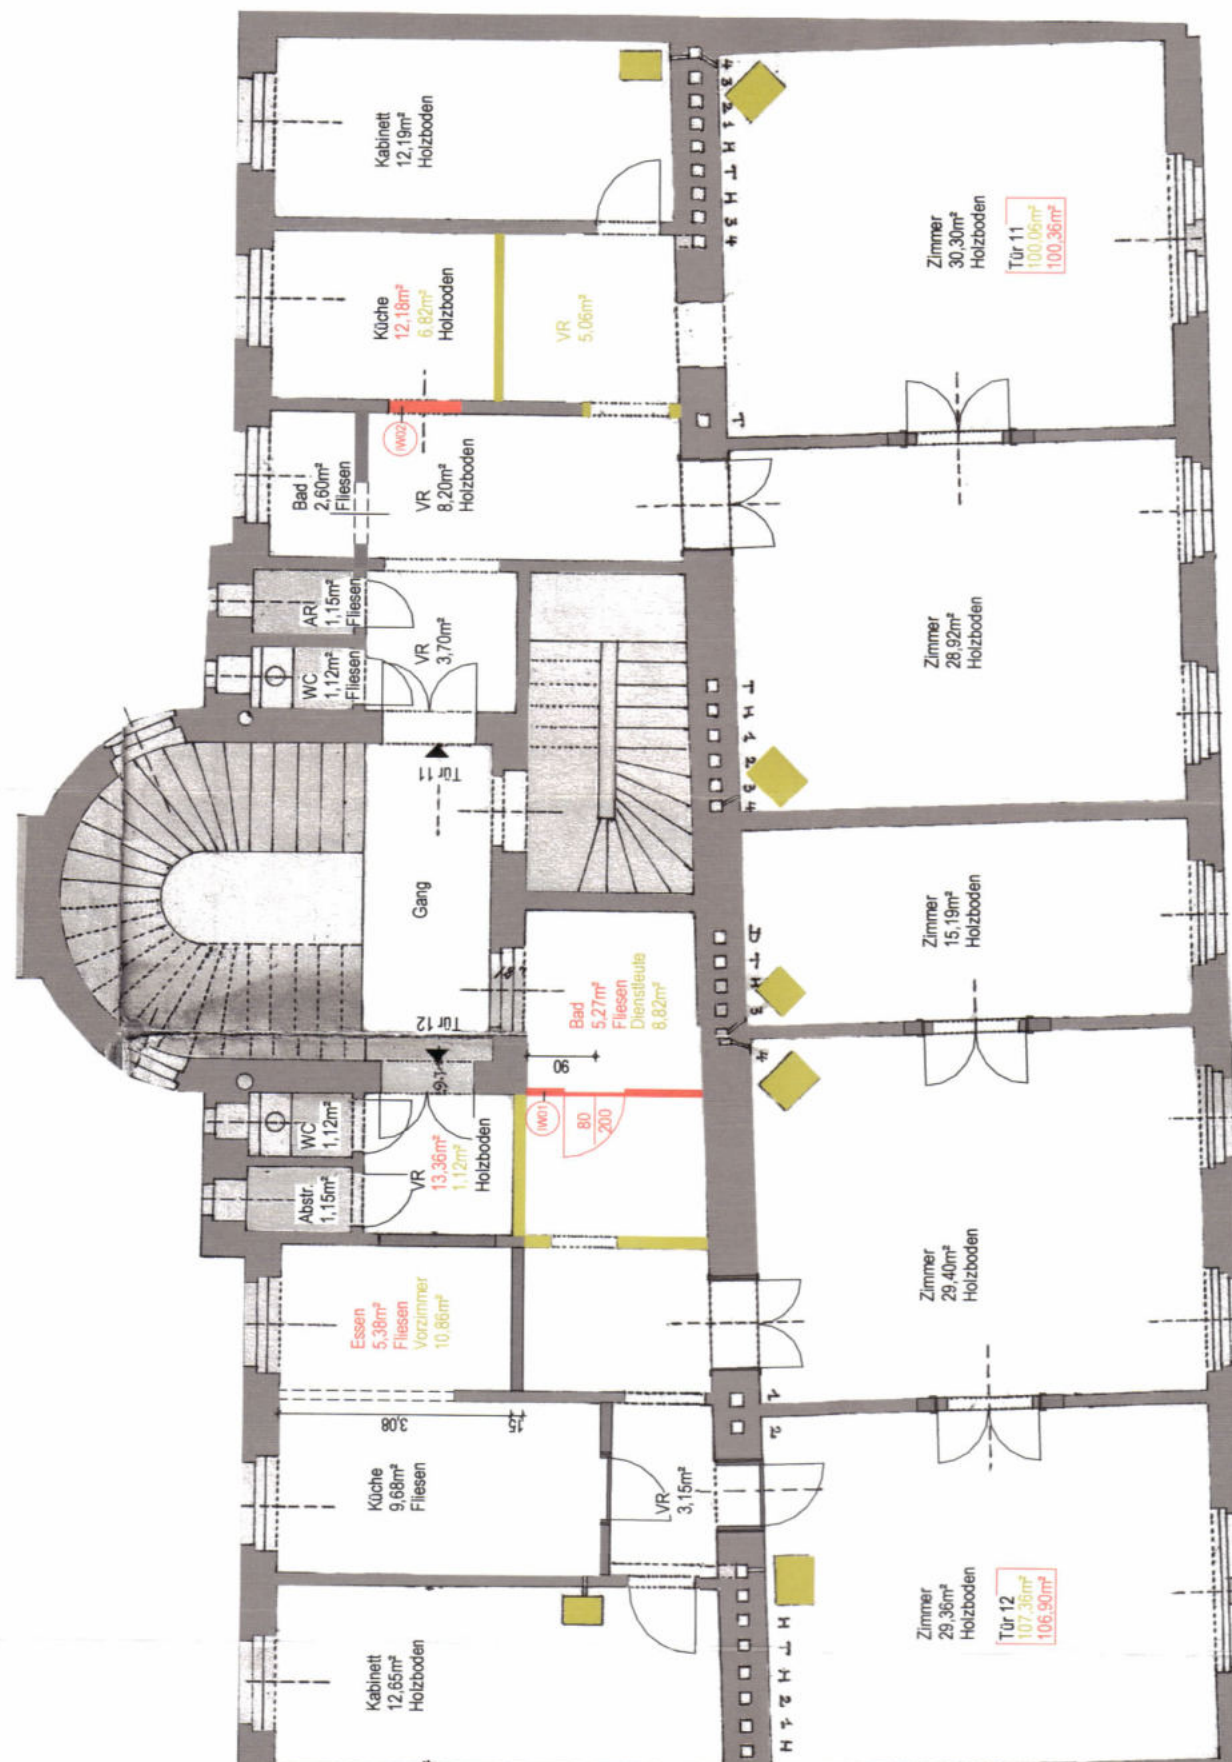


3. Stock

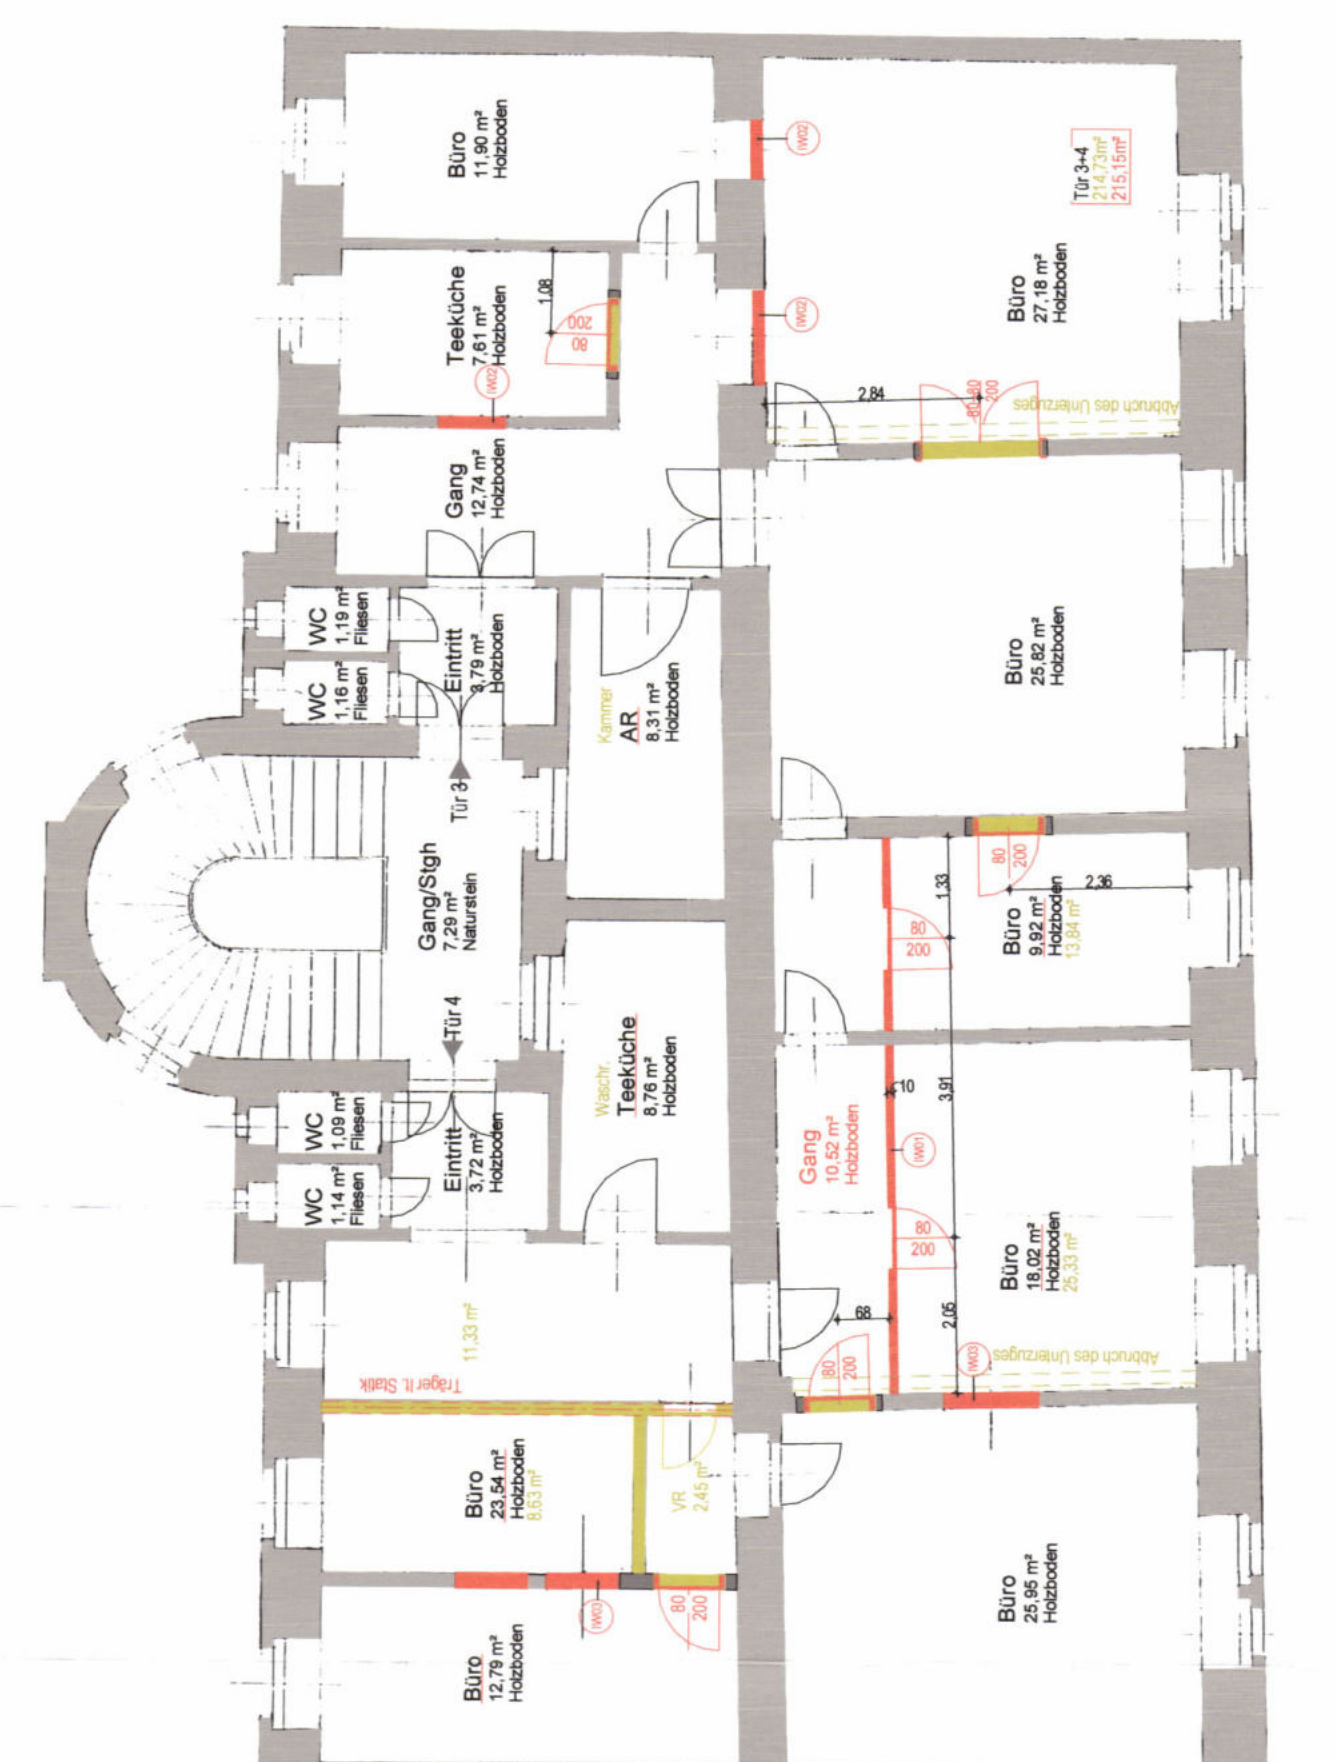


4. Stock

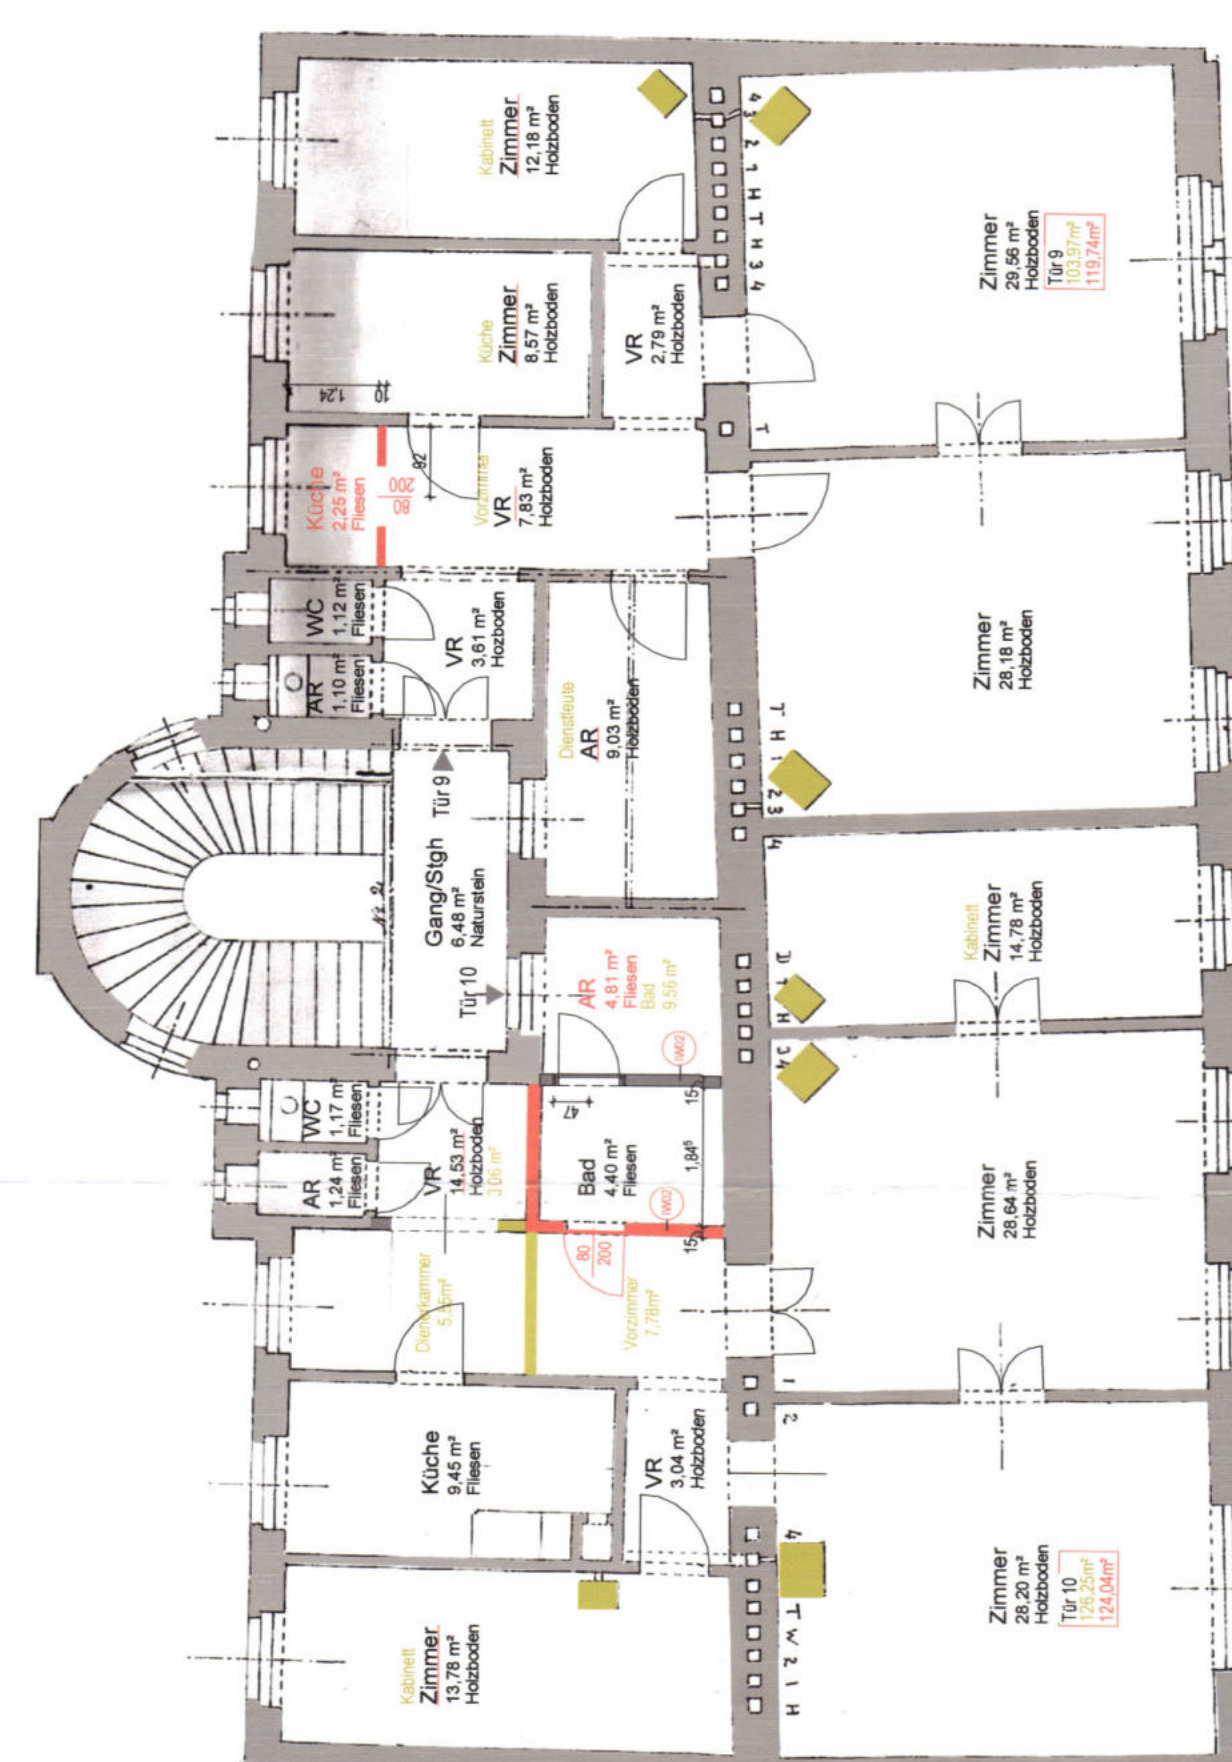


5. Stock

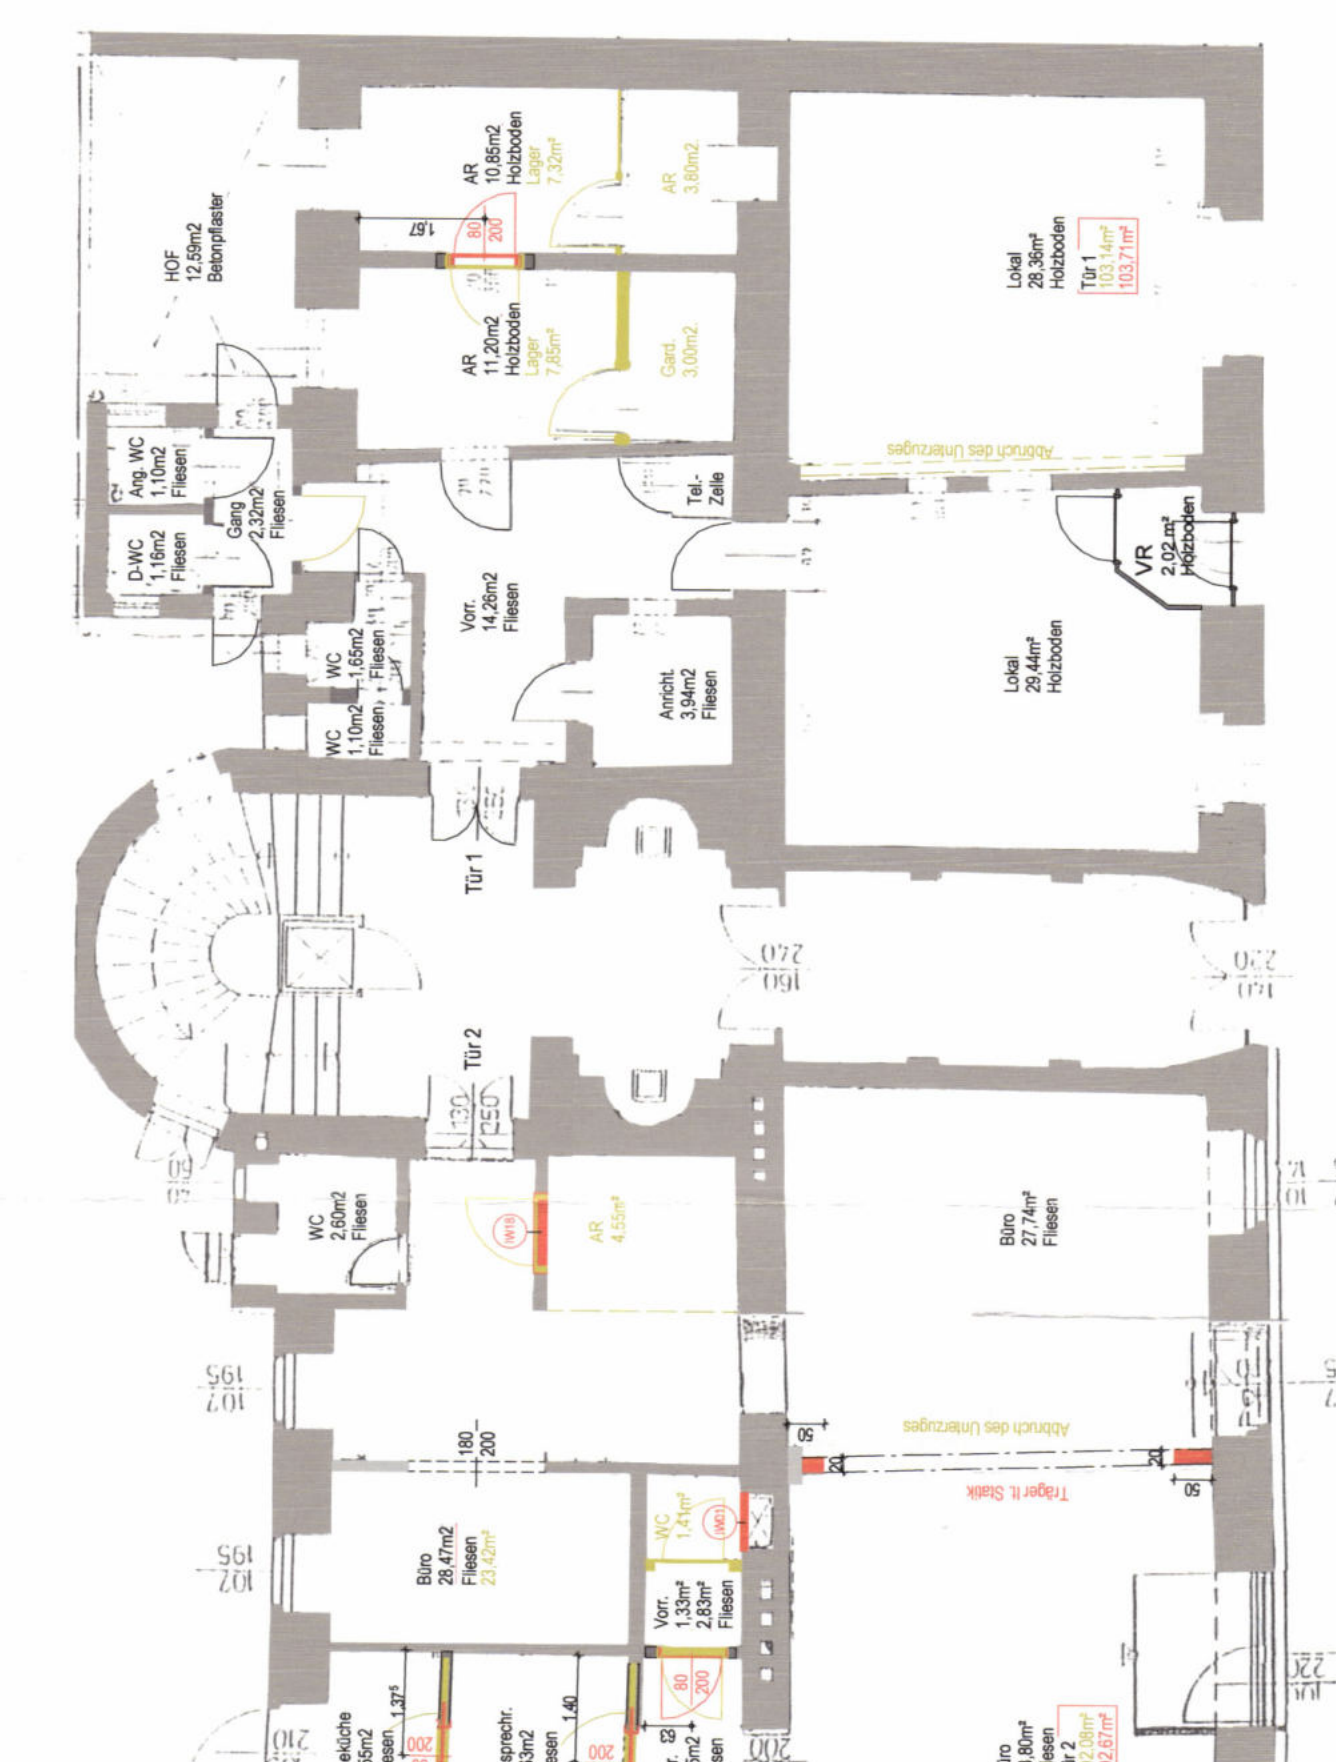

6. Stock

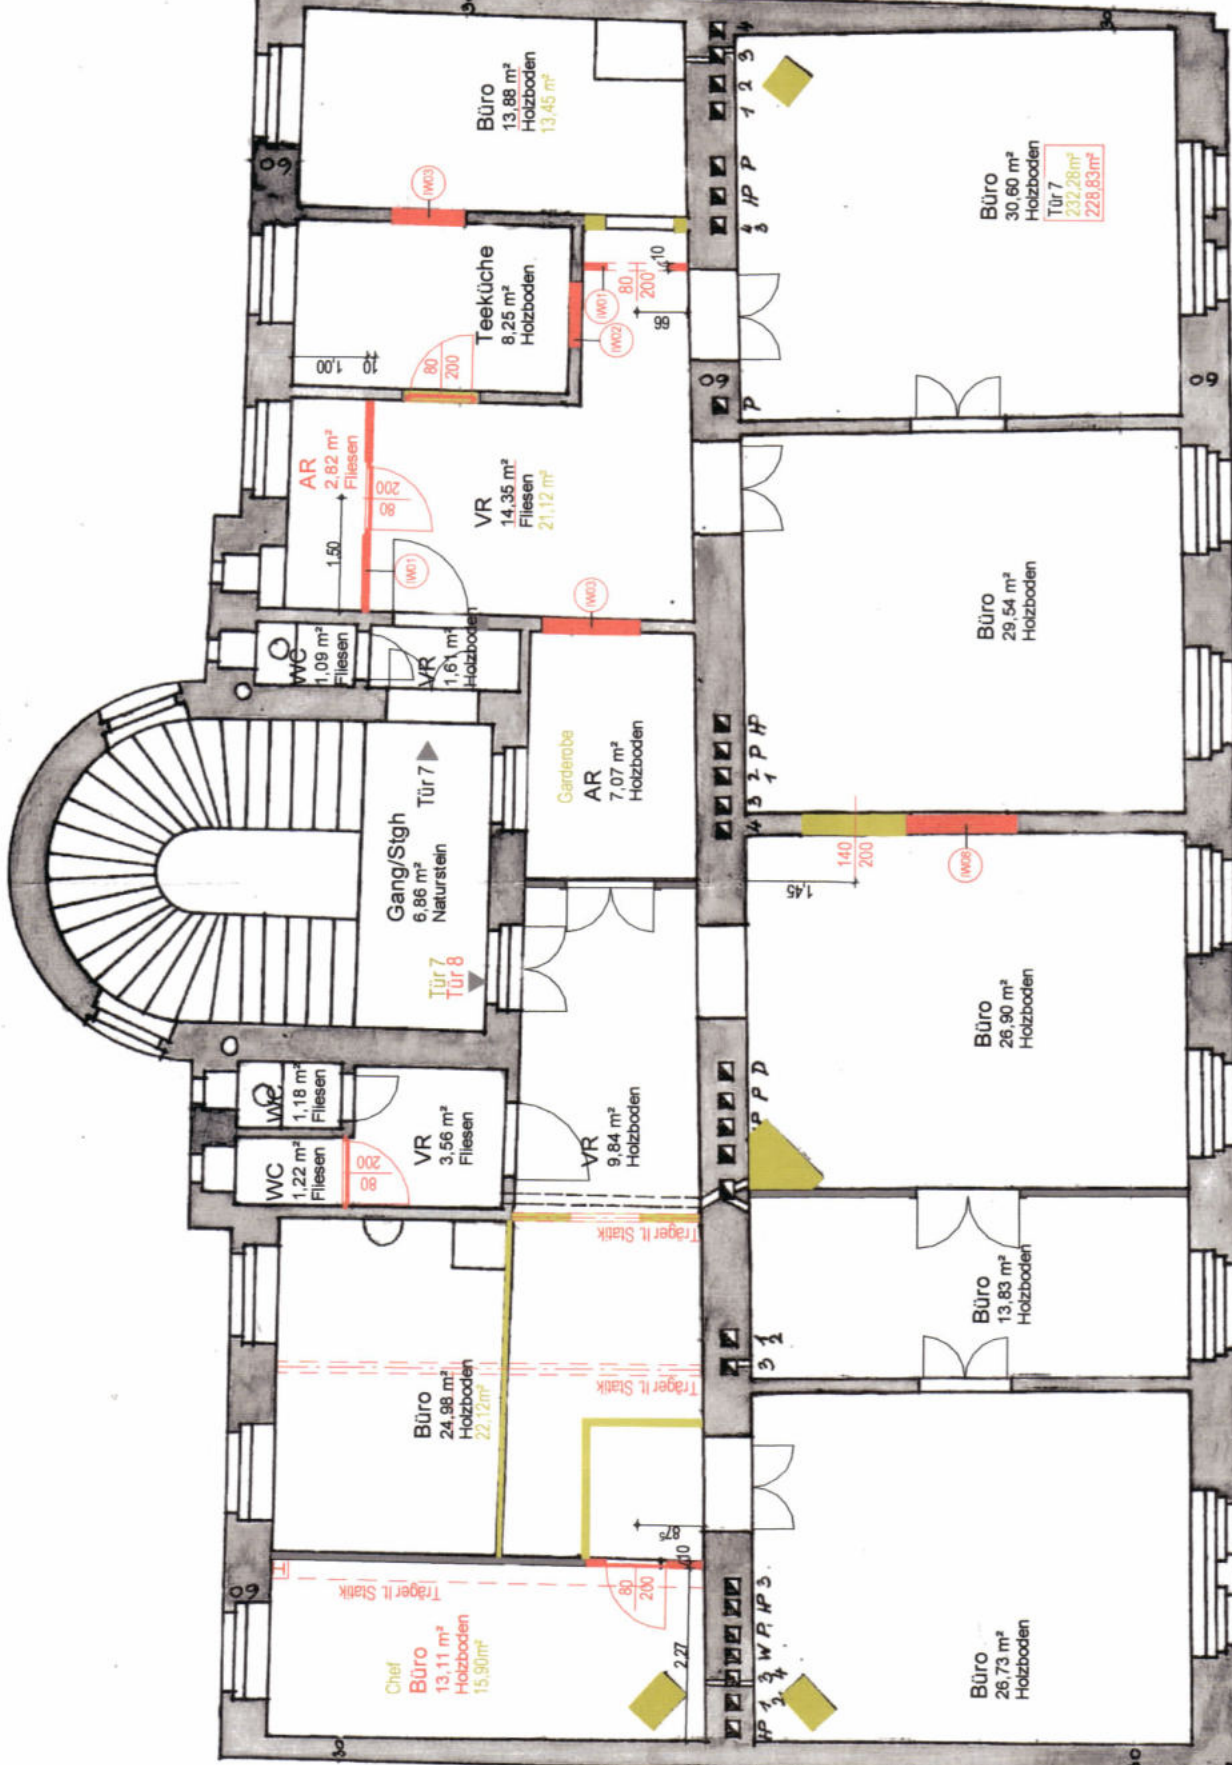

7. Stock

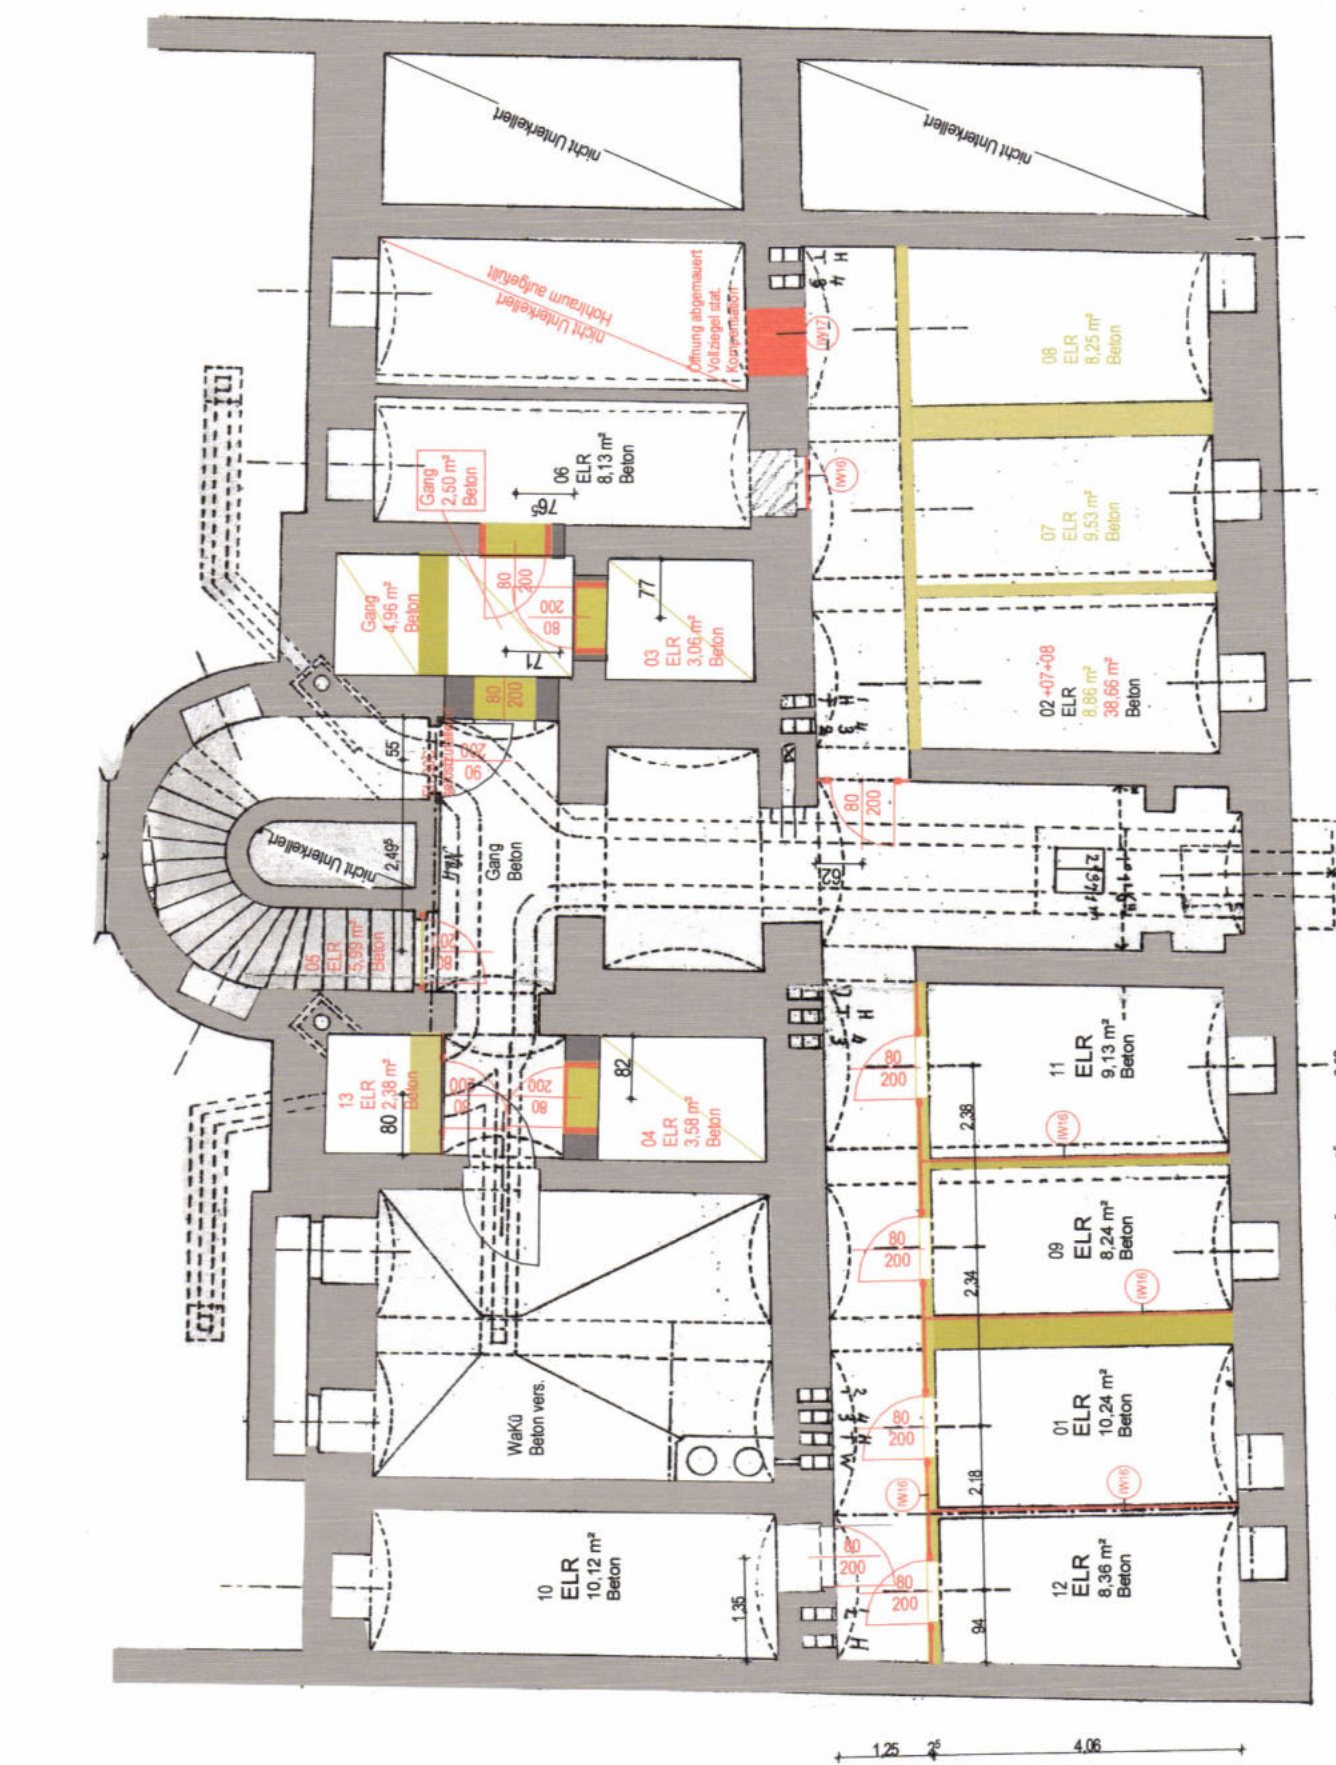

8. Stock

Legende:

- Bestand
- Abbruch
- Neu

Schadenstoffklasse: CC1

Alle innenliegenden Räume werden mechanisch be- und entlüftet.

In den Sanitärbereichen werden imprägnierte Gipskartonplatten verwendet.

In den Sanitärbereichen wird zur Abdichtung ein Hochtrag von 15 cm ausgeführt.

Alle Geländer mind. 1,00 m über FFKK.

Alle Geländer ab einer Absturzhöhe von 12 m mind. 1,1 m über FFKK.

Alle Geländer bei Türen, Fenstern und Flurwänden bis 1,50 m in ESG, bei Durch- und Absturzöffnungen VSG.

Einreichplan

EZ: 894 GST.NR.: 1526/2, KG: 01004 Innere Stadt

Objekt / Ansichten um:

bauliche Änderungen

Landesgerichtsstr. 6

1010 Wien

Planinhalt:

Lageplan

Grundrisse KG, TP,

HP, 1. Stock, 2. Stock,

3. Stock, DG, Galerie

Plannummer

P0420-LAN-EP-001-A

Parie

A / B / C / D

Malsch

1:100


15.03.2018

Plangröße

155 cm x 43 cm

Bauwerferin

Grundstückseigenümerin

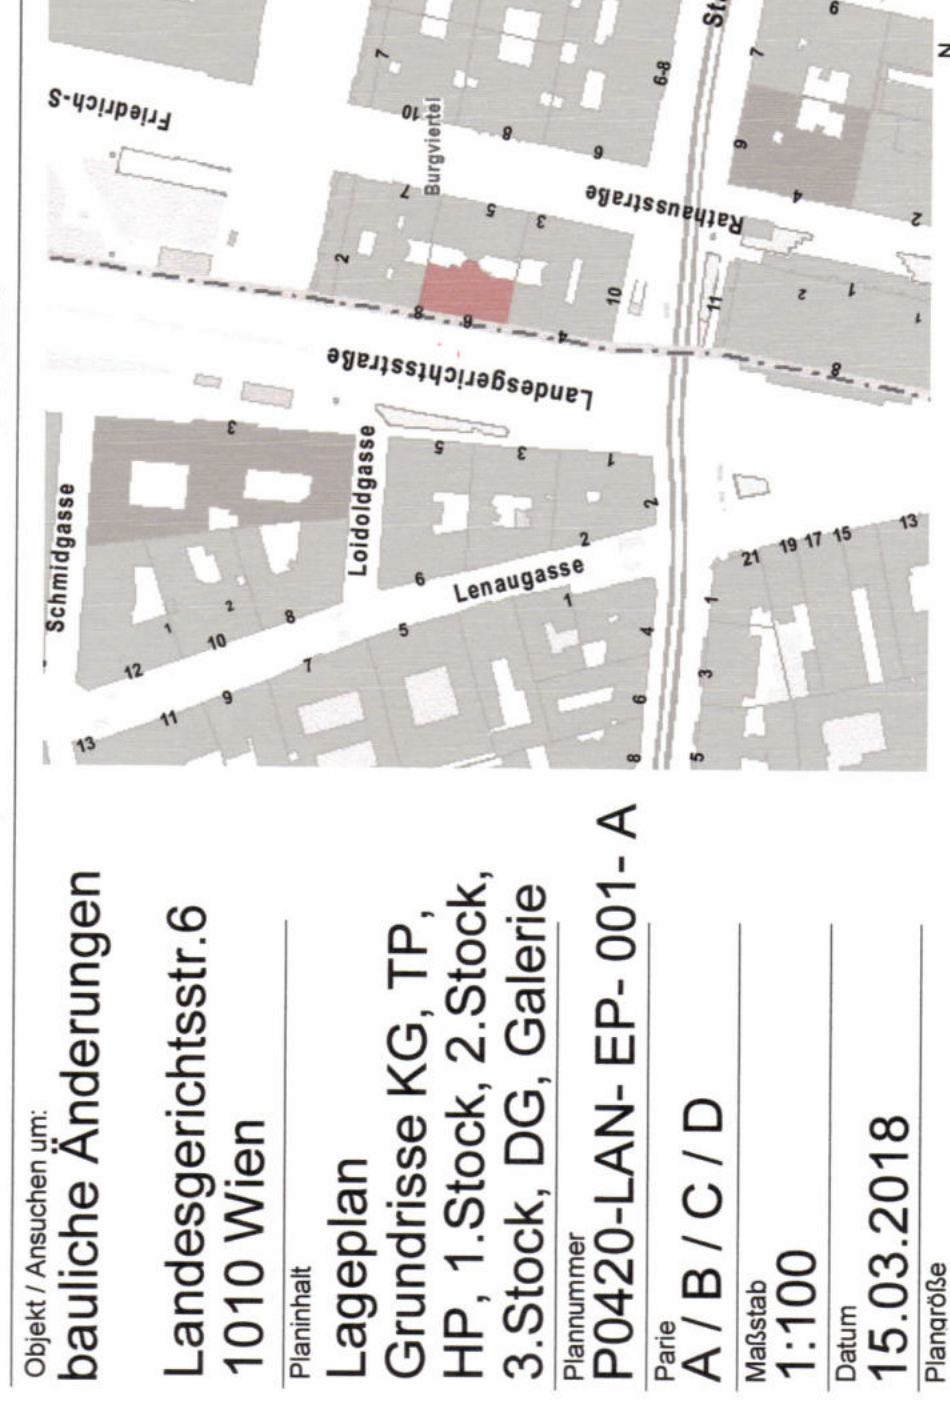

Zentralfond der Hausbesitzer
Kommunikationsverein
1010 Wien, Landesgerichtsstrasse 6
Tel. 01 406 33 18 Fax 01 406 53 49
ZVR 187843163 ATU 9962708

Bauwerkstatt der Stadt Wien
Magistratsabteilung 37 - Baupolizei
Gebietssgruppe Ost, Stadterneuerung 1
Zl: MA37/438141-2018-1

B+C Baubetriebs GmbH
A-1010 Wien, Leopoldgasse 7
Tel. 01 406 33 18 Fax 01 406 53 49
ZVR 187843163 ATU 9962708

BAUWERKSTATT
A-1010 Wien, Leopoldgasse 7
Tel. 01 406 33 18 Fax 01 406 53 49
ZVR 187843163 ATU 9962708

Planverfasserin
Manuela Giesmayr
Architektin
Wien, 15.3.2018

baukult
... der Stoff aus dem realitäten sind!

Architektin
Manuela Giesmayr
Architektin
Wien, 15.3.2018

Architektin
Manuela Giesmayr
Architektin
Wien, 15.3.2018