

Adresse:

1., Wien, Landesgerichtsstraße 6

MA37
BAUPOLIZEI
SICHER BAUEN

Stadt Wien

EZ / KG:

EZ 894, KG Innere Stadt
(01004), Gst.Nr. 1526/2

BEARBEITUNGSBOGEN

§62

Zahl MA 37/881097-2018-1

Eingereicht am: 15.10.2018

Stiege / Stock / Tnr. EG / Top1

Art der Bauführung (gem.: § 62 Abs.1):

Produkte:
Bauanzeigen (Sonstige Bauführung -§62(1)Z4)

☒ Schutzzone

☐ Badeinbau (Ziff. 1)

☐ Loggienverglasung (Ziff. 2)

☐ Fenster- / -türtausch (Ziff. 3)

☒ baul. Änderung (Ziff. 4)

Stat. Vorbemessung erforderlich?

Nein ☒
Ja ☐

☒ Bauanzeige vollständig belegt - frühest möglicher Baubeginn am:

15.10.2018

Schutzzone (Ziff. 1, 2, oder 3) bzw. erf. Vorstatik (Ziff. 4) berücksichtigt!

☐ Baubeginnsanzeige liegt vor - angezeigter Baubeginn möglich? Ja ☐
Nein ☐

☐ Bauanzeige unvollständig belegt

Verbesserungsauftrag am:

Frist:

Vollständig belegt am:

☐ Bauanzeige bleibt unvollständig belegt, daher Zurückweisung erforderlich

AV vom: 25.10.2018

Die Bauanzeige wurde im Sinne der Bestimmungen der §§ 67 Abs. 1 und 62 Abs. 1 BO geprüft.

☒ Es liegt kein Untersagungsgrund vor. ☒ § 70 ☐ § 70 in Verb. mit § 68 ☐ § 71

EUR 28.- VA mit eBezahlen vorschreiben

30 OKT. 2018

Die Sachbearbeiterin:

Ing.ⁱⁿ Werner

Für den Abteilungsleiter:

29.10.

Bauführer/in: REAL INTERIO GMBHWien, 27.2.2020

Schönbrunnerstraße 88A/6

A-1050 Wien

Tel.: +43 (01) 81 00 588

Fax: +43 (01) 81 02 746

Bauvorhaben:UMB AU TOP 1

(Gegenstand)

(Geschäftszahl der ursprünglichen Baubewilligung)

LANDESGERICHTSSTR. 6, 1010 WIEN

(Adresse)

STEH-GAST GMBH

(BauwerberIn)

GZ: MA37/881097-2018-1**Erklärung des/r Bauführers/in zur Fertigstellung**

- ☒ **Gemäß § 62 Abs. 7 BO**
(nach Bauanzeige gem. § 62 Abs. 1 Z 1 bis 3)
- ☒ **Gemäß § 128 Abs. 3 bzw. 3a BO**
(nach Baubewilligung bzw. Bauanzeige gem. § 62 Abs. 1 Z 4)

Es wird erklärt, dass das o.a. Bauvorhaben der Baubewilligung/ Bauanzeige und den Bauvorschriften entsprechend ausgeführt wurde.

- ☐ **Weiters wird bestätigt, dass die vorgenommenen Abänderungen, die nun im Rahmen der Fertigstellungsanzeige/-meldung durch farbliche Ersichtlichmachung in den Ausführungsplänen bekannt gegeben werden, den Umfang des § 73 Abs. 3 nicht überschreiten.**
- ☐ **Darüber hinaus wird das Erreichen der erforderlichen Zuverlässigkeit der Tragwerke gemäß § 128 Abs. 2 Z 2 und Z 2a bestätigt.**

REAL INTERIO GMBH

Schönbrunnerstraße 88A/6

A-1050 Wien

Tel.: +43 (01) 81 00 588

Fax: +43 (01) 81 02 746

(Bauführer/in, Stempel / Unterschrift)

Wichtige Hinweise umseitig!

EINREICHPLAN §62

für bauliche Änderungen im
Souterrain - Cafe Bendl
auf der Liegenschaft
Landesgerichtsstraße 6, 1010 Wien


KAT. GEMEINDE: Innere Stadt - 01004	GST-NR.: 1526/2	EZ: 894	PARIE A B C D
PLANINHALT: GRUNDRISS: EG EG SOUTERRAIN M 1:100 Flächenaufstellung Legende			
BAUWERBER: Steh-Gast Gastronomie- betriebsstätten GmbH Landesgerichtsstraße 6 1010 Wien Steh-Gast Gastronomiebetriebsstätte Ges.m.b.H. Landesgerichtsstr. 6 1010 Wien Tel / Fax: +43 (1) 890 41 05 Wien, 29.10.2018 cafe.bendl@gmx.at		Magistrat der Stadt Wien Magistratsabteilung 37 - Baupolizei Gebietsgruppe Ost, Stadterneuerung 1 Zl.: MA37/881097-2018-1 Dieses Bauvorhaben gilt als gem. § 70 BO bewilligt. MA37 BAUPOLIZEI SICHER BAUEN Stadt Wien Für den Abteilungsleiter: Dipl.-Ing. Fischer Oberstadtbaurat 	
PLANVERFASSER:  PROFESSOR DIPL. ING. DR. TECHN. GERHARD KRAML ZIVILINGENIEUR FÜR BAUWESEN 1020 WIEN, CASTELLEZGASSE 15 FAX 01/219 73 01		BAUFÜHRER: REAL INTERIO GMBH Schönbrunnerstraße 88A/6 A-1050 Wien Tel.: +43 (01) 81 00 588 Fax: +43 (01) 81 02 746	
GEZ. KH	PLAN NR. LAND/07/2018	VERSION 002	DATUM 30.07.2018

Landesgerichtsstraße


Flächenaufstellung

Legende

Neu	Alt
Lokal 1 25,91 m²	Lokal 1 25,91 m²
Lokal 2 27,93 m²	Lokal 2 27,93 m²
Gang 13,59 m²	Gang 13,59 m²
Anrichte 3,80 m²	Anrichte 3,80 m²
VR 1,61 m²	VR 1,61 m²
WC H 1,13 m²	WC H 1,13 m²
Gang 2,10 m²	Gang 2,10 m²
WC D 1,42 m²	WC D 1,42 m²
WC Pers. 1,30 m²	WC Pers. 1,30 m²
Lokal 3 23,67 m²	Lokal 3 23,67 m²
Summe 102,46 m²	Summe 101,08 m²

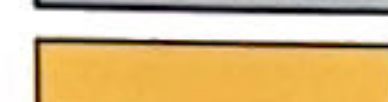	Bestand
	Abbruch
	Neu
	Stahl

ENTWÄSSERUNG: ABWASSERBESEITIGUNG INNENLIEGEND ÜBER IM FUSSBODEN VERLEGTES ZUGELASSENES PVC-HART-KANALROHR DN 125, GEFÄLLE 1,5% SCHALLISOLIERT UMMANTELT
BELÜFTUNG: WCs SIND ÜBER FENSTER ENTLÜFTET

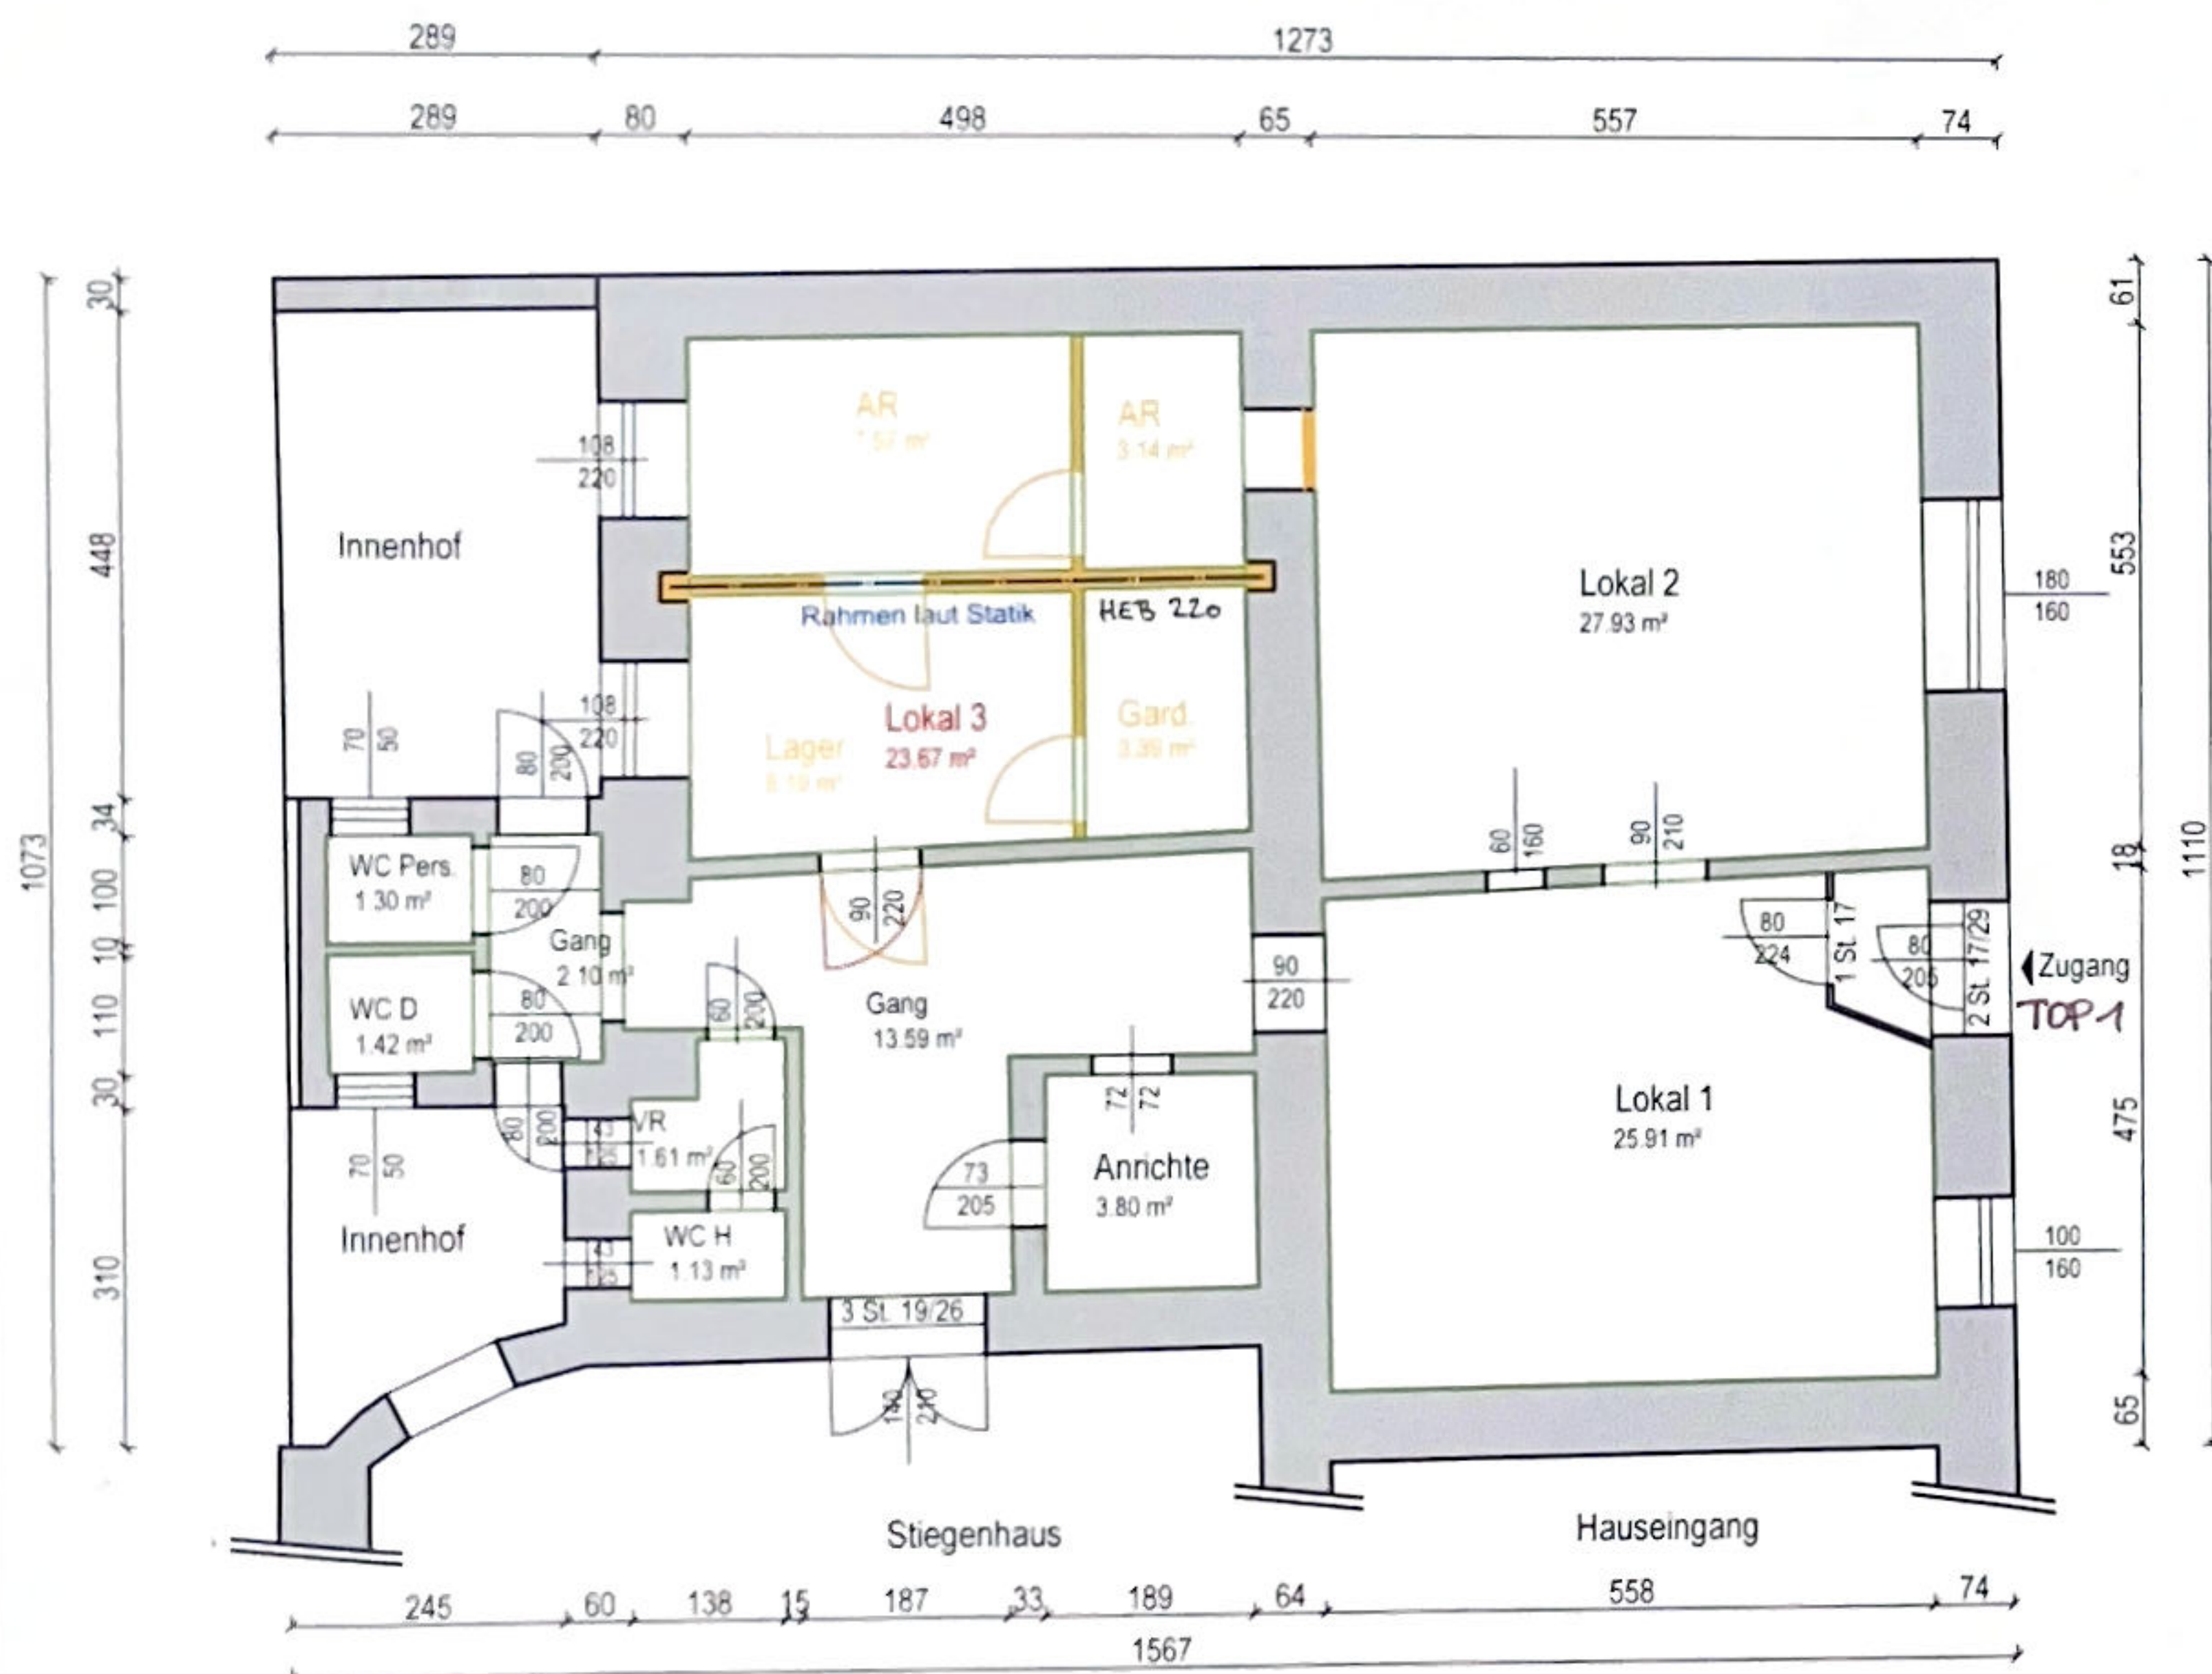

EINREICHPLAN §62

für bauliche Änderungen im
Souterrain - Cafe Bendl
auf der Liegenschaft
Landesgerichtsstraße 6, 1010 Wien

KAT. GEMEINDE: Innere Stadt - 01004	GST-NR.: 1526/2	EZ: 894	PARIE ☒ A ☐ B ☐ C ☐ D
--	-----------------	---------	---

PLANINHALT:

GRUNDRISS: EG SOUTERRAIN M 1:100
Flächenaufstellung
Legende

BAUWERBER:

Steh-Gast Gastronomie-
betriebsstätten GmbH
Landesgerichtsstraße 6
1010 Wien
Steh-Gast
Gastronomiebetriebsstätte
Ges.m.b.H.
Landesgerichtsstr. 6 1010 Wien
Tel / Fax: +43 (0) 1 890 41 05 Wien, 29.10.2018
cafe.bendl@gmx.at

Magistrat der Stadt Wien
Magistratsabteilung 37 - Baupolizei
Gebietsgruppe Ost, Stadterneuerung 1

Zl.: MA37/881097-2018-1

Dieses Bauvorhaben gilt als gem. § 70 BO bewilligt.

Für den Abteilungsleiter:
Dipl.-Ing. Fischer
Oberstadtbaurat

PLANVERFASSER:

PROFESSOR
DIPL.-ING. DR. TECHN. GERHARD
KRAML
ZIVILINGENIEUR FÜR BAUWESEN
1020 WIEN, CASTELLEZGASSE 15
FAX 01/219 73 01

BAUFÜHRER:

REAL INTERIO GMBH
Schönbrunnerstraße 88A/6
A-1050 Wien
Tel.: +43 (0) 1 81 00 588
Fax: +43 (0) 1 81 02 746

GEZ. KH	PLAN NR. LAND/07/2018	VERSION 002	DATUM 30.07.2018
------------	--------------------------	----------------	---------------------