

Klimagerät:
TOSHIBA Multisplit R32
Modell:
RAS-SM34U2AVG-E
Abmessung:
890 x 900 x 320
Kühlleistung:
10 kW
Heizleistung:
12 kW
Kältemittel:
R32
Kältemittelmenge:
2,39 kg
Energieeffizienzklasse
A++
Schalldruckpegel heizen
55,0 dB(A)
Schalldruckpegel kühlen
52,0 dB(A)
Betriebszeit:

Bestand

Abbruch

Neu

Anrainerverzeichnis
kein Wohnungseigentum
Wohnungseigentum

Legende

Magistratsabteilung 37
Zahl: 60374/18-9
EING: 08. Aug. 2019
AUSGANG: 19. Aug. 2019

Einreichplan

EZ: 894, GST.NR.: 1526/2, KG: 01004 Innere Stadt

Objekt / Ansuchen um:
Errichtung eines Klimagerätes

Landesgerichtsstr. 6
1010 Wien
Planinhalt
Grundriss Hochparterre
Schnitt 1
Hoffassade

Planummer
P0420-LAN-EP-02-A

Partie
A / B / C / D

Maßstab
1:100, 1:2000

Datum
24.04.2019

Plangröße
85 cm x 40 cm

Bauwerber/in

Zentralverband der Hausbesitzer
Hausbesitzershilfsverein
1010 Wien, Landesgerichtsstraße 6
Tel. 01/406 38 11 Fax 01/406 32 48
ZVR 187843168 KIU 58062708

Magistratsabteilung 37 - Baupolizei
Baubehörde
ZL: MA37/603974-2019-1

Bauführer/in
Hinauf bezieht sich der Bauchied
ZL: MA37/603974-2019-1
Hinauf bezieht sich der Bauchied
Wien, 25.11.2019
Planverfasser/in
INNOVOLUTION
KÄLTE- und KLIMA-TECHNIK
IMMOBILIEN- und BAU-ANLAGEN-GEHÄU
1010 Wien, Landesgerichtsstraße 47

baukult
der stoff aus dem realitäten sind

baukult ZT GmbH
Architektin Dr. Regina M. Leitner
Karl-Ludwig-Str. 1
1040 Wien
Tel. +43 1 5247857 10
www.baukult.at

Anrainerverzeichnis

Eigentümervverzeichnis aus der Katastralgemeinde: Innere Stadt (01004)

Eintragszahl Lauf.Nr. Anteil Eigentümer (Geburtsdatum), Eigentümeradresse

892 1 1/1 Johann Wilhelm Ritter von Mannagetta'sche Stiftung

Letzte Tagebuchzahl: 4067/2018 Bezirksgericht: Innere Stadt Wien (010)

894 3 1/1 Zentralverband der Hausbesitzer - Hausbesitzershilfsverein

1010 Landesgerichtsstr. 6, Österreich

Letzte Tagebuchzahl: 6355/2018 Bezirksgericht: Innere Stadt Wien (010)

896 1 1/1 Vereinigte Staaten von Amerika

1090 Botschaft der USA, Bundesgasse 16, Österreich

Letzte Tagebuchzahl: 4432/1948 Bezirksgericht: Innere Stadt Wien (010)

1535 1 1/1 Richard Adria. May (1862-03-03)


1010 Rathausstr. 5, Österreich

Letzte Tagebuchzahl: 8839/2016 Bezirksgericht: Innere Stadt Wien (010)

1793 1 1/1 Stadt Wien (Öffentliches Gut)

1082 Rathaus, Österreich

Letzte Tagebuchzahl: 3554/2019 Bezirksgericht: Innere Stadt Wien (010)

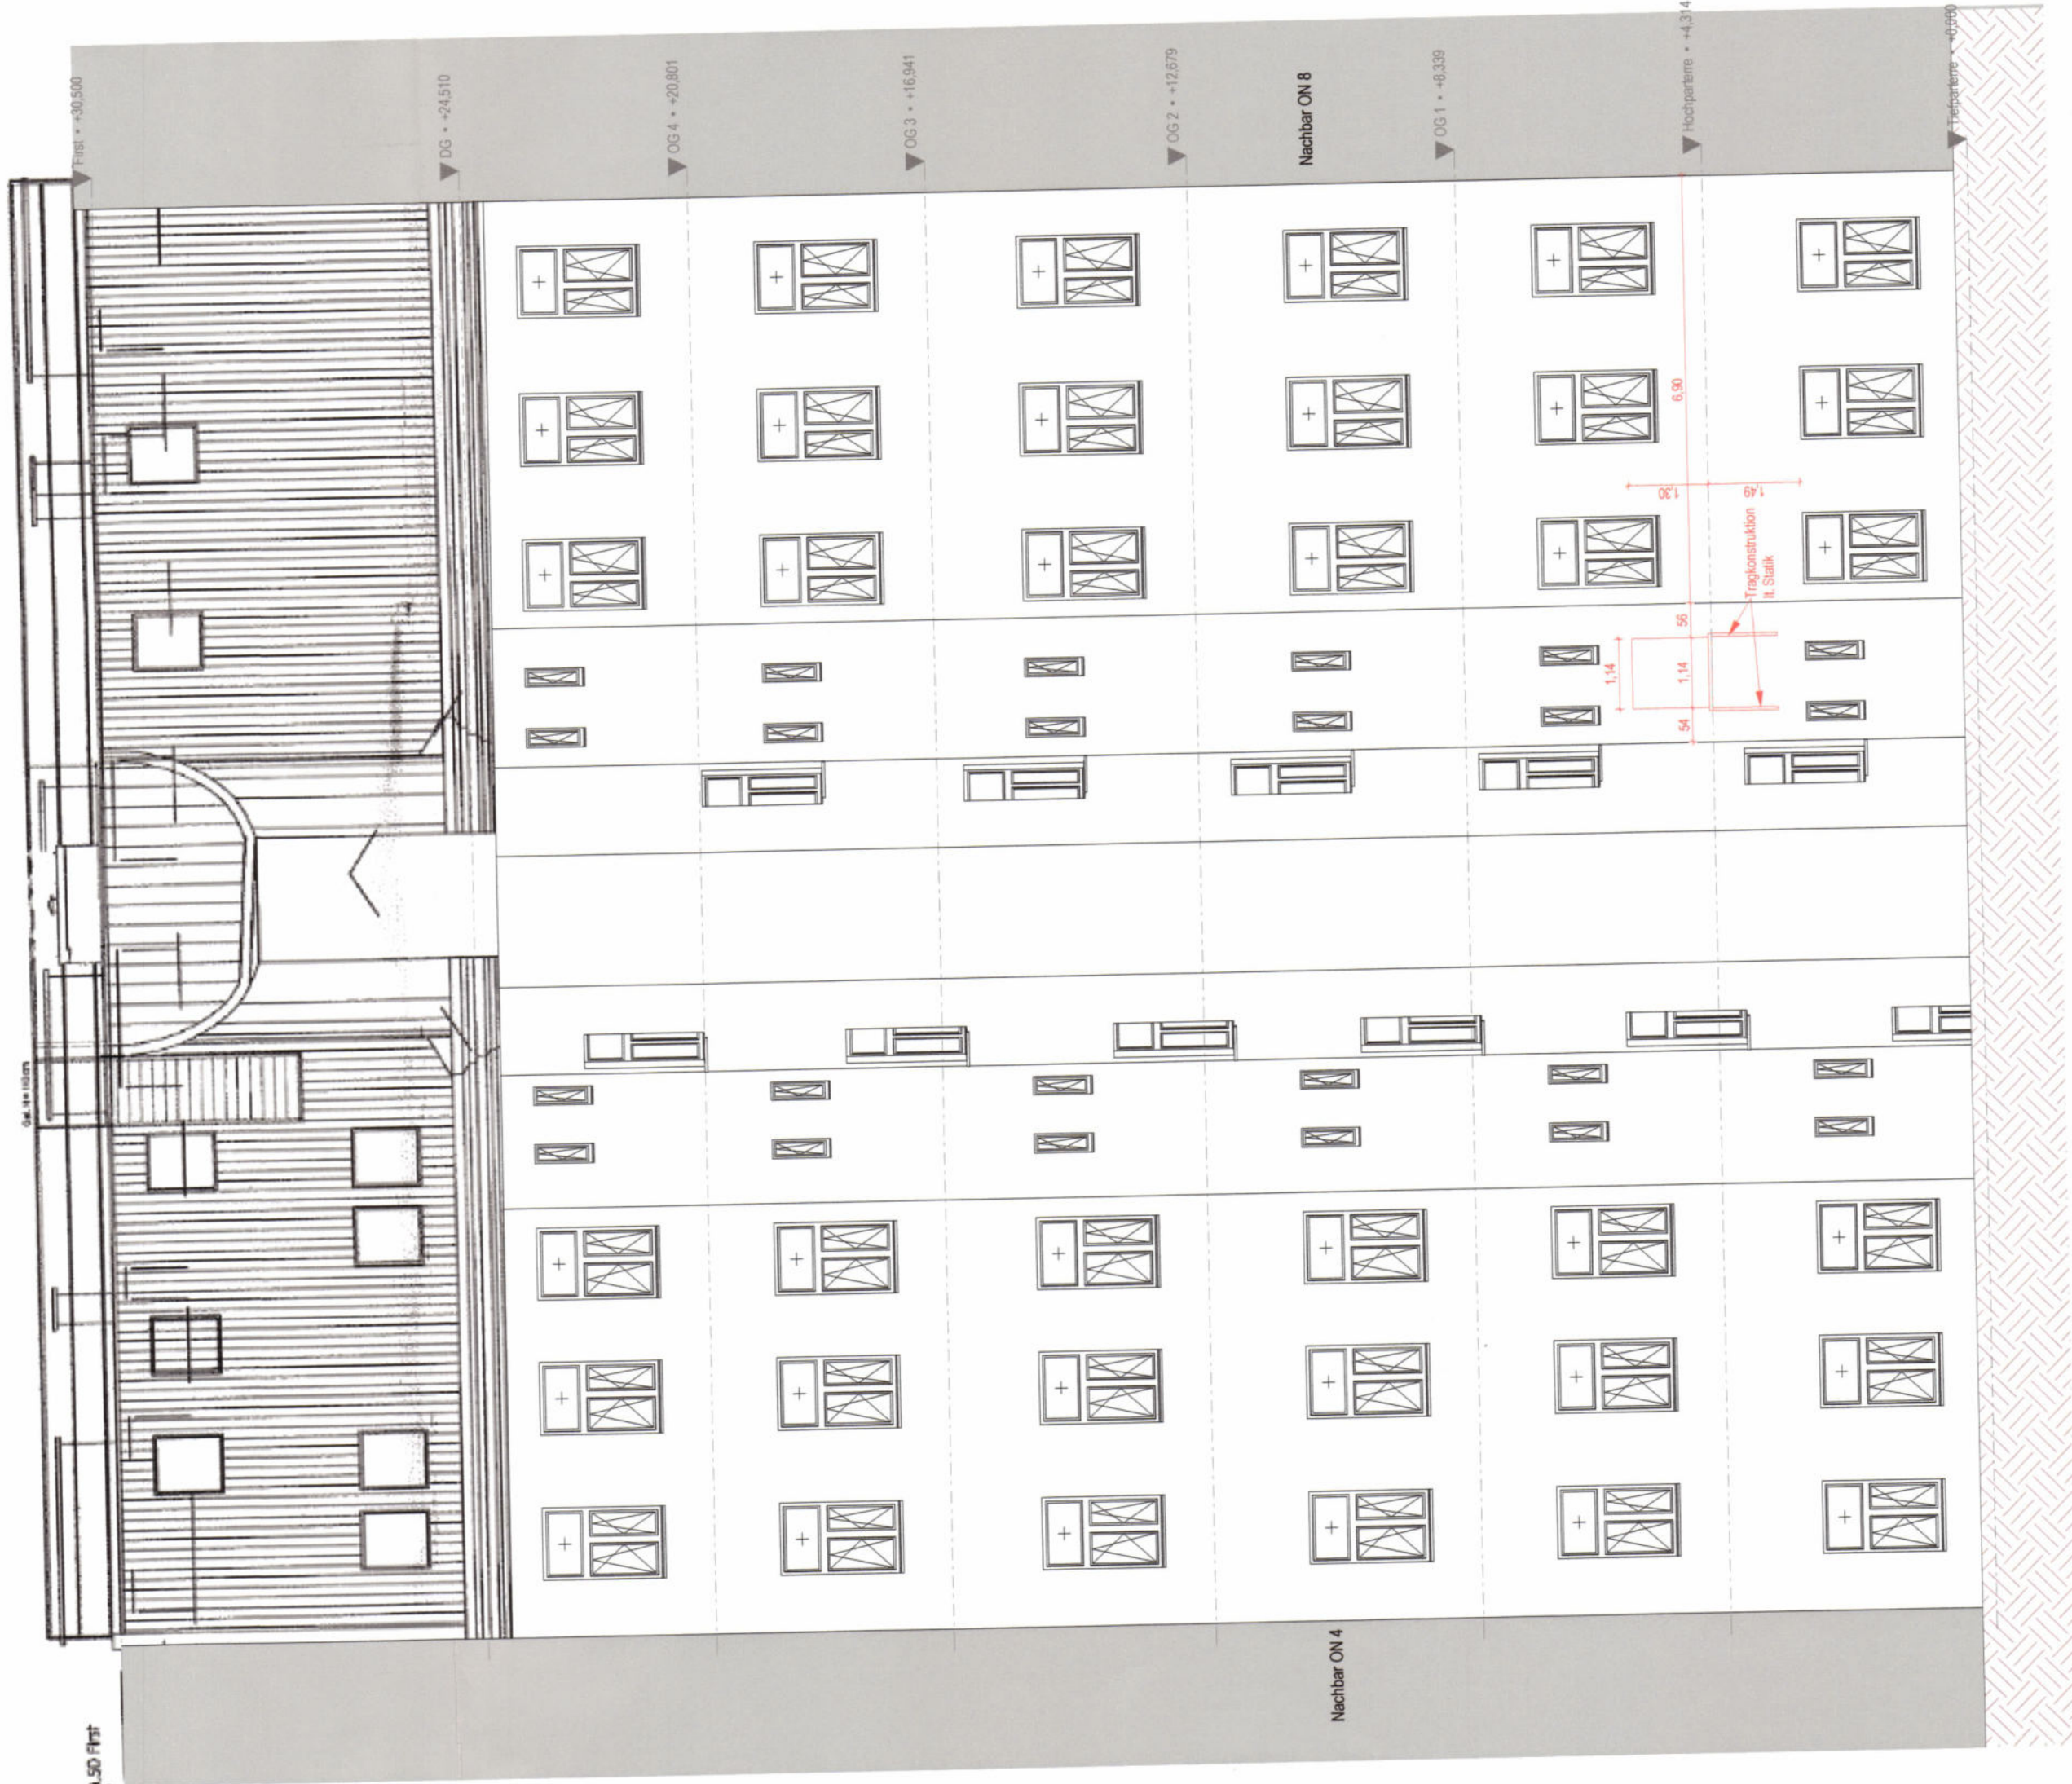

2-te Etagen-Zugang


18.11.2019

Ergänzt:

30.3.2019

GST GRENZE

GST GRENZE

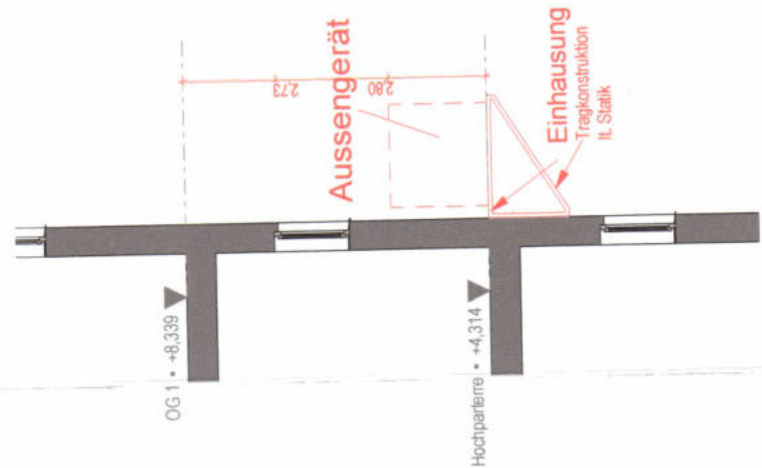

Die vorgesehenen maximalen Betriebszeiten sind zwischen 06:00- 21:00 an Werktagen.

Schnitt 1

Hochparterre