



Betreff:

1., Landesgerichtsstraße 6

Gst.Nr. 1526/2 in

EZ 894, Kat.Gem. Innere Stadt



Gebietsgruppe Ost - Stadterneuerung I

Dresdner Straße 82, 1. Stock

1200 Wien

Telefon: (+43 1) 4000-37410

Fax: (+43 1) 4000-99-37410

ggo.stadterneuerung1@ma37.wien.gv.at

bauen.wien.at

Bauanzeige (sonstige Bauführung), §62 - Bürozusammenlegung Top 7 und Top 8, sowie Sanierung und Klimatisierung

Aktenzahl	Sachbearbeiter*in	Telefon	Datum
MA37/1123908-2023-16	Bara	4000/37846	Wien, 05.05.2025

AV - FERTIGSTELLUNG

Zahl der Fertigstellungsanzeige/-meldung: MA 37/1123908-2023-16

weitere Bewilligungszahlen: MA 37/

Fertigstellungsanzeige/-meldung

Vollständig belegt am: 30.04.2025 (Tag ab dem das Gebäude / das Bauwerk benutzt werden darf)

Gebühren

22,00 VA mittels eBezahlen vorschreiben

Belege:

Bestätigung der*des Ziviltechniker*in

-

Erklärung der*des Bauführer*in

vorgelegt

Ausführungsplan/pläne: keine Ausführungspläne

-

Bei Ausführungsplan/pläne Nachweis ü. die erf. Zuverlässigkeit der Tragwerke

-

Überprüfungs-Nachweise der*des Prüfeningenieur*in

-

Positive Gutachten über Abgasanlagen (bei Abgassammlern mit Hinweis, dass eine Strömungsberechnung nach ÖNORM EN 13384-2 vorliegt)	-
Positive Gutachten über Kanal bzw. Senkgrube	-
Positive Gutachten über die Trinkwasserinstallation (Verbrauchsanlage)*	-
Bestätigung über die Registrierung der Gebäudebeschreibung*	-
Unterfertigte Förderungszusicherungen gemäß § 29 WWFSG 1989*	-
Positive Gutachten über sicherheitstechn. Einrichtungen	-
Nachweis über den Wärme- u. Schallschutz	-
Bestätigung ü. Maßnahmen z. Schutz v. Emissionen	-
Bestätigung ü. das Anlegen / die Registrierung eines Bauwerksbuches	-
Vereinbarung über den Betrieb eines Car-Sharing-Stellplatzes auf der Liegenschaft gemäß § 50b Abs. 1 Z 2 WGarG 2008	-
sonstige vorgeschriebenen Unterlagen/Nachweise	-

Gesetzliche Erfordernisse:

grundbücherliche Durchführung der Abteilung	-
Gehsteigerstellung	-
Garagenlüftungsanlage FS-Meldung vollständig erstattet	-
Kraftbetriebene Parkeinrichtung vorhanden (z.B. Stapelparksystem)	-

Das Bauvorhaben ist daher als abgeschlossen zu beurteilen

→ GWR - Meldung (Webformular) erfolgt (nur bei Neubau), Zu- und Umbauten (gesamtes Gebäude), Dachgeschoßausbau (<u>wenn neue Nutzungseinheiten entstehen</u>)	-
→ Kostenersatz für Gehsteig vorzuschreiben	-
→ Stellplatzsicherstellung außerhalb des Bauplatzes	-

Anmerkungen:

-

Der Sachbearbeiter:
Bara

Für den Abteilungsleiter:
DI Huber

Adresse:

1., Wien, Landesgerichtsstraße 6

EZ / KG:

EZ 894, KG Innere Stadt (01004),
Gst.Nr. 1526/2

BEARBEITUNGSBOGEN

§62

Zahl MA 37/1123908-2023-1

Eingereicht am:

13.09.2023

Stiege / Stock / Tnr.

2. Stock/TNr. 7, TNr. 8

Art der Bauführung (gem.: § 62 Abs.1):

Produkte:

Bauanzeigen (Sonstige Bauführung -§62(1)Z4)

☒ Schutzzone

☐ Badeinbau (Ziff. 1)

☐ Loggienverglasung (Ziff. 2)

☐ Fenster- / -türtausch (Ziff. 3)

☒ baul. Änderung (Ziff. 4)

Stat. Vorbemessung erforderlich?

Nein ☒

Ja ☐

☐ Bauanzeige vollständig belegt

frühest möglicher Baubeginn am:

15.09.2023

Schutzzone (Ziff. 1, 2, oder 3) bzw. erf. Vorstatik (Ziff. 4) berücksichtigt!

☐ Baubeginnsanzeige liegt vor - angezeigter Baubeginn möglich? Ja ☐

Nein ☐ → Bauinspektion informieren
und BauwerberIn informieren

☒ Bauanzeige unvollständig belegt

Verbesserungsauftrag am:

mündl. 15.09.2023

Frist:

7 Tage

Vollständig belegt am:

15.09.2023

☐ Bauanzeige bleibt unvollständig belegt, daher Zurückweisung erforderlich

AV vom:

20. SEP. 2023

Die Bauanzeige wurde im Sinne der Bestimmungen der §§ 67 Abs. 1 und 62 Abs. 1 BO geprüft.

☒ Es liegt kein Untersagungsgrund vor. ☐ § 70 ☒ § 70 in Verb. mit § 68 ☐ § 71

EUR 28.- VA mit eBezahlen vorschreiben

21. SEP. 2023

Die Sachbearbeiterin:
Ing. in Rabl

Für den Abteilungsleiter:

VerwaltungsassistentInnen - Checkliste

Verortung		
Unterschrift		VI
Antrag Bauwerber		
Personendaten	ZMR geprüft	✓
BauFIS	UR geprüft	
Vollmachten	Vorhanden Schlüssig Vertreter eingetragen nicht vorhanden	2
Befugnisse		
Letzter SB auf Liegenschaft	WEA	
Offene Verfahren -> in Bearbeitung (SB)	/	
Offene Aufträge	/	

Dezernatsleitung - Checkliste

Produkte		
Zuteilung		

BAUANZEIGE

FÜR DIE BAULICHE ÄNDERUNGEN BEI DER TÜR 7 UND 8, LANDESGERICHTSTRASSE 6 , 1010 WIEN

GRUNDST. NR. : 1526/2

EINLAGEZAHL : 894

GRUNDST. FL. :

KAT. GEM. : 01004 Innere Stadt

BAUWERBER:

Zentralverband der Hausbesitzer -
Hausbesitzerhilfsverein
Landesgerichtsstr. 6 Wien 1010

VOLLMACHT:
Dr. Noszek GmbH
Untere Viaduktgasse 51/10
1030 Wien

IMMOBILIENVERW. / MAKLER
Dr. FRIEDRICH NOSZEK GmbH
1030 Wien, Unt. Viaduktg. 51/10

GRUNDEIGENTÜMER:

Zentralverband der Hausbesitzer -
Hausbesitzerhilfsverein
Landesgerichtsstr. 6 Wien 1010

VOLLMACHT:
Dr. Noszek GmbH
Untere Viaduktgasse 51/10
1030 Wien

IMMOBILIENVERW. / MAKLER
Dr. FRIEDRICH NOSZEK GmbH
1030 Wien, Unt. Viaduktg. 51/10

BAUFÜHRER:

Ing. Buchberger Bau GmbH
Kranzberg 2-3
4372 St. Georgen am Walde
office@buchberger-bau.at
07954 2190 (4=Fax)



Stadt
Wien

PLANVERFASSER:



moment-home Real Estate Solutions
Markus P. Swittalek Architekt Dipl.-Ing. Dr. techn.
staatlich befugter und beordeter Ziviltechniker
Franz-Josefs-Kai 43/1010 Wien +43 1 533 97 16

Baupolizei
Gebietsgruppe Ost,
Stadterneuerung 1

ZI.: MA37/1123908-2023-1

Dieses Bauvorhaben gilt als gem. § 70 BO bewilligt.

Wien, 20.09.2023

Für den Abteilungsleiter:
Dipl.-Ing. Messner



PLANINHALT

PARIE:

A

B

C

D

GRUNDRISS 2. STOCK
LAGEPLAN 1/500

MASSTAB = 1:100

PLAN NR. :

01

PROJ. NR. : LAN_6

GEZ. : AR

INDEX:

DATUM : 23.03.2023



moment-home Real Estate Solutions
Markus P. Swittalek Architekt Dipl.-Ing. Dr. techn.
Franz Josefs-Kai 43 - 1010 Wien + 43-1-533 9716
www.moment-home.com

DIESES PROJ. BZW. PLAN IST URHEBERRECHTLICH GESCHÜTZT ©

AUFBAUTEN

INNEHWAND 10.00 CM	FLIESEN
01.25 CM GIB 12.5 (GIB 12.5 IN FLECHTHÄLLEN)	ABDICHTUNG
07.20 CM BOVER, TW-4775	ESTRICH
ZWISCHEN CM 75-PROF. ENGEREN	FOLIE
STIEHRAUSTAND LT. NORM. BEI	TRETSCHALLDÄMMUNG
VERLESTEN WÄNDEN BZW.	FOLIE
ABHÄNGIG VON RAUMHÖHE	BEISCHÜTTUNG < 1.0 NMH
01.25 CM GIB 12.5 (GIB 12.5 IN FLECHTHÄLLEN)	PARKETT
10.00 CM	SCHÜTTUNG
	02.00 CM POLSTERHOLZ
	06.00 CM BESCHÜTTUNG
	02.50 CM SCHÜTTUNG
	26.00 CM DECKE BESTAND
	02.50 CM HOLZSCHÜTTUNG BESTAND
	01.00 CM PUTZTRÄGER BESTAND
	01.50 CM VERPUTZ BESTAND
	52.00 CM

LEGENDE

BESTAND	NEU
ABBRUCH	VOLLZIEGELMAUERWERK
GLAS	LEICHTBAU, GK

BAUTEILE

ALLE INNEN LIEGENDEN RÄUME WERDEN MICH. INS FREIE ENTLÜFTET

ISOLIEREBENE IN MASSÄULEN ÜBER ZEMENTESTRICH

VORSATZSCHALEN IN MASSÄULEN


GIPS-KARTON-PLATTEN IN MASSÄULEN SIND FEUCHTRÄUMPLATTEN (VOLLFÄHIGKEIT)

ALLE TÜRGROSSEN SIND DURCHGANGSLICHTEN


HEIZUNG: GAS KOMBITHERME

ALLE MASSE DES BESTANDES SIND GESCHOSSENWEISE GEENTWURFTE FERTIGMASSE MIT PUTZ

BODENBELÄGE IN BAD, WC, TEEKÜCHE = KERAMISCHE FLIESEN

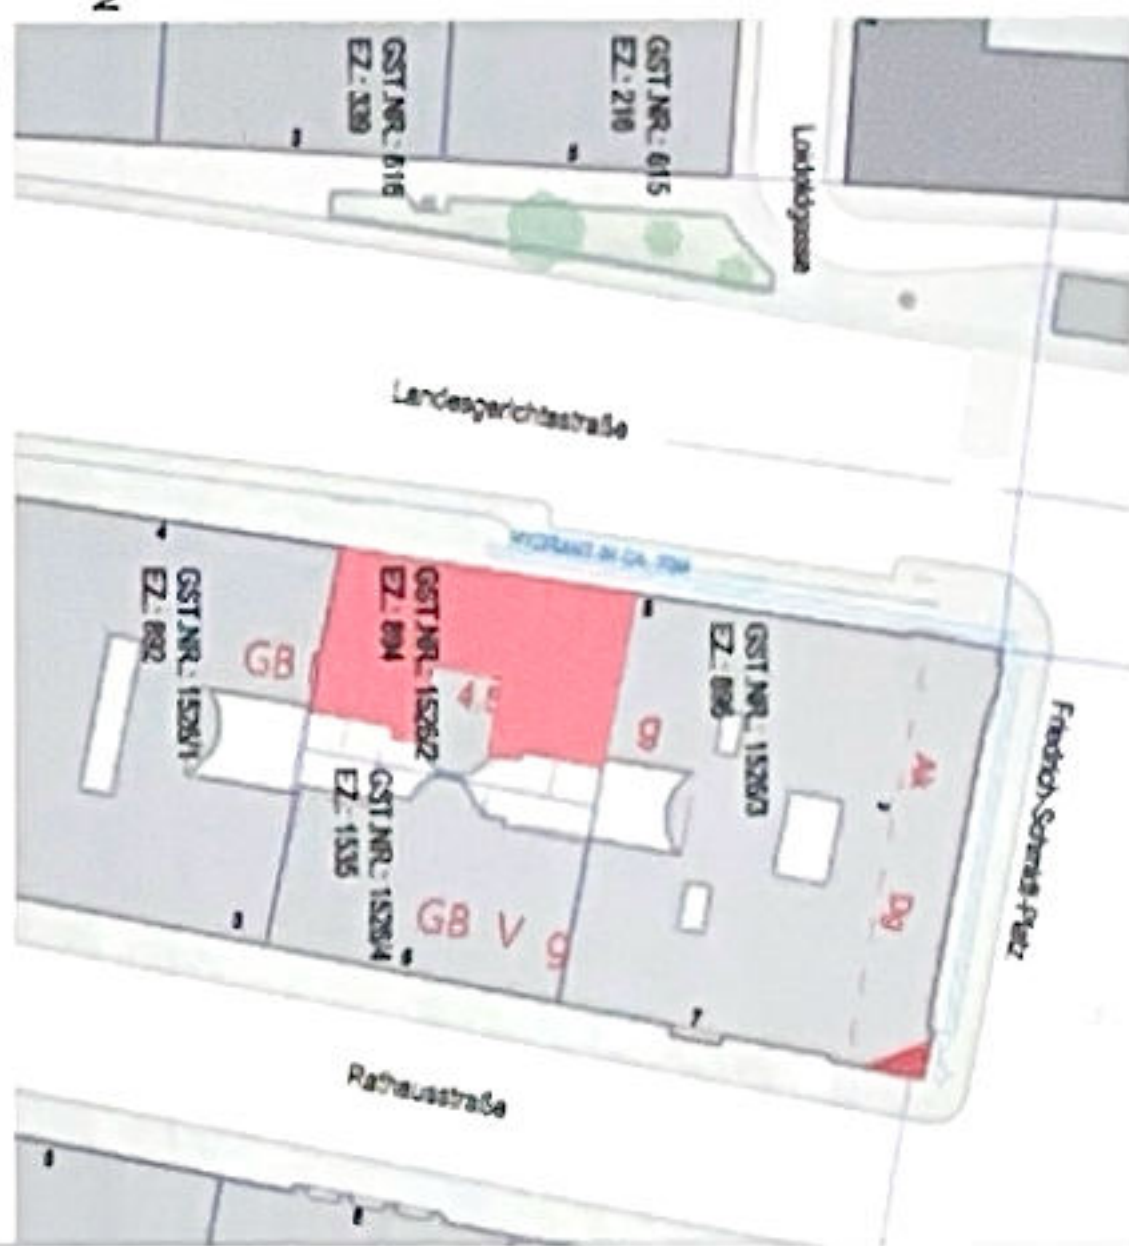

LAGEPLAN 1/500

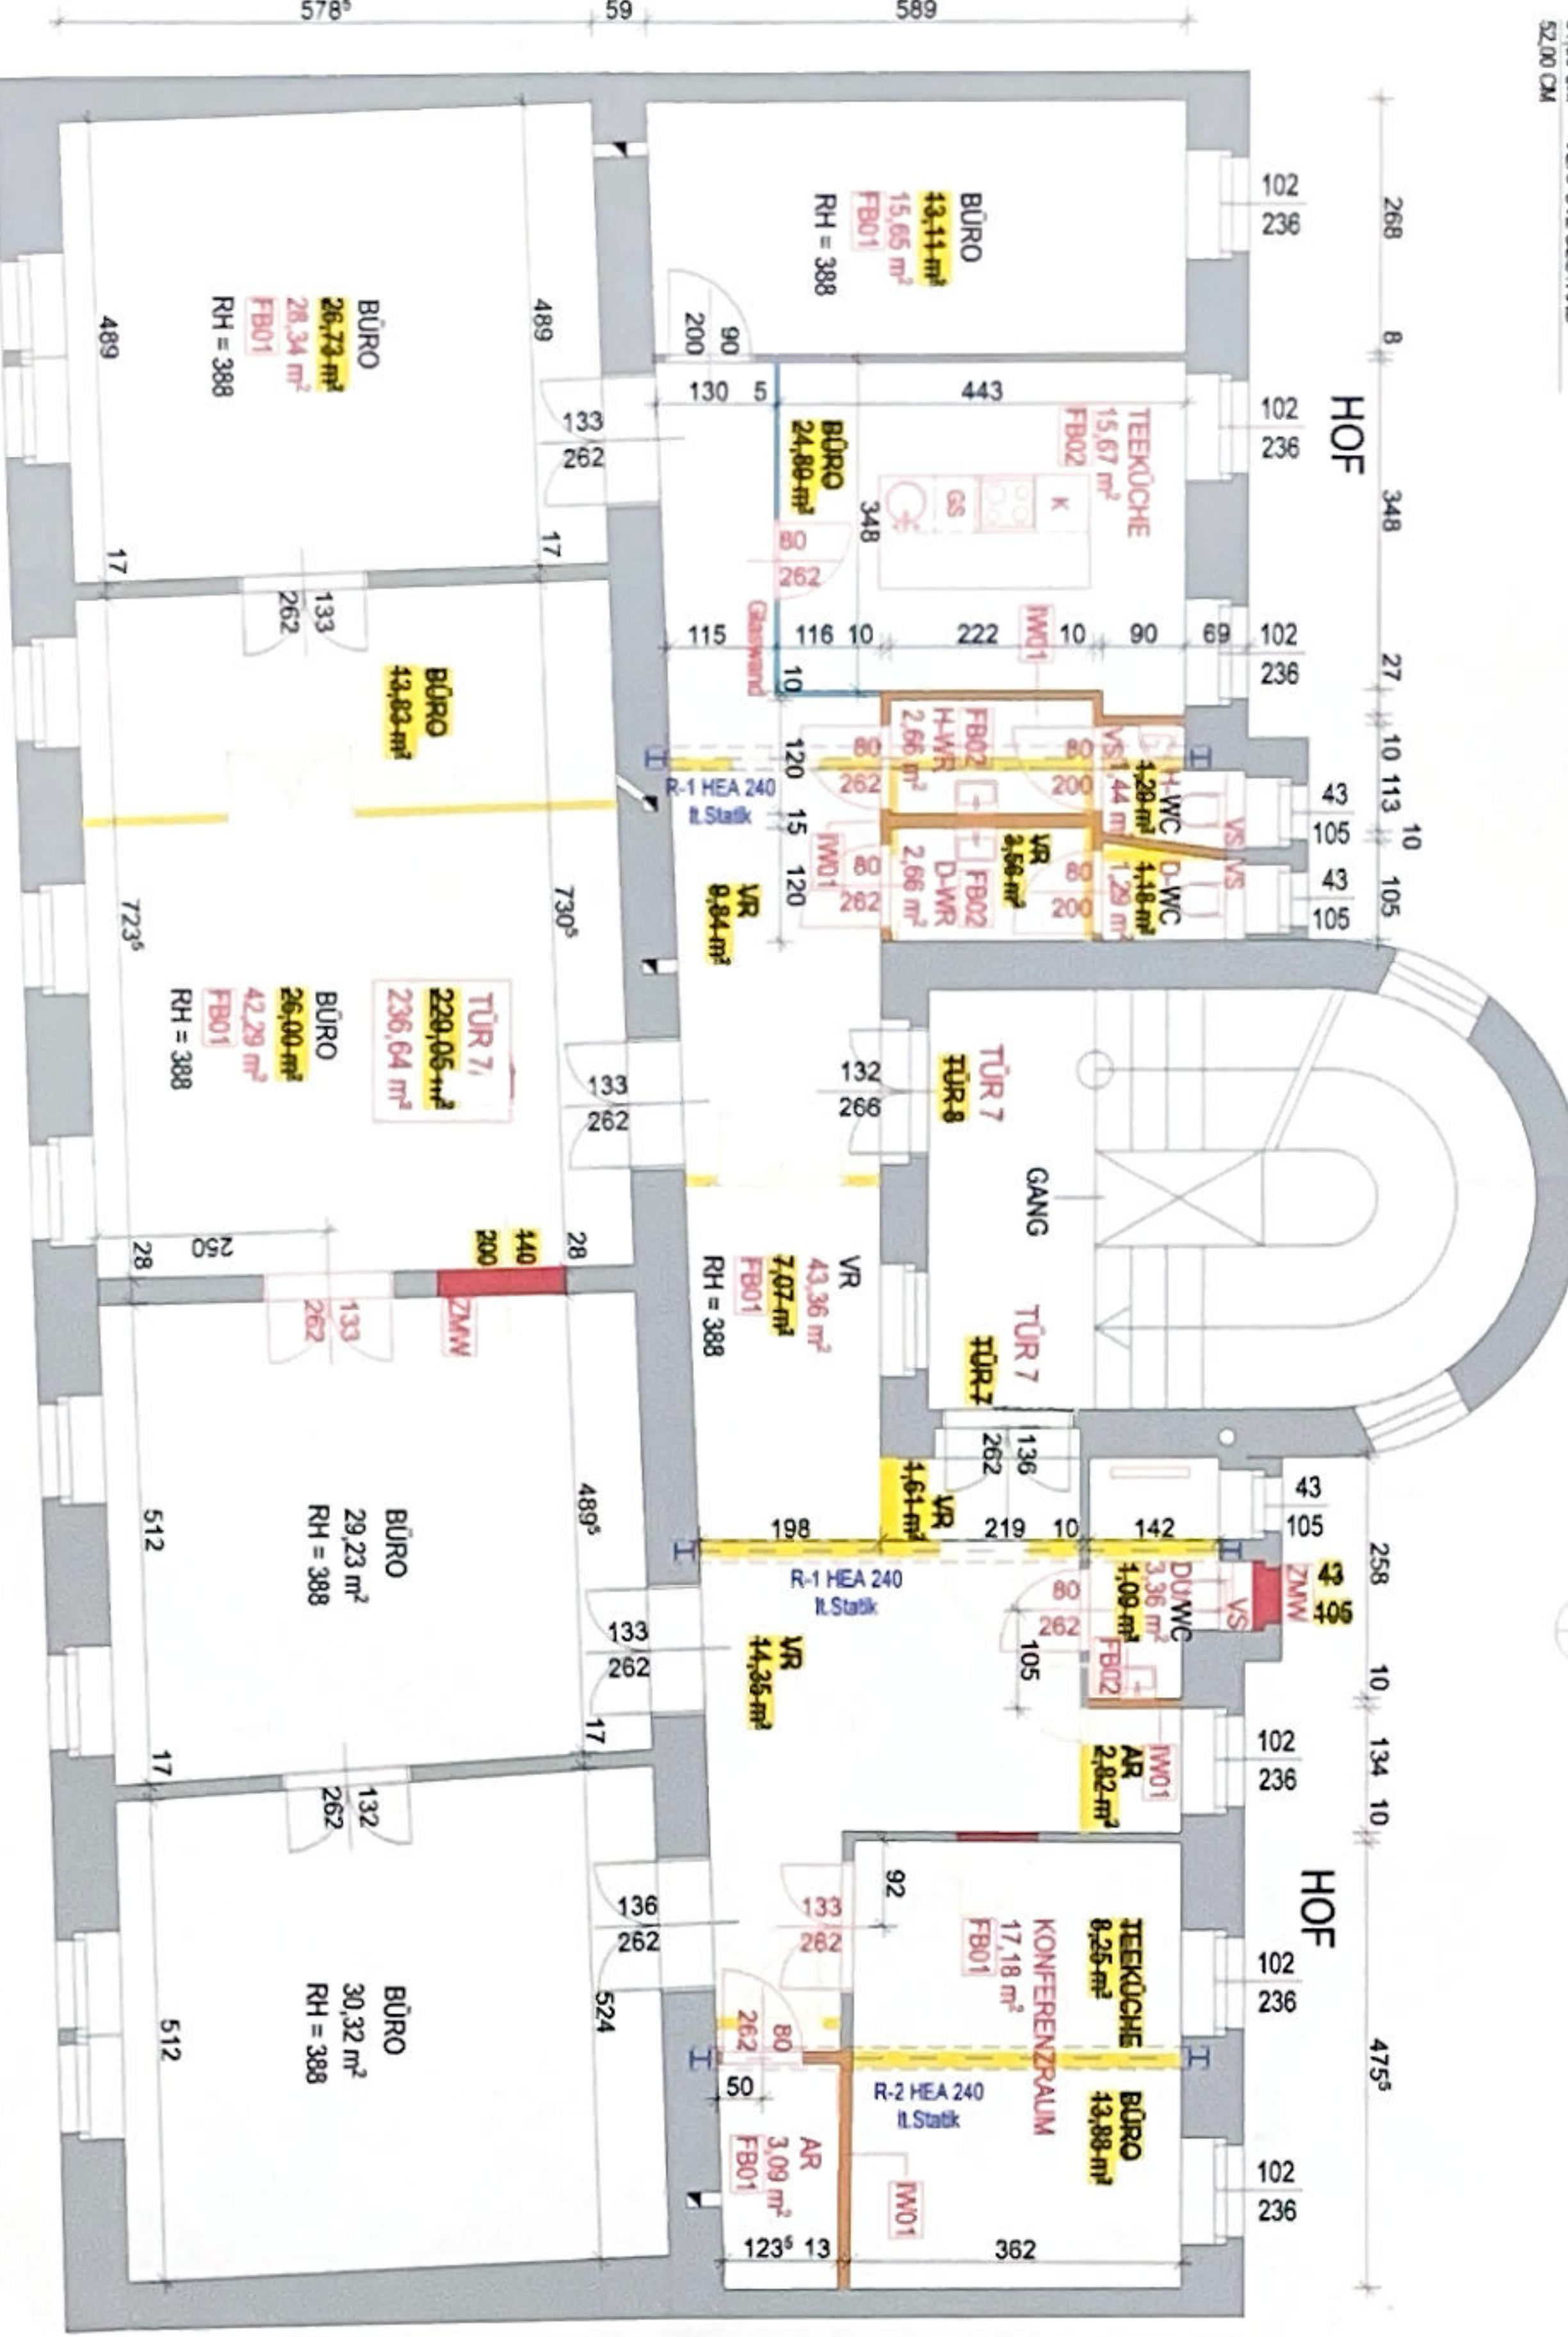

LANDESGERICHTSTRASSE 6
2. STOCK

BAUANZEIGE

FÜR DIE BAULICHE ÄNDERUNGEN
BEI DER TÜR 7 UND 8,
LANDESGERICHTSTRASSE 6, 1010 WIEN

GRUNDST. NR.:	1526/2	EINLAGEZAH.:	894
GRUNDST. FL.:		KAT. GEM.:	01004 Innere Stadt
BAUWERBER:	Zentralverband der Hausbesitzer - Hausbesitzhilfsverein Landesgerichtsstr. 6 Wien 1010	GRUNDEIGENTÜMER:	Zentralverband der Hausbesitzer - Hausbesitzhilfsverein Landesgerichtsstr. 6 Wien 1010

VOLLMACHT:
Dr. Noszek GmbH
Untere Viaduktgasse 51/10
1030 Wien

IMMOBILIENVERW. / MAKLER
DR. FRIEDRICH NOSZEK GMBH
Untere Viaduktgasse 51/10
1030 Wien

BAUFÜHRER:
Ing. Buchberger Bau GmbH
Kranzberg 2-3
4372 St. Georgen am Walde
office@buchbergersbau.at
079542190 (4=Fax)

PLANVERFASSER:
moment-home Real Estate Solutions
Markus P. Switalek Architekt Dipl.-Ing. Dr. techn.
Franz-Josefs-Kai 43/1010 Wien +43 1 533 97 16

Stadt Wien
Baupolizei
Gebietsgruppe Ost,
Stadterneuerung 1

Stadtsabteilung 37
WIEN

Für den Abteilungsleiter:
Dipl.-Ing. Moser

PLANINHALT	PARIE:	A	B	C	D
GRUNDRISS 2. STOCK	MASSTAB =	1:100	PLAN NR.:		
LAGEPLAN 1/500	PROJ. NR.:	LAN_6	GEZ.:	AR	INDEX
	DATUM:	23.03.2023			

GEBÜHRENFREI!

Bauführer/in:

Wien, 30.04.2025

Baumeister Buchberger GmbH

Emil-Kralik-Gasse 3/27

1050 Wien

Bauvorhaben:

Umbauarbeiten

(Gegenstand)

Landesgerichtsstraße 6, 1010 Wien

(Adresse)

Zentralverband der Hausbesitzer - Hausbesitzerhilfsverein

(Bauverberlin)

(Geschäftszahl der ursprünglichen Baubewilligung)

ERKLÄRUNG DES BAUFÜHRERS / DER BAUFÜHRERIN ZUR FERTIGSTELLUNG



Gemäß § 62 Abs. 7 BO

(nach Bauanzeige gem. § 62 Abs. 1 Z 1 bis 3)

Gemäß § 128 Abs. 3 bzw. 3a BO

(nach Baubewilligung bzw. Bauanzeige gem. § 62 Abs. 1 Z 4)

Es wird erklärt, dass das o.a. Bauvorhaben der Baubewilligung/ Bauanzeige und den Bauvorschriften entsprechend ausgeführt wurde.

Weiters wird bestätigt, dass die vorgenommenen Abänderungen, die nun im Rahmen der Fertigstellungsanzeige/-meldung durch farbliche Ersichtlichmachung in den Ausführungsplänen bekannt gegeben werden, den Umfang des § 73 Abs. 3 nicht überschreiten.



Darüber hinaus wird das Erreichen der erforderlichen Zuverlässigkeit der Tragwerke gemäß § 128 Abs. 2 Z 2 und Z 2a bestätigt.

BUCHBERGER Baumeister Buchberger GmbH
1050 Wien, Emil-Kralik-Gasse 3/27
Telefon +43 (0) 1 644 68 65
office@buchberger-bau.at

(Bauführer/in, Stempel / Unterschrift)

HINWEISE

Gemäß § 128 beziehungsweise § 62 Abs. 7 der Bauordnung für Wien (BO) ist nach Fertigstellung der Bauarbeiten vom/von der Bauwerber/in eine schriftliche Fertigstellungsanzeige/-meldung der MA 37 zu übermitteln.

Eine der erforderlichen **Beilagen zur Fertigstellungsanzeige/-meldung** ist beim gegenständlichen Bauvorhaben die Erklärung des/r Bauführers/in, dass der Bau entsprechend der Baubewilligung und den Bauvorschriften ausgeführt worden ist.

Die/r Bauführer/in hat die Möglichkeit, dieses Formular zu verwenden und vollständig ausgefüllt dem/r Bauwerber/in oder direkt der zuständigen Bezirksstelle der MA 37 zu übermitteln.