




2. STOCK

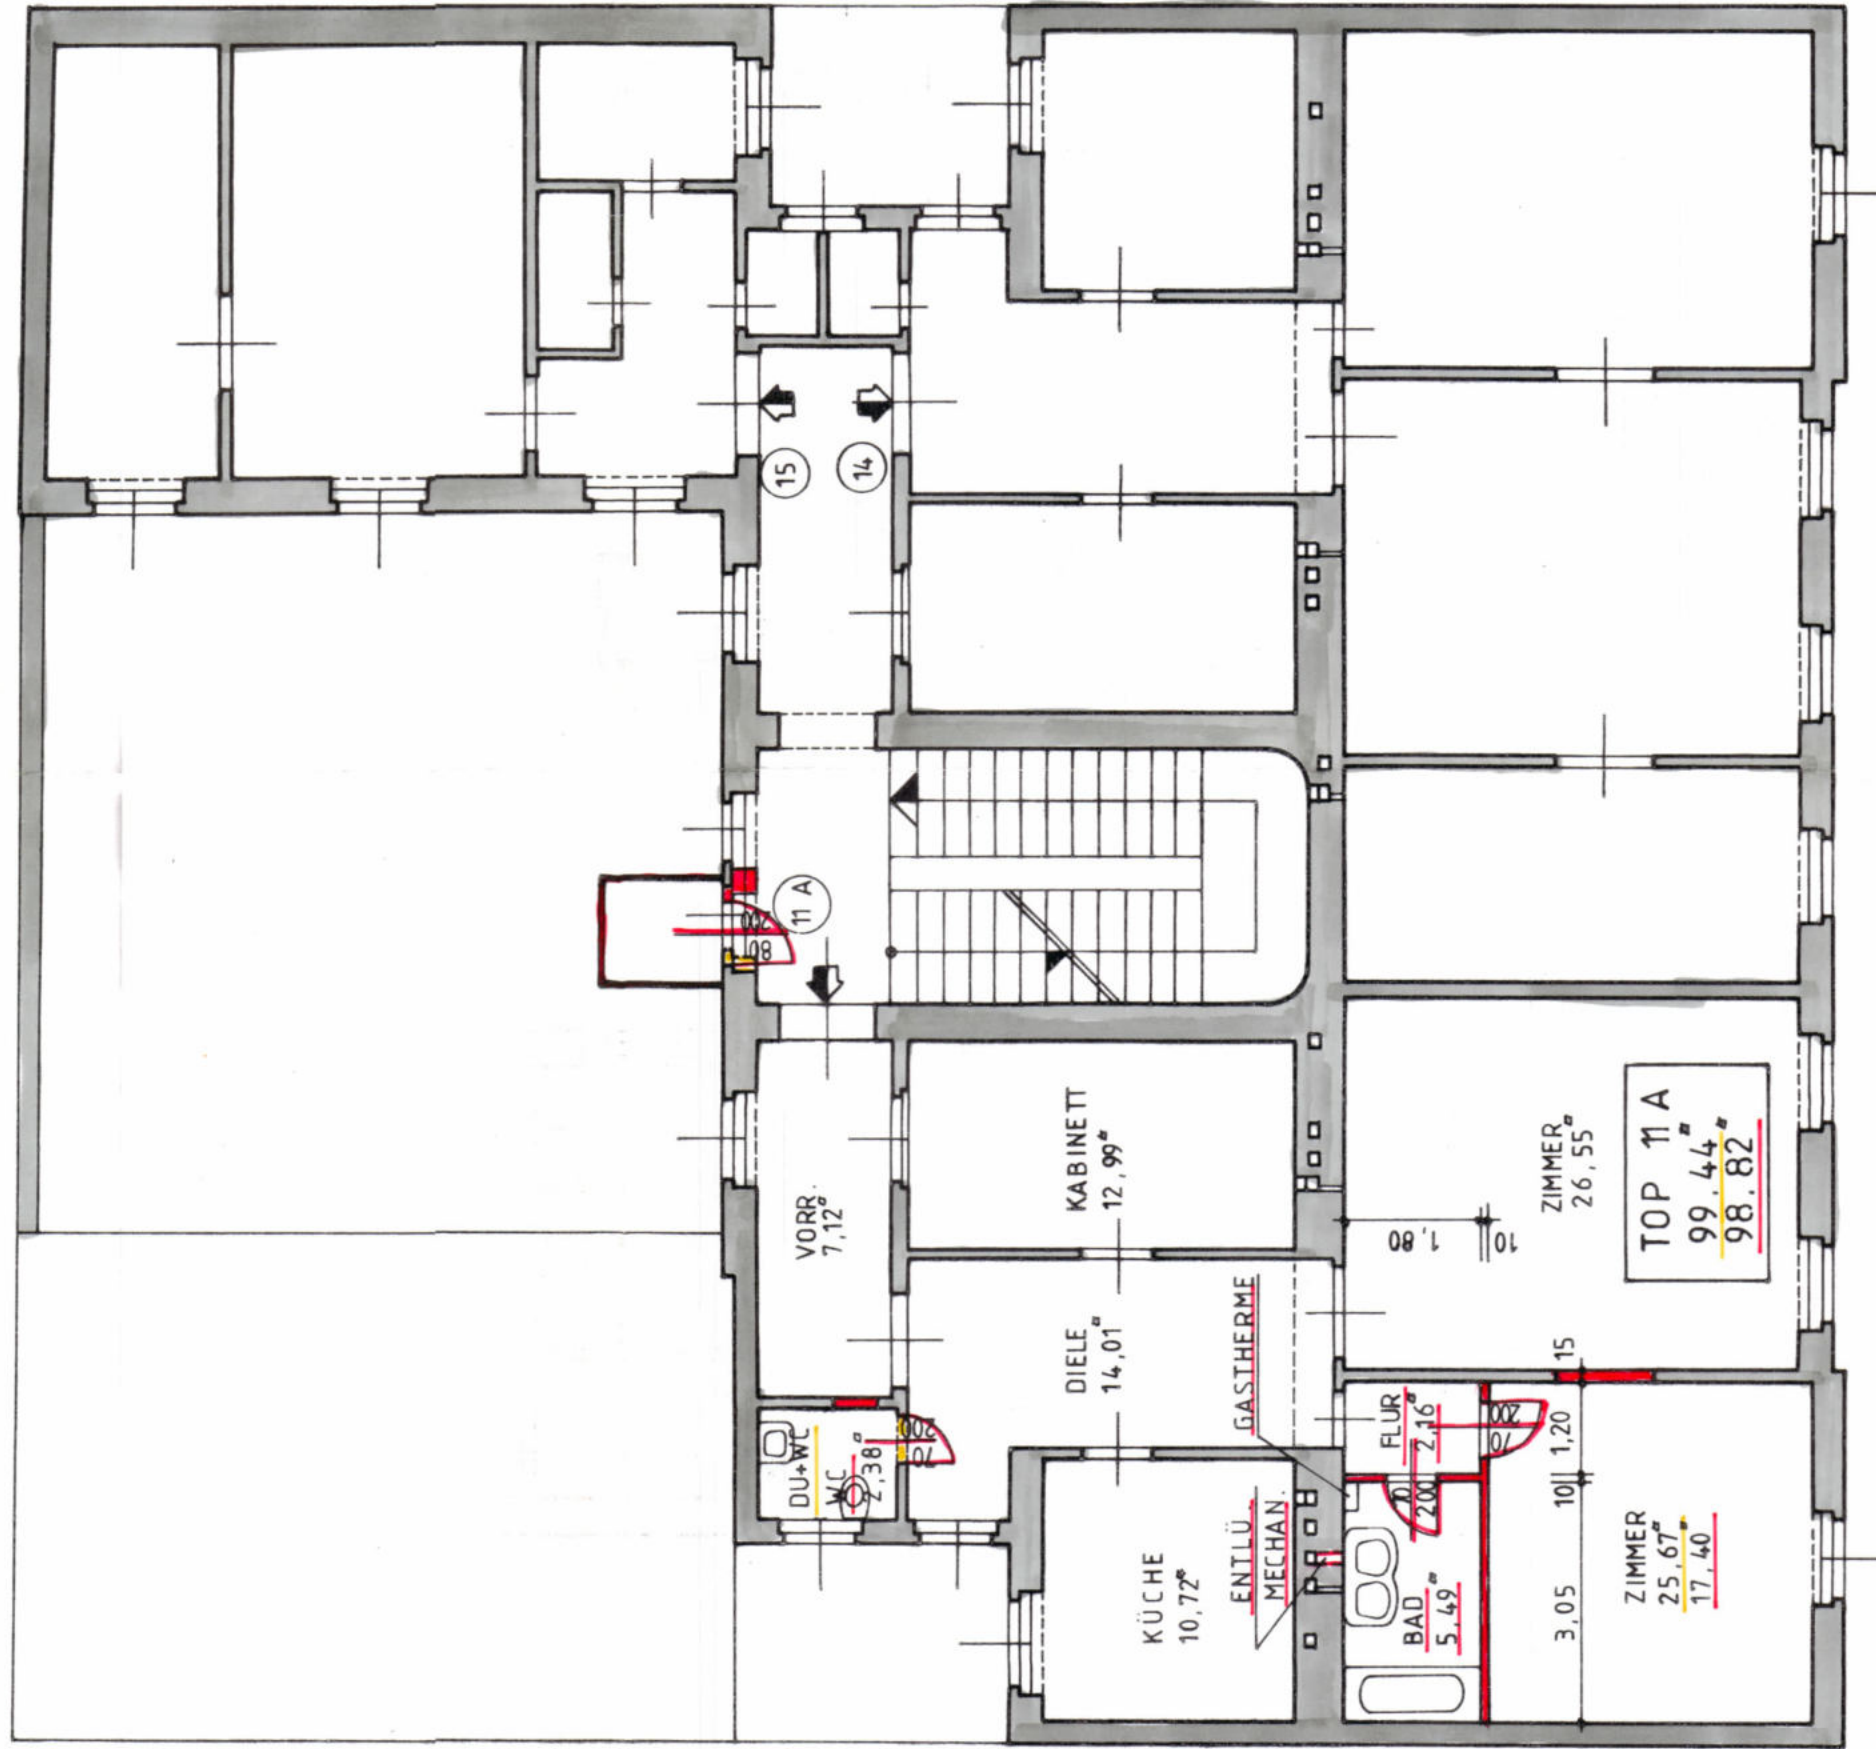


3. STOCK

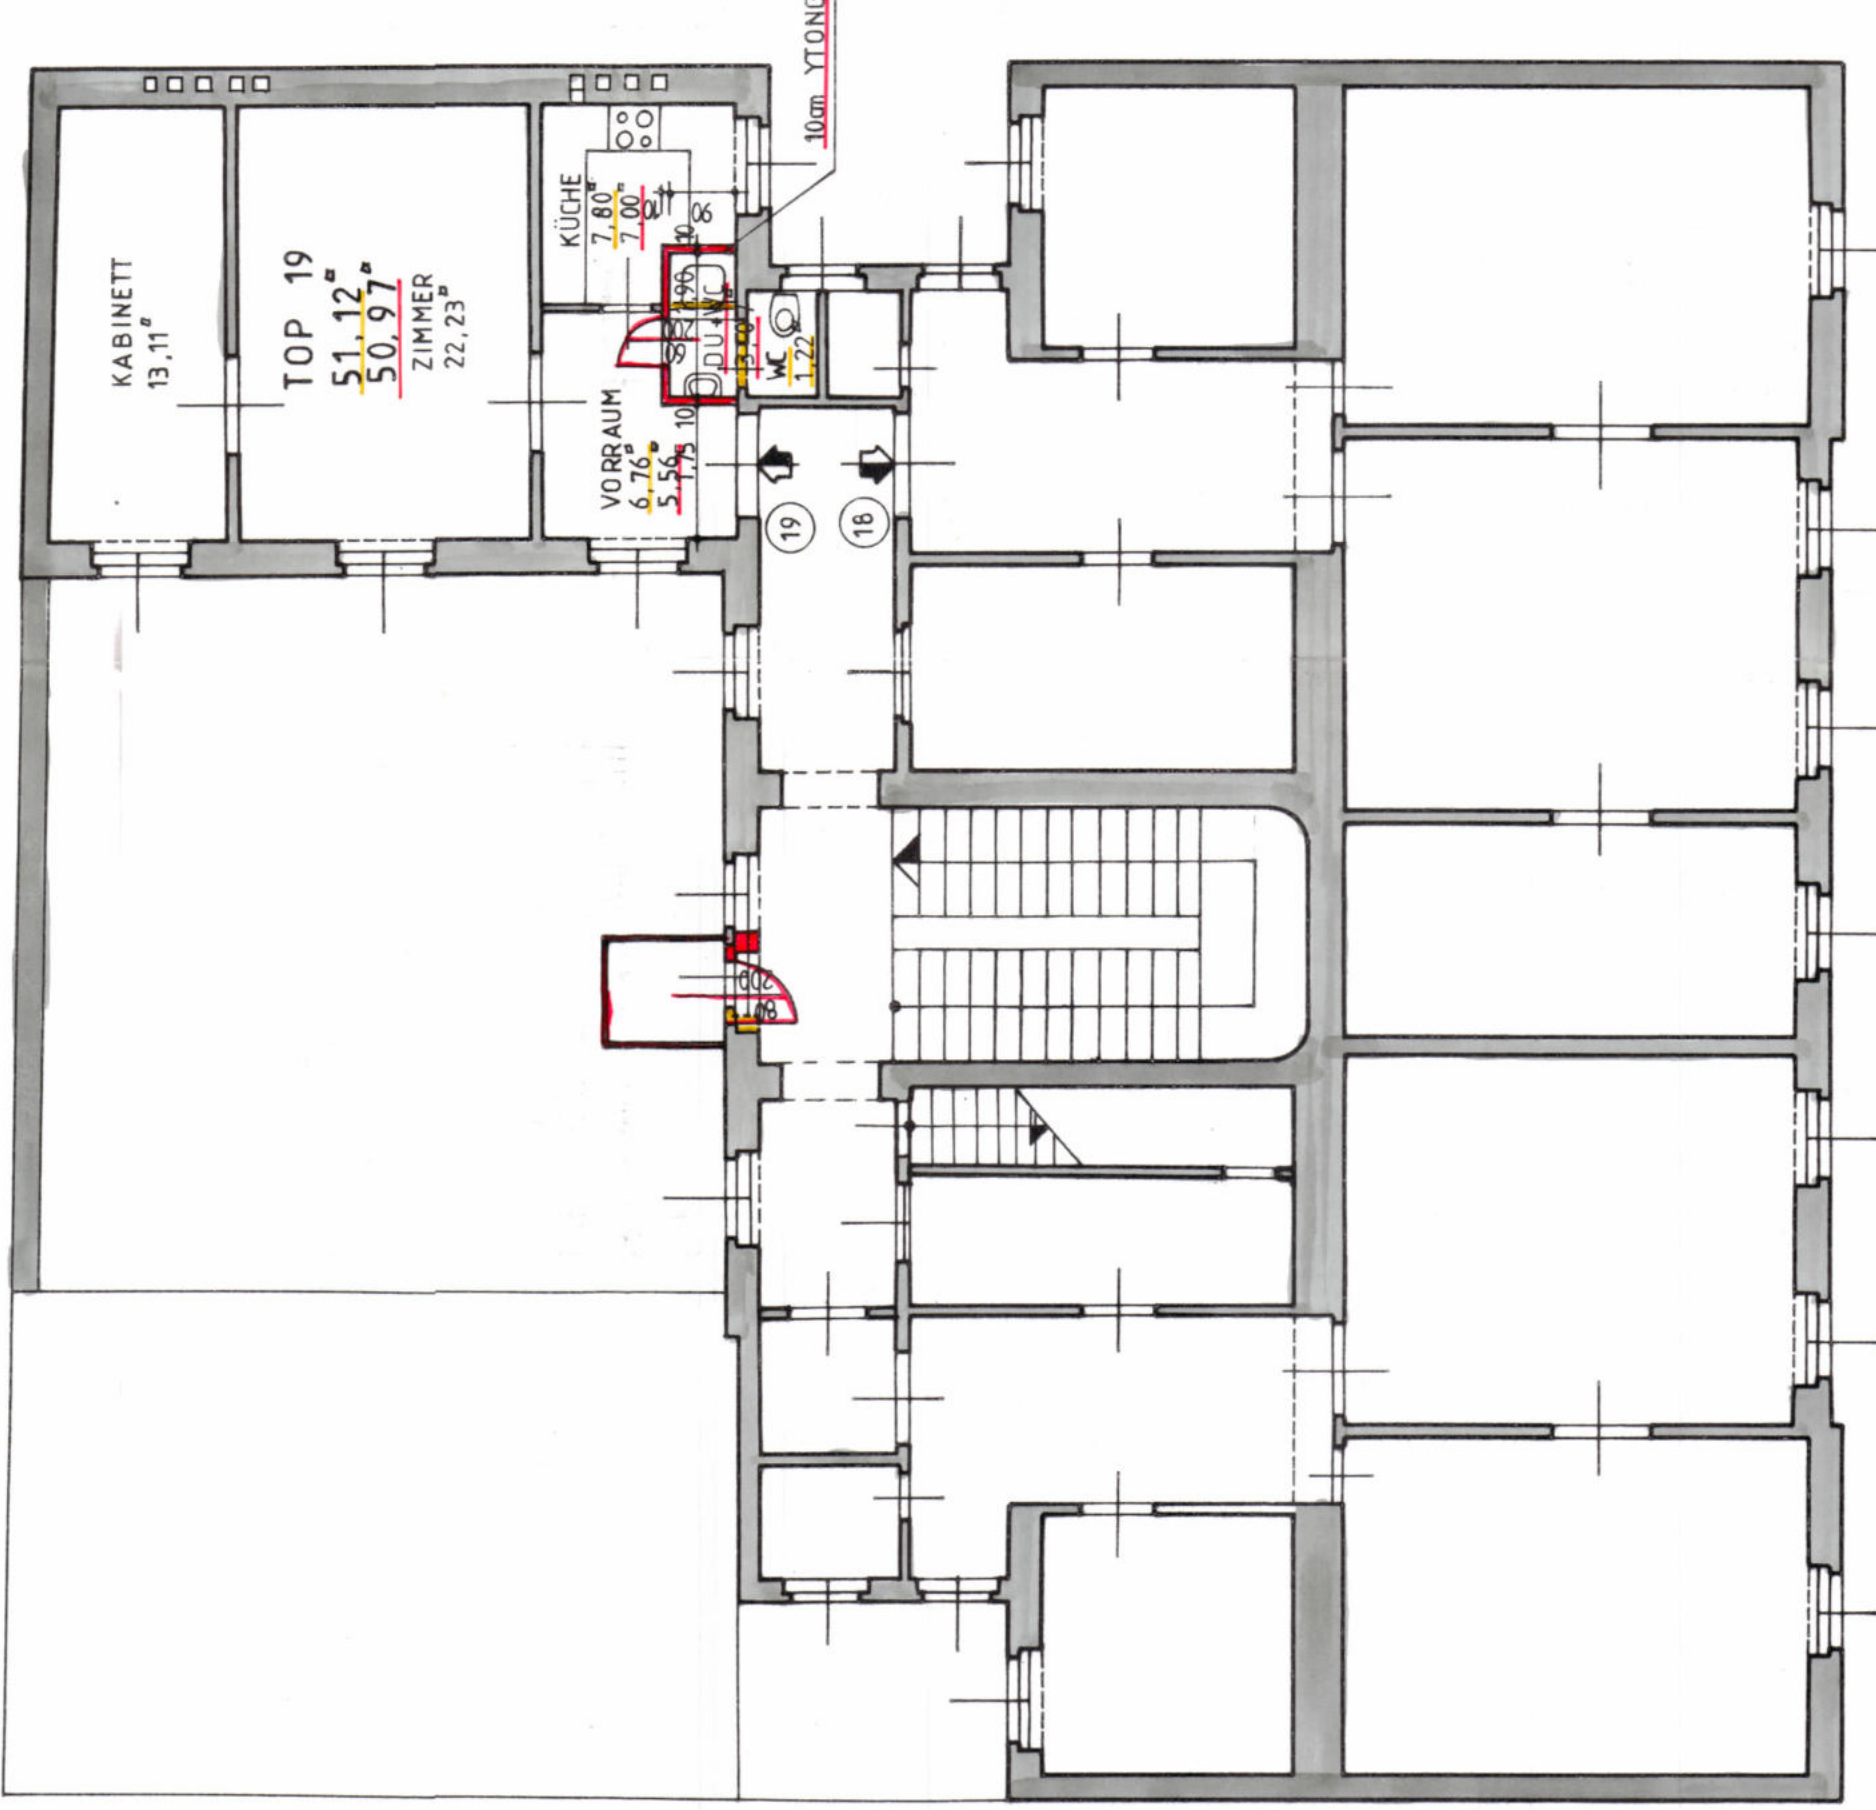


DACHGESCHOSZ

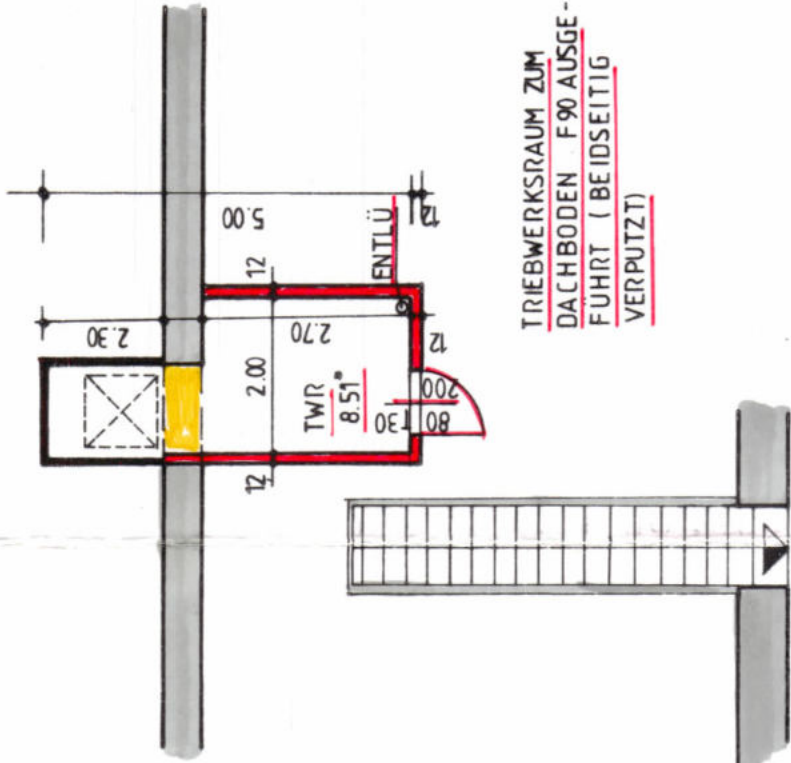


FUSZBODENAUFBAU -
NASTRÄUME 1: 20

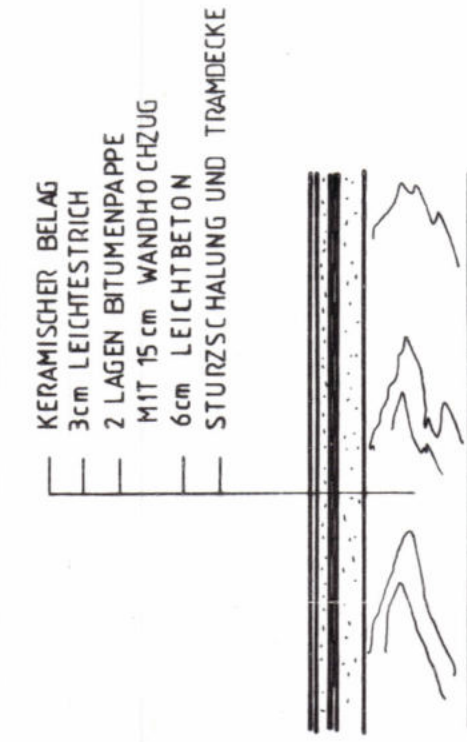


LAGE 1 : 500

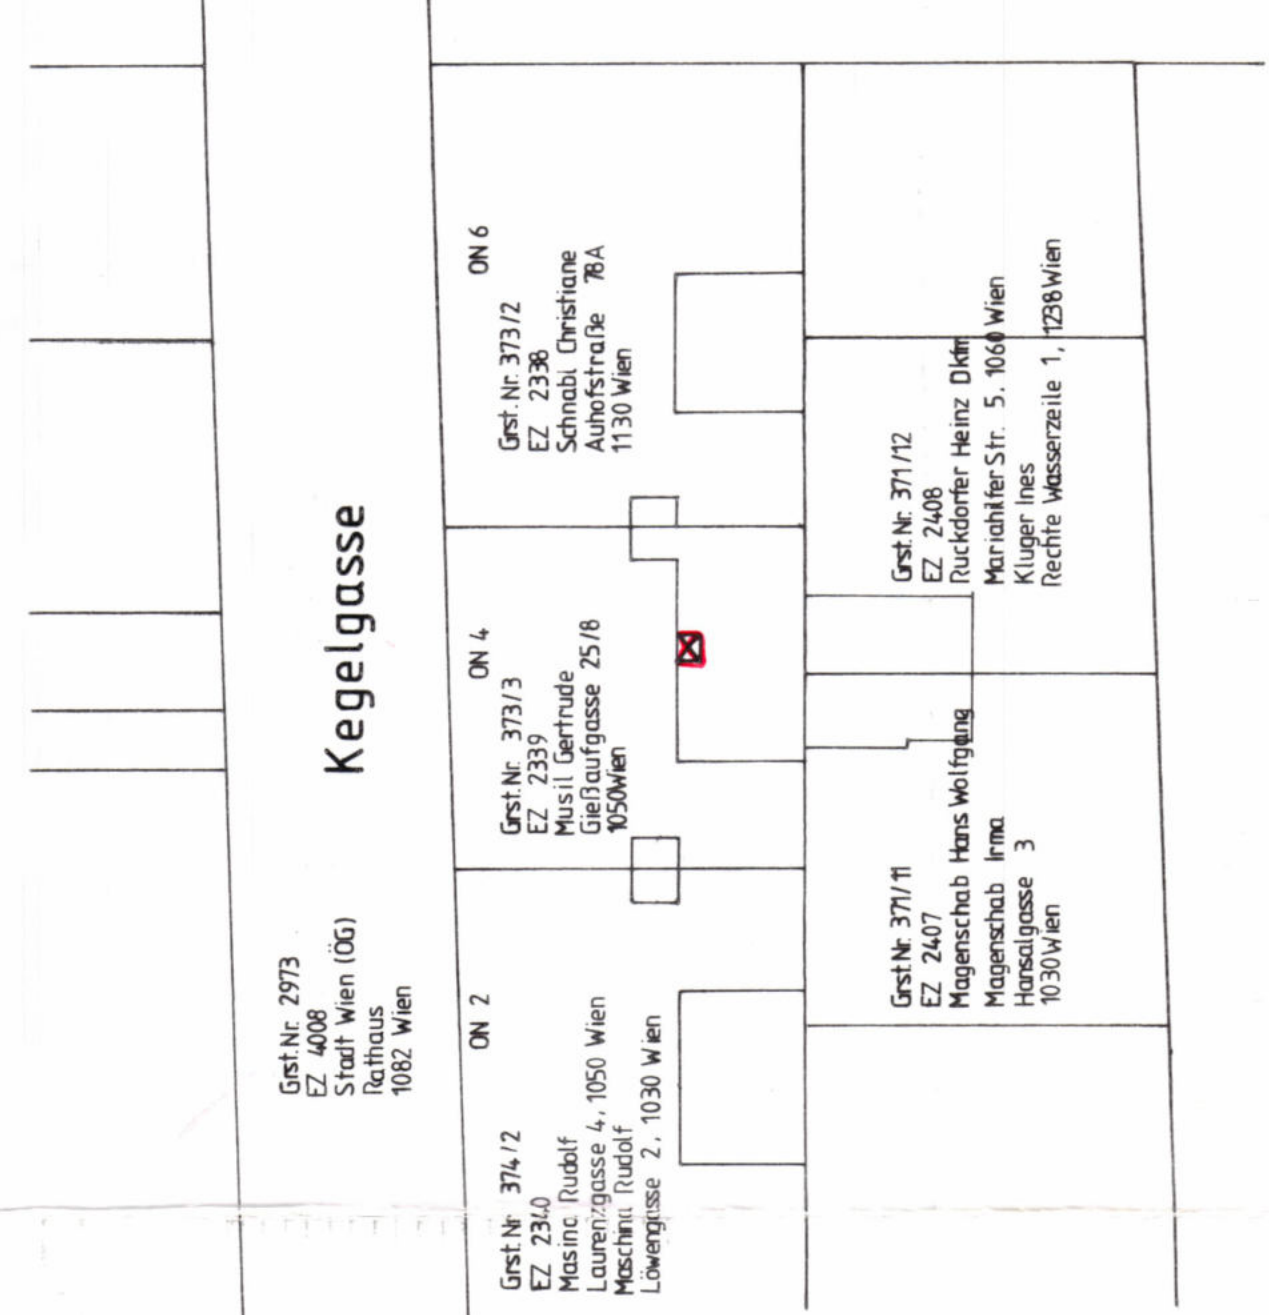


HOFANSICHT

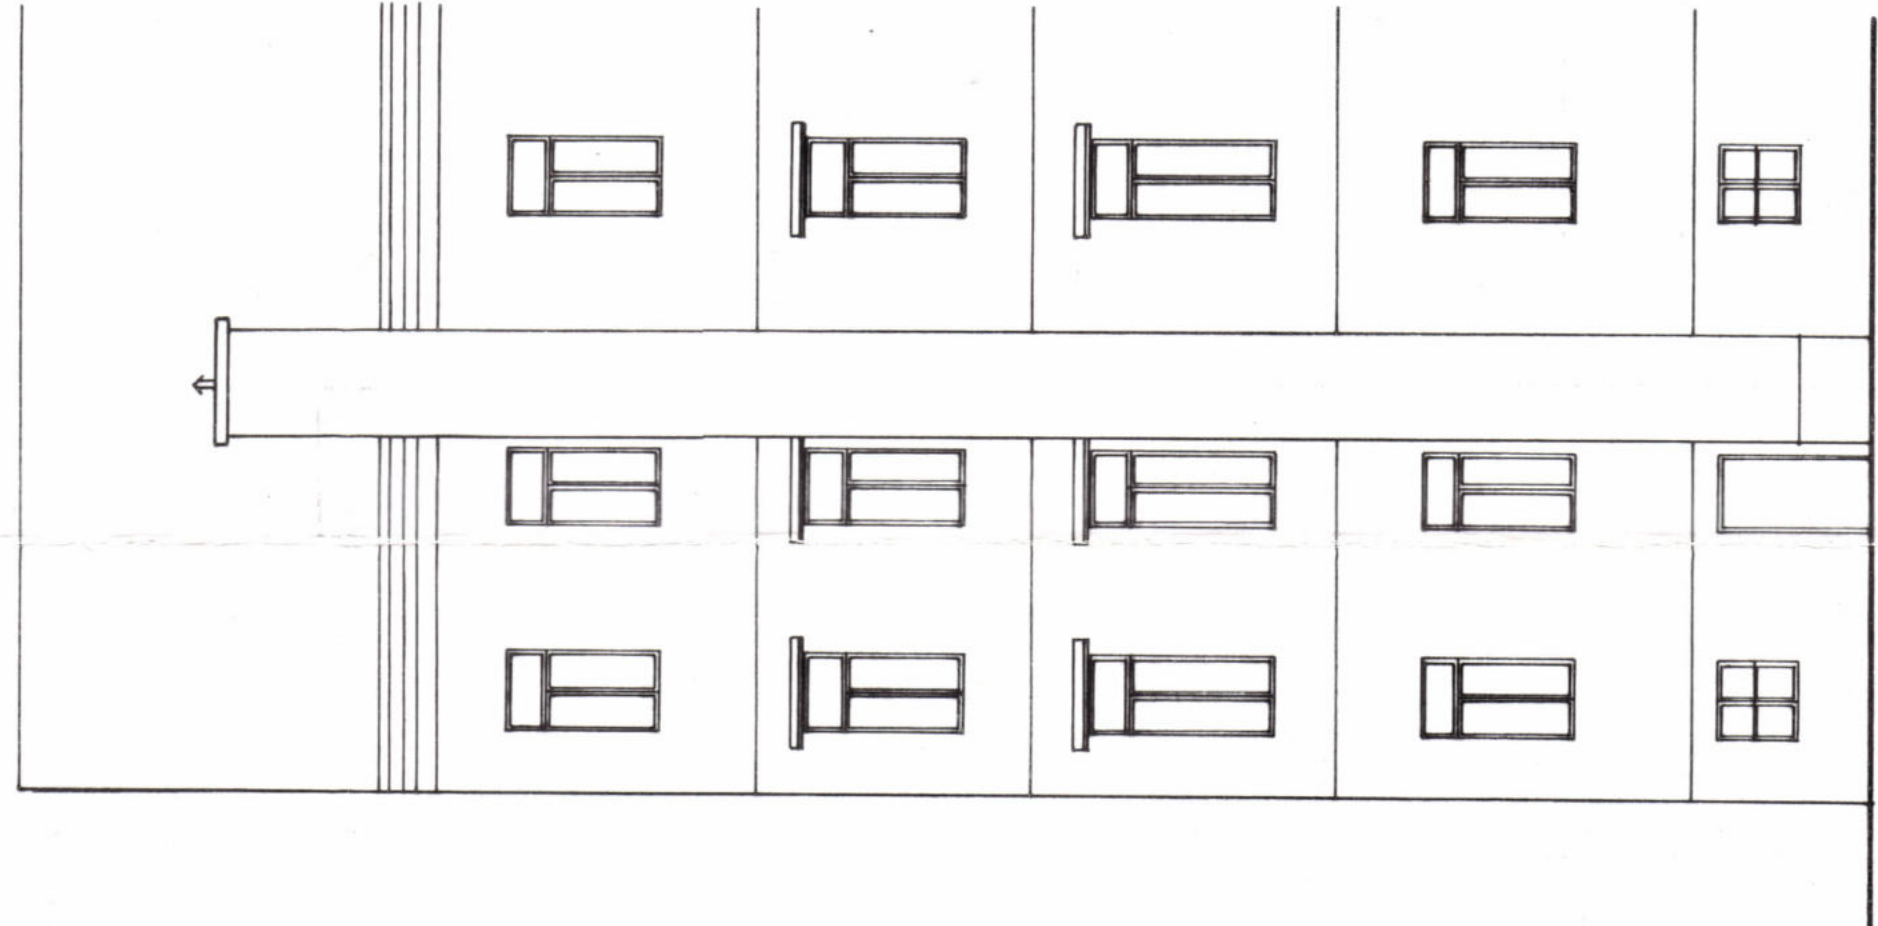


SCHNITT

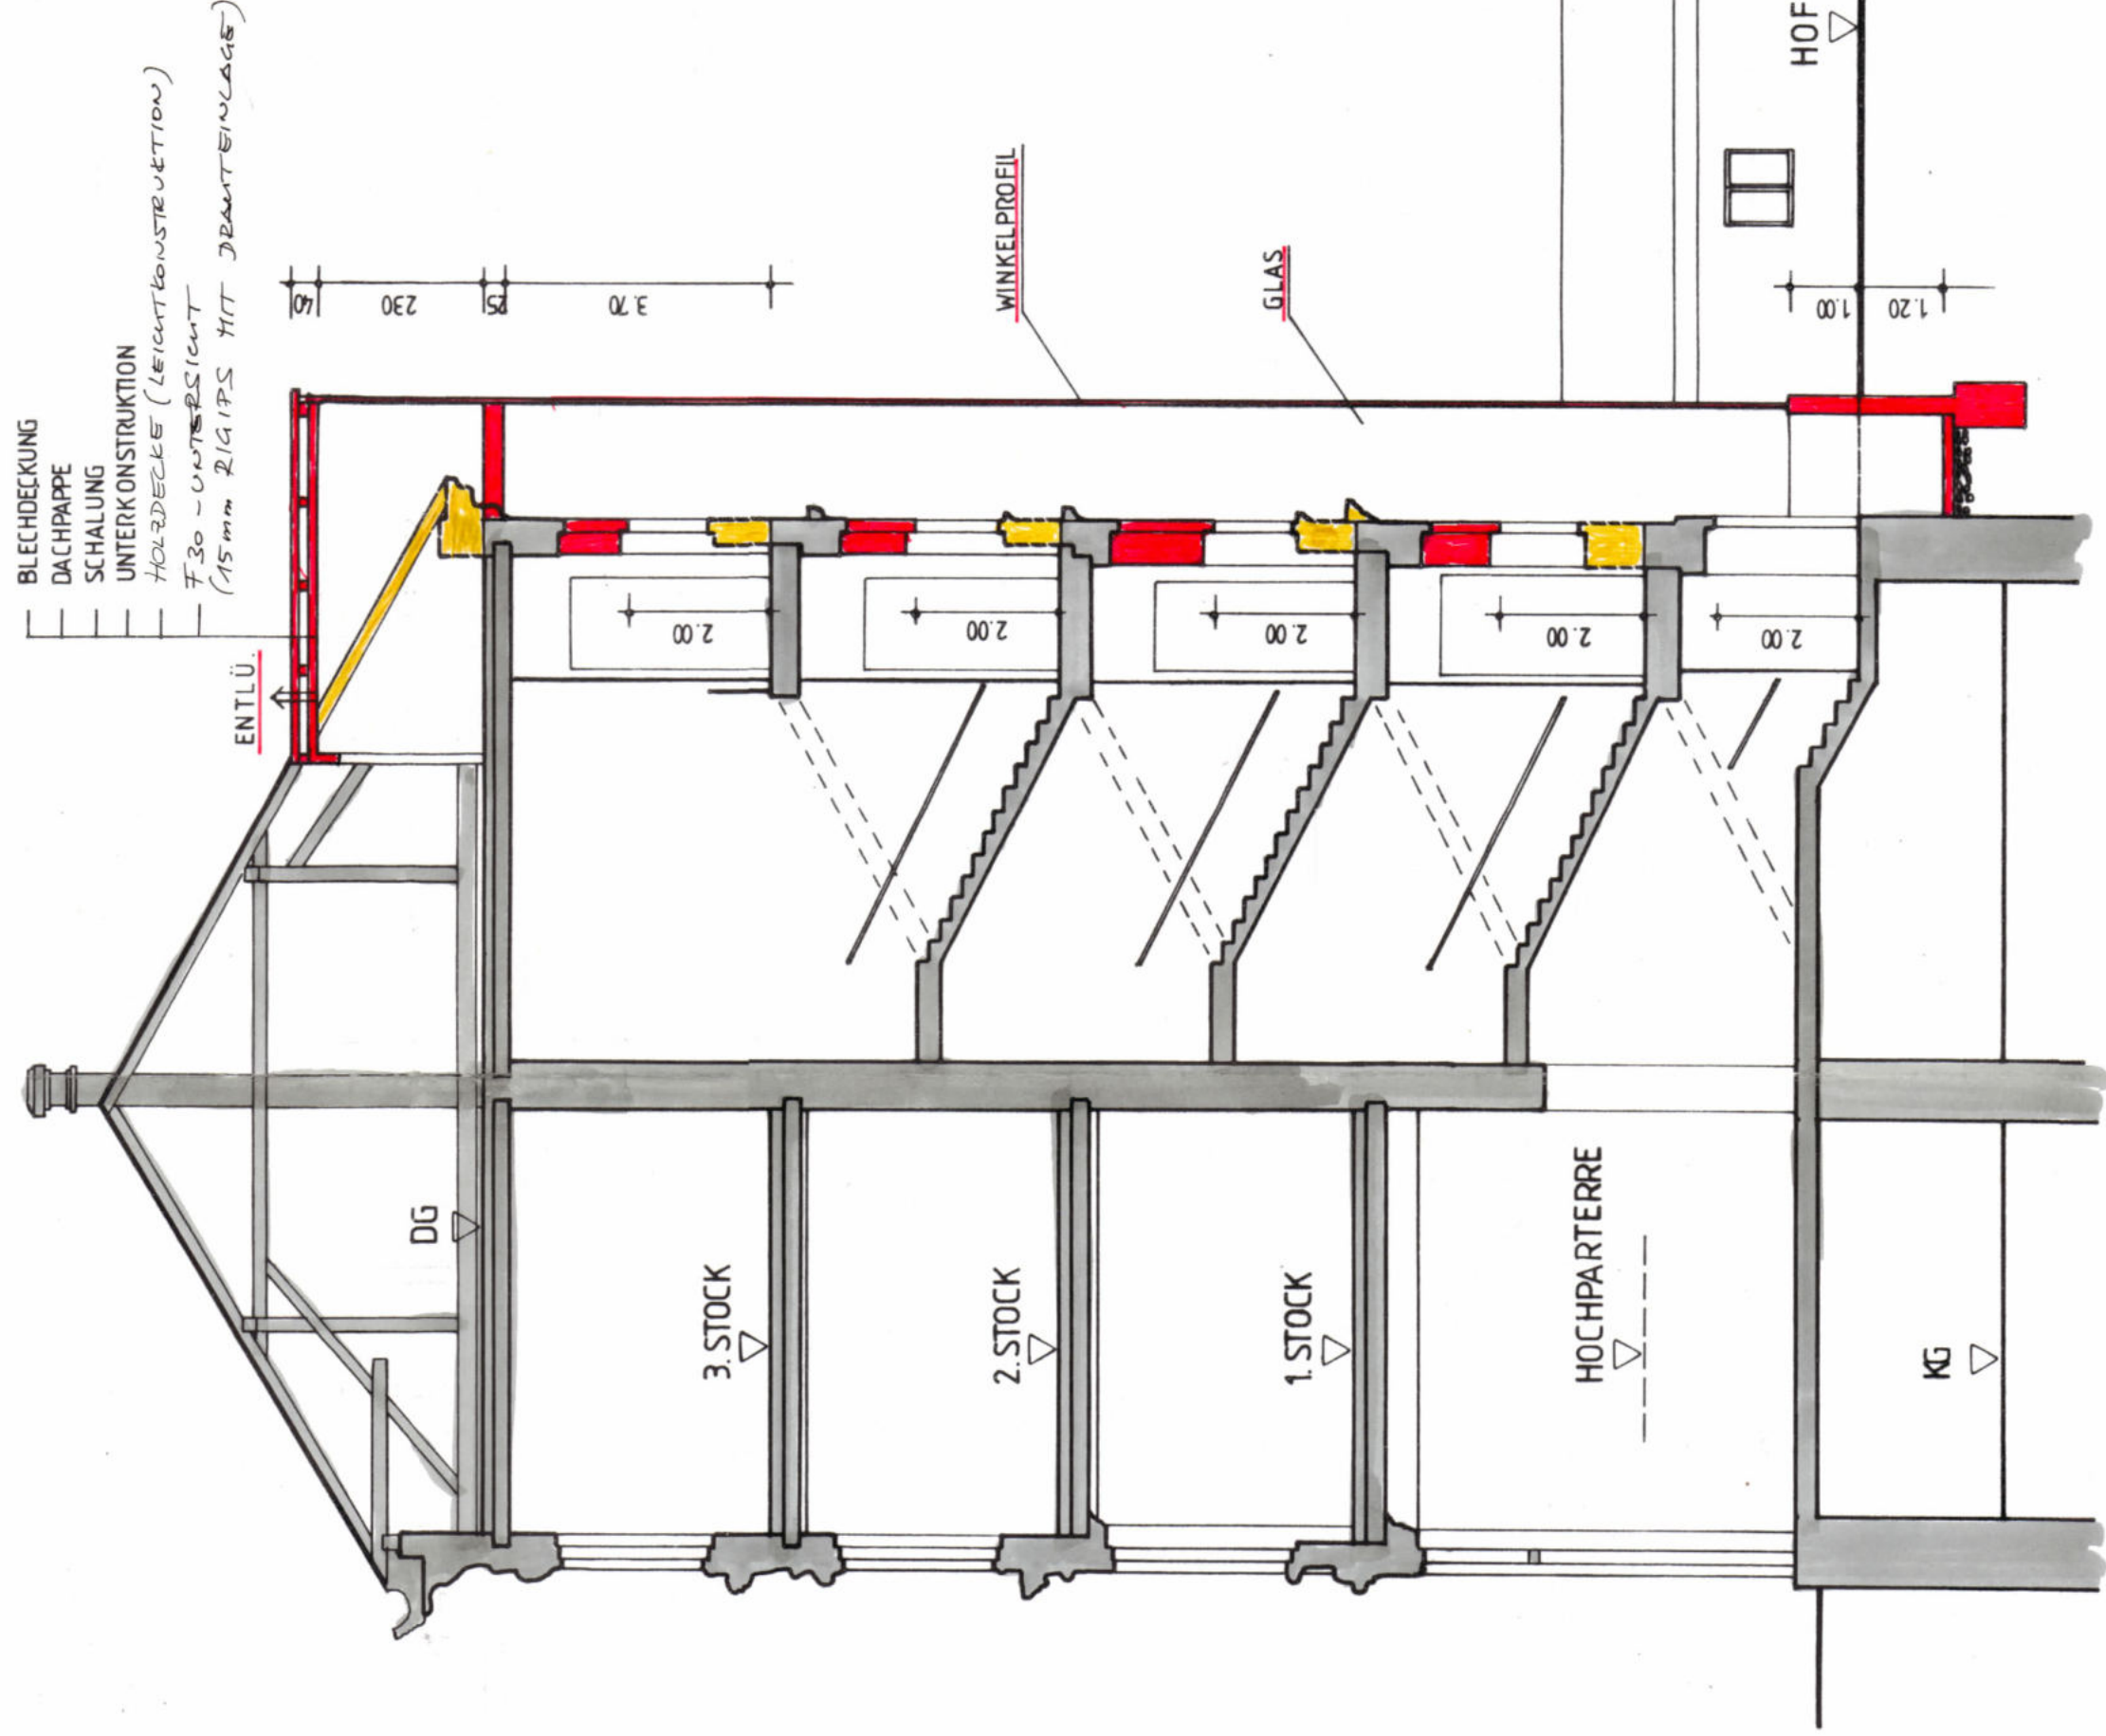

HOCHPARTERRE

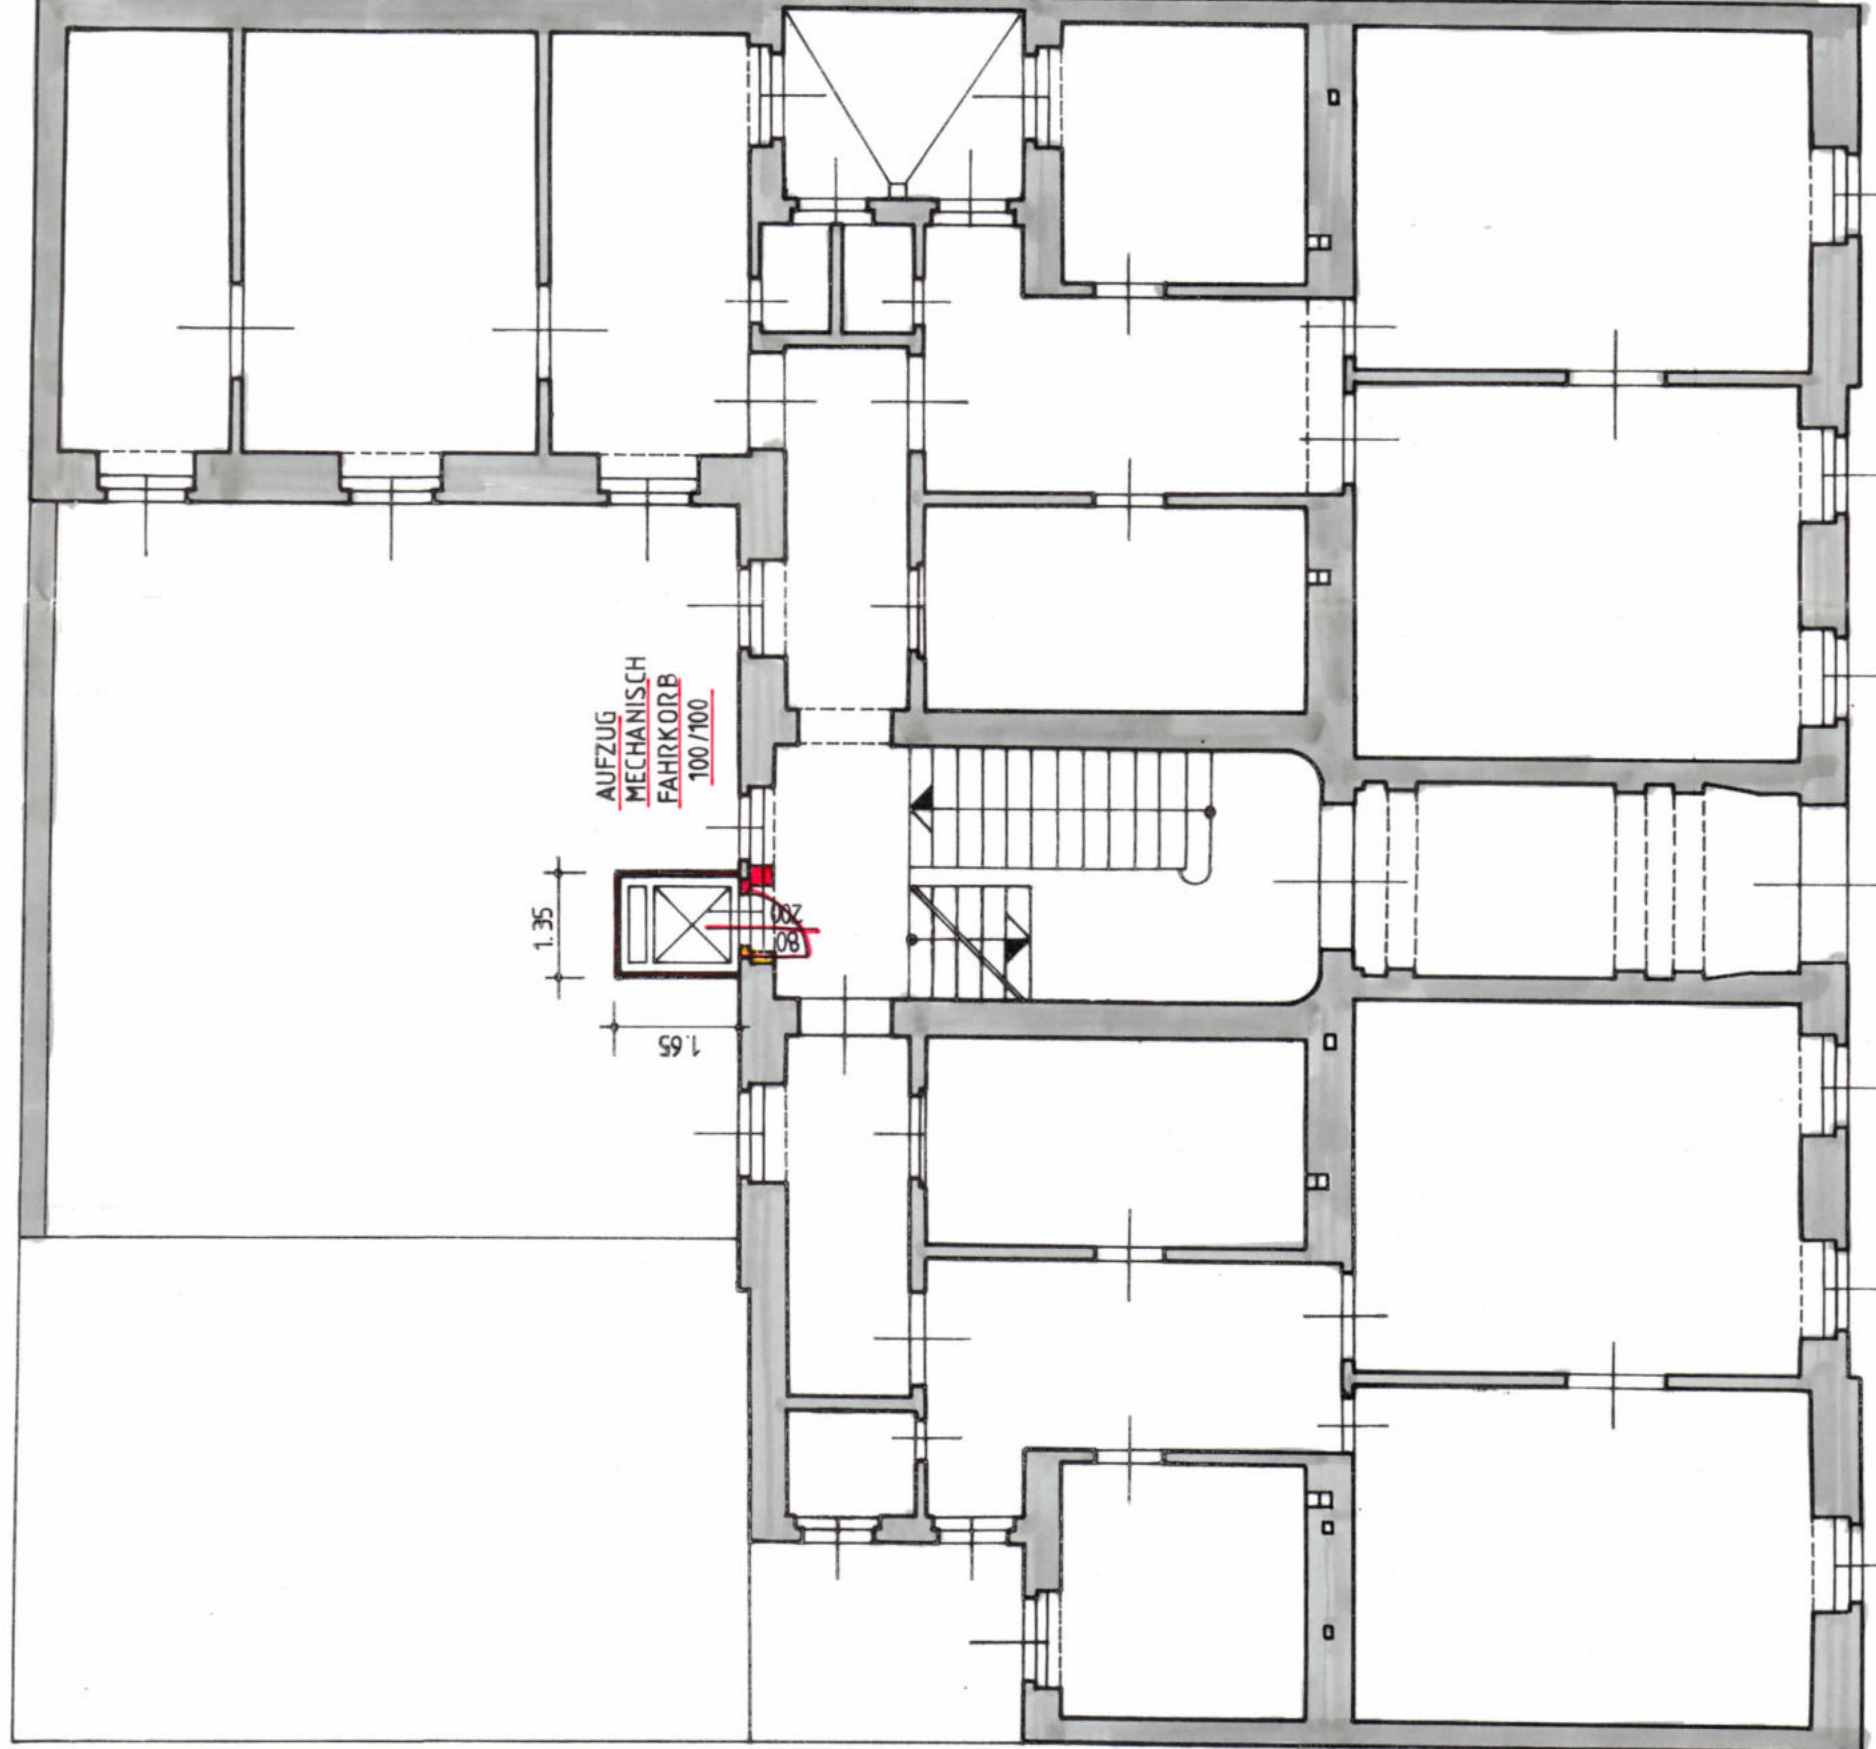

KELLER

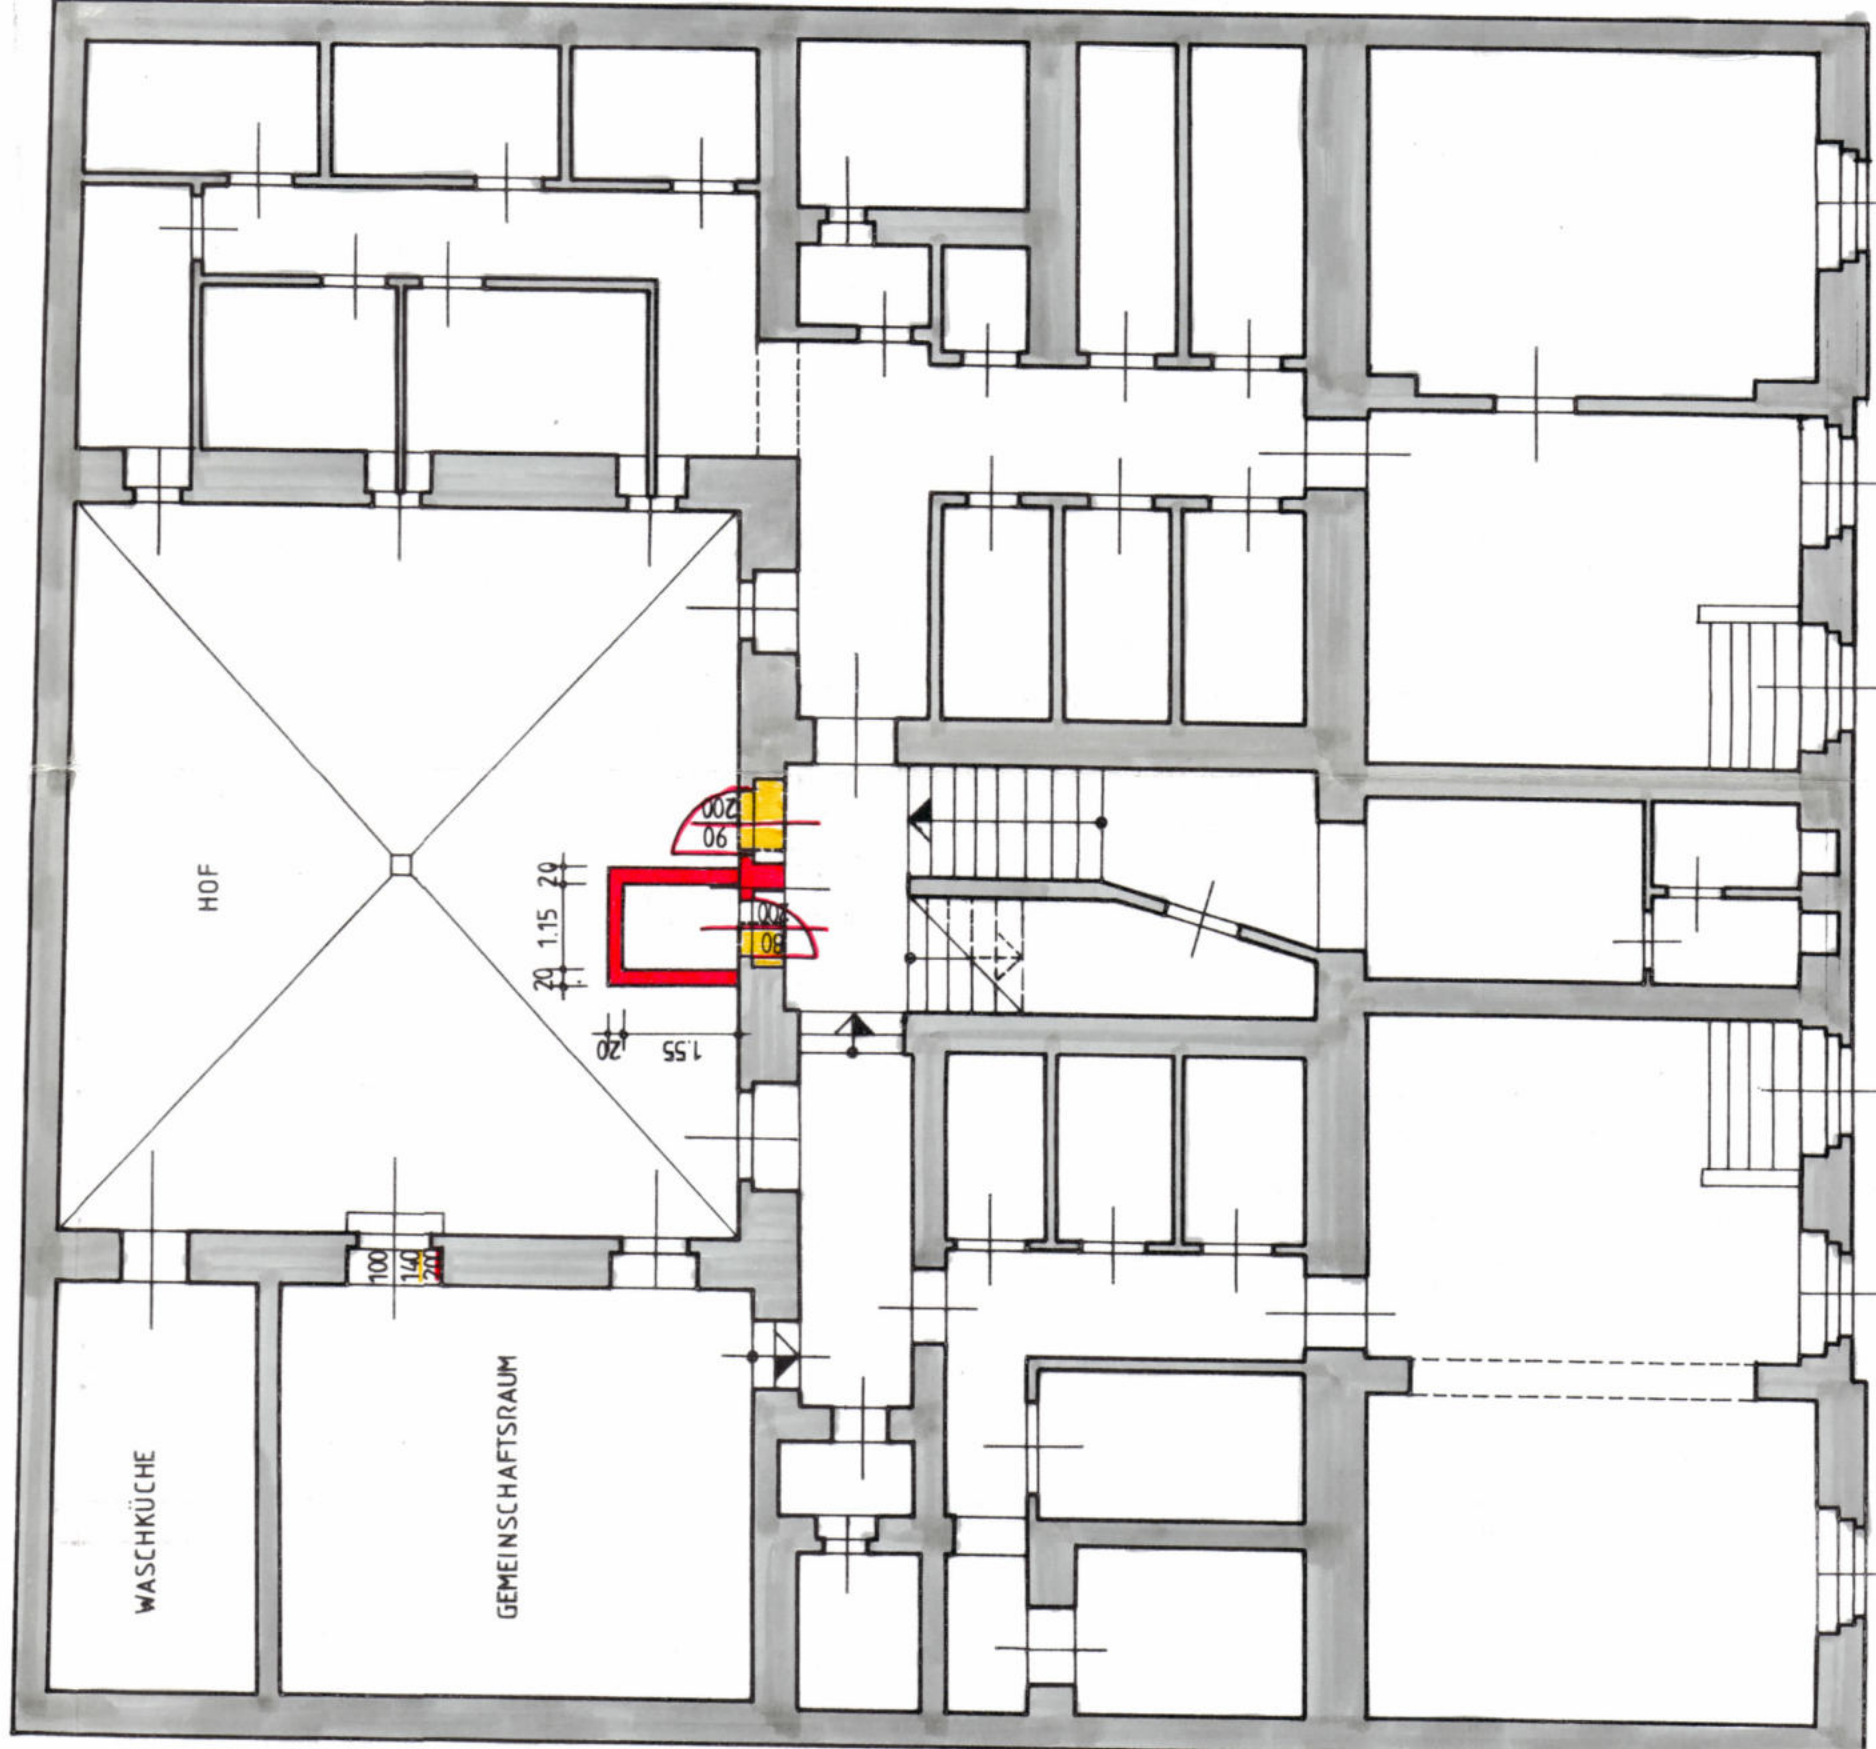

PARIE

EINREICHPLAN

M 1: 100

ÜBER BAULICHE ÄNDERUNGEN IM HAUSE 1030 WIEN,
KEGELGASSE 4 FÜR FRAU GERTRUDE MUSIL IN
1050 WIEN, GIESZAUFASSE 25/8

EZ 2339 KG LANDSTRASSE

BAUWERBER UND GRUNDEIGENTUMER

BAUFÜHRER

PLANVERFASER

BAUBEHÖRDE

HUBER

Magistratsabteilung 37

Magistratsabteilung 37

Magistratsabteilung 37

Magistratsabteilung 37

Magistratsabteilung 37

Wien, AM 3 AUGUST 1987