
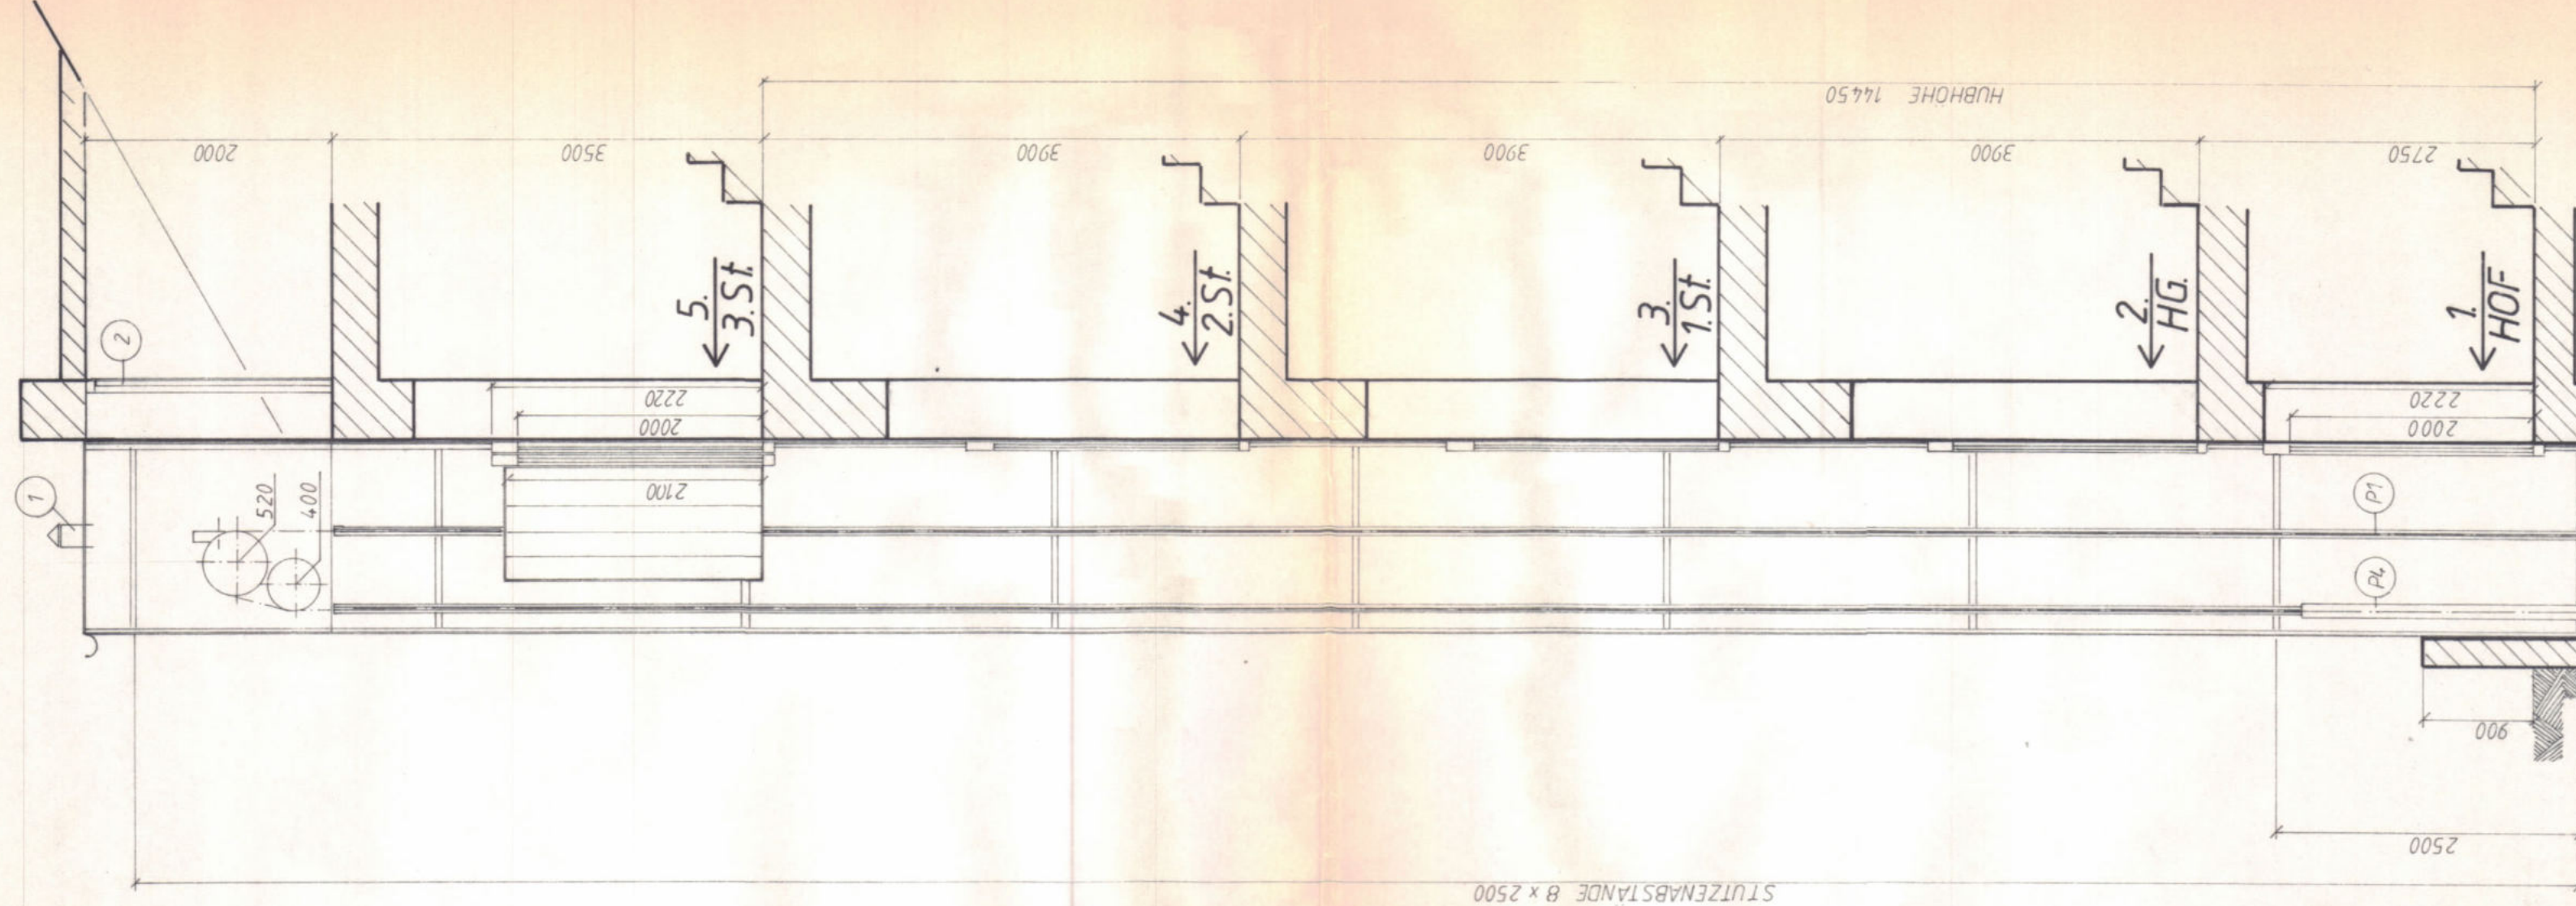
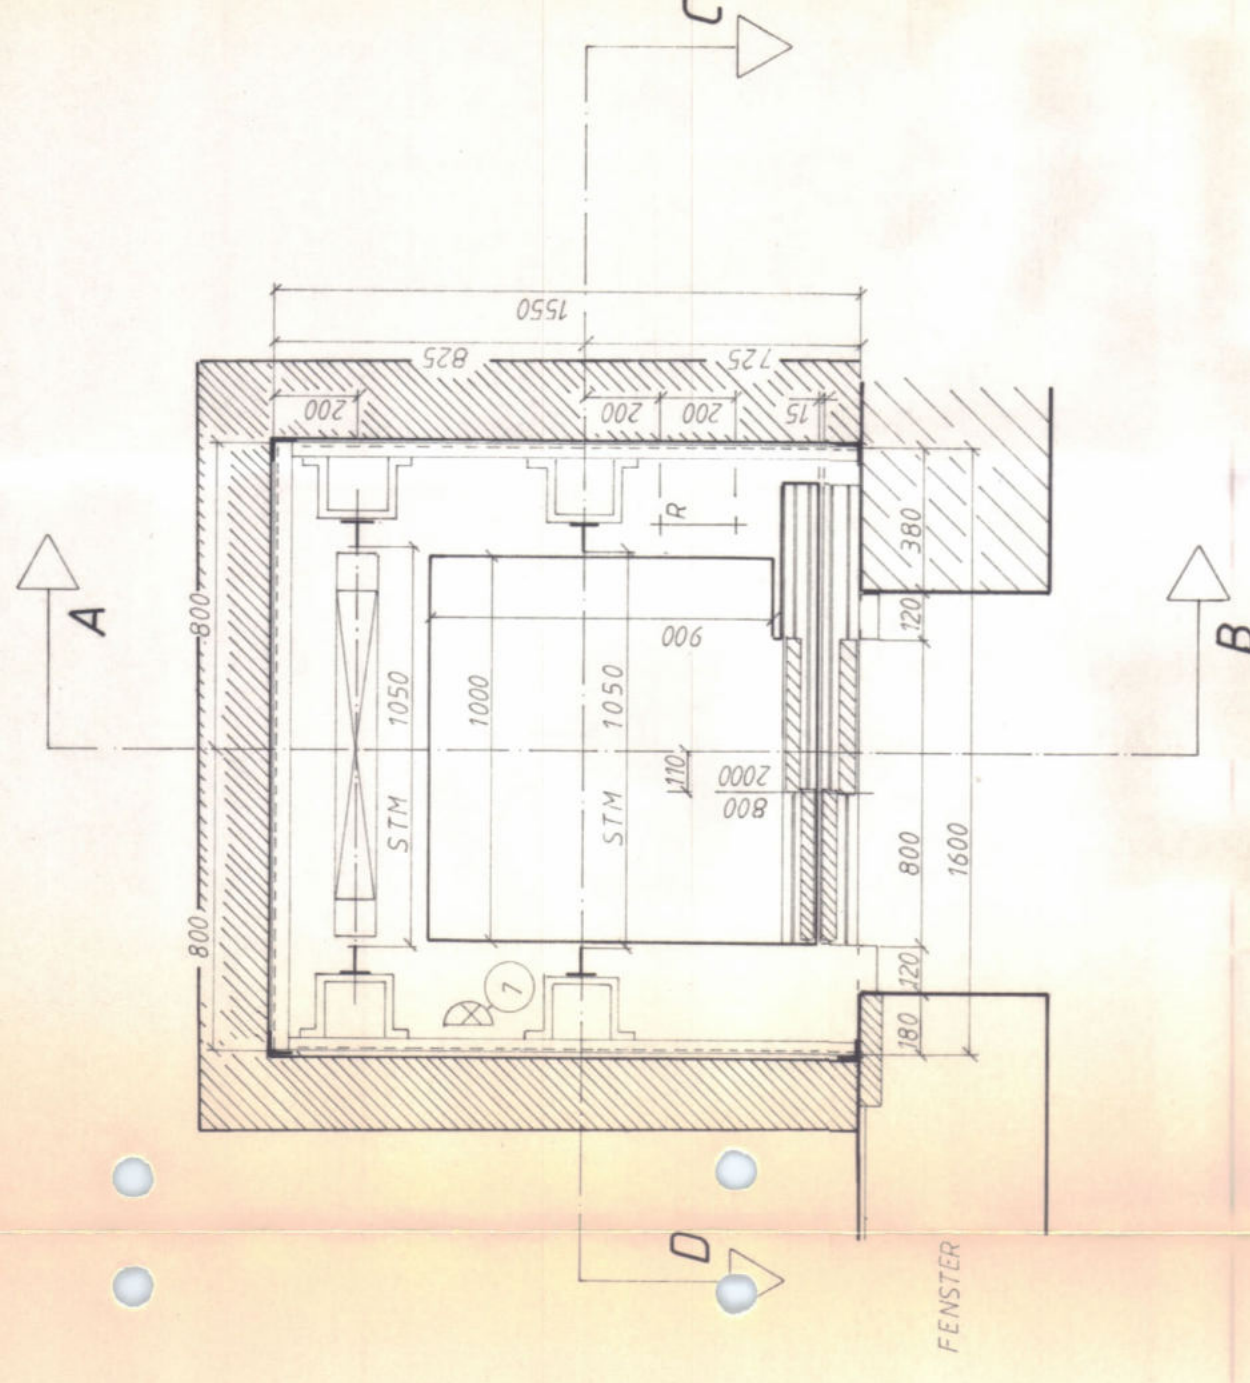


SCHNITT C-D
M 1:50

LAGEPLAN


TWR-GRUNDRISS
M 1:20 ZUGANG ÜBER DACHBODEN

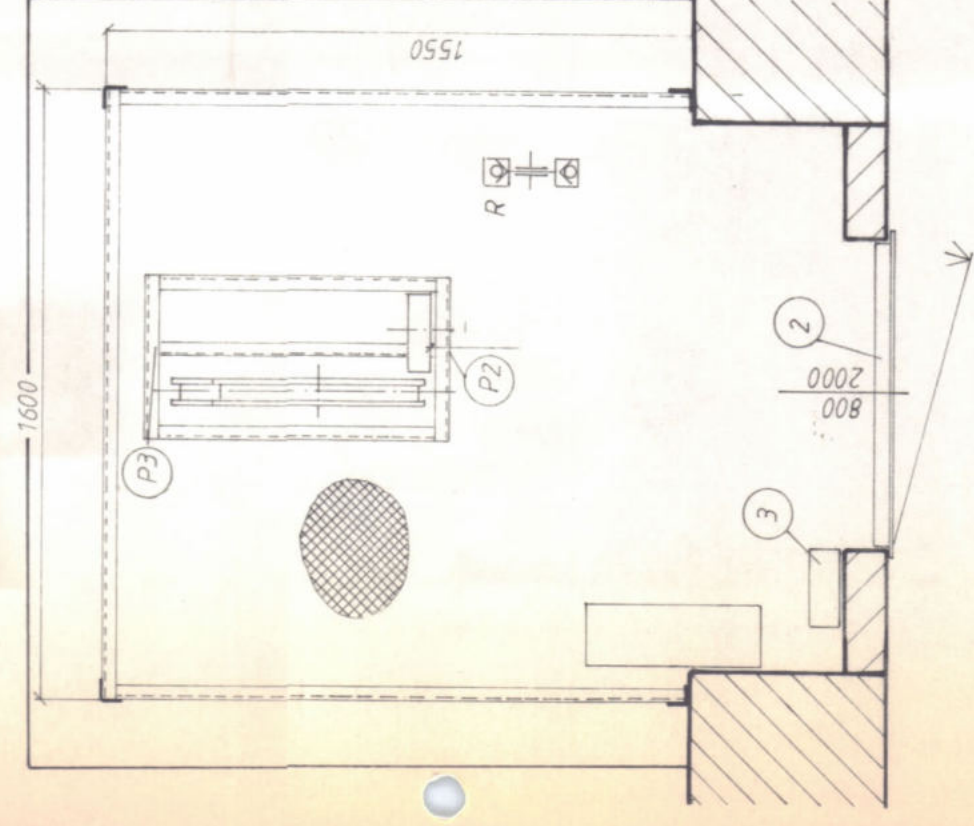

Magistrat der Stadt Wien
Magistratsabteilung 35
Allgemeine Baupolizeigenossheiten
Hierauf bezieht sich der Bescheid
MA35- A / 3-126/88
1988-06-17

Wien, _____ Für den Abteilungsleiter:

Für die Richtigkeit der Ausfertigung: Dipl. Ing. Molin e. h.
Der Kanzleileiter: Oberstadtbaurat
I. V. Jungmann

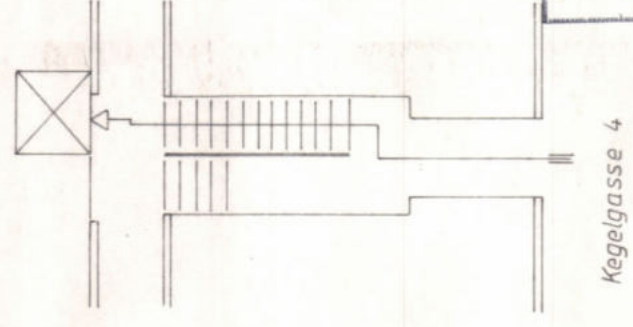

Magistrat der Stadt Wien
Magistralabteilung
20, D 60 75
120 Wien


AUF VERTRAGSGRUNDLAGE GEPRÜFT
 }
 FACHTECHNISCHE
 REGIERUNG
 G. ZL.: T 7482/68
 WIEN: 29. 4. 1988
 DRUCK- u. TECHN. ERNST ZEIBIG
 DRUCKEREI FÜR MASCHINENBAU
 1010 WIEN, ALTE PERLE 10
 (AUFZUGSBAU) 10222 35 15 01

EINRICHTUNGEN UND BAUSEITIGE VORKEHRUNGEN

- 1 Ständig wirkende Ba. u. Zirkulation ins Freie min. 300 cm², im Treibwerksraum, bei für Luftdurchsatz max. 80/h, dabei Raumtemperatur min.+10°C
- 2 Versperbare einseitige Pflanz- max. +30°C
max. +35°C -min +15°C-pure bzw. ausbalancierte Eiseneindeckung.
- 3 Stromzuführung laut NORM (Informationsblatt)
- 4 Gelände- gebietstestbedingender Schwenker- Schutzkette
- 5 Umkehrung laut Informationsblatt) NORM.
- 6 Podeste zwischen den Ruten müssen dauerhaft gerat sein (z.B. Hartputz mit Ölstrich) oder eine Holzbohlen-Auslage-Geländeinformationsblatt).
- 7 Schattenbeleuchtung laut UNORM (Informationsblatt).
- 8 Montageplatz - heckter-OK 60 m-v. Treibwerksabdeckte- heckter-NN.
- 9 Montageaufbau mit abwechselndem Hühner- diffusenbelichtung
- 10 Betonsockel laut Monteurangaben
- 11 Eisenblech- einbauelement mit Treibwerks- Einbauten
- 12 Nicht verschwinden- Eisenblecher
- 13 Gittereinbauelement - verschieben) 10mm-M. - 15mm-Drehachse
- 14 Schallisolierung
- 15 Differenziertheit für Graben- Treibwerksraum- Installationenante 150mm hoch
- 16 Beutetextur- bittensches Stahlrohr- 01 bzw.-wasserdicht.

The diagram shows a frame structure with a horizontal beam and a vertical column. Horizontal loads are applied to the beam at various points, labeled with values like 9,75, 8,8, 8,8, 7,67, and 9,4. Internal force diagrams are shown on the beam and column, with labels like H1, H2, and H3 indicating specific points or values. The structure is supported by a fixed base.

[illegible]