
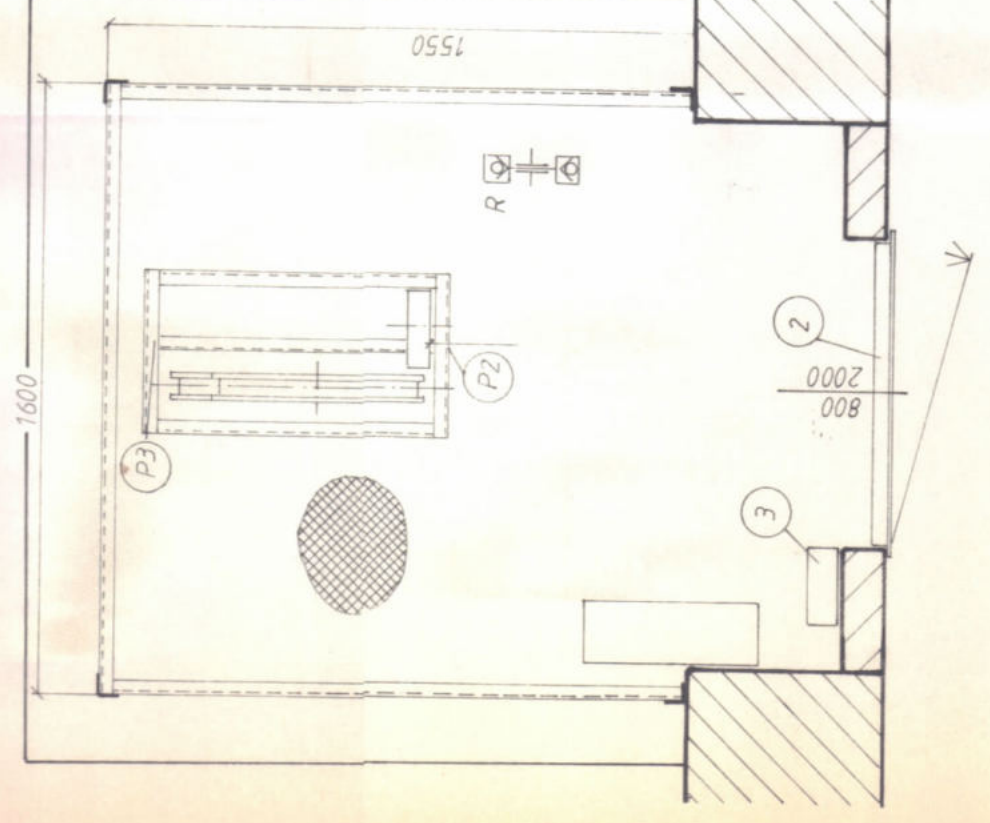
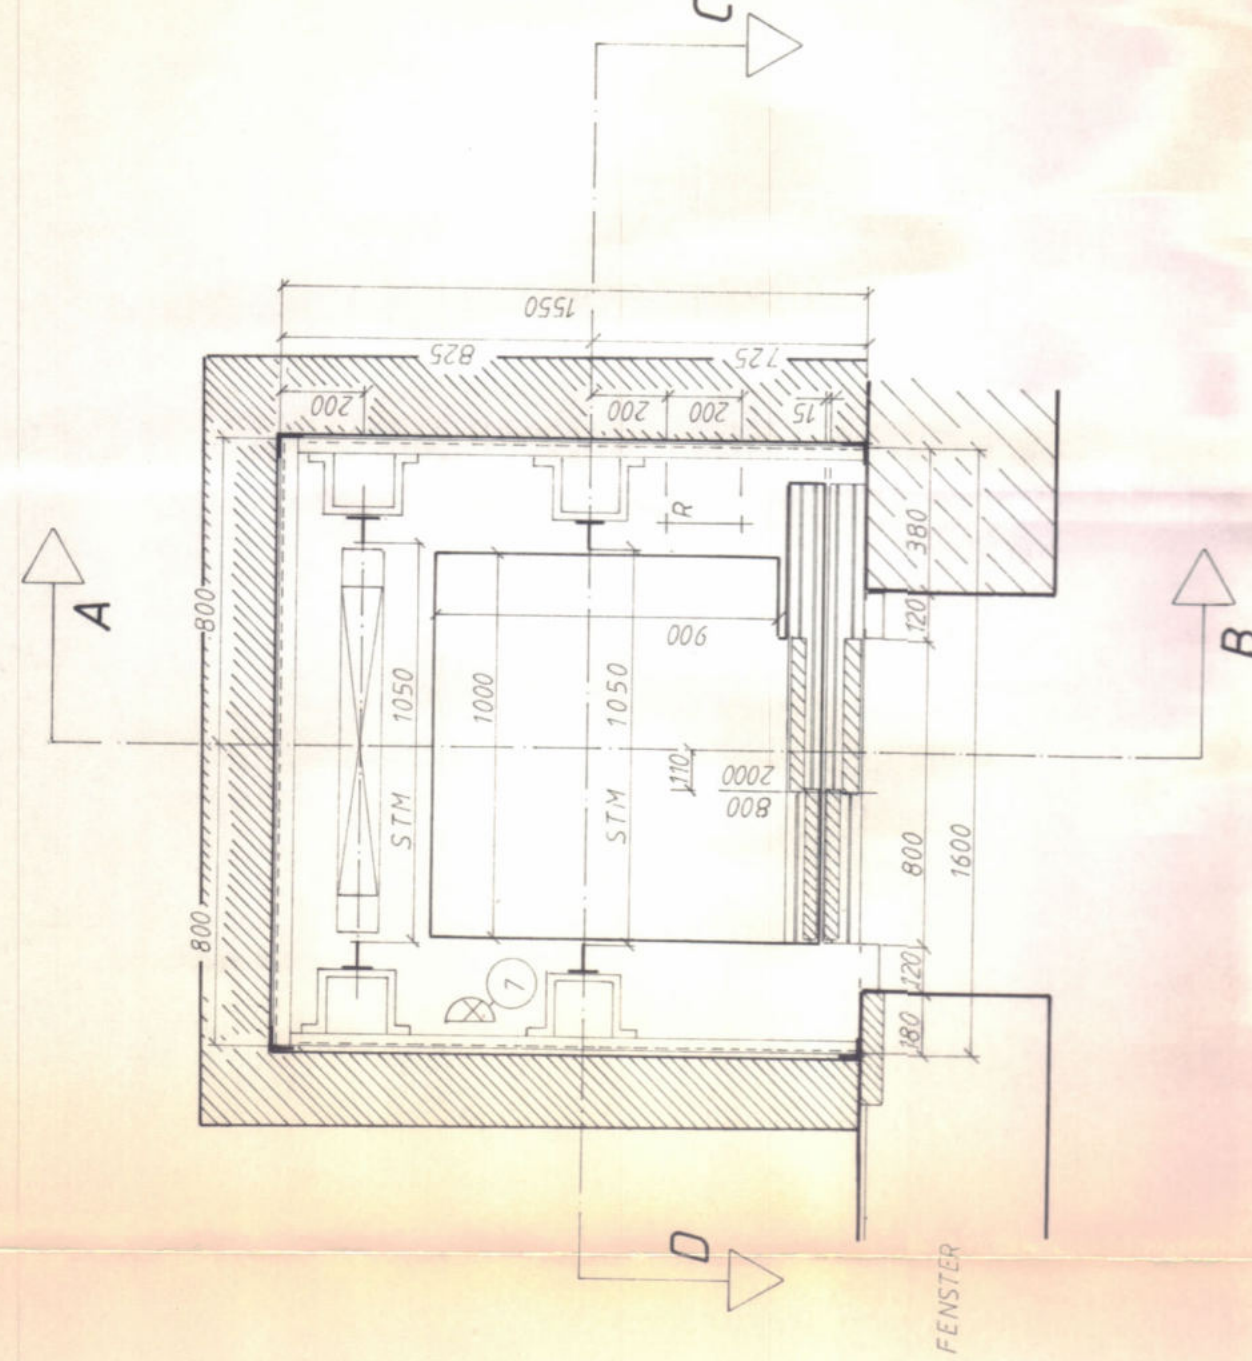
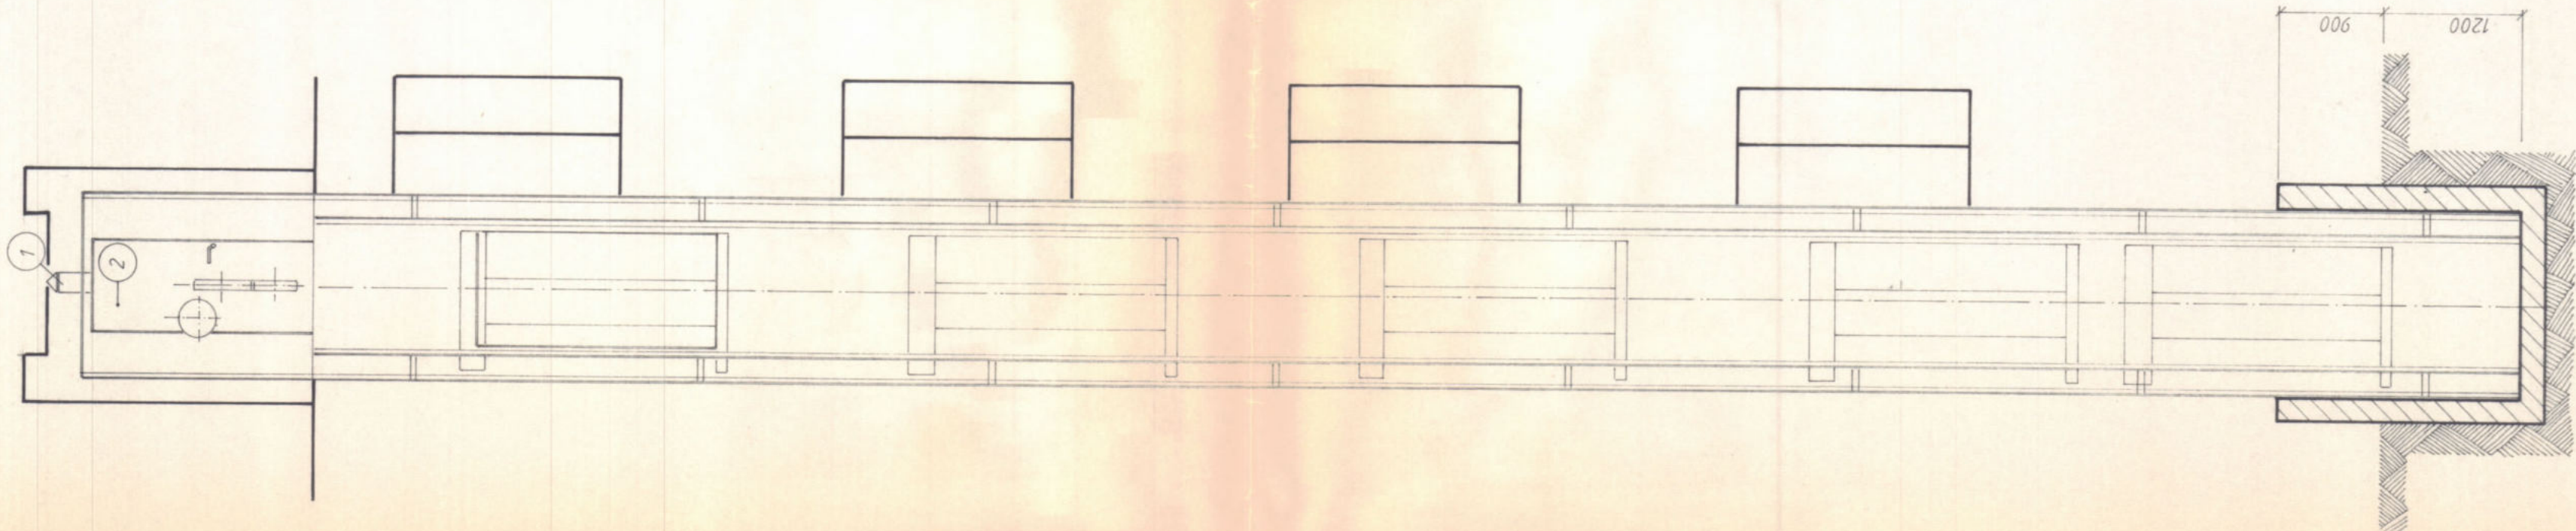


SCHNITT C-D
M 1:50

LAGEPLAN

Dipl. Ing. Molin ~~e.h.~~
Oberstadtbaurat

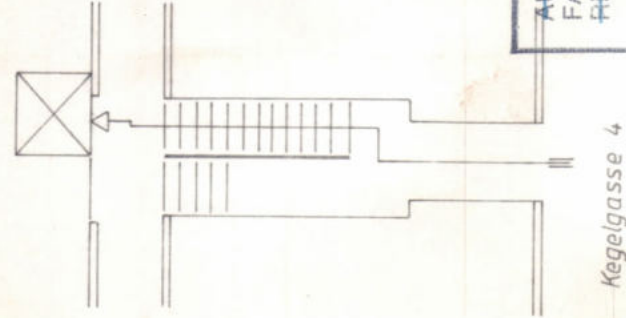

AUF VERTRAGSMÄSSIGKEIT
 FACHTECHNISCH
 RECHNERISCH

GEPRÜFT

O. ZL.: T 782/88
 WIEN, 29.4.1988

DISCIPLINE DER TECHN. ERNST ZEIBIG
 INGENIEURWISSENSCHAFTEN MASCHINENBAU
 AUFGABENSTELLUNG (NACHRICHTEN) (NACHRICHTEN)
 A. 1180 W. 22.03.88

EINRICHTUNGEN UND BAUSEITIGE VORKEHRUNGEN

- 1 Ständig wirkende Be- u. Entlüftung ins Freie min. 300 cm², im Triebwerkraum, bemessen für abzuführende Wärmemenge v. kJ/h, dabei Raumtemperatur min.+10°C max.+35°C, min.+15°C max.+30°C.
 - 2 Verwendbare elektrische FHR-Türe bzw. ausbaufähige Eisenabdeckung.
 - 3 Stromzuleitung laut NORM (Informationsblatt)
 - 4 Gehäuse der elektrischen Leitungen schützen Siebmetallgitter
 - 5 Steuerung laut Informationsblatt - NORM.
 - 6 Leuchte nach dem Typen müssen durchgef. sein (z.B. Halogen mit Glühlampe, wenn Glühlampe aufgef. durchschaltbar ist).
 - 7 Schachtleuchtung laut DIN EN (Informationsblatt).
 - 8 Montageabstände: bei 50 mm v. Triebwerkraum abgehängte Abl.
 - 9 Montageabstände: bei abgehängten FHR-Abdeckungen
 - 10 Betonsocke l. u. u. Montagenaben
 - 11 Elektrische Kabel zusammen mit Betonsocke
 - 12 Nicht verputzte Betondecke
 - 13 Gitterabstand: vorgegeben 10 mm Abl. 5 mm Druckbetondecke
 - 14 Schutzbleche
 - 15 Gitter: Abstände für Gitter, Triebwerkraum, Inbetriebnahme 150 mm hoch
 - 16 Betondecke: Betondecke Stahlblech 41 bzw. verschiebbar.
- P Betriebs- und Fanplatten incl. 30% Stützlast ohne Eigengewicht von Betonsocken, Decken, Hauptträgern usw.

Horizontalkräfte bei jeder Stützenreihe wirkend				ANSCHRIFT	
DER BAUWEISER		UNTERSCHRIFT		PAUL PADELEK architekt, Gesellschaft für FRIEDRICH & PLATZ, G. m. b. H. 1000 WIEN, LANGEASSE 50	
DER HAUSEIGENTÜMER				HTABORSKY-AUFZÜGE 1100 WIEN, LEEBGASSE 8 TEL. 78.74.44 HUBER bet und senkrt Ing. F. u. H. HUBER Bauges. m. b. H. 1100 Wien, Jägerasse 27 02-44 93	
DER PLANVERFASSER UND AUFGEBERAUER				HTABORSKY-AUFZÜGE 1100 WIEN, LEEBGASSE 8	
DER BAUFÜHRER FÜR DIE BAUWEISERARBEITEN				Ing. F. u. H. HUBER Bauges. m. b. H. 1100 Wien, Jägerasse 27 02-44 93	
DER GRUNDEIGENTÜMER				HTABORSKY-AUFZÜGE 1100-WIEN LEEBGASSE 80	
Art des Aufzuges: PERSONENAUFZUG		Tragkraft: 320 kp oder 4 Personen		Zeichnungen: 2/2	
Auftraggeber: F. Gedrups, MUEHL 1050-WIEN, GRIENGASSE 25		Höhe: 14,45 m		Fahr. Nr.: 2/2	
Aufstellungsort: 1030 - WIEN, KEGELGASSE 4		Wahl: 5		Motorleistung	
		Vz. 000 02 2		DK-Aufzugsystem Elektronik	