

Ebn

Magistrat der Stadt Wien
Magistratsabteilung 37
Baupolizei
Außenstelle für den 3., 4. und 5. Bezirk
Am Modenapark 1-2
1031 Wien

MA 37/3 - Kegelgasse 4/2577/87

Wien, 12. Jänner 1988

3. Bez., Kegelgasse ONr. 4 Gst.
Nr. 373/3 in EZ 2339 des Grundbuches
der Kat. Gem. Landstraße

Bauliche Änderungen

Baubewilligung

+ 991/87 ✓
+ 1002/87 ✓

AUV. 26.3.1980
Wurde ausgeführt
Einlegen in EZ 2339/III
F.d. Abb.
EBR

BESCHIED

Gemäß § 70 der Bauordnung für Wien (BO) wird die Bewilligung erteilt, nach den mit dem amtlichen Sichtvermerk versehenen Plänen auf der im Betreff genannten Liegenschaft die nachstehend beschriebene Bauführung vorzunehmen:

Vom Hochparterre bis in den 3. Stock soll an der hofseitigen Außenwand ein Aufzugsschacht für den Einbau eines Personenaufzuges hergestellt werden. In den Wohnungen Top Nr. 11A im 2. Stock und Top Nr. 19 im 3. Stock sollen durch Aufstellen von Scheidewänden Sanitärräume eingebaut werden.

Vorgeschrieben wird:

- ✓ 1) Der Bauführer hat gemäß § 124, Abs. 2 BO den Beginn der Bauführung mindestens 3 Tage vorher der jeweiligen Außenstelle der MA 37 und weiters dem Arbeitsinspektorat für Bauarbeiten (Fichtegasse 11 - 1010 Wien) anzuzeigen.
- 2) Mindestens einen Monat vor Beginn der Bauarbeiten ist gemäß § 127, Abs. 1, lit. b BO über die Festigkeit der Fundamente, der Tragkonstruktionen und der sonstigen besonders beanspruchten Bauteile eine statische Berechnung samt Konstruktionsplänen der MA 35-S (Dresdner Straße 75, 1200 Wien) vorzulegen. Gleichzeitig mit der statischen Berechnung ist vom Bauwerber eine bewilligte Planparie der Baubewilligung oder ein vom Planverfasser gefertigtes Gleichstück zu übermitteln.
- 3) Der Aufzugsschacht ist unbrennbar auszuführen.
- 4) Die Stahlkonstruktion von Aufzugsschächten im Freien ist mit einer Blitzschutzeinrichtung auszustatten.
- 5) Die Wände und Decken von Aufzugstriebwerksräumen müssen mindestens feuerhemmend und der Fußboden dieser Räume aus unbrennbaren Material ausgeführt werden.
- 6) Der Zugang zu Aufzugstriebwerksräumen muß direkt von allgemein zugänglichen Räumen der Baulichkeit aus über Stiegen oder befestigte Leitern erfolgen.

- 7) Eingangstüren zu Triebwerksräumen müssen mindestens 1,80 m hoch sein. Für Türen und Einstiege in Verbindungswegen zu einem Triebwerksraum gelten die gleichen Mindestausmaße.
- 8) Die Raumhöhe im Bereich des Standortes zur Betätigung des Handrades und zur Wartung der Schaltgeräte muß mindestens 1,80 m betragen.
- 9) Der waagrechte Abstand des Motorwellenendes muß zur Umfassungswand mindestens 60 cm, zu Schaltgeräten mindestens 80 cm betragen.
- 10) Triebwerksräume sind direkt aus dem Freien zu belüften; der Lüftungsquerschnitt muß mindestens 200 cm² betragen.
- 11) Die Schachtgrube muß mindestens 1,20 m tief sein.
- 12) Vom Erfordernis einer Benützungsbewilligung wird gemäß § 128 Abs. 1 BO Abstand genommen; es ist jedoch die Vollendung der Bauführung bei der Baubehörde schriftlich anzuzeigen.

B e g r ü n d u n g

Der dem Bescheide zugrunde gelegte Sachverhalt ist den eingereichten Plänen und dem Ergebnis des durchgeführten Ermittlungsverfahrens entnommen. Die Bauführung ist nach den bestehenden Rechtsvorschriften zulässig. Die vorgeschriebenen Auflagen sind in der Bauordnung für Wien und den einschlägigen Nebengesetzen begründet.

Rechtsmittelbelehrung

Gegen diesen Bescheid kann innerhalb von zwei Wochen ab Zustellung bei diesem Amt schriftlich, telegrafisch oder fernschriftlich Berufung erhoben werden. Die Berufung hat einen begründeten Berufungsantrag zu enthalten und ist mit S 120,-- Bundesstempel zu versehen.

Hinweis auf Rechtsvorschriften:

- 1) Überdies wird auf die Vorschriften des dem Bescheide angeschlossenen Merkblattes über wichtige, bei Bauherstellungen einzuhaltende Bestimmungen hingewiesen. Hierbei wird aufmerksam gemacht, daß die einschlägigen baurechtlichen Vorschriften (Gesetze, Verordnungen, Normen), sofern im Baubewilligungsbescheid nicht anders bestimmt, auch dann auf den Bau Anwendung finden, wenn sie im Bescheid oder im Merkblatt nicht angeführt sind.
- 2) Für Aufzüge ist eine besondere Bewilligung nach dem Wiener Aufzuggesetz, LGBI. Nr. 12/53, für Ölfeuerungsanlagen eine Genehmigung nach dem Wiener Ölfeuerungsgesetz vom 22. Februar 1974, LGBI. Nr. 19/74 erforderlich, um die bei der MA 35, Gruppe A (Dresdner Straße 75, 1200 Wien) anzusuchen ist.

Die Kanaleinmündungsgebühr von 216,-- S wurde am 28. Dezember 1987 bezahlt.

Ergeht als Bescheid an:

- 1)2) Frau Gertrude Musil, z.Hd. GV. Friedrich und Padelek OHG, Lange Gasse 50, 1080 Wien als Bauwerber und Grundeigentümer unter Anschluß der Pläne A und B, des Grundbuchauszuges und eines Merkblattes

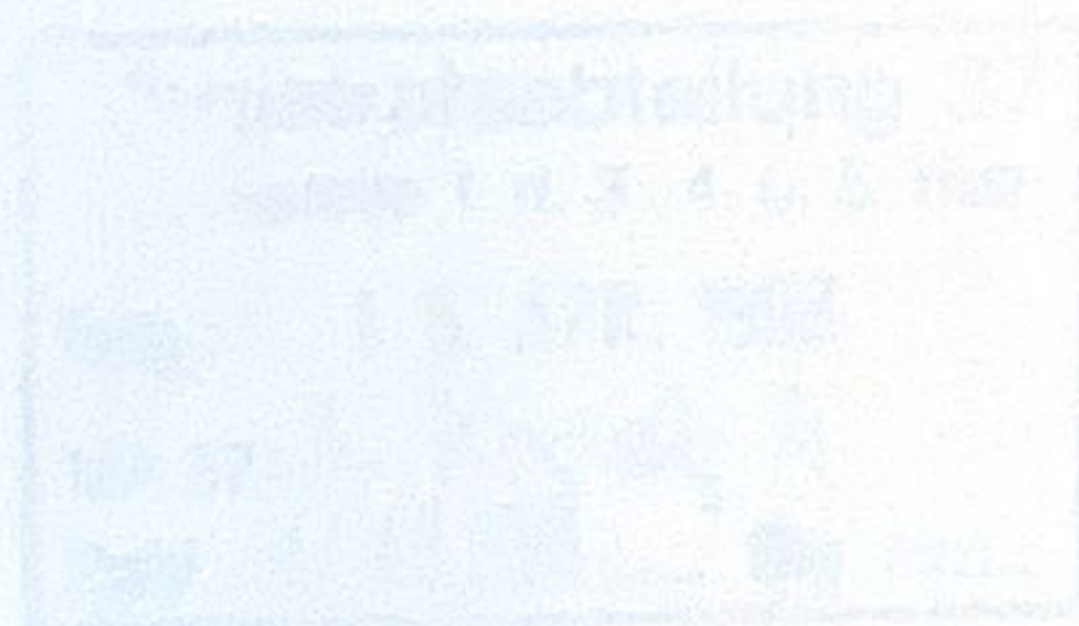
In Abschrift an:

- 3) Firma Hans Pokorny Bauges. mbH., Döblinger Hauptstraße 33a, 1190 Wien als
Bauführer unter Anschluß eines Merkblattes
- 4) Firma Domus-Plan Ges. mbH., Lange Gasse 50/12, 1080 Wien als Planverfasser
- 5) MA 37/3 unter Anschluß des Planes C
- 6/7) Finanzamt f.d. 1. Bez., Stamm-Betriebsprüfungsstelle, Nachrichtenreferat,
Vordere Zollamtsstraße 5, 1030 Wien
- 8) MA 35/S
- 9) zum Akt

Für die Richtigkeit
der Ausfertigung:

Lechner

Für den Abteilungsleiter:
Dipl.-Ing. Hahn
Oberstadtbaurat



[Handwritten signature]

✓

1577/1

Baubeginnanzeige

- 1) Baubewilligung vom _____, Zahl MA 37/3-KEGELGASSE 4/2577/87
- 2) Bauführende Firma und Adresse: _____
- 3) Ort der Baustelle: 1030 WIEN, KEGELGASSE 4
- 4) Art der Bauarbeit: UMBAU
- Baubeginn: 9.5.1988
- 5) Voraussichtliche Zahl der Beschäftigten:
- a) männliche: 3 b) weibliche: _____ c) jugendliche: _____
- 6) Obsorge für die Unterbringung der Beschäftigten in den Arbeitspausen:

HUBER
baut und saniert

Ing. F. u. H. HUBER Bauges.m.b.H.
1100 Wien, Jagdgasse 27 62 44 53

M. HAUS

Magistratsabteilung 37

Außenstelle f. d. 3., 4. u. 5. Bez.

Eing.: 05. MAI 1988

Datum: 4.5.1988

MA 37/ 3- Kegelg. 4
Zahl 1507/88 Blg. W.O.

HUBER
baut und saniert

Ing. F. u. H. HUBER Bauges.m.b.H.
1100 Wien, Jagdgasse 27 62 44 53

Unterschrift

Ergeht an:

- 1) Die Magistratsabteilung 37/3
- 2) Das Arbeitsinspektorat 1, Fichtegasse 11, 1010 Wien

1988-05-05

Ausdel - 2577/87

AD 1514 - 10 - 867 - 124321 - 20

Wir teilen Ihnen mit, daß bei o.a. Bauvorhaben die

Fa. Ing. Franz und Hans Huber Bauges.m.b.H.
1100 Wien, Jagdgasse 27/6

mit der Bauführung betraut ist.

Magistratsabteilung 37
Außenstelle f. d. 3., 4. u. 5. Bez.
Eing.: 15. APR. 1988
MA 37/3- Kegelg. 4
Zahl 1178/88 Blg. W.O.

Mit vorzüglicher Hochachtung

DOMUSPLAN
Ges.m.b.H. & Co. KG

2339

ausdel an BbW 2577/87

Bankverbindung: Erste österreichische Spar-Casse-Bank, Konto 032-36250
Gerichtsstand Wien.

DOMUS-PLAN

ALTHAUSSANIERUNGSGESELLSCHAFT
M. B. H. & CO. KG

1080 WIEN, LANGE GASSE 50/12
TEL. (0222) 48 59 28, 48 63 78

An
den Magistrat der Stadt Wien
Mag. Abteilung 37
Außenstelle f.d. 3. Bezirk
Am Modenapark 1-2
1031 Wien

Wien, 1988.04.14
KI/FE

Betrifft: 1030 Wien, Kegelgasse 4

Änderung des Bauführers

Wir teilen Ihnen mit, daß bei o.a. Bauvorhaben die

Fa. Ing. Franz und Hans Huber Bauges.m.b.H.
1100 Wien, Jagdgasse 27/6

mit der Bauführung betraut ist.

Magistratsabteilung 37	
Außenstelle f. d. 3., 4. u. 5. Bez.	
Eing.:	15. APR. 1988
MA 37/3- Kegelg. 4	
Zahl 1178/88	Blg. w.w.

Mit vorzüglicher Hochachtung

DOMUS-PLAN
M. B. H. & CO. KG

2339

an BbW Zl 2577/87

Bankverbindung: Erste österreichische Spar-Casse-Bank, Konto 032-36250
Gerichtsstand Wien.

X

An die
Magistratsabteilung 37/3

MODENAPARK 1-2

1030 Wien

Wien, 13.3.1989

Wir geben hiermit die Fertigstellung der zu Zahl MA 37/3 -
..KEGELASSE 4/2577/87... genehmigten baulichen Herstell-
lung auf der Liegenschaft Wien 3, ..KEGELASSE.....
..... ONr. 4, EZ,
Kat. Gem. bekannt.

Hochachtungsvoll

HUBER

baute und saniert
Ing. F. HUBER Bauges.m.b.H.
1100 Wien, Jagdgasse 27 62 44 53

Magistratsabteilung 37
AUBAU... Coz.
17. MÄZ. 1989
MA 37/ 3 Kegel 4
Zahl 2577/87 2339

Edm ✓

zugestellt am:

7.3.90

Ebn

Magistrat der Stadt Wien
Magistratsabteilung 37
Baupolizei
Außenstelle für den 3., 4. und 5. Bezirk
Am Modenapark 1 - 2, 1030 Wien

MA 37/3 - Kegelgasse 4/565/90

Wien, 16. Feber 1990

3. Bezirk, Kegelgasse ONr. 4
EZ 2339 der Kat. Gem. Landstraße

Nichterfüllte Verpflichtung -
Mahnung

Sehr geehrte Frau
Sehr geehrter Herr

Es wurde am 15. Feber 1990 erhoben, daß der nachstehenden, in dem Bescheid vom 12. Jänner 1988, Zl. MA 37/3 - Kegelgasse 4/2577/87, enthaltenen, rechtskräftigen Verpflichtung bisher noch nicht entsprochen wurde:

Mindestens einen Monat vor Beginn der Bauarbeiten ist gemäß § 127 Abs. 1, lit. b BO über die Festigkeit der Fundamente, der Tragkonstruktionen und der sonstigen besonders beanspruchten Bauteile eine statische Berechnung samt Konstruktionsplänen der MA 35 - S (Dresdner Straße 75, 1200 Wien) vorzulegen. Gleichzeitig mit der statischen Berechnung ist vom Bauwerber eine bewilligte Planparie oder ein vom Planverfasser gefertigtes Gleichstück zu übermitteln.

Sollte innerhalb von 8 Wochen nach Zustellung dieser Mahnung die Verpflichtung nicht erfüllt werden, müßten Zwangsmaßnahmen im Sinne des Verwaltungsvollstreckungsgesetzes 1950 beantragt werden.

Erght an:

1.) Gebäudeverwaltung Friedrich & Padelek OHG, Lange Gasse 50,
1080 Wien als Bauwerber

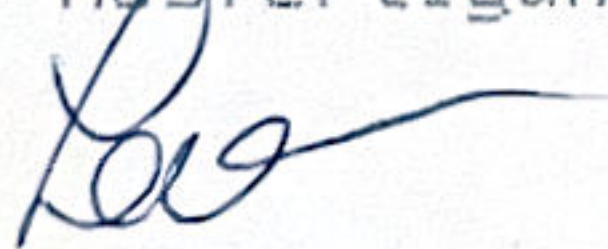
In Abschrift an:

2.) MA 37/3

3.) zum Akt

Für den Abteilungsleiter:
Dipl.-Ing. Hahn
Oberstadtbaurat

Für die Richtigkeit
der Ausfertigung:



Von

DOMUS-PLAN

Althausanierungs-Ges.m.b.H.
1080 WIEN, LANGE G. 50/12
Tel. 48 63 78

Ihre Zeichen/Nachricht vom

Kurzbrief

Unser Zeichen *HQJ/7A*

Datum *13.3.90*

Mit der Bitte um: ☐ Erledigung ☒ Kenntnisnahme ☐ Verbleib

☐ Stellungnahme bis/am

Anlage *1*

An die
Magistratsabteilung 37
Baupolizei f.d. 3. Bezirk

Am Modenapark 1-2
1030 Wien

Betr.: *3., Kegelgasse 4*

In der Anlage übermitteln wir
Ihnen eine Kopie unseres Schrei-
bens an die MA 35 vom 13.3.90,
betreffend Festigkeitsberechnung
und Beschreibung der Aufzugsan-
lage zu o.a. Objekt, mit der
Bitte um Kenntnisnahme.

Mit freundlichen Grüßen
D O M U S - P L A N
AlthausanierungsgesmbH.

AB 23.3.90 NEUE TEL.-NR.
408 59 28, 408 59 29, 408 63 78

Betrifft: 1030 Wien, Kegelgasse 4/565/90
Ihre Mahnung vom 16.2.1990

Sehr geehrte Damen und Herren,

in der Anlage übermitteln wir Ihnen aufgrund Ihrer o.a.
Mahnung die Festigkeitsberechnung für den Aufzug, die Be-
schreibung der Aufzugsanlage und eine bewilligte Planparie
zu o.a. Objekt.

Mit freundlichen Grüßen

D O M U S - P L A N

ALTHAUSSANIERUNGSGESMBH.

Anlagen:
erwähnt
Kopie an:
MA 37

Magistratsabteilung 37
Außenstelle f.d. 3., 4. u. 5. Bez.

Eing.: 14. MRZ. 1990

MA 37/3-*Kegelgasse 4*

Zahl *817/90* Blg. u. o.

15. März 1990

Sendung an Kegelgasse 4/2577/87 an Ebn

Ebn
2339

KfL-Bille auf
Kegelgasse 4
Unprotokollieren

DOMUS-PLAN

ALTHAUSSANIERUNGSGESELLSCHAFT
M. B. H.

1080 WIEN, LANGE GASSE 50/12

TEL. (0222) 48 59 28, 48 63 78

Telefax - Nr. 48 67 32 ,

An den
Magistrat der Stadt Wien
Magistratsabteilung 35

Dresdner Straße 75
1200 Wien

Wien, 1990.03.13.
Hro/Za

Betrifft: 1030 Wien, Kegelgasse 4/565/90
Ihre Mahnung vom 16.2.1990

Sehr geehrte Damen und Herren,

in der Anlage übermitteln wir Ihnen aufgrund Ihrer o.a.
Mahnung die Festigkeitsberechnung für den Aufzug, die Be-
schreibung der Aufzugsanlage und eine bewilligte Planparie
zu o.a. Objekt.

Mit freundlichen Grüßen

DOMUS - PLAN

ALTHAUSSANIERUNGSGESMBH.

Anlagen:
erwähnt
Kopie an:
MA 37

Magistratsabteilung 37	
Außenstelle f.d. 3., 4. u. 5. Bez.	
Eing.:	14. MRZ. 1990
MA 37/3	16. März 1990
Zahl	8.17.1990
	Blg. W.O.

15. März 1990

Sendung an Kegelgasse 4/2577/87 an Ebn

Ebn
2339

KfL = Bitte auf
Kegelgasse 4
unproblematik

Absender (mit Anschrift): Magistral der Stadt Wien Magistratsabteilung 35 20, Dresdner Straße 75 1200 Wien	Datum: 19.3.90	Telefon: 35-66-11/4070w	Eingangs- u. Zuteilungsvermerk:
	GZ., Betreff: CH/71/90 Festlegungs berechnung f. Aufzug 3. Kegelplane 4		
An MA 37/3			

☒ wie vereinbart ☐ zu Ihrer Information ☐ zu Ihrer Verwendung ☐ mit Dank zurück ☐ nach Entsprechung zurück ☒ zuständigkeitshalber weitergeleitet ☒ Abgabennachricht erteilt	mit der Bitte um ☐ Stellungnahme ☐ weitere Veranlassung ☐ Behandlung wie vereinbart ☐ Antwortentwurf ☐ Bericht ☐ Überprüfung ☐ Rückruf	☐ Kenntnisnahme ☐ Rücksendung an Absender ☐ Erledigung ☐ Zusendung einer Erled.-Kopie ☐ Genehmigung ☐ Entscheidung ☐ Weisung ☐ Weiterleitung an
---	--	--

Mitteilungen, Anweisungen usw. allgemeiner Art:

Beilagen: 4

Magistratsabteilung 37
 Außenstelle f. d. 3., 4. u. 5. Bez.
 Eing.: 21. MRZ. 1990
 MA 37/3 - Kegel. 4
 Zahl 1002/90 Blg. w.o. - Ebn 2339

Unterschrift

AD 1156A - 130.000 Garnituren à 2 Blatt - 885 - 118364 - 42

Mahnung die Festigkeitsberechnung für den Aufzug, die Beschreibung der Aufzugsanlage und eine bewilligte Planparie zu o.a. Objekt.

Mit freundlichen Grüßen

DOMUS - PLAN
ALTHAUSSANIERUNGSGESMBH.

Anlagen:
erwähnt
Kopie an:
MA 37

DOMUS-PLAN

ALTHAUSSANIERUNGSGESELLSCHAFT
M. B. H.

1080 WIEN, LANGE GASSE 50/12

TEL. (0222) 48 59 28, 48 63 78

Telefax-Nr. 48 67 32

An den
Magistrat der Stadt Wien
Magistratsabteilung 3537/3

Dresdner Straße 75
1200 Wien

Wien, 1990.03.13.
Hro/Za

Betrifft: 1030 Wien, Kegelgasse 4/565/90
Ihre Mahnung vom 16.2.1990

Sehr geehrte Damen und Herren,

in der Anlage übermitteln wir Ihnen aufgrund Ihrer o.a.
Mahnung die Festigkeitsberechnung für den Aufzug, die Be-
schreibung der Aufzugsanlage und eine bewilligte Planparie
zu o.a. Objekt.

Mit freundlichen Grüßen

DOMUS - PLAN

ALTHAUSSANIERUNGSGESMBH.

Anlagen:
erwähnt
Kopie an:
MA 37

Aufzugseigentümer: Fr. Gertrude MUSIL
1050-Wien Gießaufgasse 25

Art des Aufzuges: Personen – Vereinfachter – Nichtberufsaufzug – Klein – Lasten – Umlauf-Aufzug –
hauptsächlich – Personen – Beförderung, Antriebsart: Elektrisch –
Nennlast: 320 kg oder 4 Pers., Betriebsgeschw.: 0,8/0,2 m/s, Hubhöhe: 14,45 m
Aufzugserbauer: H. TABORSKY-Aufzüge, Baujahr: 1988, Fabriks-Nr.: 212

Fahrbahn: Führt vom HOF bis 3.St., 5 Haltestellen, 5 Ladestellen

Baustoff der Umwehrung: Mauerwerk — verglaster Stahlurm

Anschläge in der Schachtgrube: ~~Waldholz~~ - Gummi - Puffer -

Fahrschachttüren: Baustoff: Stahlblech —

Teleskopschiebetüre

Betätigung mit: ~~Schüssel~~ - ~~Handgriff~~ - ~~Selbstschreiber~~ - Kraftantrieb

Verriegelung mit: Riegelschalter — Fehlschließsicherung, Type: TV299

Triebwerksraum: Lage: – über dem Schacht, Baustoff: ~~Mauerwerk~~ – verglaster Stahlbau...

Triebwerk: Treibscheibe — , Schneckengetriebe —

~~XXXXXX~~ – Drehstrom 380 V, Antriebsmotor ca. 3,3 kW, Nenndrehzahl 1500 min⁻¹

Bremslüftung: Elektrisch 180 v Gleich -Strom -

Feineinstellung: Polumschaltung - ~~Feldregelung~~ - ~~Feldstärkenmil~~ -

Notendschaltung: Steuerstrom — **Verzögerungskontrollschalter**

Steuerung: ~~XXXXXX~~ – Wechselstrom 220 V, Innen und Außen: Druckknopf –

~~PUL - SEITE XXXXIXAUBEN-GEWÄHRUNG~~ - Sammelsteuerung: ~~XXX-~~ Ab

Sonstige Steuerung:

Abschaltung der Außensteuerung durch: Zeitschaltung – ~~Beweglichen-Fahrkorbfußboden~~

Tragmittel: Anzahl: 3, Art und Abmessung: Ø 10mm Sealeseile

Fahrkorb: Baustoff: Stahlblech — , Nutzbare Fahrkorbgrundfläche: 1 m²

Anzahl der Fahrkorböffnungen: 1, 1 Tür(en) kraftbetätigt – Lichtschranke(n), ~~Dachaustieg~~

~~Sperr~~ - Rollen - ~~Bremse~~-Fangvorrichtung, Type: RS 38, Geschwindigkeitsbegrenzer, Type: GB 068

Gegengewicht: Baustoff: ~~Beton~~ – Eisen , führt bis Erdboden – Widerlager

Sperr – Rollen – Brems-Fangvorrichtung, Type: _____, Geschwindigkeitsbegrenzer, Type: _____

Beleuchtung: Im Fahrkorb: Dauerlicht – **Schachtlicht**, Im Fahrschacht

Notrufvorrichtung: Klingel –

Fahrkorbstellungsanzeige: Bei den Ladestellen durch **Schauöffnung** – Anwesenheitsanzeiger – ~~offene Tür~~ –

Ausführung nach ÖNORM B 2450 Teil, Ausgabe NOV 66, Teil, Ausgabe

ÖNORM B 2455 Ausgabe _____

Nichtzutreffendes streichen

Bemerkungen:

Magistrat der Stadt Wien
Magistratsabteilung 35
Allgemeine Baupolizeiangelegenheiten
Hierauf bezieht sich der Bescheid

MA 35-*A*/ 3 - 1 2 6 / 8 8

Wien, _____

Für den Abteilungsleiter:

Für die Richtigkeit der
Ausfertigung
Der Kanzleileiter:

V. Murnig



	Unterschrift	Anschrift
Der Bauwerber	<i>[Signature]</i>	PAUL FADDELER geschäftl. Gesellschafter der FRIEDRICH & FADDELER OHG 1060 WIEN, LANGE GASSE 50
Der Haus- / Grund- Eigentümer	<i>[Signature]</i>	
Der Planverfasser	<i>[Signature]</i>	H. TABORSKY-AUFZÜGE 1100 WIEN, LEEBGASSE 80 TEL. 78 74 44
Der befugte Aufzugserbauer	<i>[Signature]</i>	H. TABORSKY-AUFZÜGE 1100 WIEN, LEEBGASSE 80 TEL. 78 74 44
Der Bauführer für die Baumeisterarbeiten	<i>[Signature]</i>	HUBER best und seniert Ing. F. u. H. HUBER Bauges.m.b.H. 1100 Wien, Jagdgasse 27 62 44 53

Festigkeitsberechnung für den Aufzug

Aufstellungsort: 1030 - Wien Kegelgasse 4

Aufzugselgentümer: Fr. Gertrude MUSIL
1050-Wien Gießaufgasse 25

Art des Aufzuges: Personen - ~~XXXXXX~~ - ~~XXXXXX~~ - ~~XXXX~~ - ~~XXXX~~ - ~~XXXX~~ - Aufzug -

hauptsächlich - ~~XXXXXX~~ - Personen - ~~XXXX~~ - ~~XXXX~~ Beförderung, Antriebsart: Elektrisch -

Nennlast: 320 kg oder 4 Pers., Betriebsgeschw.: 0,8/0,2 m/s, Hubhöhe: 14,45 m

Aufzugserbauer: H. TABORSKY-Aufzüge, Baujahr: 1988, Fabriks-Nr.: 212

Belastungsannahmen (Näherungsweise kann mit 1 kp = 10 N gerechnet werden)

Nennlast in Newton	$Q = 3200$ N	Fahrkorbgewicht	$E = 4300$ N
Gedrängelast	$Q_G = \text{---}$ N	Gegengewicht	$G = 5900$ N

Tragmittel

Selle

Anzahl der tragenden Seilstränge $z = 3$
Seildurchmesser $d = 10$ mm
Bruchlast eines Selles $B = 80800$ N
Seilgeschwindigkeit $v_c = 0,8$ m/s

Seilbiegung

Treibscheibendurchmesser } $D = 520$ mm
Trommeldurchmesser }

Kleinsten Rollendurchmesser $D_1 = 400$

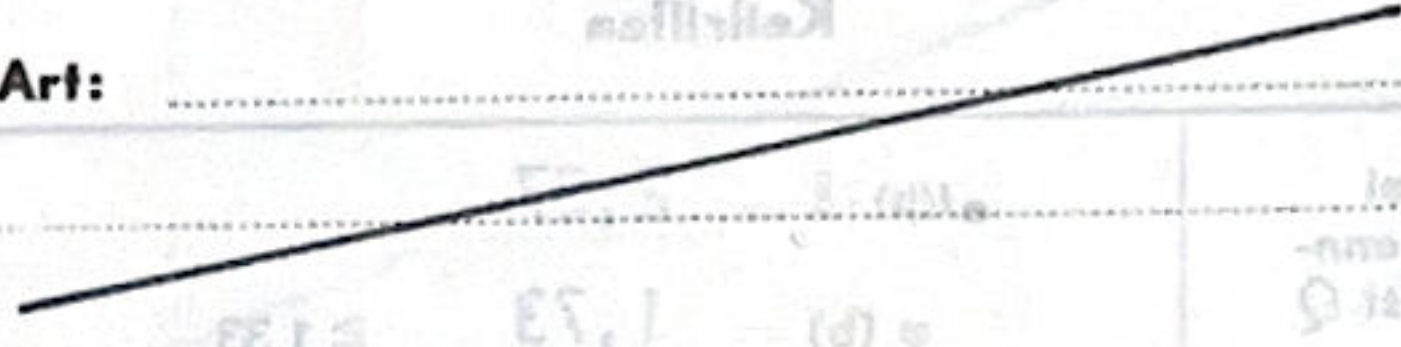
$\frac{D}{d} \geq 30 - 35 - 40$

$\frac{D}{d} = 52$

$\frac{D_1}{d} \geq 33 - 40$

$\frac{D_1}{d} = 40$

Ketten

Art: 

Anzahl der tragenden Kettenstränge $z =$

Bruchlast einer Kette $B =$ N

Zugbeanspruchung der Tragmittel

Sicherheitsfaktor $s = 14$

Belastung aller Tragmittel $Q + E = 7500$ N

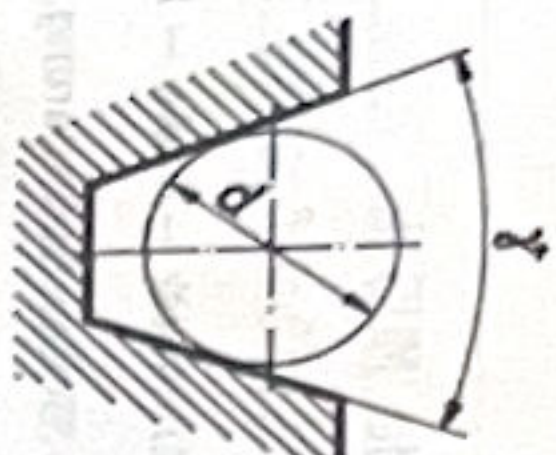
Zulässige Belastung aller Tragmittel $\frac{z \cdot B}{s} = 17314$ N

Gewicht der Selle (Hubhöhe $\times$ Metergewicht $\times z$) $S = 191$ N

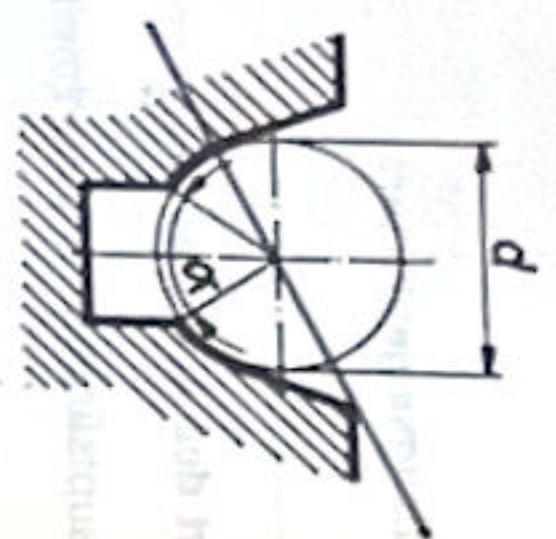
Gewicht der Unterselle (Hubhöhe $\times$ Metergewicht $\times$ Anzahl der Unterselle) $S_u =$ N

TreibscheibeUmschlingungswinkel $\beta = 165^\circ$ Kettwinkel $\gamma = 35^\circ$ Zentriwinkel $\alpha = 0^\circ$ **Treibscheibenformen**

Kettzelle



Sitzrille mit Unterschnitt

Größtes Seilspannungsverhältnis $\frac{\sigma_2}{\sigma_1}$

	ohne Unterselle	mit Untersellen
Triebwerk oben	$\frac{G+S}{E} = 1,37$	$\frac{G+S}{E+S_u} = \frac{G}{E+S_u-S}$
Triebwerk unten	$\frac{E+Q_G}{G-S} = \frac{E+Q_G}{G+S_u-S}$	$\frac{E+Q_G}{G+S_u-S} = \frac{E+Q_G}{G+S_u-S}$

Treibfähigkeit

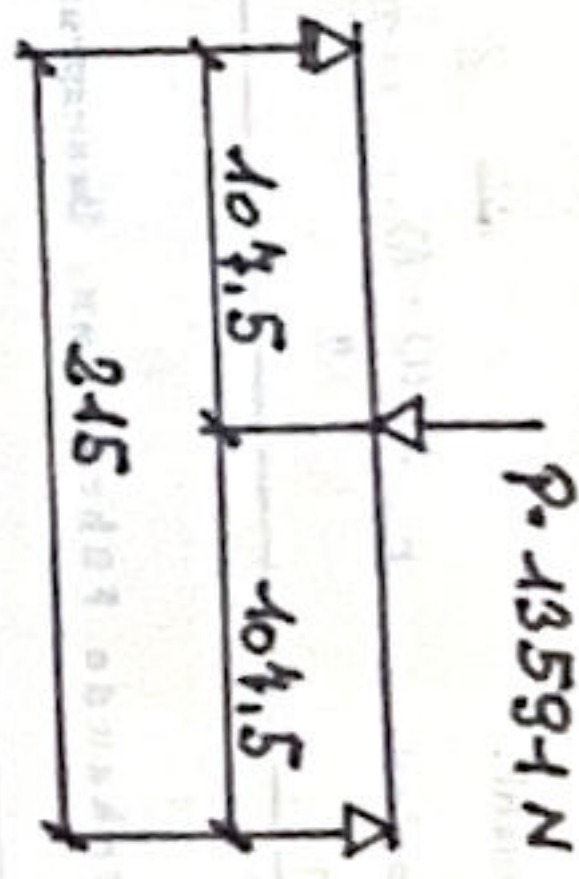
	Kettzelle	Sitzrille mit Unterschnitt
Bei Nennlast Q	$e(f_{(p)} \cdot \beta) = 2,37$ $\varphi(b) = 1,73 \geq 1,33$	$e(f_{(p)} \cdot \beta) =$ $\varphi(b) = \geq 1,15$
Bei Gedrängelast Q_G	$e(f_{(p)} \cdot \beta) =$ $\varphi(b) = \geq 1,15$	$e(f_{(p)} \cdot \beta) =$ $\varphi(b) = \geq 1,07$
	$f(p) = \frac{\mu}{\sin \gamma/2}$	$f(p) = 4 \mu \frac{1 - \sin \alpha/2}{\pi - \alpha - \sin \alpha}$
	$\varphi(b) = \frac{e(f_{(p)} \cdot \beta)}{\sigma_2/\sigma_1}$	$\mu = 0,09$ für den Zustand der Bewegung, $\mu = 0,11$ für den Zustand der Ruhe

Spezifische Pressung

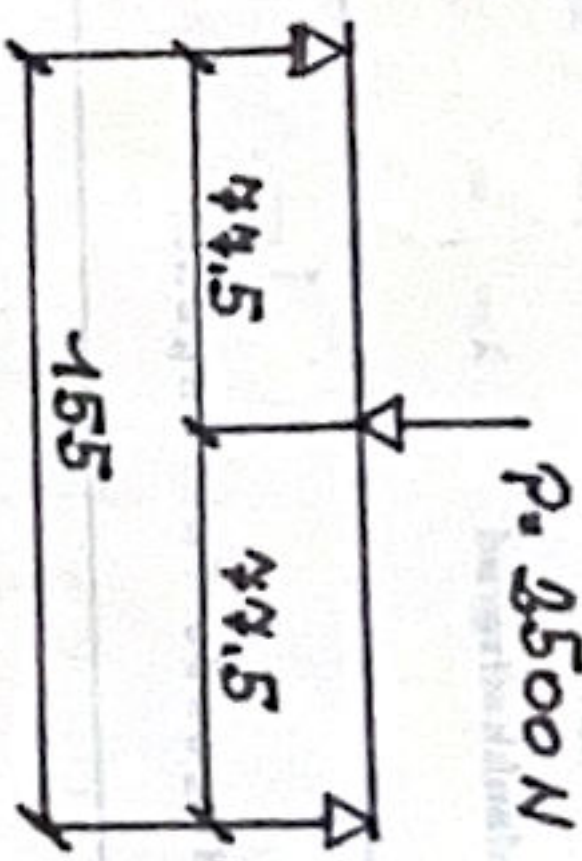
Kettzelle	Sitzrille mit Unterschnitt
$K = \frac{E+Q+S}{z \cdot d \cdot D} \cdot \frac{4,5}{\sin \gamma/2} = 7,37 \text{ N/mm}^2 \leq p$	$K = \frac{E+Q+S}{z \cdot d \cdot D} \cdot \frac{8 \cdot \cos \alpha/2}{\pi - \alpha - \sin \alpha} = \text{---} \text{ N/mm}^2 \leq p$
$S = S$ bei obenstehendem Triebwerk $S = 0$ bei untenstehendem Triebwerk	Max. zulässige Pressung $p = \frac{12,5 + 4 v_e}{1 + v_e} = 8,72 \text{ N/mm}^2$

Triebwerkschelle

Durchmesser	$d = 65 \text{ mm}$
Widerstandsmoment	$W = 26961 \text{ mm}^3$
Größtes Biegemoment	$M = 730516 \text{ N \cdot mm}$
Beanspruchung	$\frac{M}{W} = 27,1 \text{ N/mm}^2$
Zugfestigkeit	$\sigma_z = 600 \text{ N/mm}^2$
Zugfestigkeit Beanspruchung	$\frac{\sigma_z}{M/W} = 22,1 \geq 8$

Darstellung des Belastungsfalles**Rollenachse (höchstbeansprucht)**

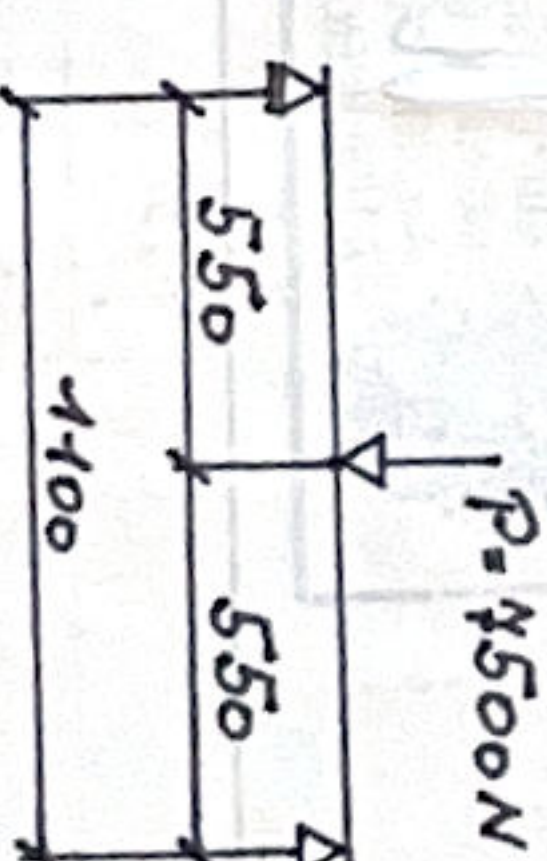
Durchmesser	$d = 50 \text{ mm}$
Widerstandsmoment	$W = 12272 \text{ mm}^3$
Größtes Biegemoment	$M = 96875 \text{ N \cdot mm}$
Beanspruchung	$\frac{M}{W} = 7,89 \text{ N/mm}^2$
Zugfestigkeit	$\sigma_z = 600 \text{ N/mm}^2$
Zugfestigkeit Beanspruchung	$\frac{\sigma_z}{M/W} = 76 \geq 8$

**Träger für****(höchstbeansprucht)**

Profil:	$W =$	mm^3
Widerstandsmoment	$M =$	$\text{N \cdot mm}$
Größtes Biegemoment	$\frac{M}{W} =$	N/mm^2
Beanspruchung	$\sigma_z =$	N/mm^2
Zugfestigkeit	$\frac{\sigma_z}{M/W} =$	≥ 5

Fahrkorridor (Biegeträger)

Profil:	$2 \times \text{UNP } 80$
Widerstandsmoment	$W = 53000 \text{ mm}^3$
Größtes Biegemoment	$M = 2062500 \text{ N \cdot mm}$
Beanspruchung	$\frac{M}{W} = 38,92 \text{ N/mm}^2$
Zugfestigkeit	$\sigma_z = 370 \text{ N/mm}^2$
Zugfestigkeit Beanspruchung	$\frac{\sigma_z}{M/W} = 9,51 \geq 5$



Fahrkorbführungsschienen

Profil:	70/70/9		
Anzahl	$n = 2$		$K_0 = 3$ bei Rollenfangvorrichtung
Fanglast	$F = \frac{K_0 (Q + E)}{n} = 11250$	N	

a) stehende Führungen: Beanspruchung auf Knickung

Querschnitt einer Führung	$A = 1150$	mm ²	Nach ÖNORM B 4600 Teil 4 Stabilitätsnachweis:
Trägheitsmoment	$J = 239000$	mm ⁴	Zulässige Druckspannungen bei Knickgefahr
Trägheitsradius	$i = \sqrt{\frac{J}{A}} = 14,42$	mm	für den Regelfall $zul \sigma_K = 29$ N/mm ²
Stützlänge	$l = 2500$	mm	Zulässige Fanglast
Schlankheitsgrad	$\lambda = \frac{l}{i} = 173,4$		$zul F = zul \sigma_K \cdot A = 33350$ N $\geq F$

b) hängende Führungen:

Führungslasche: Beanspruchung auf Zug		Laschenschrauben: Beanspruchung auf Abscherung	
Profil:		Abmessung:	
Querschnitt	$A =$ mm ²	Anzahl	$n =$
Zugfestigkeit	$\sigma_z =$ N/mm ²	Querschnitt	$A =$ mm ²
Zulässige Fanglast	$zul F = \frac{\sigma_z \cdot A}{5} =$ N $\geq F$	Scherfestigkeit	$\tau =$ N/mm ²
		Zulässige Fanglast	$zul F = \frac{\tau \cdot n \cdot A}{5} =$ N $\geq F$

Bemerkungen:

AUF VERTRAGSMÄSSIGKEIT
FACHTECHNISCH
RECHNERISCH

} GEPRÜFT

G. ZL.: T 782/88
WIEN, 29.4.1988

DIPL. ING. DR. TECHN. ERNST ZEIBIG
INGENIEUR FÜR MASCHINENBAU
AUFZUGS- UND EISENBAU (AUFZUGSPRÜFER)
A-1190 WIEN, KREINDLG. 4 - 0222/36 15 81

Magistrat der Stadt Wien
Magistratsabteilung 35
Allgemeine Baupolizeiangelegenheiten
Hierauf bezieht sich der Bescheid
MA 35- A / 3 - 126 / 88
1988 -06- 17

Wien, _____
Für den Abteilungsleiter:
Dipl. Ing. Molin e. h.
Oberstadtbaurat

Für die Richtigkeit
der Ausfertigung
Der Kanzleileiter:
i.v. Münggenberg

Der befugte Aufzugserbauer	Unterschrift <i>[Signature]</i>	Anschrift H. LABORSKY-AUFZÜGE 1100 WIEN, LEEBGASSE 80 TEL 78 74 44
-------------------------------	------------------------------------	---



EINREICHPLAN

M 1:100

ÜBER BAULICHE ÄNDERUNGEN IM HAUSE 1030 WIEN,
KEGELGASSE 4 FÜR FRAU GERTRUDE MUSIL IN
1050 WIEN, GIESZAUGASSE 25/8

EZ 2339 KG: LANDSTRASSE

Für den

BAUWERBER UND GRUNDEIGENTÜMER

BAUFÜHRER

HANS POKORNY
Baugesellschaft m.b.H. & Co. KG.
Döblinger Hauptstraße 33a
1190 Wien Tel. 36 23 87

PLANVERFASSER

DOMUS - PLAN
Ges.m.b.H. & Co. KG
1080 WIEN, LANGE 50/12
Tel. 48 63 78

BAUBEHÖRDE

Magistrat der Stadt Wien
Magistratsabteilung 37

Baupolizei

Hierauf bezieht sich der Bescheid
MA 37/3-Kegelgasse 4/2577/87

Wien, **12. März 1988**

Für den Abteilungsleiter:



Dipl.-Ing. Hahn
Oberstadtbaurat

WIEN, AM 3.AUGUST 1987



- 8 ~~Montageträger (haken) OK 50 mm v. Treibwerksraumdecke Tragkraft kN.~~
- 9 ~~Montageöffnung mit abschraubbarer FHT-Riffelblechabdeckung~~
- 10 Betonsockel laut Monteurangaben
- 11 ~~Einschubtreppe Einbaumaß mit Lieferfirma festlegen~~
- 12 ~~Nicht wegnehmbarer Eisenleiter~~
- 13 ~~Gittertrennwand (wegnehmbar) 10mm Mw, 1,5mm Drahtstärke~~
- 14 ~~Schallisolierung~~
- 15 ~~Ölfester Anstrich für Grube, Treibwerksraum, Installationkanäle 150mm hoch~~
- 16 ~~Beputetes, bitumiertes Stahlrohr öl bzw. wasserdicht.~~
- P Betriebs- und Fanglasten incl. 30% Stoßzuschlag ohne Eigengewicht von Betonsockeln, Decken, Hauptträgern usw.

B1

P1 9,75 kN

P2 8,8 kN

P3 8,8 kN

P4 7,67 kN

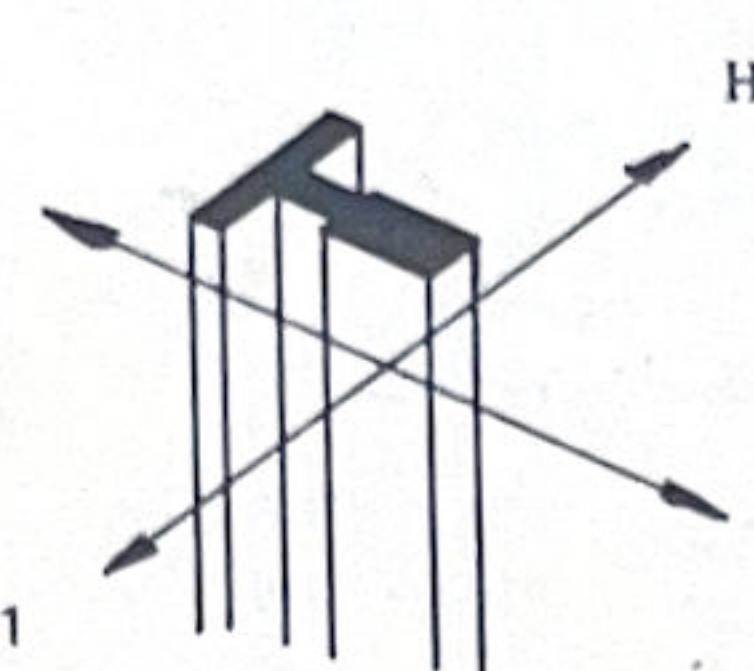
P5 — kN

P6 — kN

P7 — kN

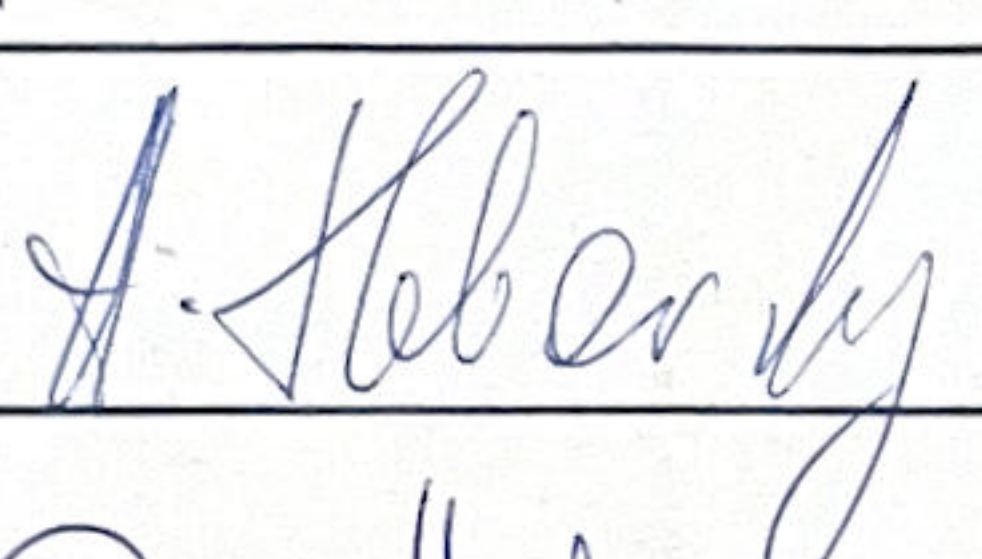
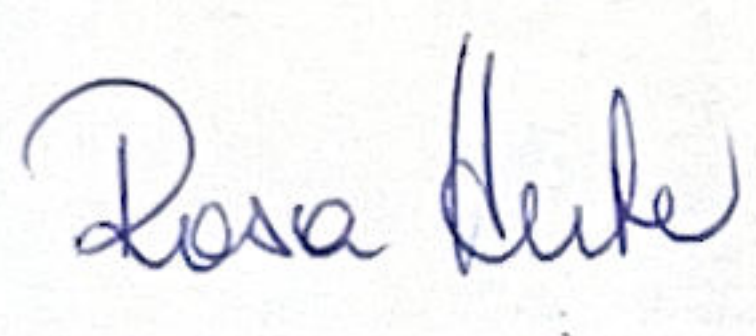
P8 — kN

Horizontalkräfte bei jeder Stützenreihe wirkend



H1 — kN

H2 — kN

	UNTERSCHRIFT	ANSCHRIFT
DER BAUWERBER		
DER HAUSEIGENTÜMER		PAUL PADELEK geschäftsl. Gesellschafter der FRIEDRICH & PADELEK OHG 1060 WIEN, LANGE GASSE 50
DER PLANVERFASSER UND AUFZUGERBAUER		H. TABORSKY-AUFZÜGE 1100 WIEN, LEEBGASSE 8 TEL. 78 74 44
DER BAUFÜHRER FÜR DIE BAUMEISTERARBEITEN		HUBER baut und saniert Ing. F. u. H. HUBER Bauges.m.b.H. 1100 Wien, Jagdgasse 27 62 44 53
DER GRUNDEIGENTÜMER		

Art des Aufzuges: PERSONENAUFZUG		H. TABORSKY-AUFZÜGE 1100-WIEN LEEBGASSE 80		
Auftraggeber: Fr. Gertrude MUSIL 1050-WIEN, GIBAUFGASSE 25				
Aufstellungsort: 1030-Wien, Kegelgasse 4		Zeichnungsnr: 212		
M 1.20 1.50 1.100	Tragkraft: 320 kp oder 4 Personen		TAG	Name
	Hubhöhe: 14,45 Halt: 5 Ladest: 5		10.03.88	
	V= 0,8/0,2 Motorleistung			
	DK-Rufsystem elektronik			
		Fabr. Nr: 212		