




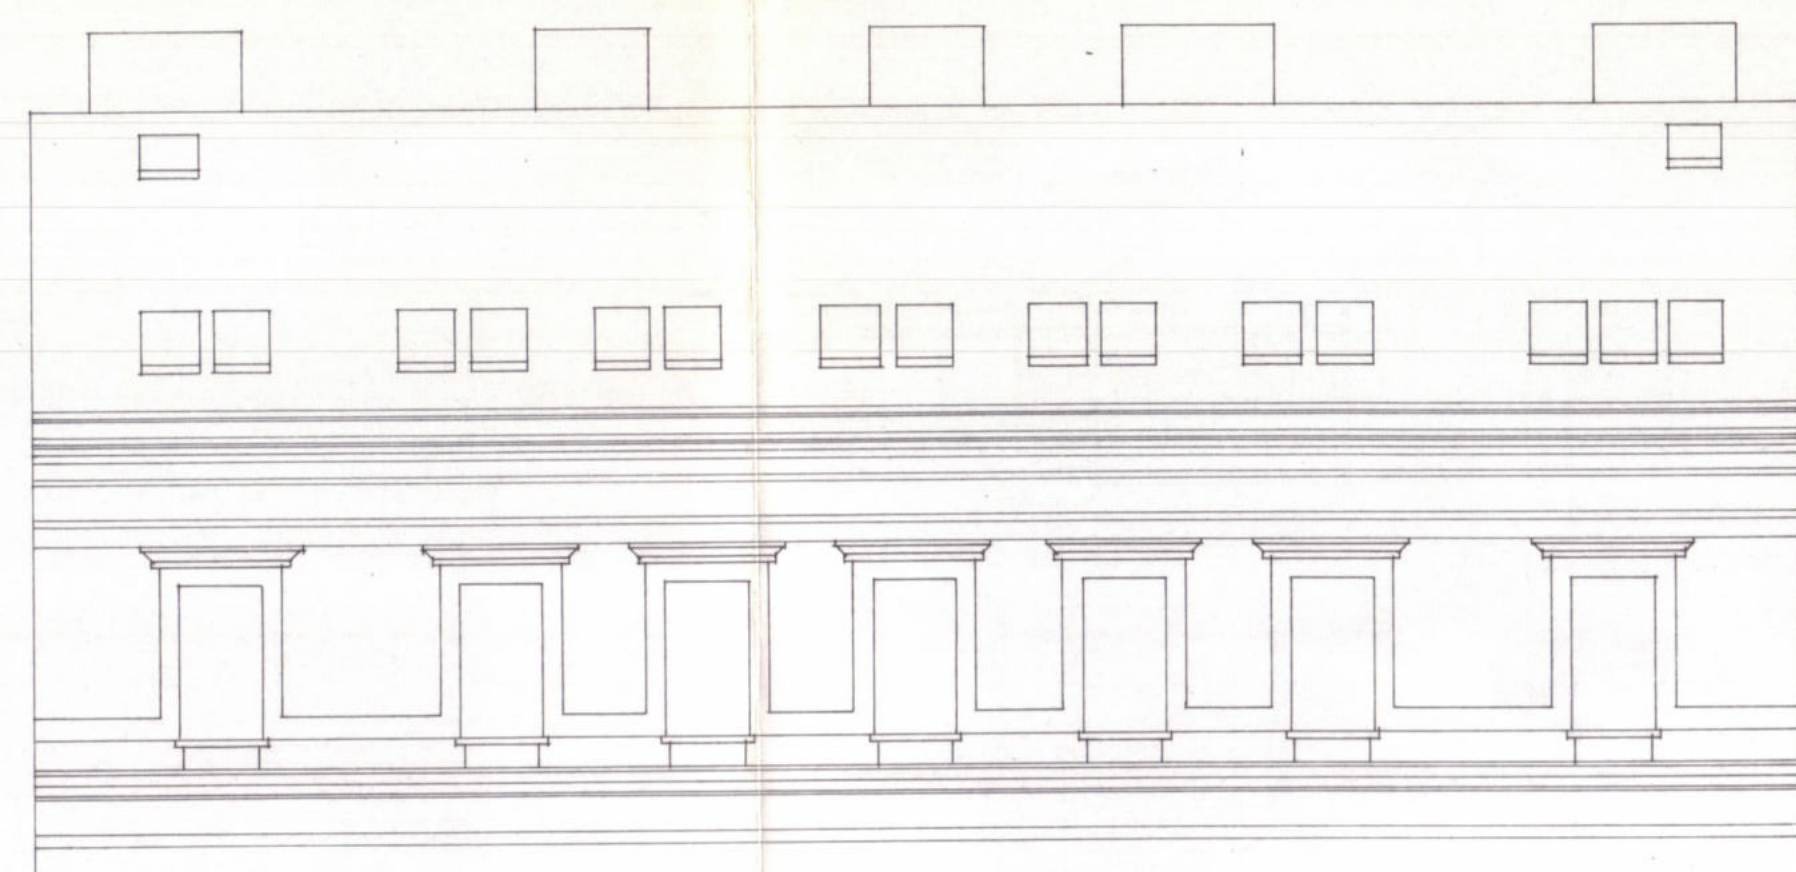


STRASSENANSICHT

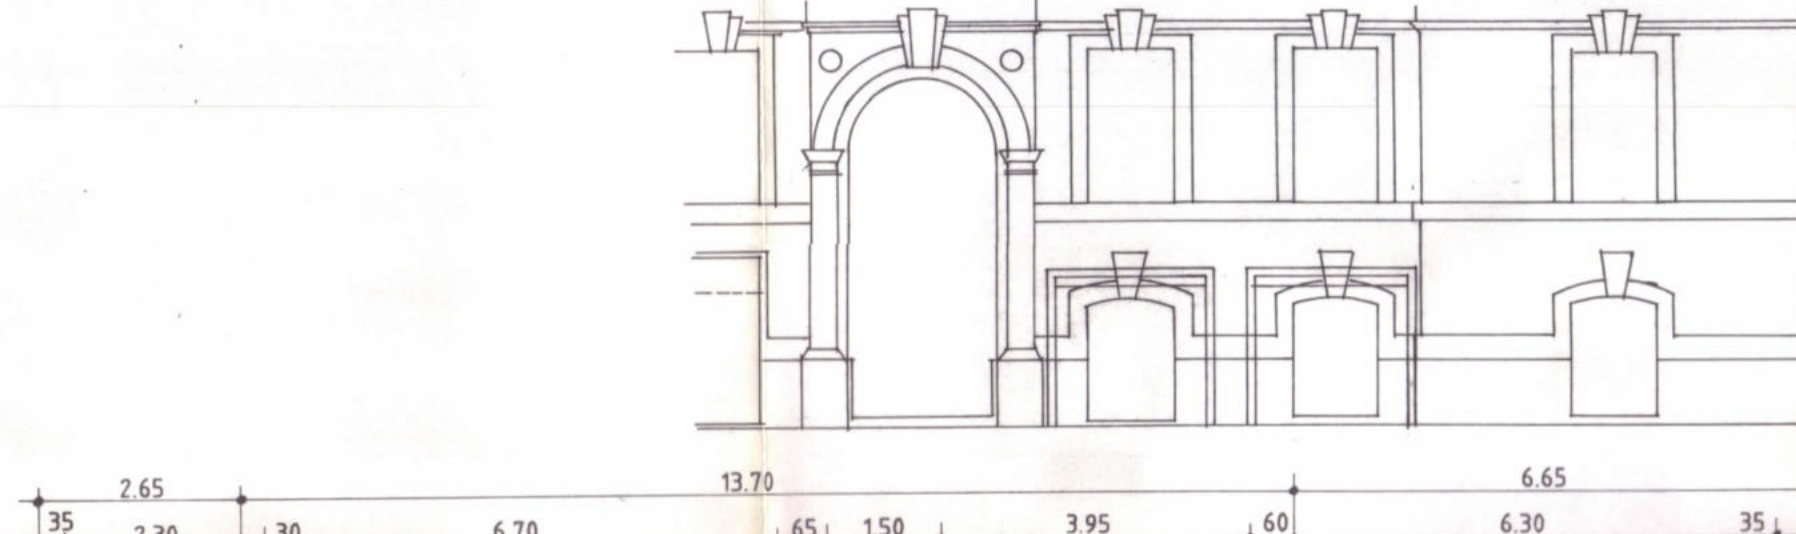


HOFANSICHT

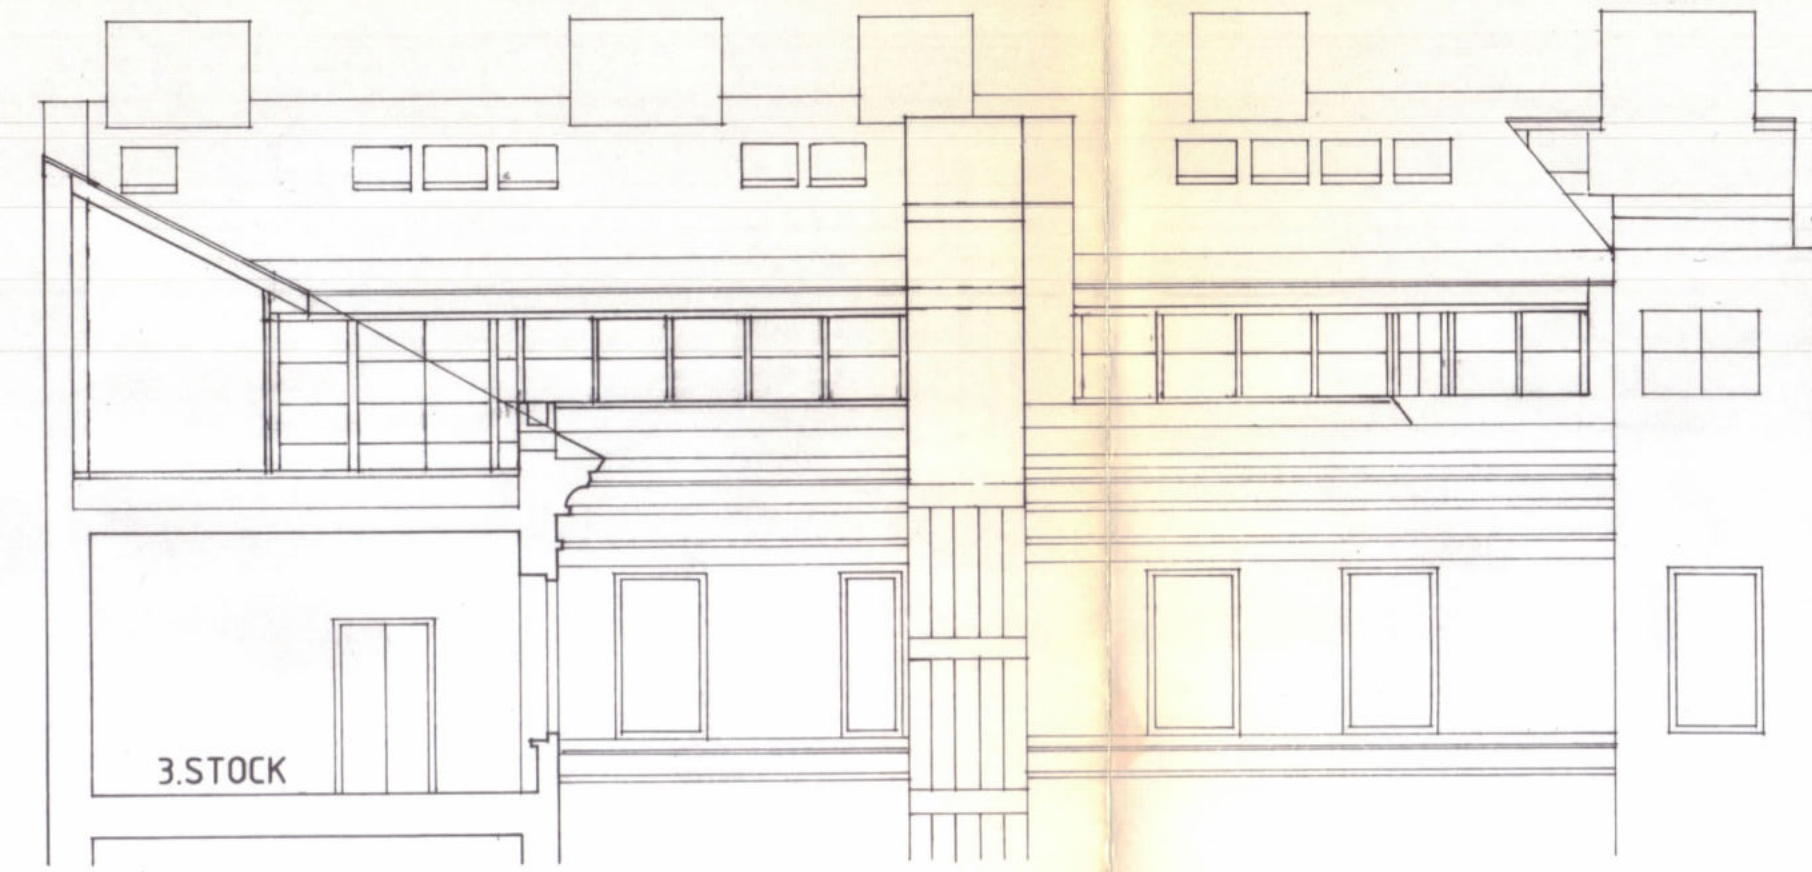


SNITT A-A

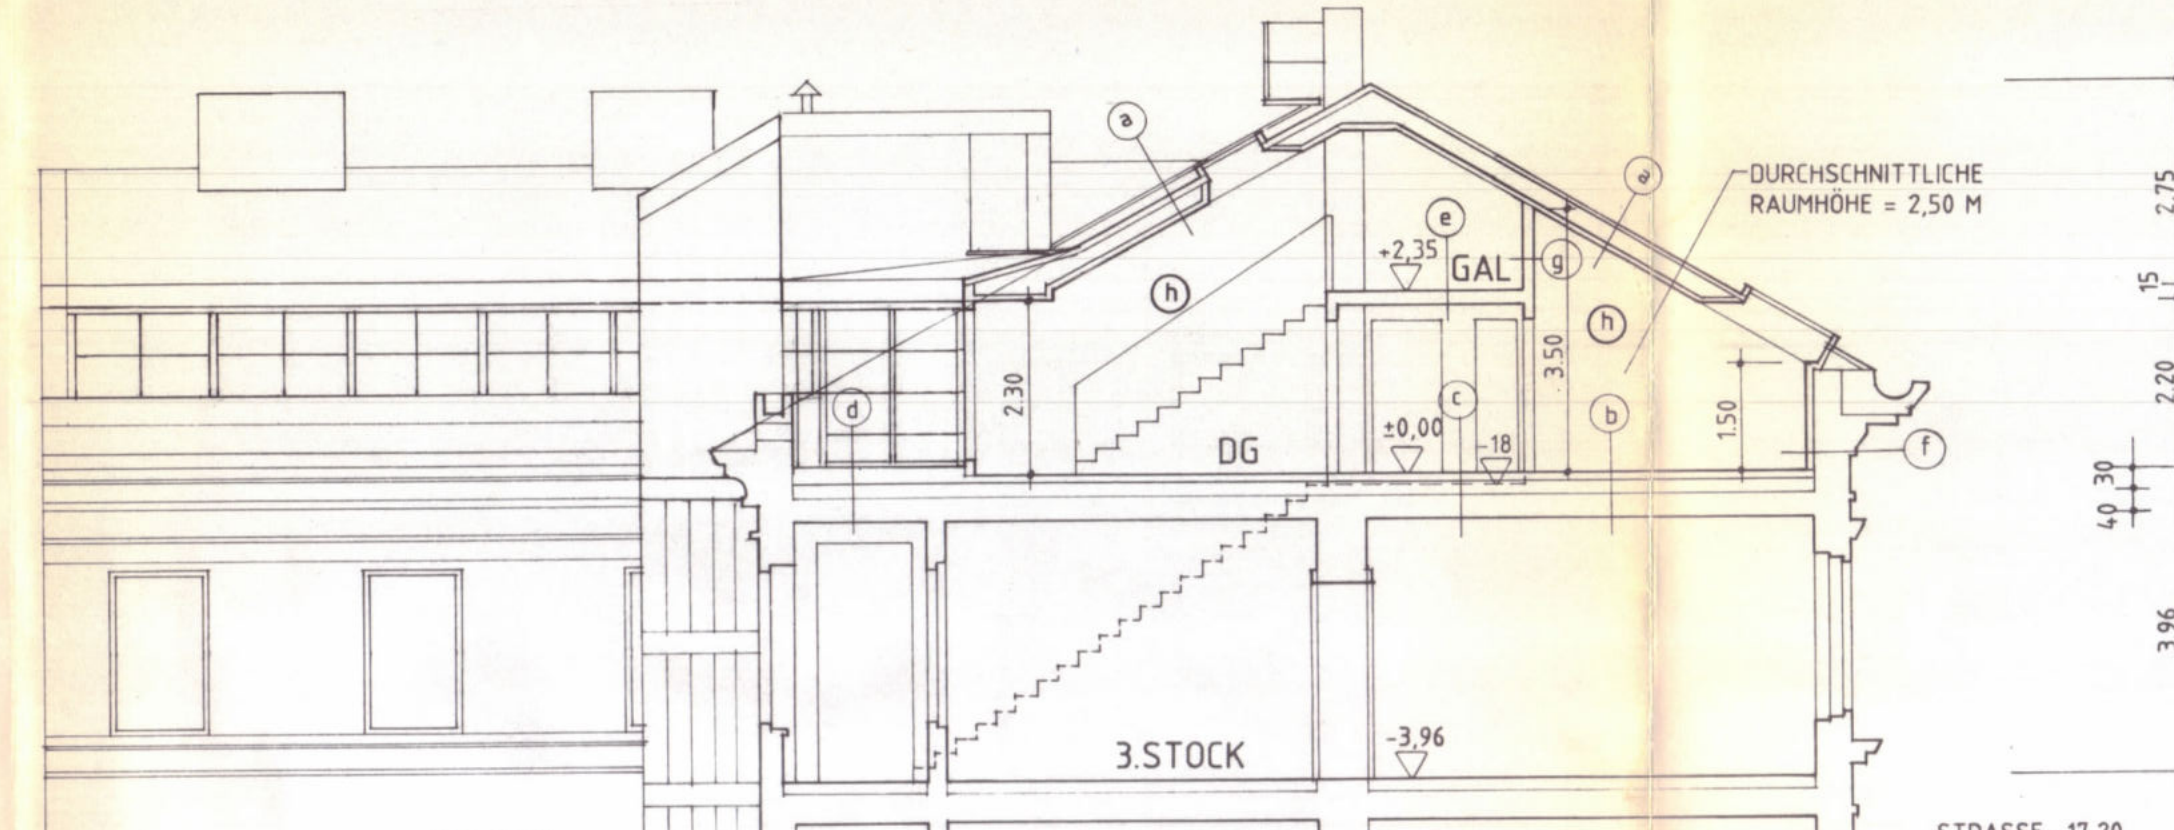


SNITT B-B

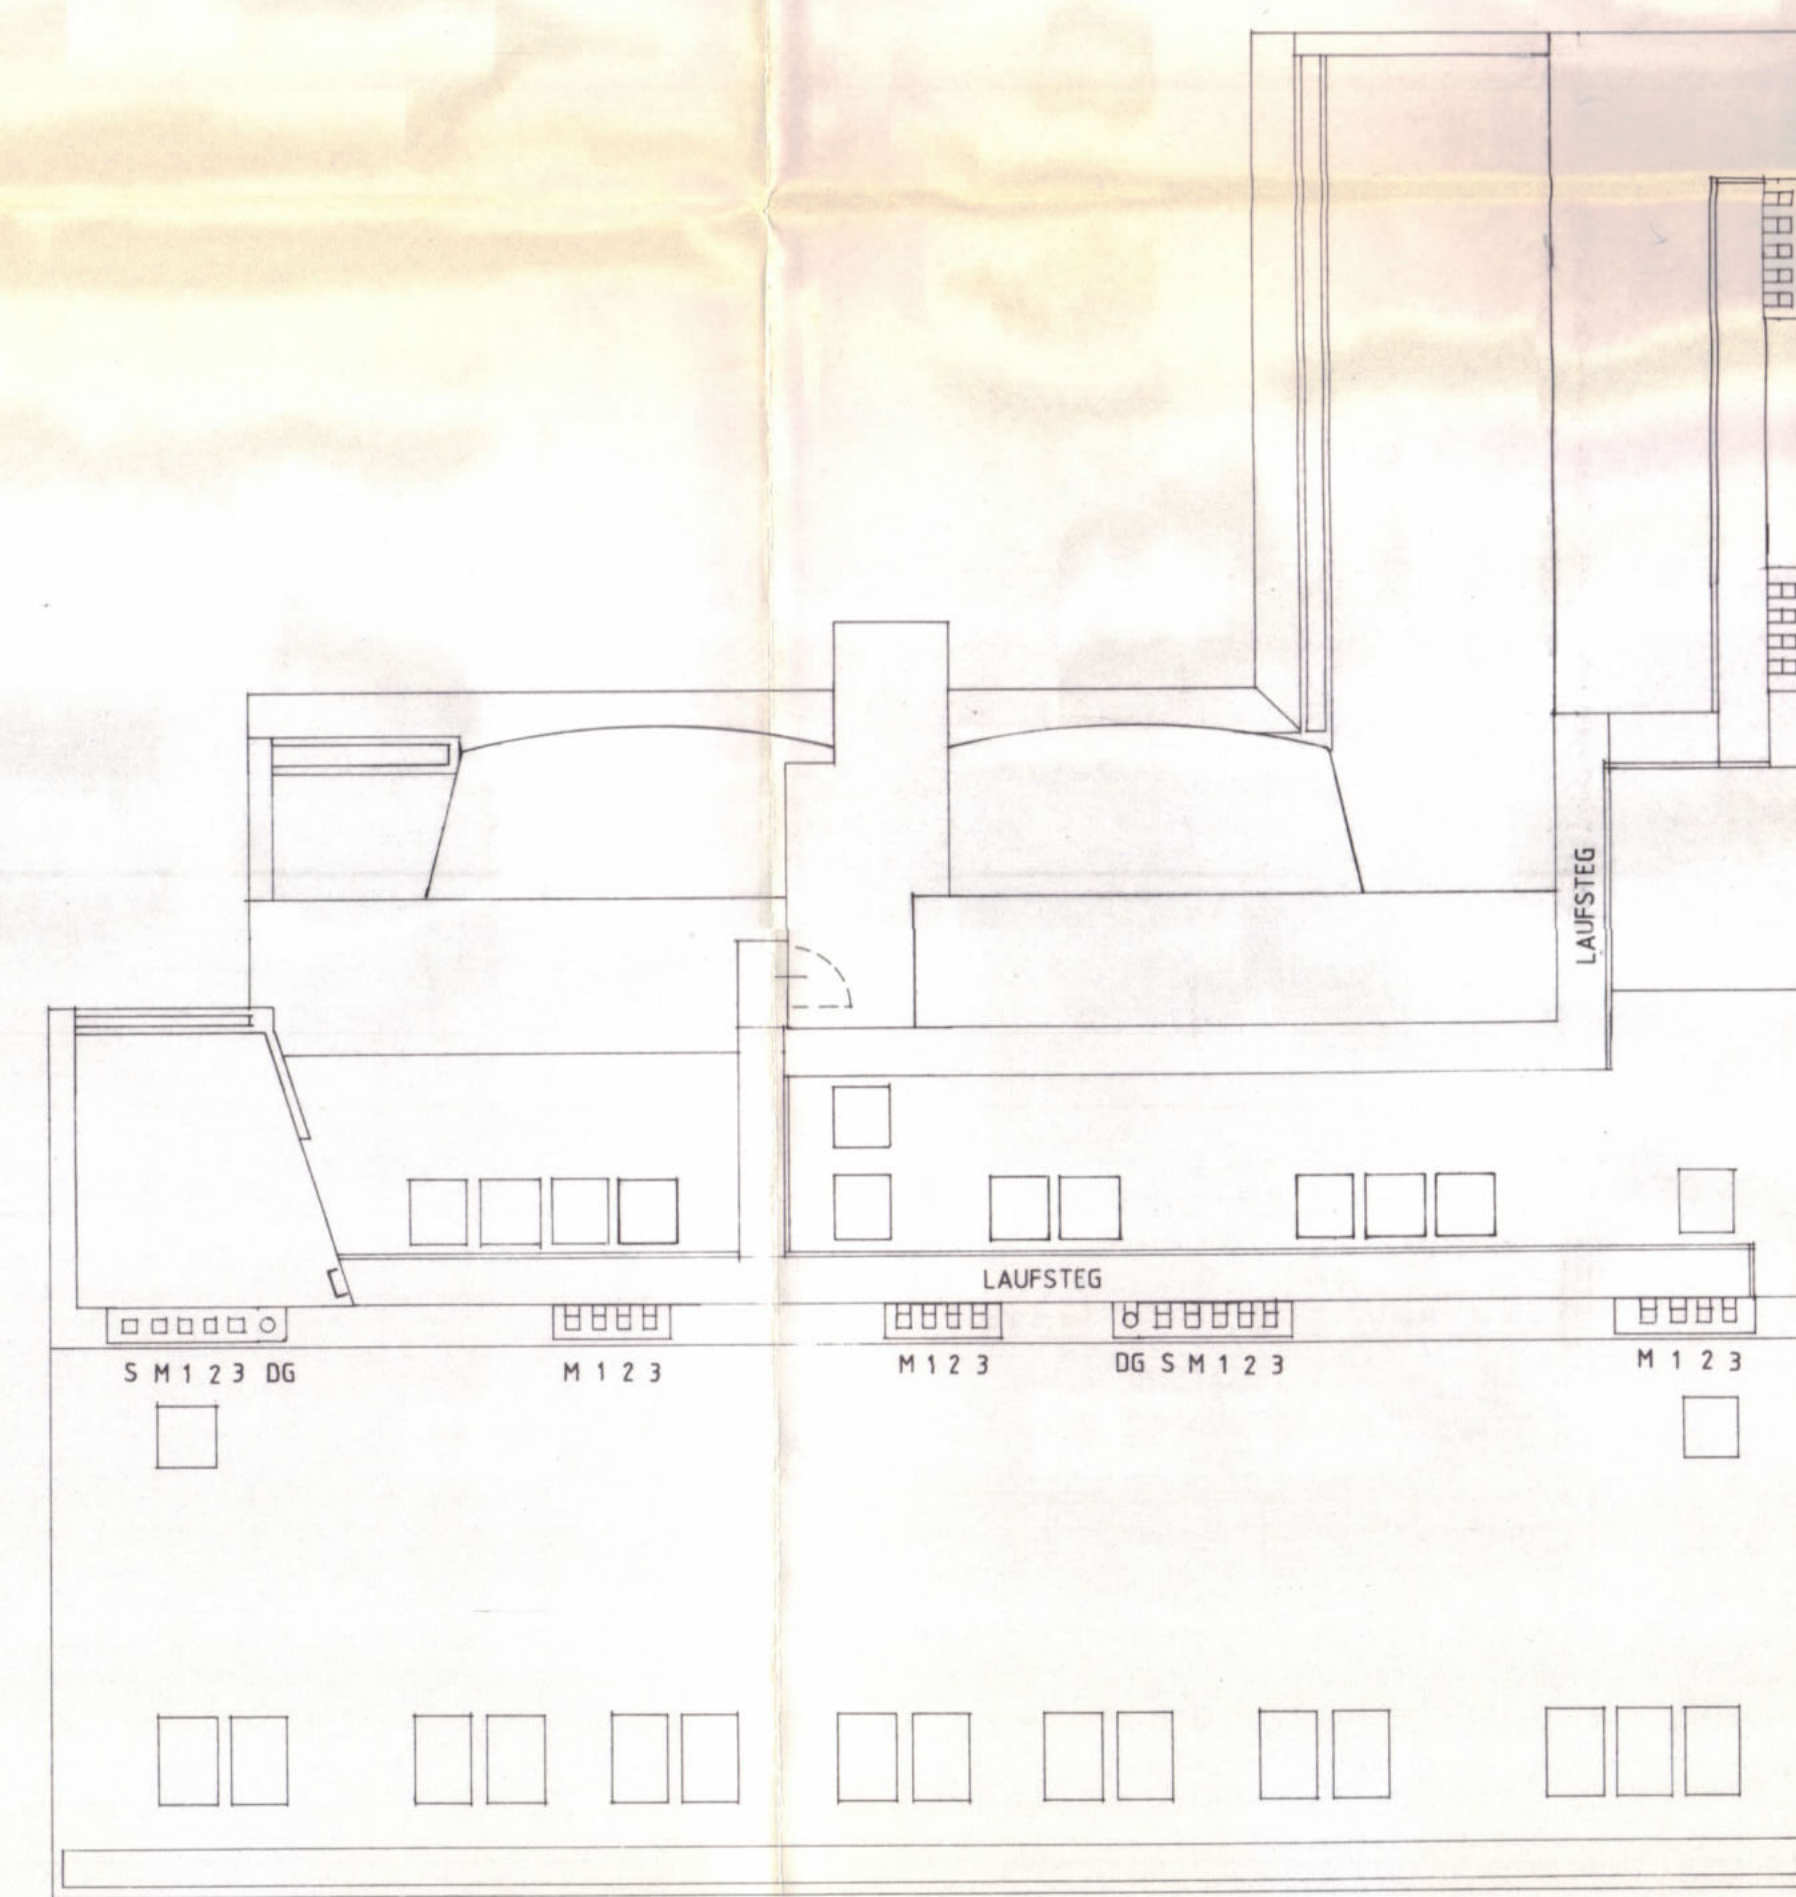


DACHDRAUFSICHT

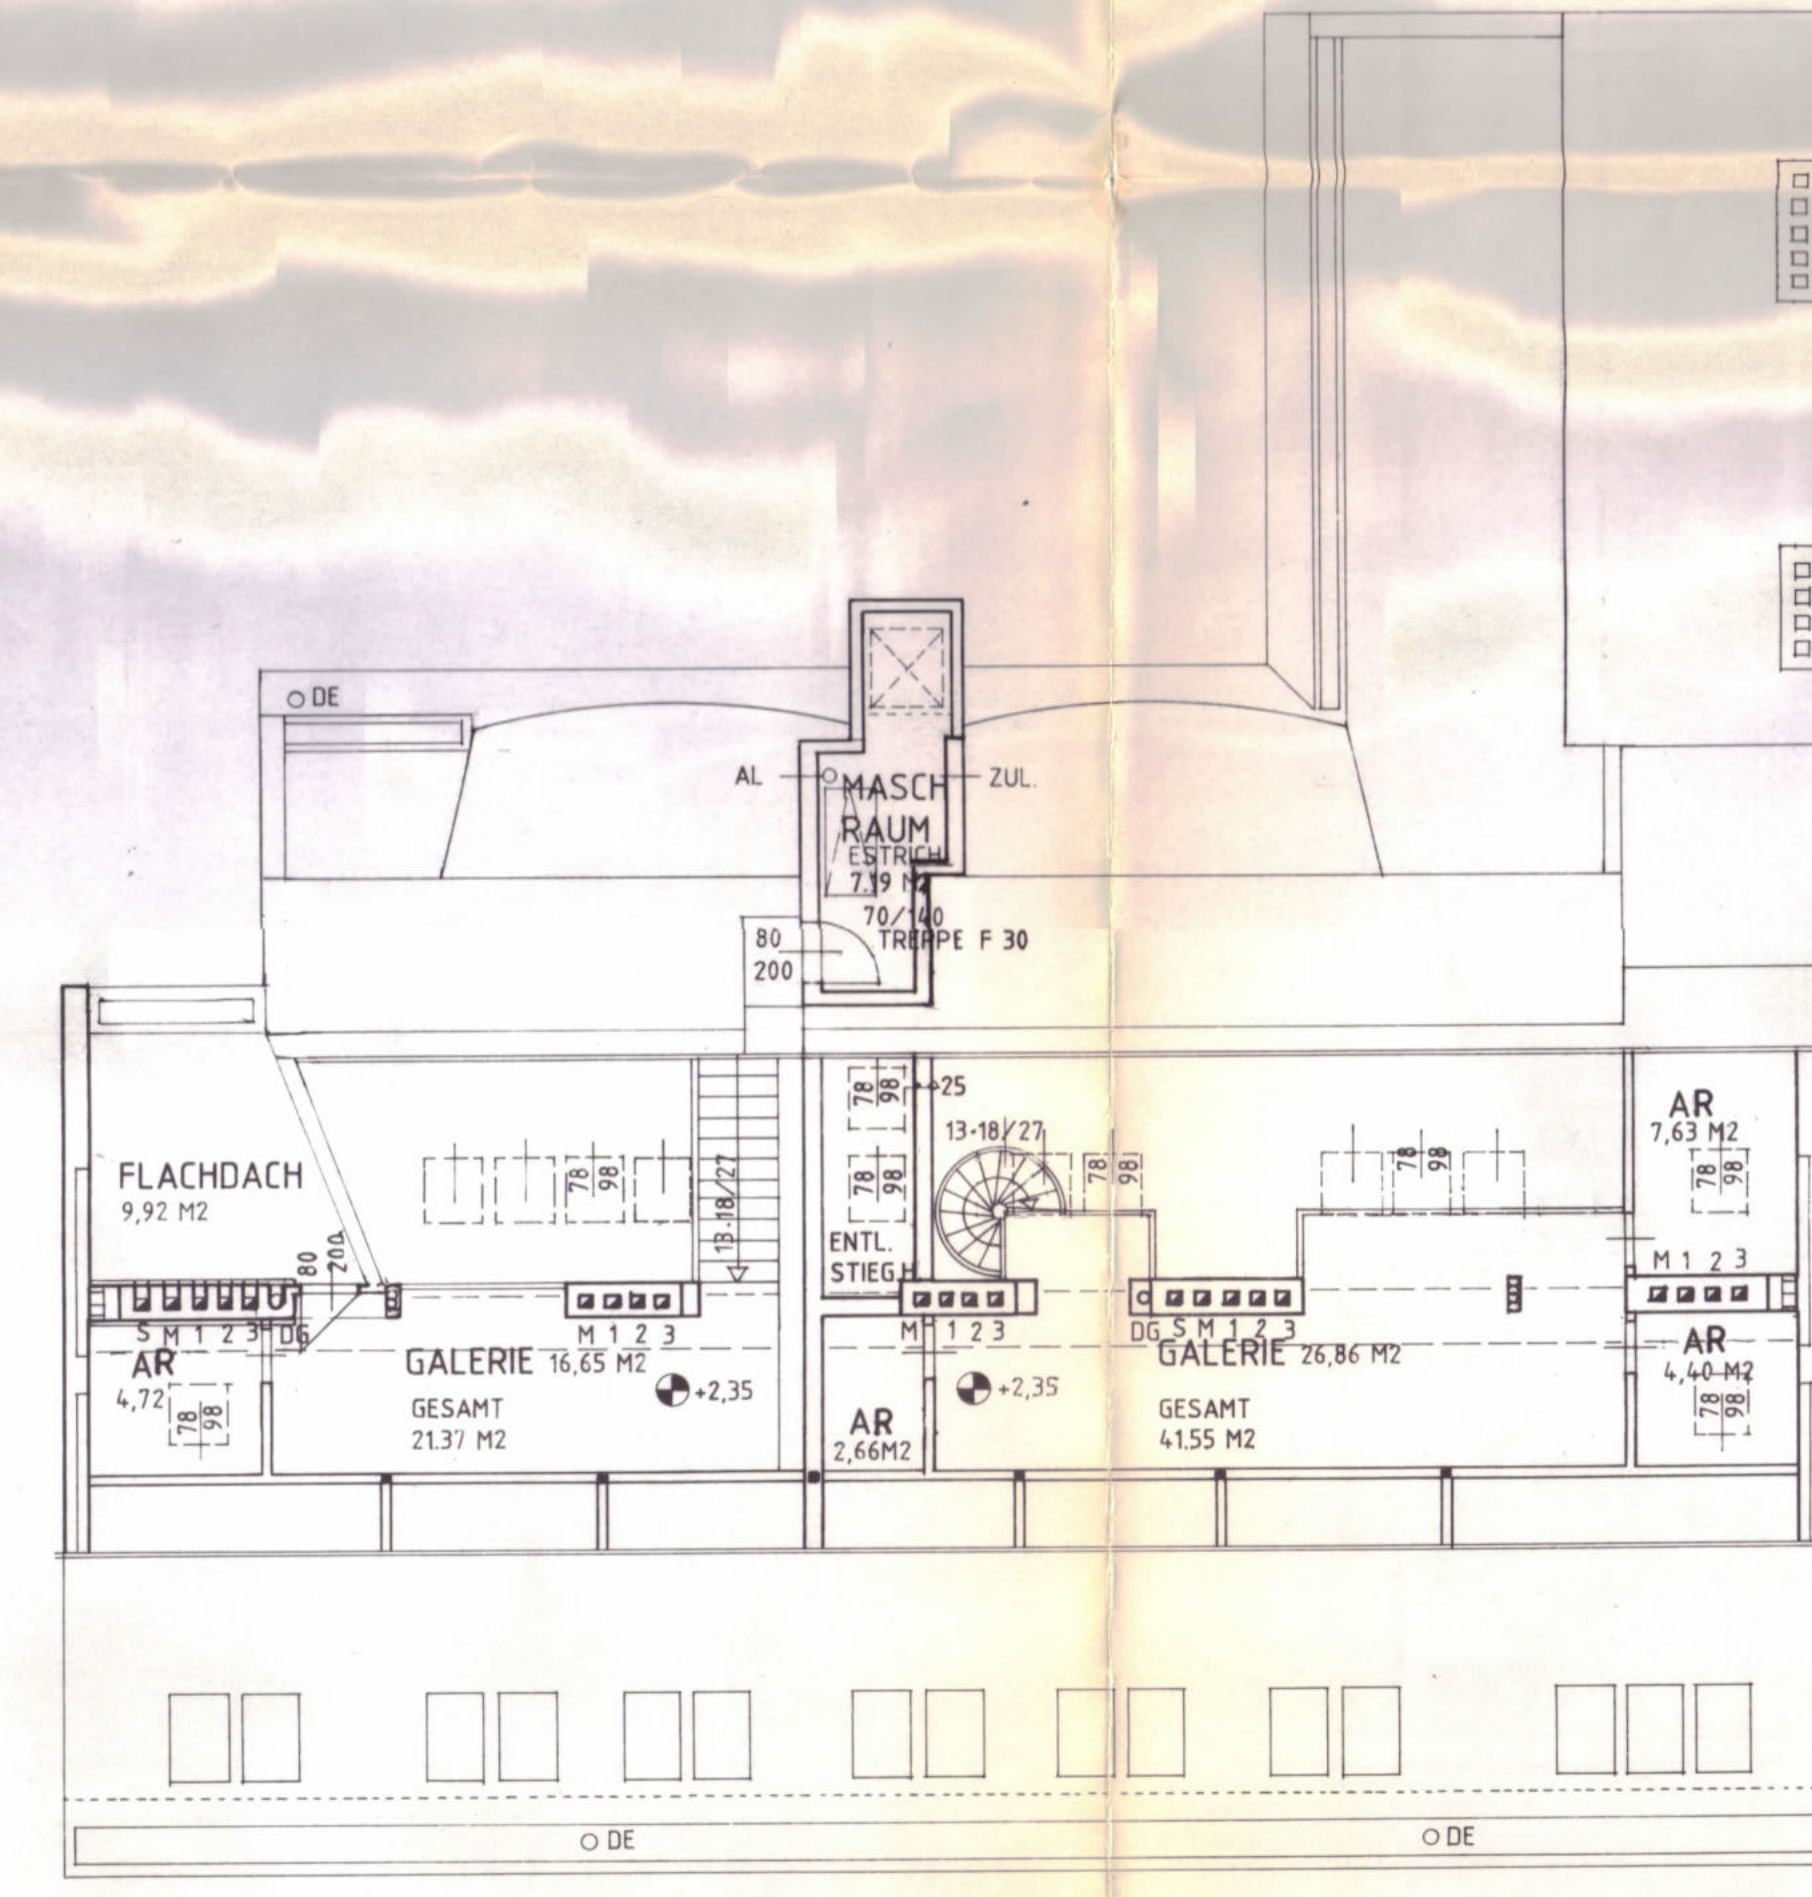


LUFTRAUM / GALERIE

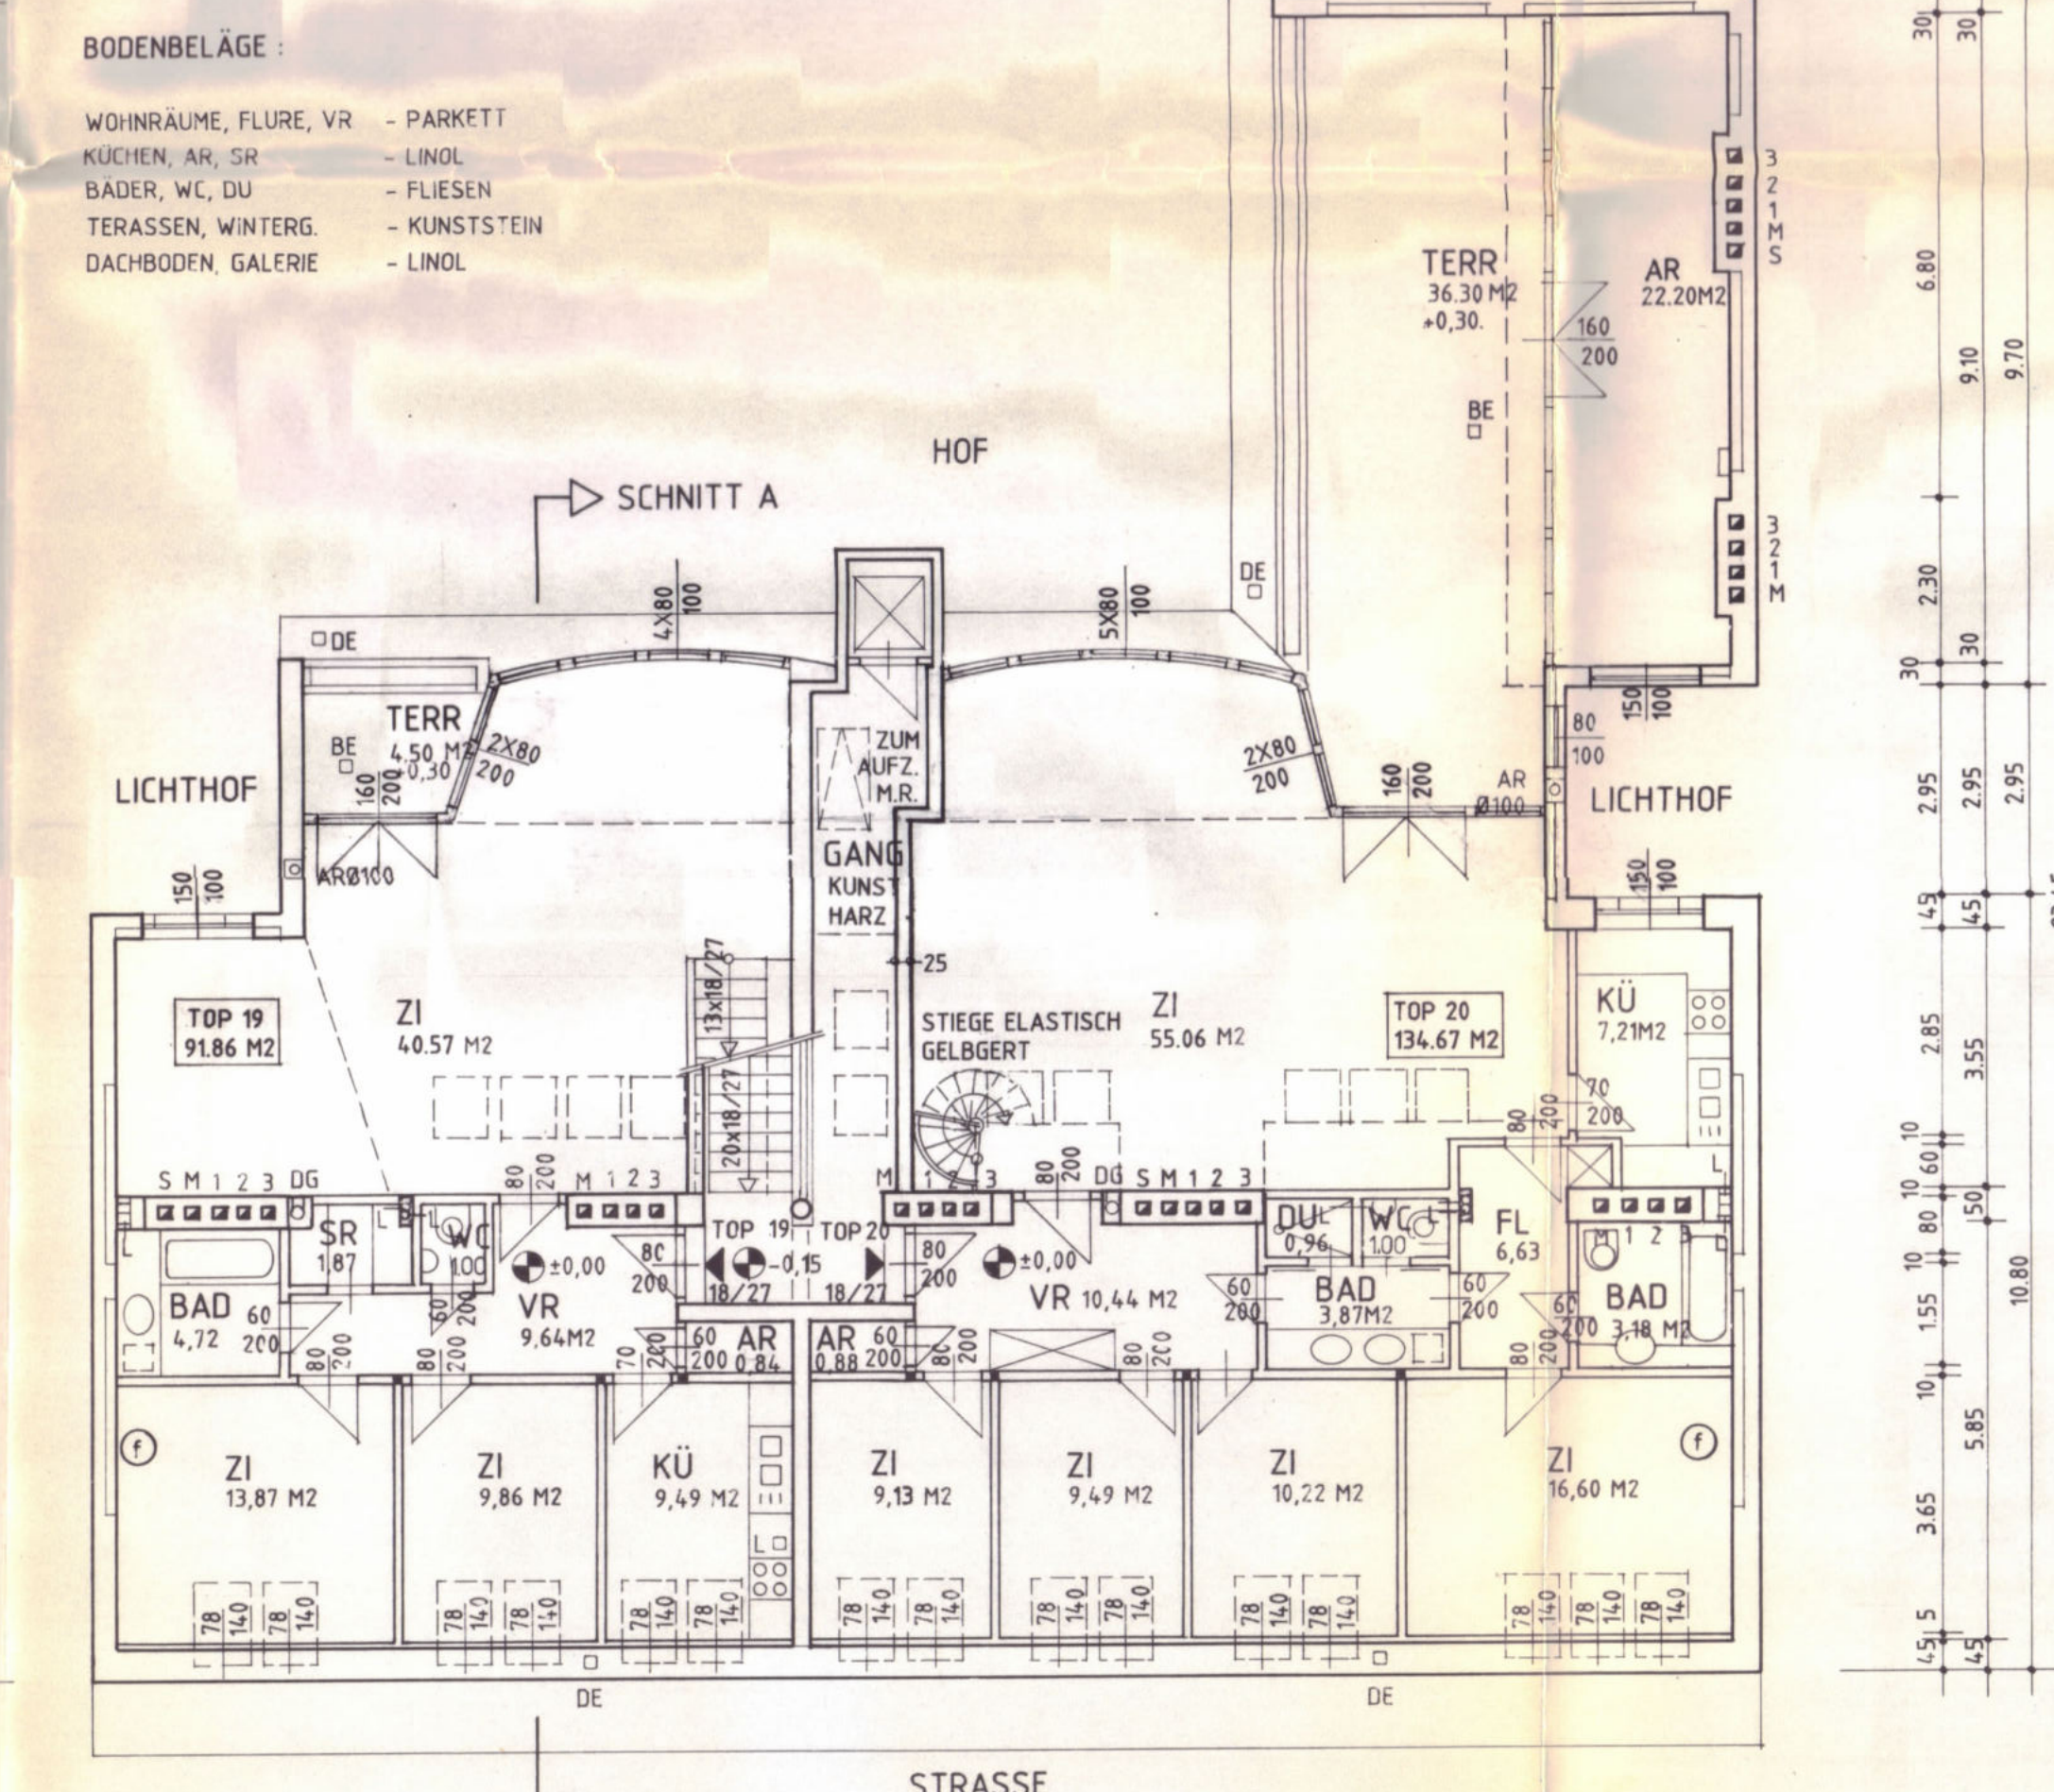

DACHGESCHOSS

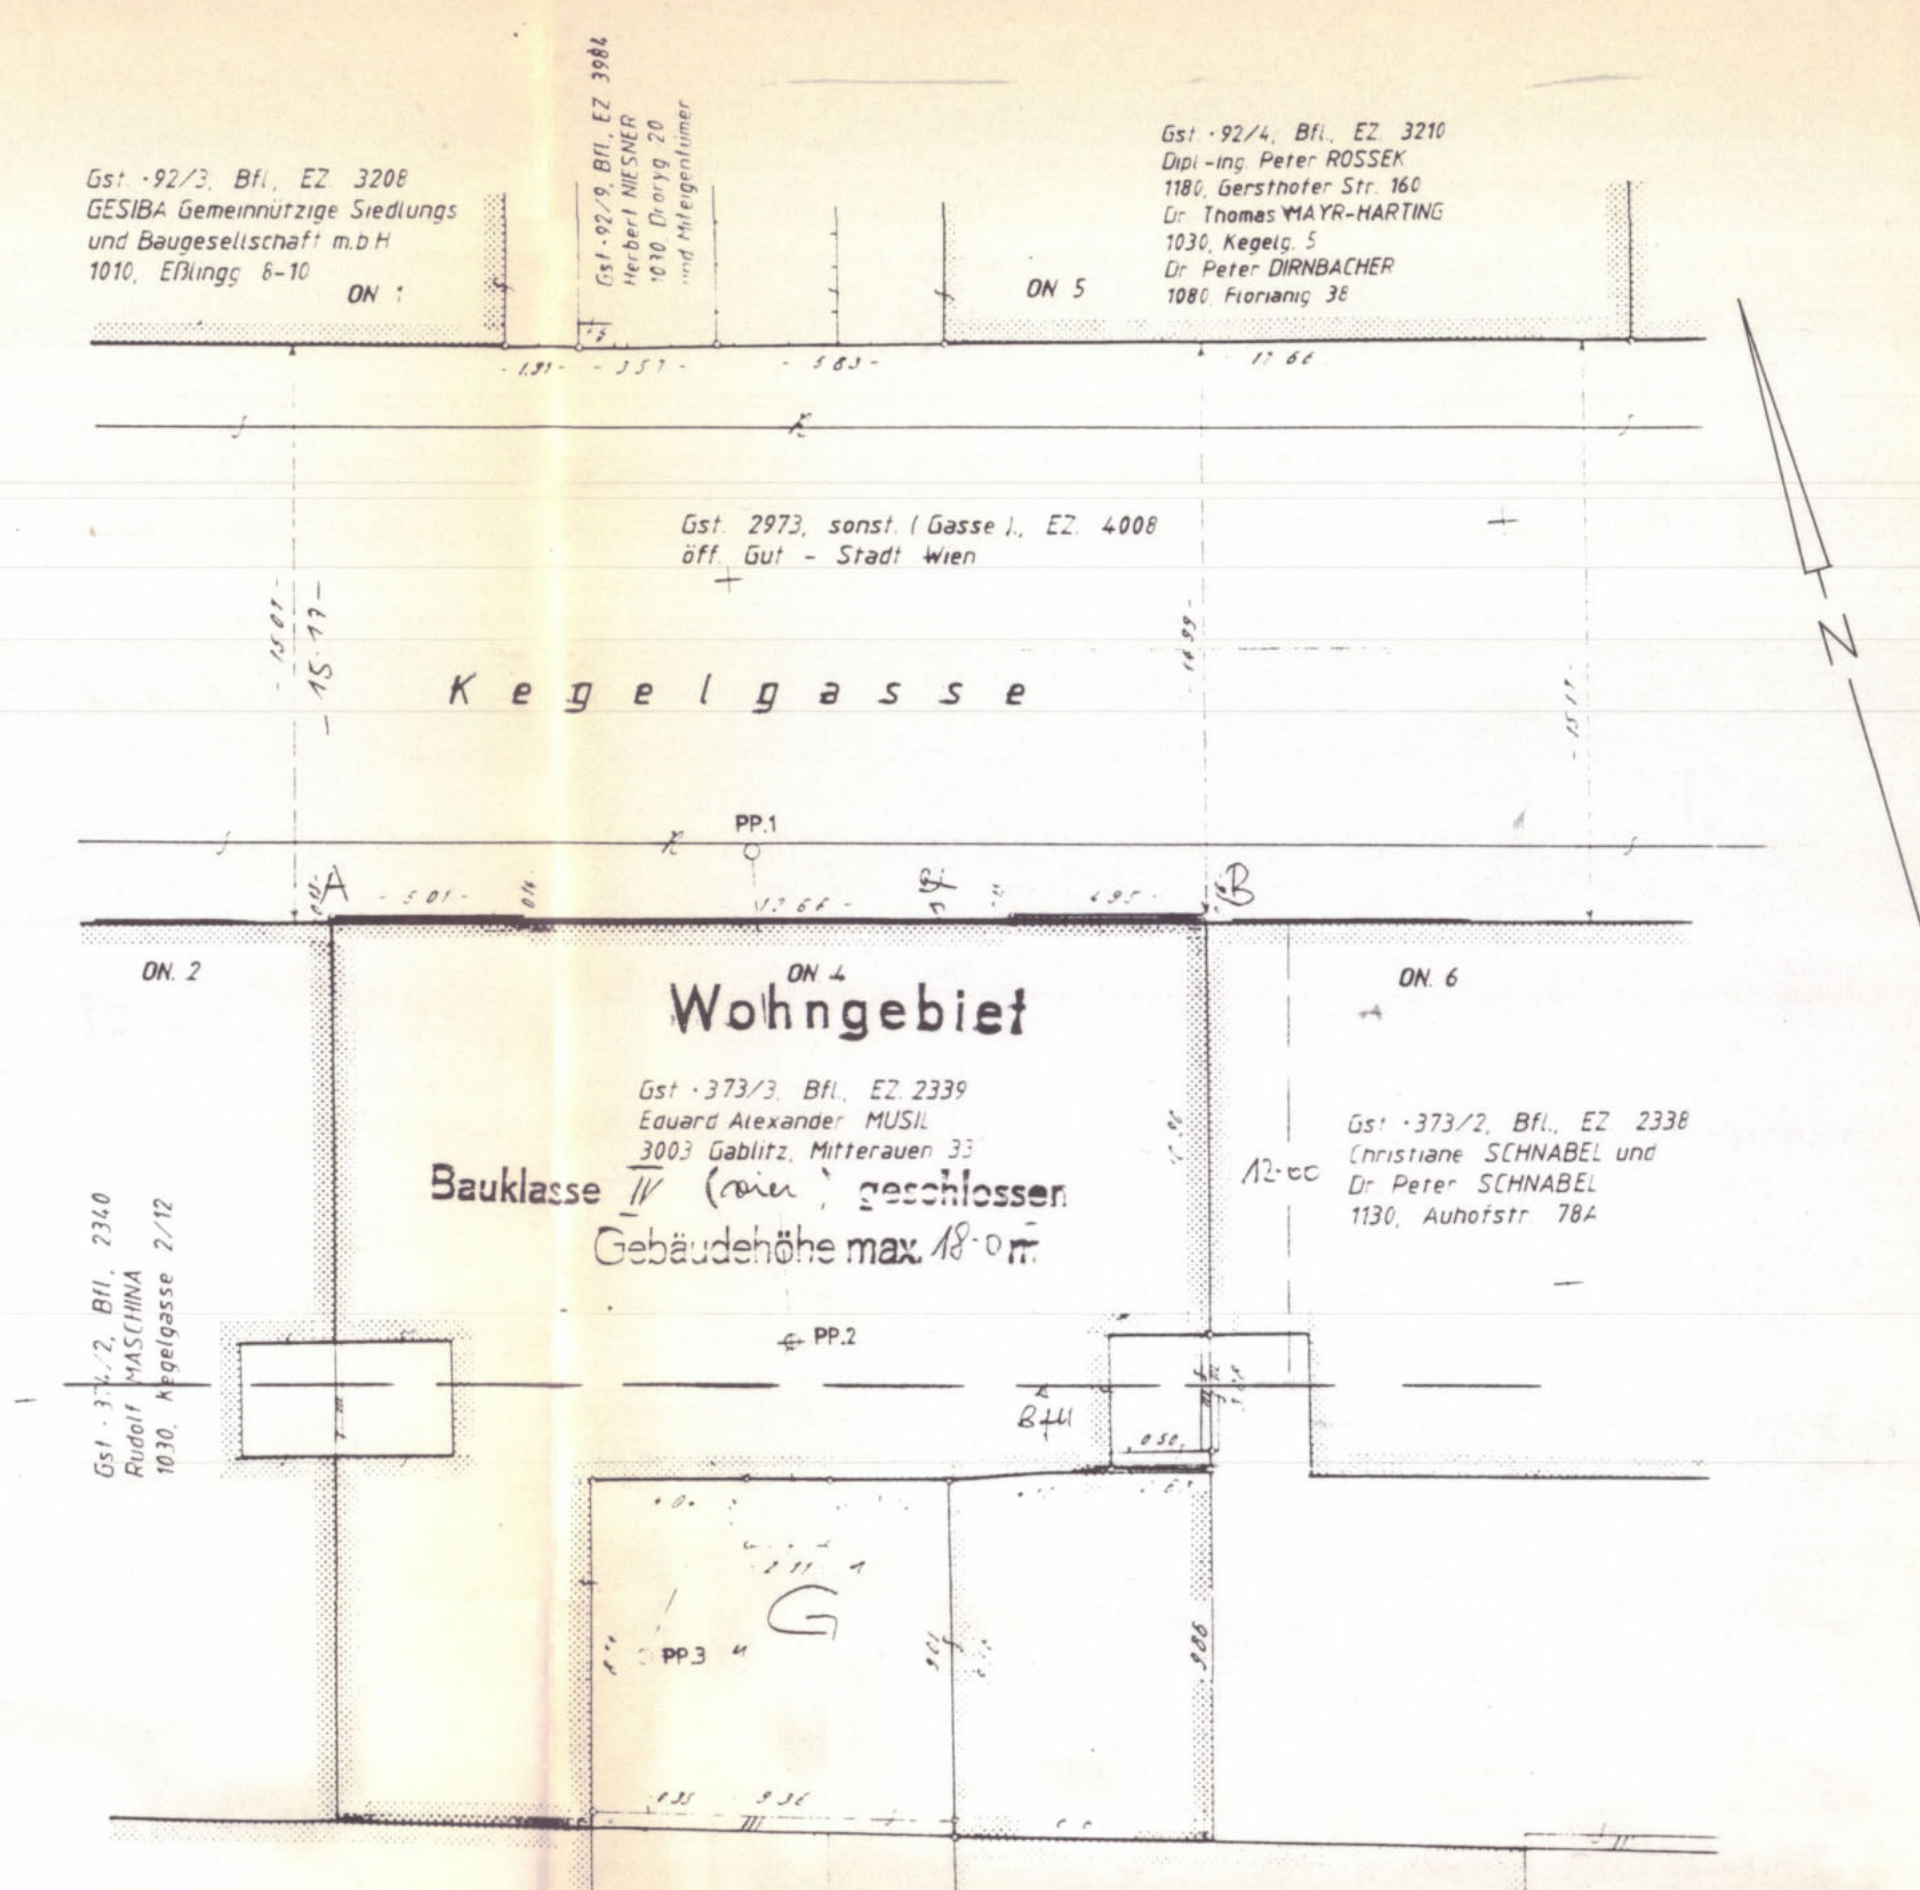

LAKEPLAN

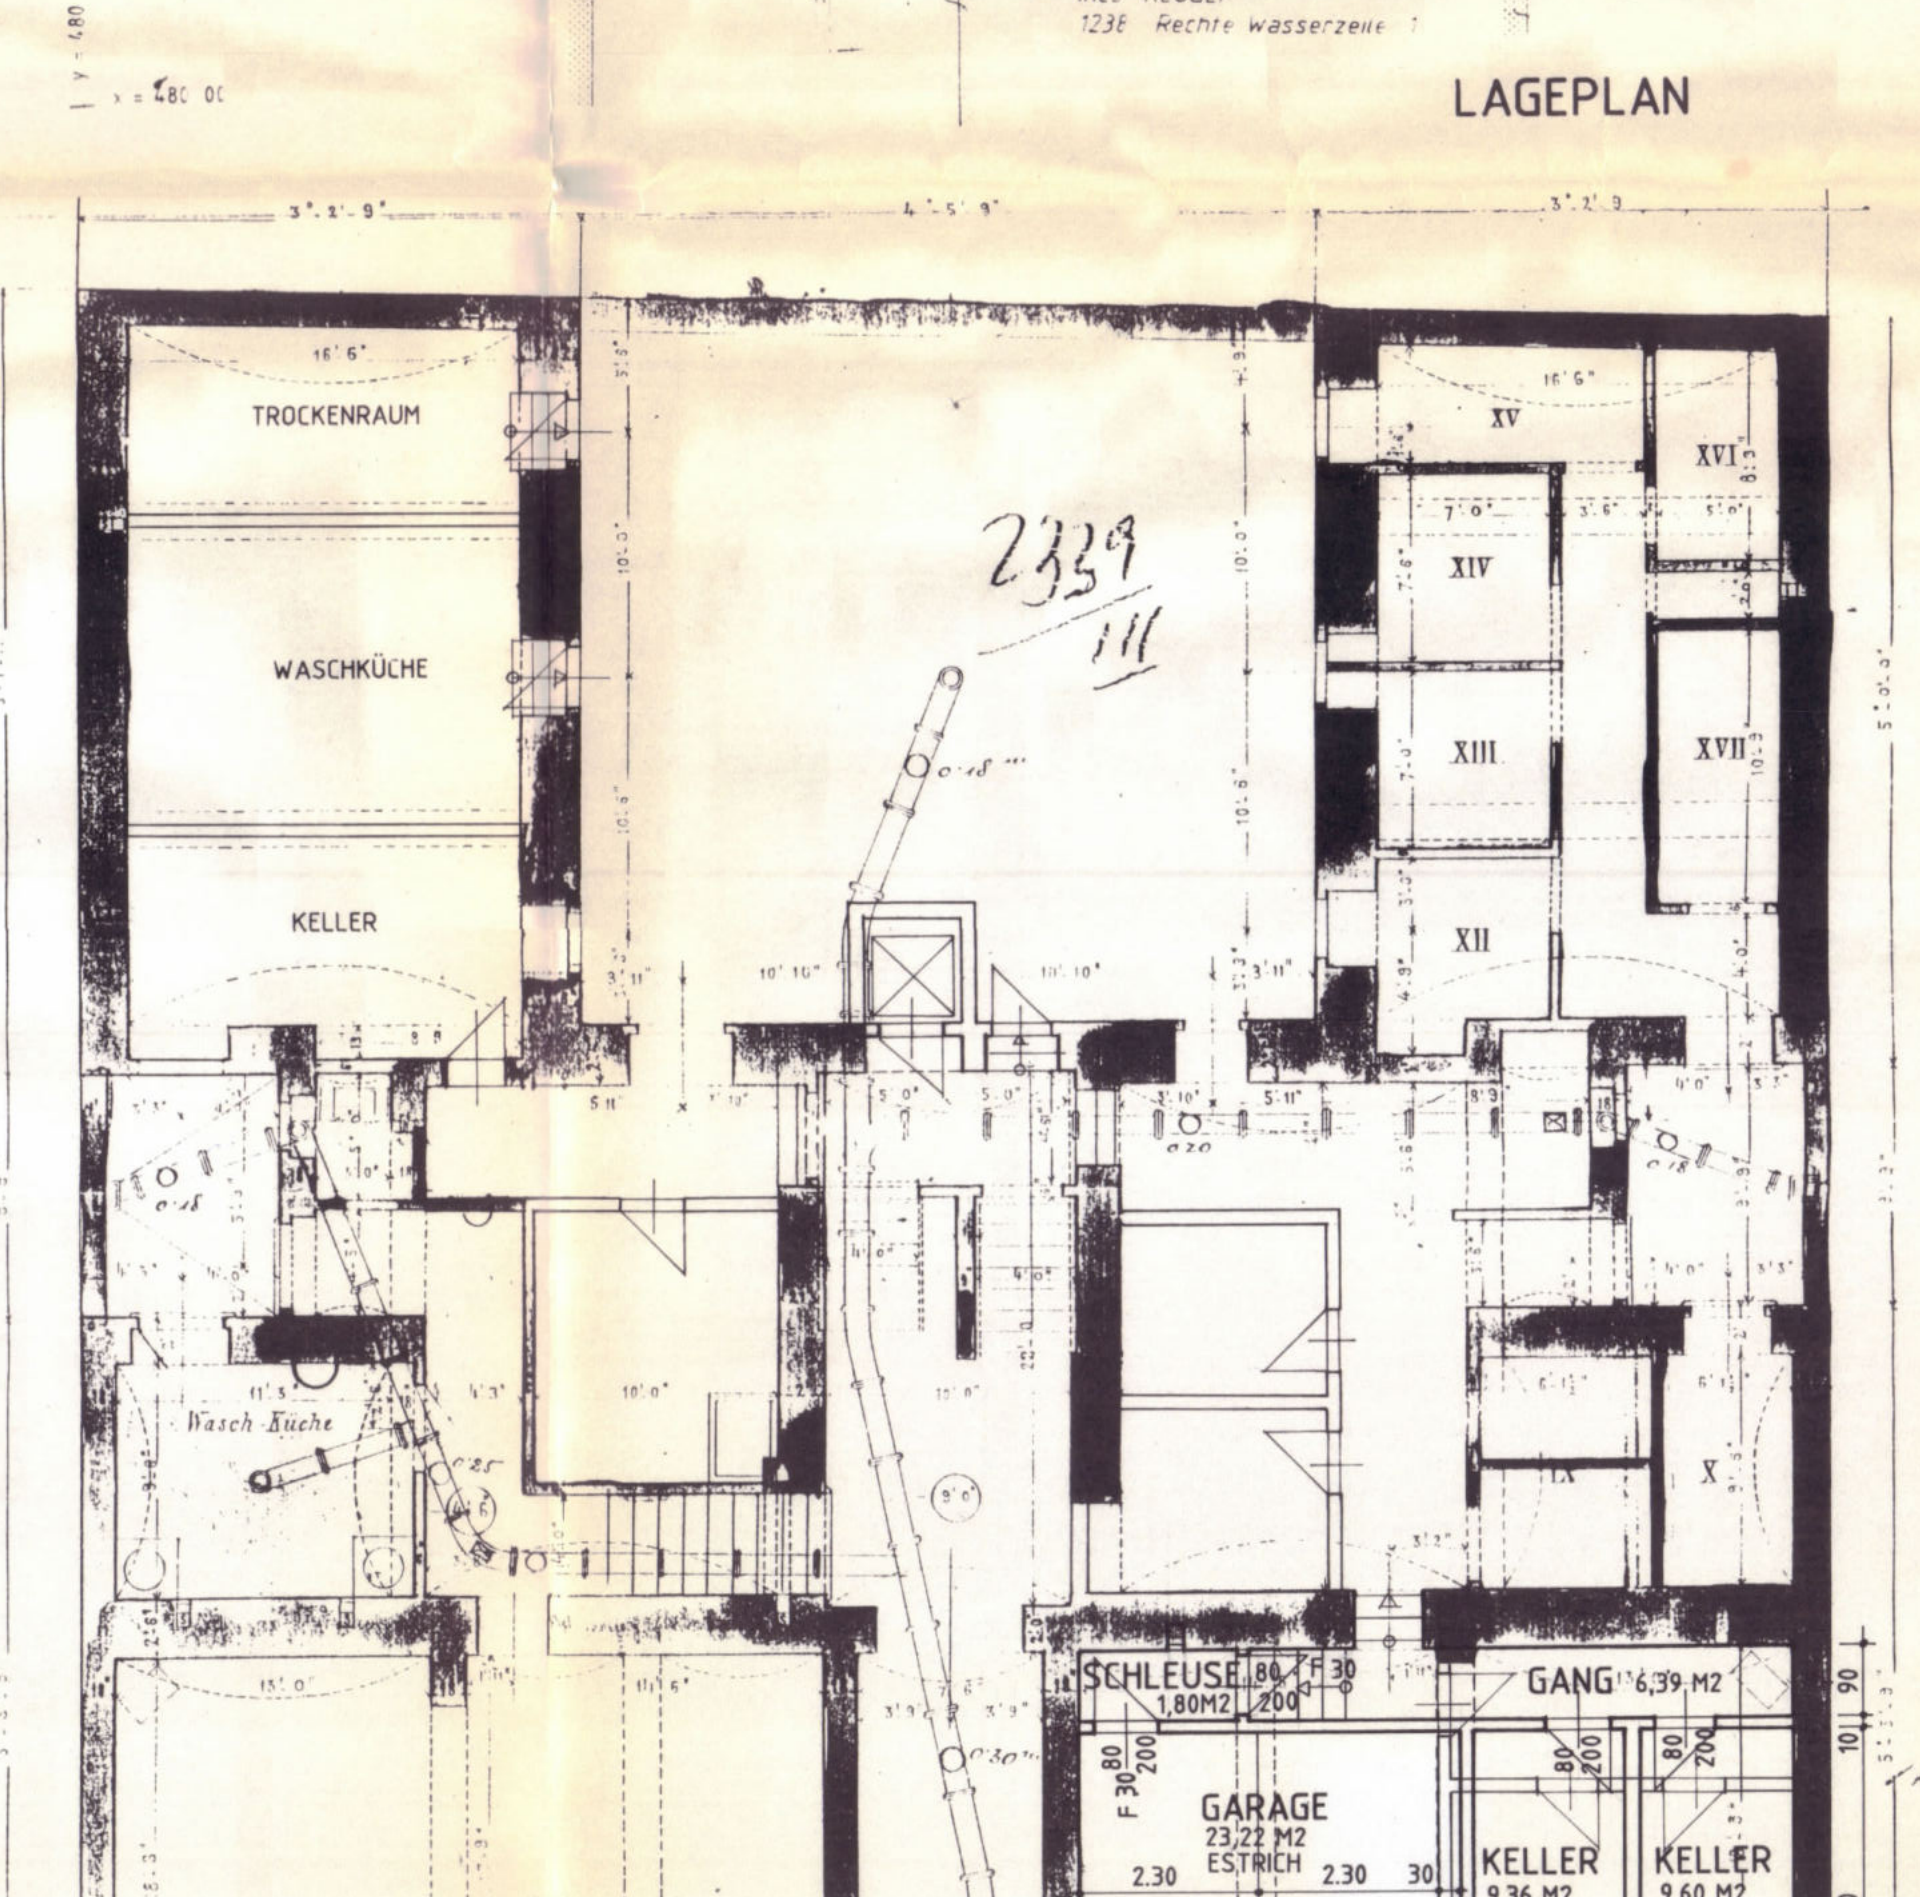

KNITT B

KONSTRUKTION

- 1 DACHAUFBAU
15 cm GK - PLATTEN
DAMPFBREMSE
70 cm LATUNG
50 cm KONTERLATUNG
DACHPAPPE
25 cm SCHALUNG
16.0 cm WD MIN. FASERMATTEN
25 cm SPARSCHALUNG
30 cm 2x15 GKF-PLATTEN
BEI GAUBEN BLECHENDECKUNG
- 2 FUSSBODENAUFBAU
10 cm BODENBELAG
10 cm BRANDSCHUTZPLATTEN THERMAX
25 cm SCHALUNG
20 cm TSD 25/20
36.0 cm WPE STARKTRÄGER, MIN. FASERM. 10 cm
15.0 cm DIPPELBAUDECKE
7.5 cm STUKKATUR, PUTZ
- 3 NASSRAUME
10 cm FLEBSPH
10 cm F-ISOlierUNG
70 cm ESTRICH
20 cm TRITTSCHALLDÄMMUNG 25/20
19.0 cm STB - DECKE
- 4 ZWISCHENDECKE
100 cm BODENBELAG
200 cm SPANPLATTEN
8.00 cm STAFFELKONSTRUKTION
150 cm GK - PLATTEN
- 5 TERRASSENDAUFBAU
50 cm BETONPLATTEN
20 cm LAGER ELASTISCH
80 cm ROOFMATE
FEUCHTKEITSSOLIERUNG 3-FACH
50 -100 cm GEFÄLLSBETON
80 cm WÄRMEDÄMMUNG / TSD
70 cm STB - PLATTE
- 6 TREMPPELWÄNDE / FEUERMAUER
15 cm GK - PLATTEN
DAMPFBREMSE
8.0 cm WD MIN. FASERMATTEN / STAFFELN
15.0 -45.0 cm ZIEGELMAUERWERK
AUSSENPUTZ
- 7 ZWISCHENWÄNDE
125 cm GK - PLATTEN
6.0 cm PROFILSTÄNDER - MIN. FASERMATTEN
125 cm GK - PLATTEN
- 8 WOHNUNGSTRENNWÄNDE - ZWEIFACHIG
2x125 cm GKF-PLATTEN
6.0 cm PROFILSTÄNDER - MIN. FASERMATTEN
125 cm GK-PLATTEN
6.0 cm PROFILSTÄNDER - MIN. FASERMATTEN
2x125 cm GKF-PLATTEN
25 cm VOLLZIEGELWAND ZUR STIEGE
- 9 AUSSENWÄNDE LEICHTBAU
10 cm ETERNIT
25 cm LATUNG 24/50
15 cm SPANPLATTEN
100 cm STEHER / MIN. FASERPLATTEN
15 cm SPANPLATTEN
7x125 cm GKF-PLATTEN
- 10 INNENTREPPEN
25 cm HARHOLZSTUFEN
20 cm TSD-PLATTEN 25/20
16.0 cm STB-PLATTE
10.0 cm MIN. FASERMATTEN
10 cm GK-PLATTEN

EINREICHPLAN
FÜR DEN DACHGESCHOSSAUFBAU
1030 WIEN, KEGELGASSE 4
GST Nr 373/3, EZ 2339, KG. LANDSTR.
M 1:100
WIEN, OKT. 1990

LEGENDE

- ABBRUCH
BESTAND
STAHLBETON
ZIEGEL
TRAGENDE, STAHL U. HOLZKONSTRUKTIONEN F 60
ZWISCHENWÄNDE, GK - STÄNDERKONSTRUKTION

BAUWERBER:

GRUNDEIGENTÜMER:

PLANVERFASSER:

BAUFÜHRER: