EINREICHPLAN
PARIE C

FÜR DEN DACHGESCHOSSAUSBAU
1030 WIEN, KEGELGASSE 4
GST Nr 373/3, EZ 2339, KG. LANDSTR.

Magistrat der Stadt Wien
Magistratsabteilung 37
Außenstelle für den 3., 5. Bez.
3, Am Modenapark 1-2
1031 Wien

M 1:100

Magistratsabteilung 19
Zahl B3/6251/90
Beilagen 1
EINGANG 31. 10. 90 + 20.11.90
AUSGANG 1.11.90 + 21.11.90

WIEN, OKT. 1990

Magistrat der Stadt Wien
Magistratsabteilung 37
Baupolizei
Hierauf bezieht sich der Bescheid
MA 37/3-Kegelg. 4/3488/90
Wien, am 10. Juli 1991
Für den Abteilungsleiter:
Dipl.-Ing. Hahn
Oberstadtbaurat

LEGENDE

- 🟨 ABBRUCH
- ⬜ BESTAND
- ⬛ STAHLBETON
- 🟥 ZIEGEL
- 🟥 TRAGENDE, STAHL U. HOLZKONSTRUKTIONEN F 60
- 🟧 ZWISCHENWÄNDE, GK - STÄNDERKONSTRUKTION

~~MA 37~~/ BV 3 - A 917/91
Dem Beschluß des Bauausschußes
vom 11. Juni 1991 zugrunde
gelegen.

BAUWERBER:

Hannelore Schwarz

GRUNDEIGENTÜMER:

PAUL PADELEK
GESCHÄFTSFÜHRER
FRIEDRICH & PADELEK Ges.m.b.H.
1080 WIEN, LANGE GASSE 50

PLANVERFASSER:

ARCHITEKT DIPL. ING. GEORG ... BEFUGTER UND BEEIDETER ... WIEN
Georg

BAUFÜHRER:

E. SATLER
Baugesellschaft m. b. H.
Ketzergasse 57
1234 Wien, ☎ 69 49 81
Satler

KONSTRUKTION

ⓐ DACHAUFBAU

	DACHZIEGEL
3.0 cm	LATTUNG
5.0 cm	KONTERLATTUNG
	DACHPAPPE
2.5 cm	SCHALUNG
16.0 cm	WD. MIN. FASERMATTEN
2.5 cm	SPARSCHALUNG
3.0 cm	2x1.5 GKF PLATTEN

BEI GAUBEN BLECHEINDECKUNG

ⓑ FUSSBODENAUFBAU

1.0 cm	BODENBELAG
3.0 cm	BRANDSCHUTZPLATTEN THERMAX
26.0 cm	IPE STAHLTRÄGER, MIN. FASERM. 10 CM
2.5 cm	SCHALUNG
2.0 cm	TSD 25/20
ca 15.0 cm	DIPPELBAUMDECKE
2.5 cm	STUKKATUR, PUTZ

ⓒ NASSRÄUME

1.0 cm	FLIESEN
1.0 cm	F - ISOLIERUNG
7.0 cm	ESTRICH
20 cm	TRITTSCHALLDÄMMUNG 25/20
19 0 cm	STB - DECKE

ⓔ ZWISCHENDECKE

1.00 cm	BODENBELAG
2.00 cm	SPANPLATTEN
8.00 cm	STAFFELKONSTRUKTION
1.50 cm	GK - PLATTEN

ⓓ TERRASSENAUFBAU

5.0 cm	BETONPLATTEN
2.0 cm	LAGER ELASTISCH
8.0 cm	ROOFMATE
	FEUCHTIGKEITSISOLIERUNG 3-FACH
5.0 -10.0 cm	GEFÄLLSBETON
8.0 cm	WÄRMEDÄMMUNG / TSD
20.0 cm	STB - PLATTE

ⓕ TREMPELWÄNDE / FEUERMAUER

1.5 cm	GK - PLATTEN
	DAMPFBREMSE
8.0 cm	WD. MIN. FASERMATTEN / STAFFELN
15.0 -45.0 cm	ZIEGELMAUERWERK
	AUSSENPUTZ

ⓖ ZWISCHENWÄNDE

1.25 cm	GK - PLATTEN.
6.0 cm	PROFILSTÄNDER + MIN. FASERMATTEN
1.25 cm	GK - PLATTEN

ⓗ WOHNUNGSTRENNWÄNDE - ZWEISCHALIG

2x1.25 cm	GKF-PLATTEN
6.0 cm	PROFILSTÄNDER + MIN.FASERMATTEN 5cm
1.25 cm	GKF- PLATTEN
6.0 cm	PROFILSTÄNDER + MIN.FASERMATTEN 5cm
2x1.25 cm	GKF- PLATTEN

25 cm VOLLZIEGELWAND ZUR STIEGE

ⓘ AUSSENWÄNDE LEICHTBAU

1.0 cm	ETERNIT
2.5 cm	LATTUNG 24/50
1.5 cm	SPANPLATTEN
10.0 cm	STEHER / MIN. FASERPLATTEN 8cm
1.5 cm	SPANPLATTEN
2x1.25cm	GKF -PLATTEN

ⓚ INNENTREPPE

2.5 cm	HARTHOLZSTUFEN
2.0 cm	TSD- PLATTEN 25/20
18.0 cm	STB- PLATTE
10.0 cm	MIN. FASERMATTEN
1.0 cm	GK PLATTEN

DER PLAN LIEGT DER STELLUNGNAHME DER
MAGISTRATSABTEILUNG 35 - B ZUGRUNDE.
WIEN, AM 1990 -11- 13 SACHB.:

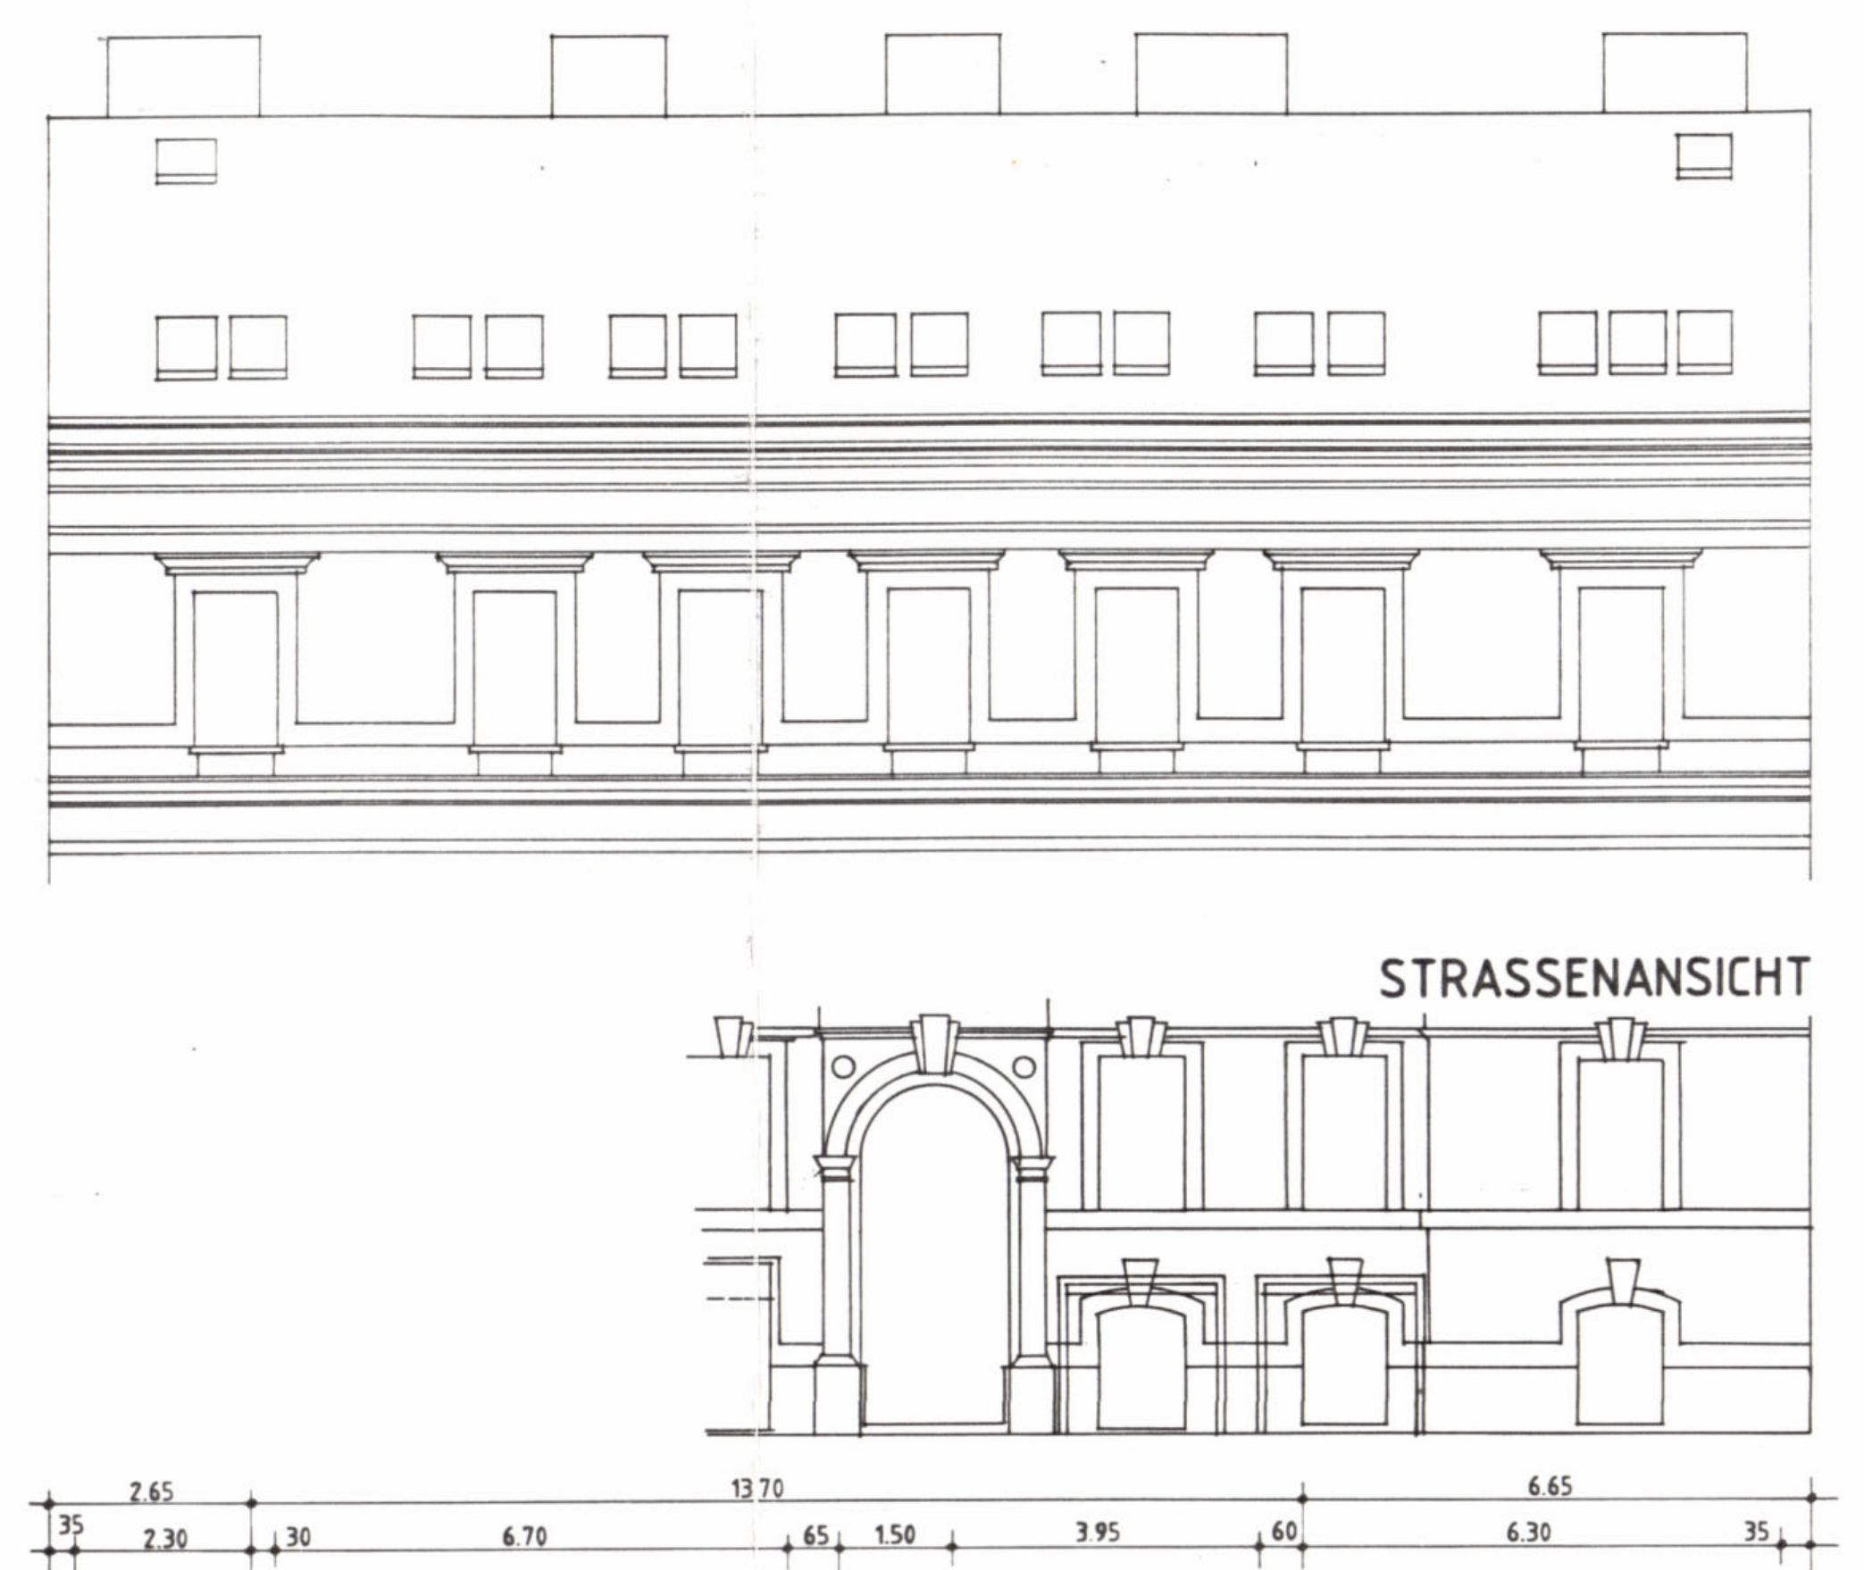
STRASSENANSICHT

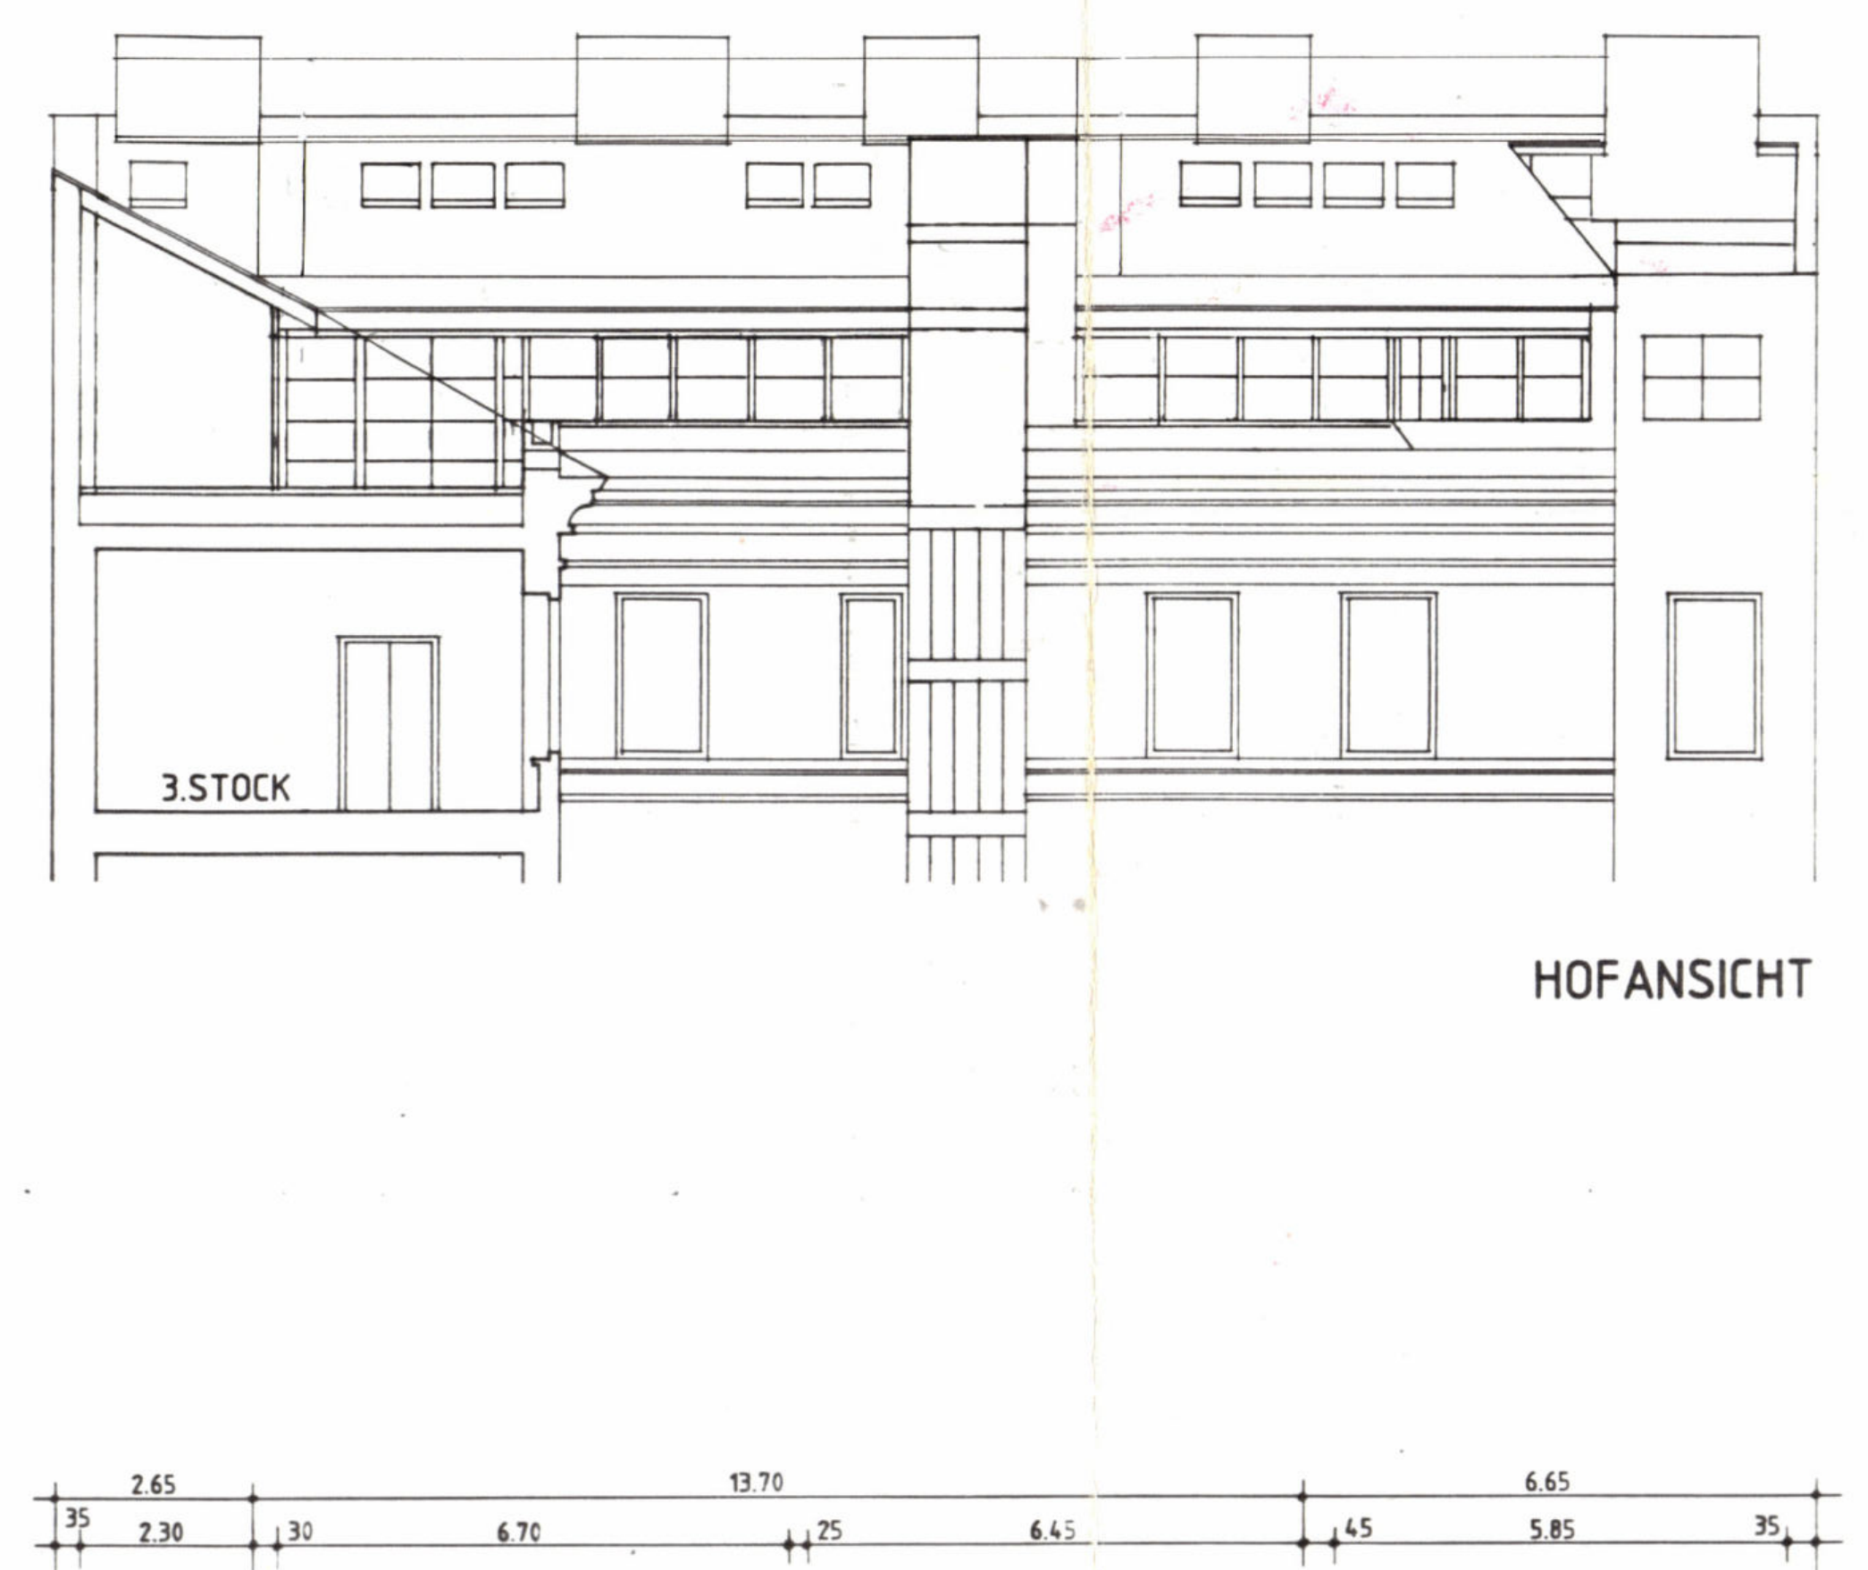
HOFANSICHT

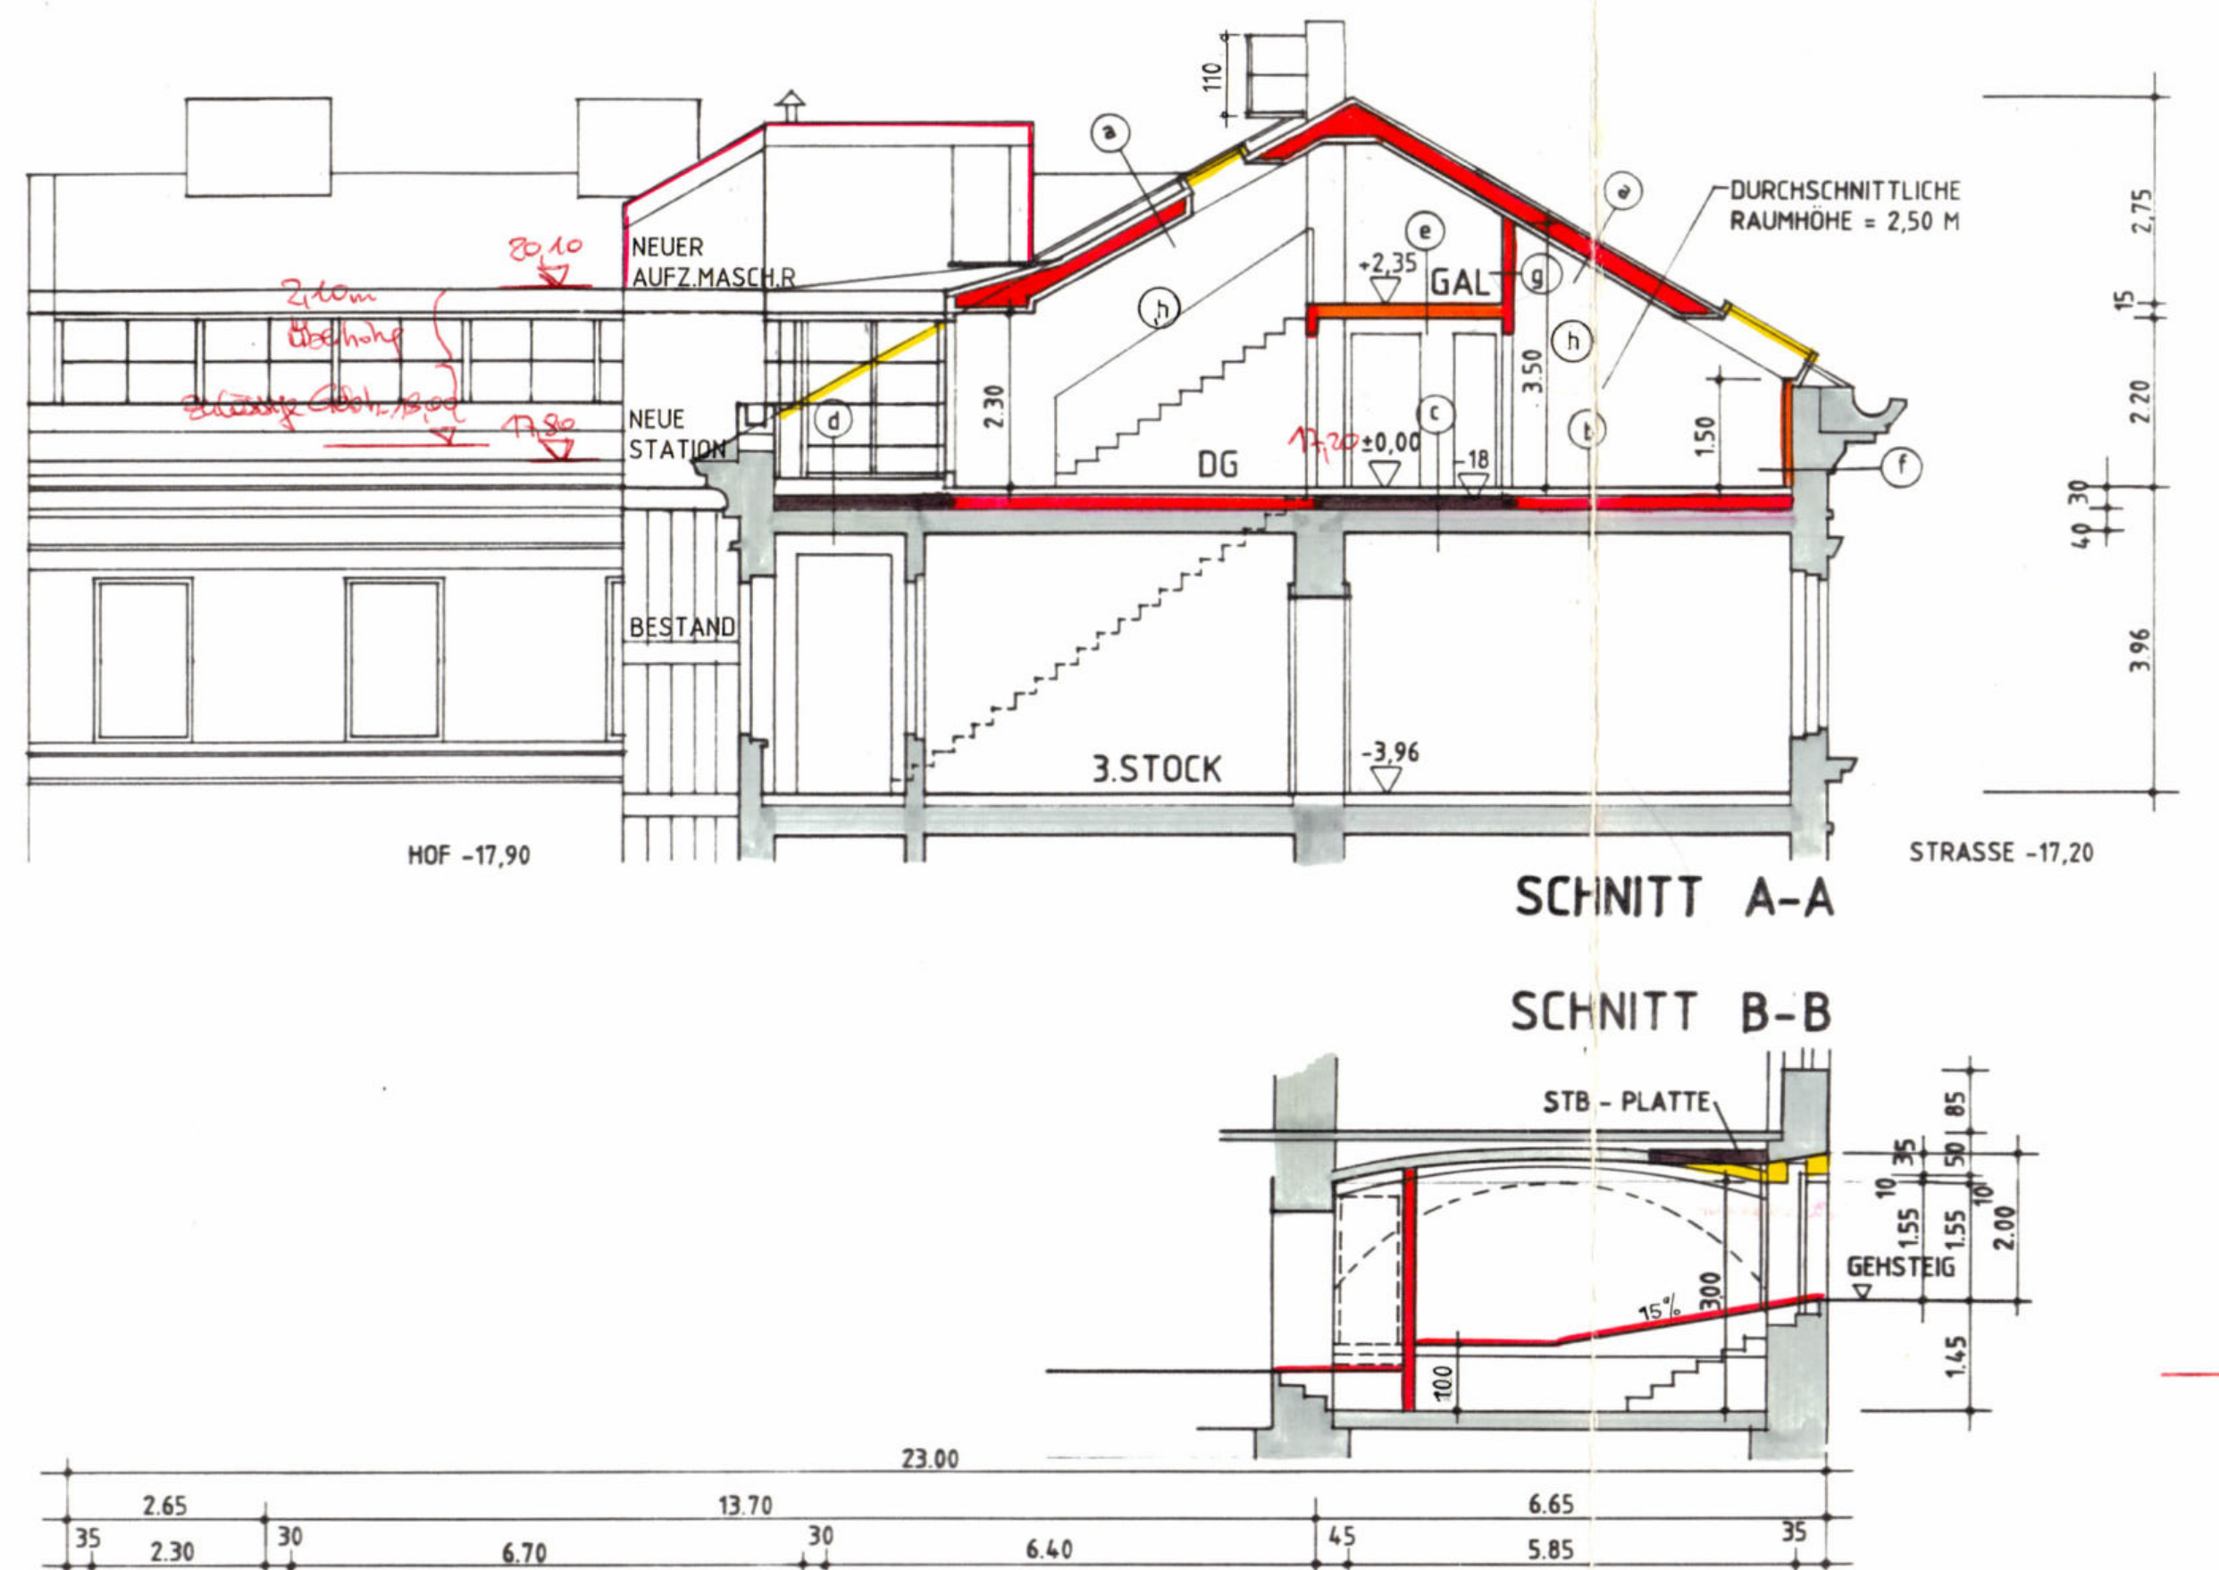

SCHNITT A-A

SCHNITT B-B

17. April 1991
Bebauungsbestimmungen vom 16.08.80, lt. MA 37/V-3/3780/80 übertragen

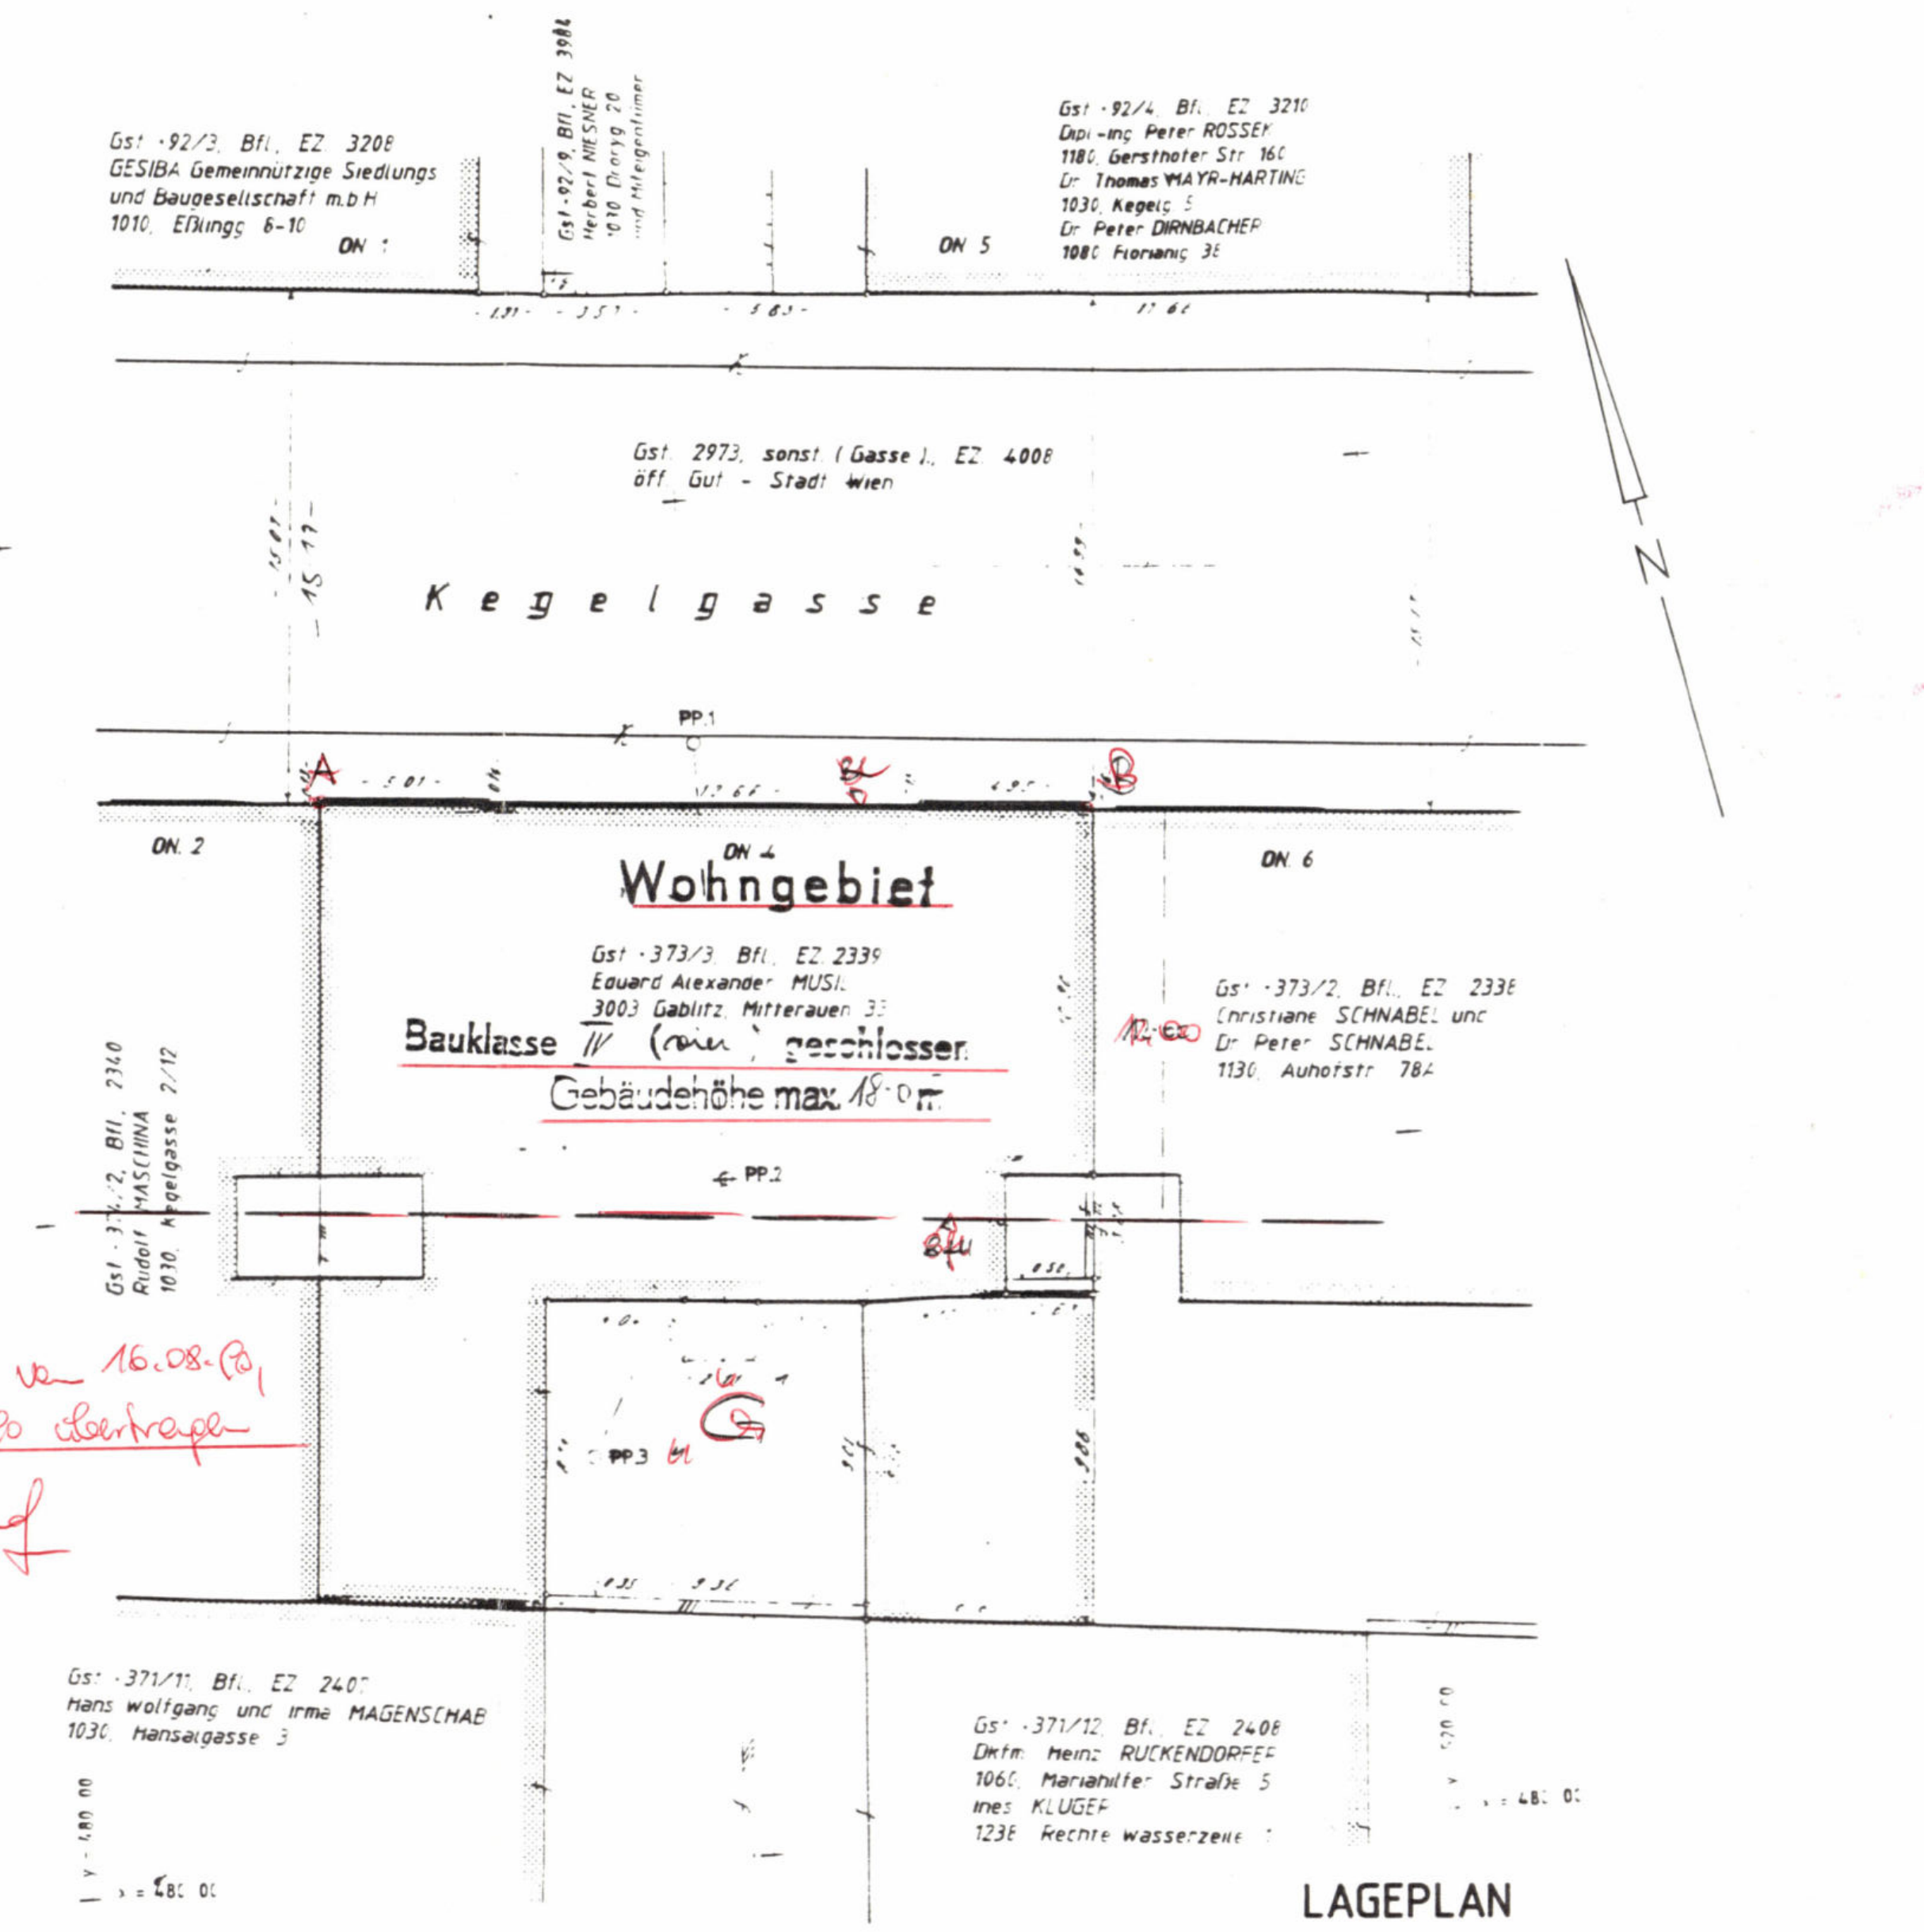
Gst. 92/3, Bfl., EZ 3208
GESIBA Gemeinnützige Siedlungs und Baugesellschaft m.b.H.
1010, Eßlingg. 8-10
Gst. 92/4, Bfl., EZ 3210
Dipl.-Ing. Peter ROSSEK
1180, Gersthofer Str. 160
Dr. Thomas MAYR-HARTING
1030, Kegelg. 5
Dr. Peter DIRNBACHER
1080 Florianig. 35
Gst. 2973, sonst. (Gasse), EZ 4008
öff. Gut - Stadt Wien
Kegelgasse
Wohngebiet
Gst. 373/3, Bfl., EZ 2339
Eduard Alexander MUSIL
3003 Gablitz, Mitterauen 33
Bauklasse IV (rein) geschlossen
Gebäudehöhe max. 18.0 m
Gst. 373/2, Bfl., EZ 2338
Christiane SCHNABEL und Dr. Peter SCHNABEL
1130, Auhofstr. 78A
Gst. 371/11, Bfl., EZ 2407
Hans Wolfgang und Irma MAGENSCHAB
1030, Hansalgasse 3
Gst. 371/12, Bfl., EZ 2408
Dkfm. Heinz RUCKENDORFER
1060, Mariahilfer Straße 5
Ines KLUGER
1238 Rechte Wasserzeile
N
LAGEPLAN

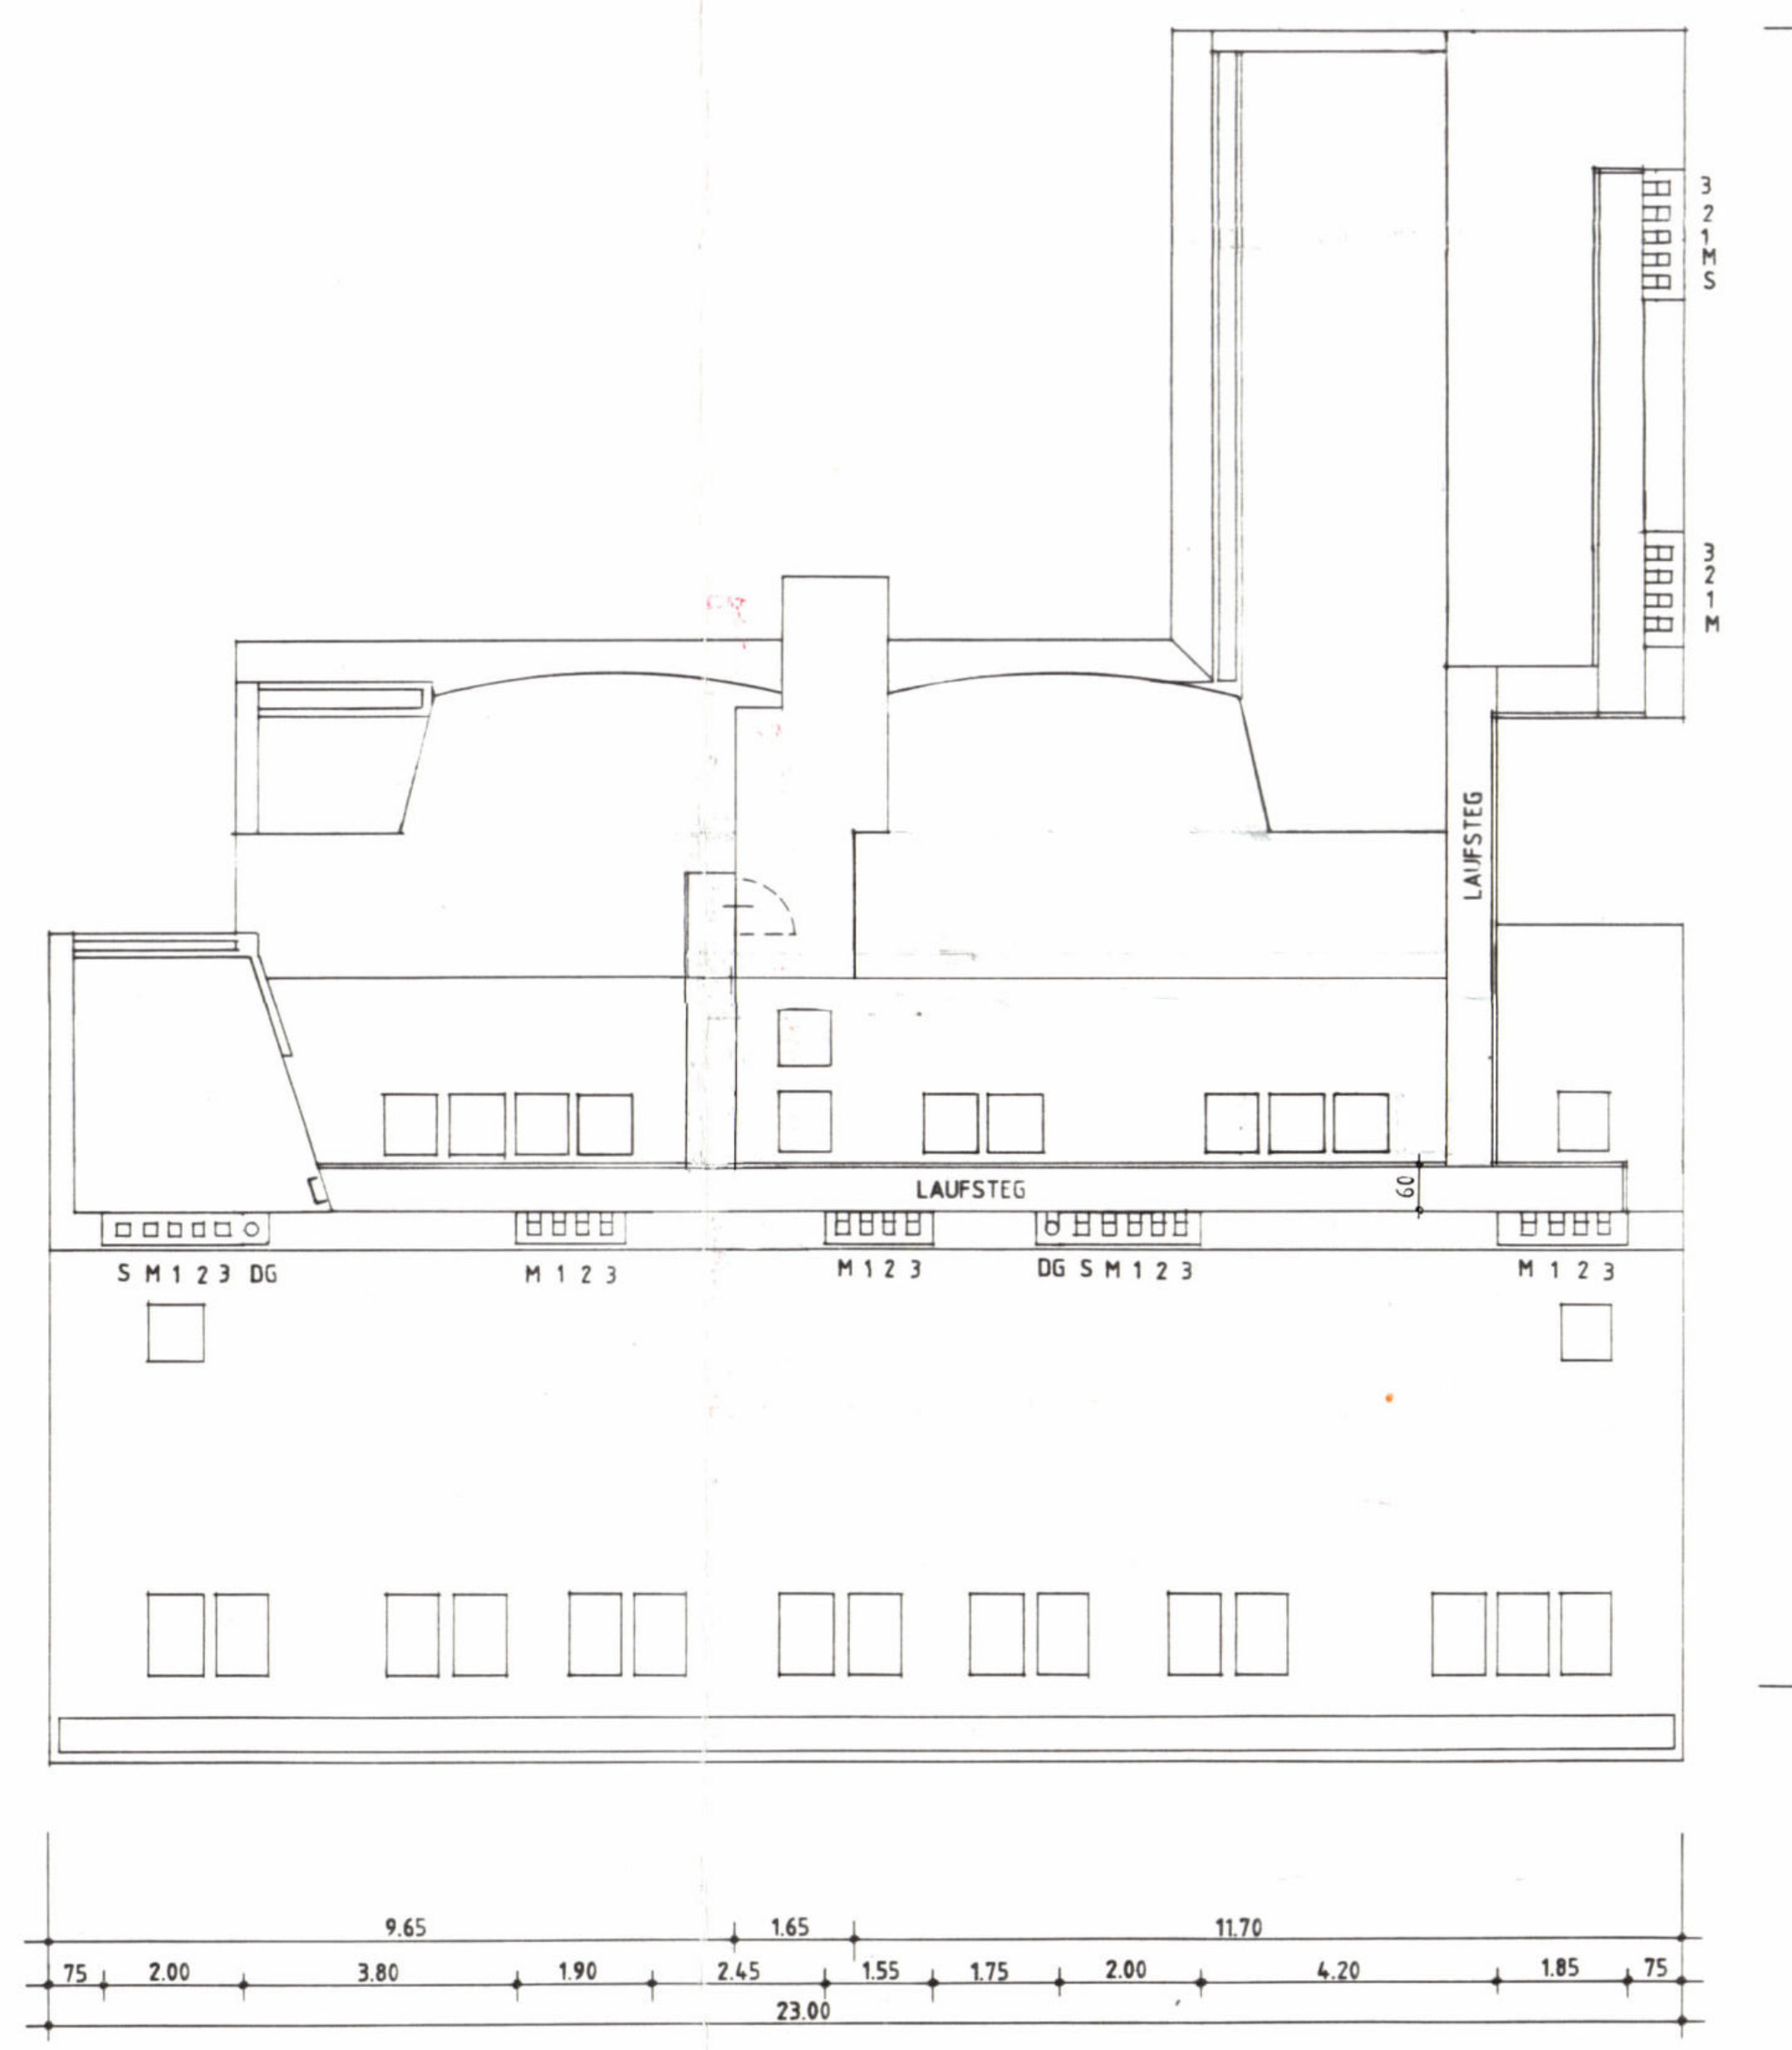
DACHDRAUFSICHT

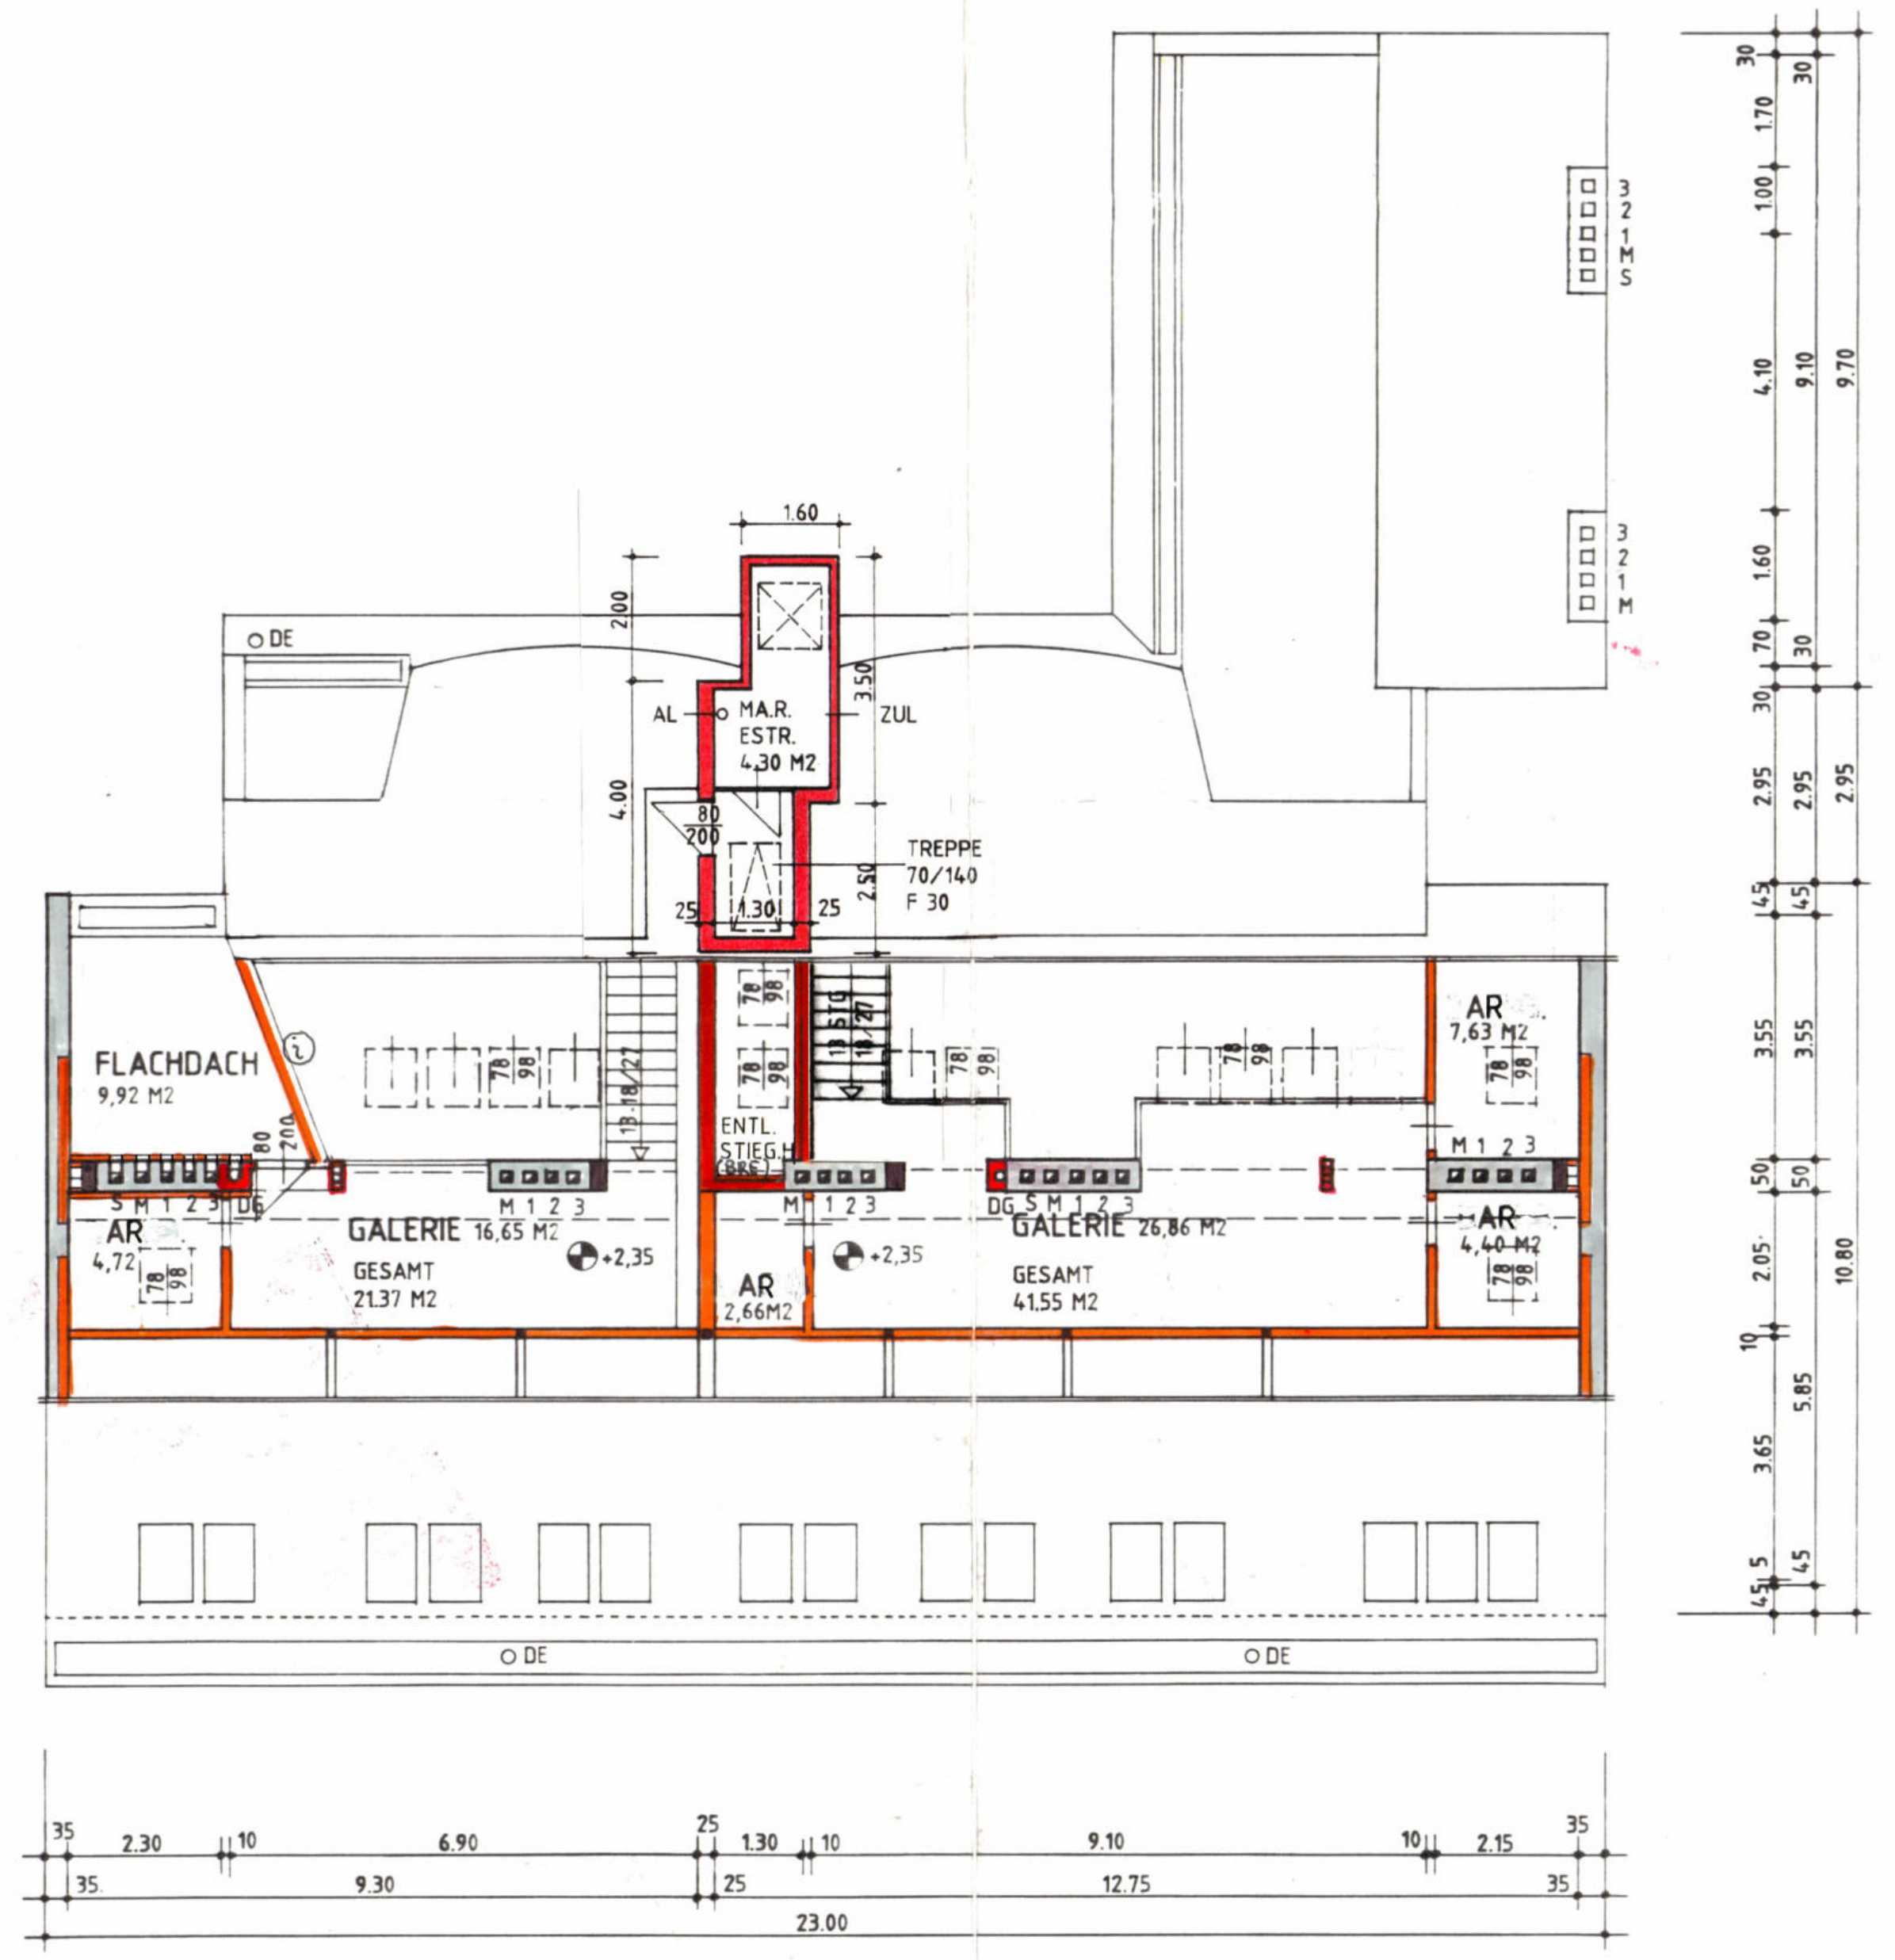

LUFTRAUM / GALERIE

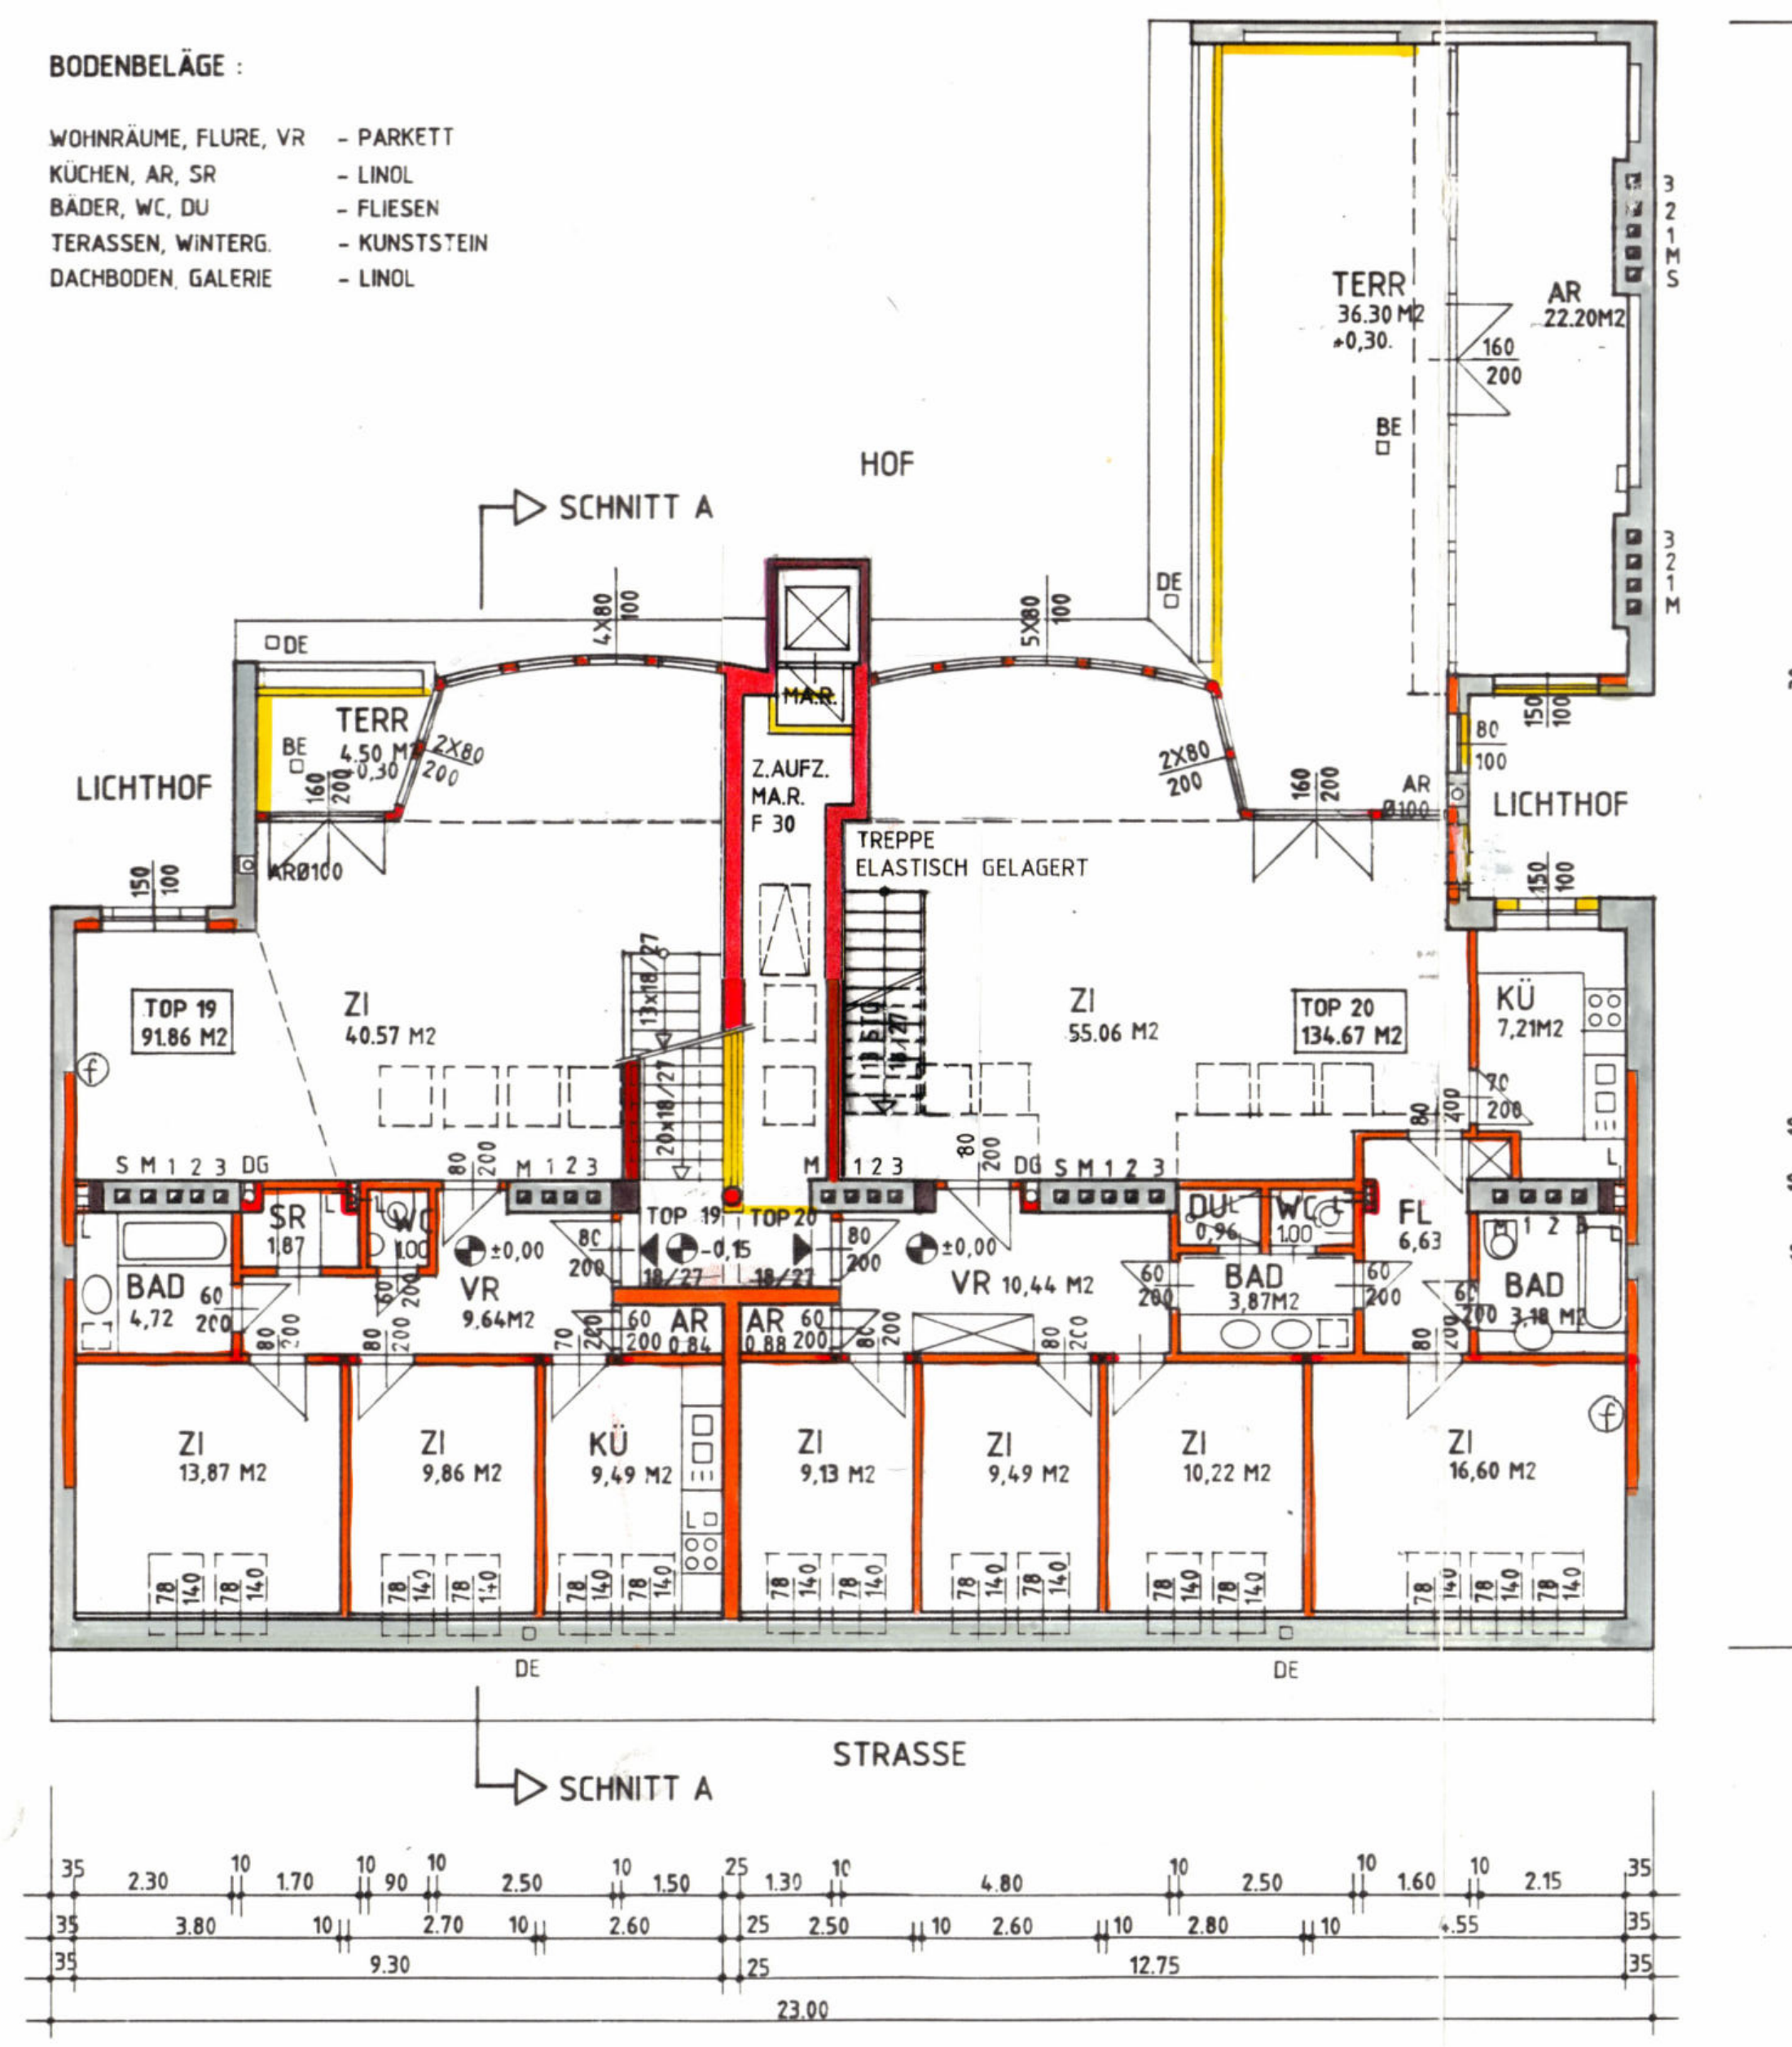
BODENBELÄGE:

WOHNRÄUME, FLURE, VR	- PARKETT
KÜCHEN, AR, SR	- LINOL
BÄDER, WC, DU	- FLIESEN
TERASSEN, WINTERG.	- KUNSTSTEIN
DACHBODEN, GALERIE	- LINOL

DACHGESCHOSS

1990 -10- 23
Magistratsabteilung 46
Verkehrsorganisation und
techn. Verkehrsangelegenheiten
Kein Einwand vom
Verkehrsstandpunkt.
ING. WALDEGG-LINDL

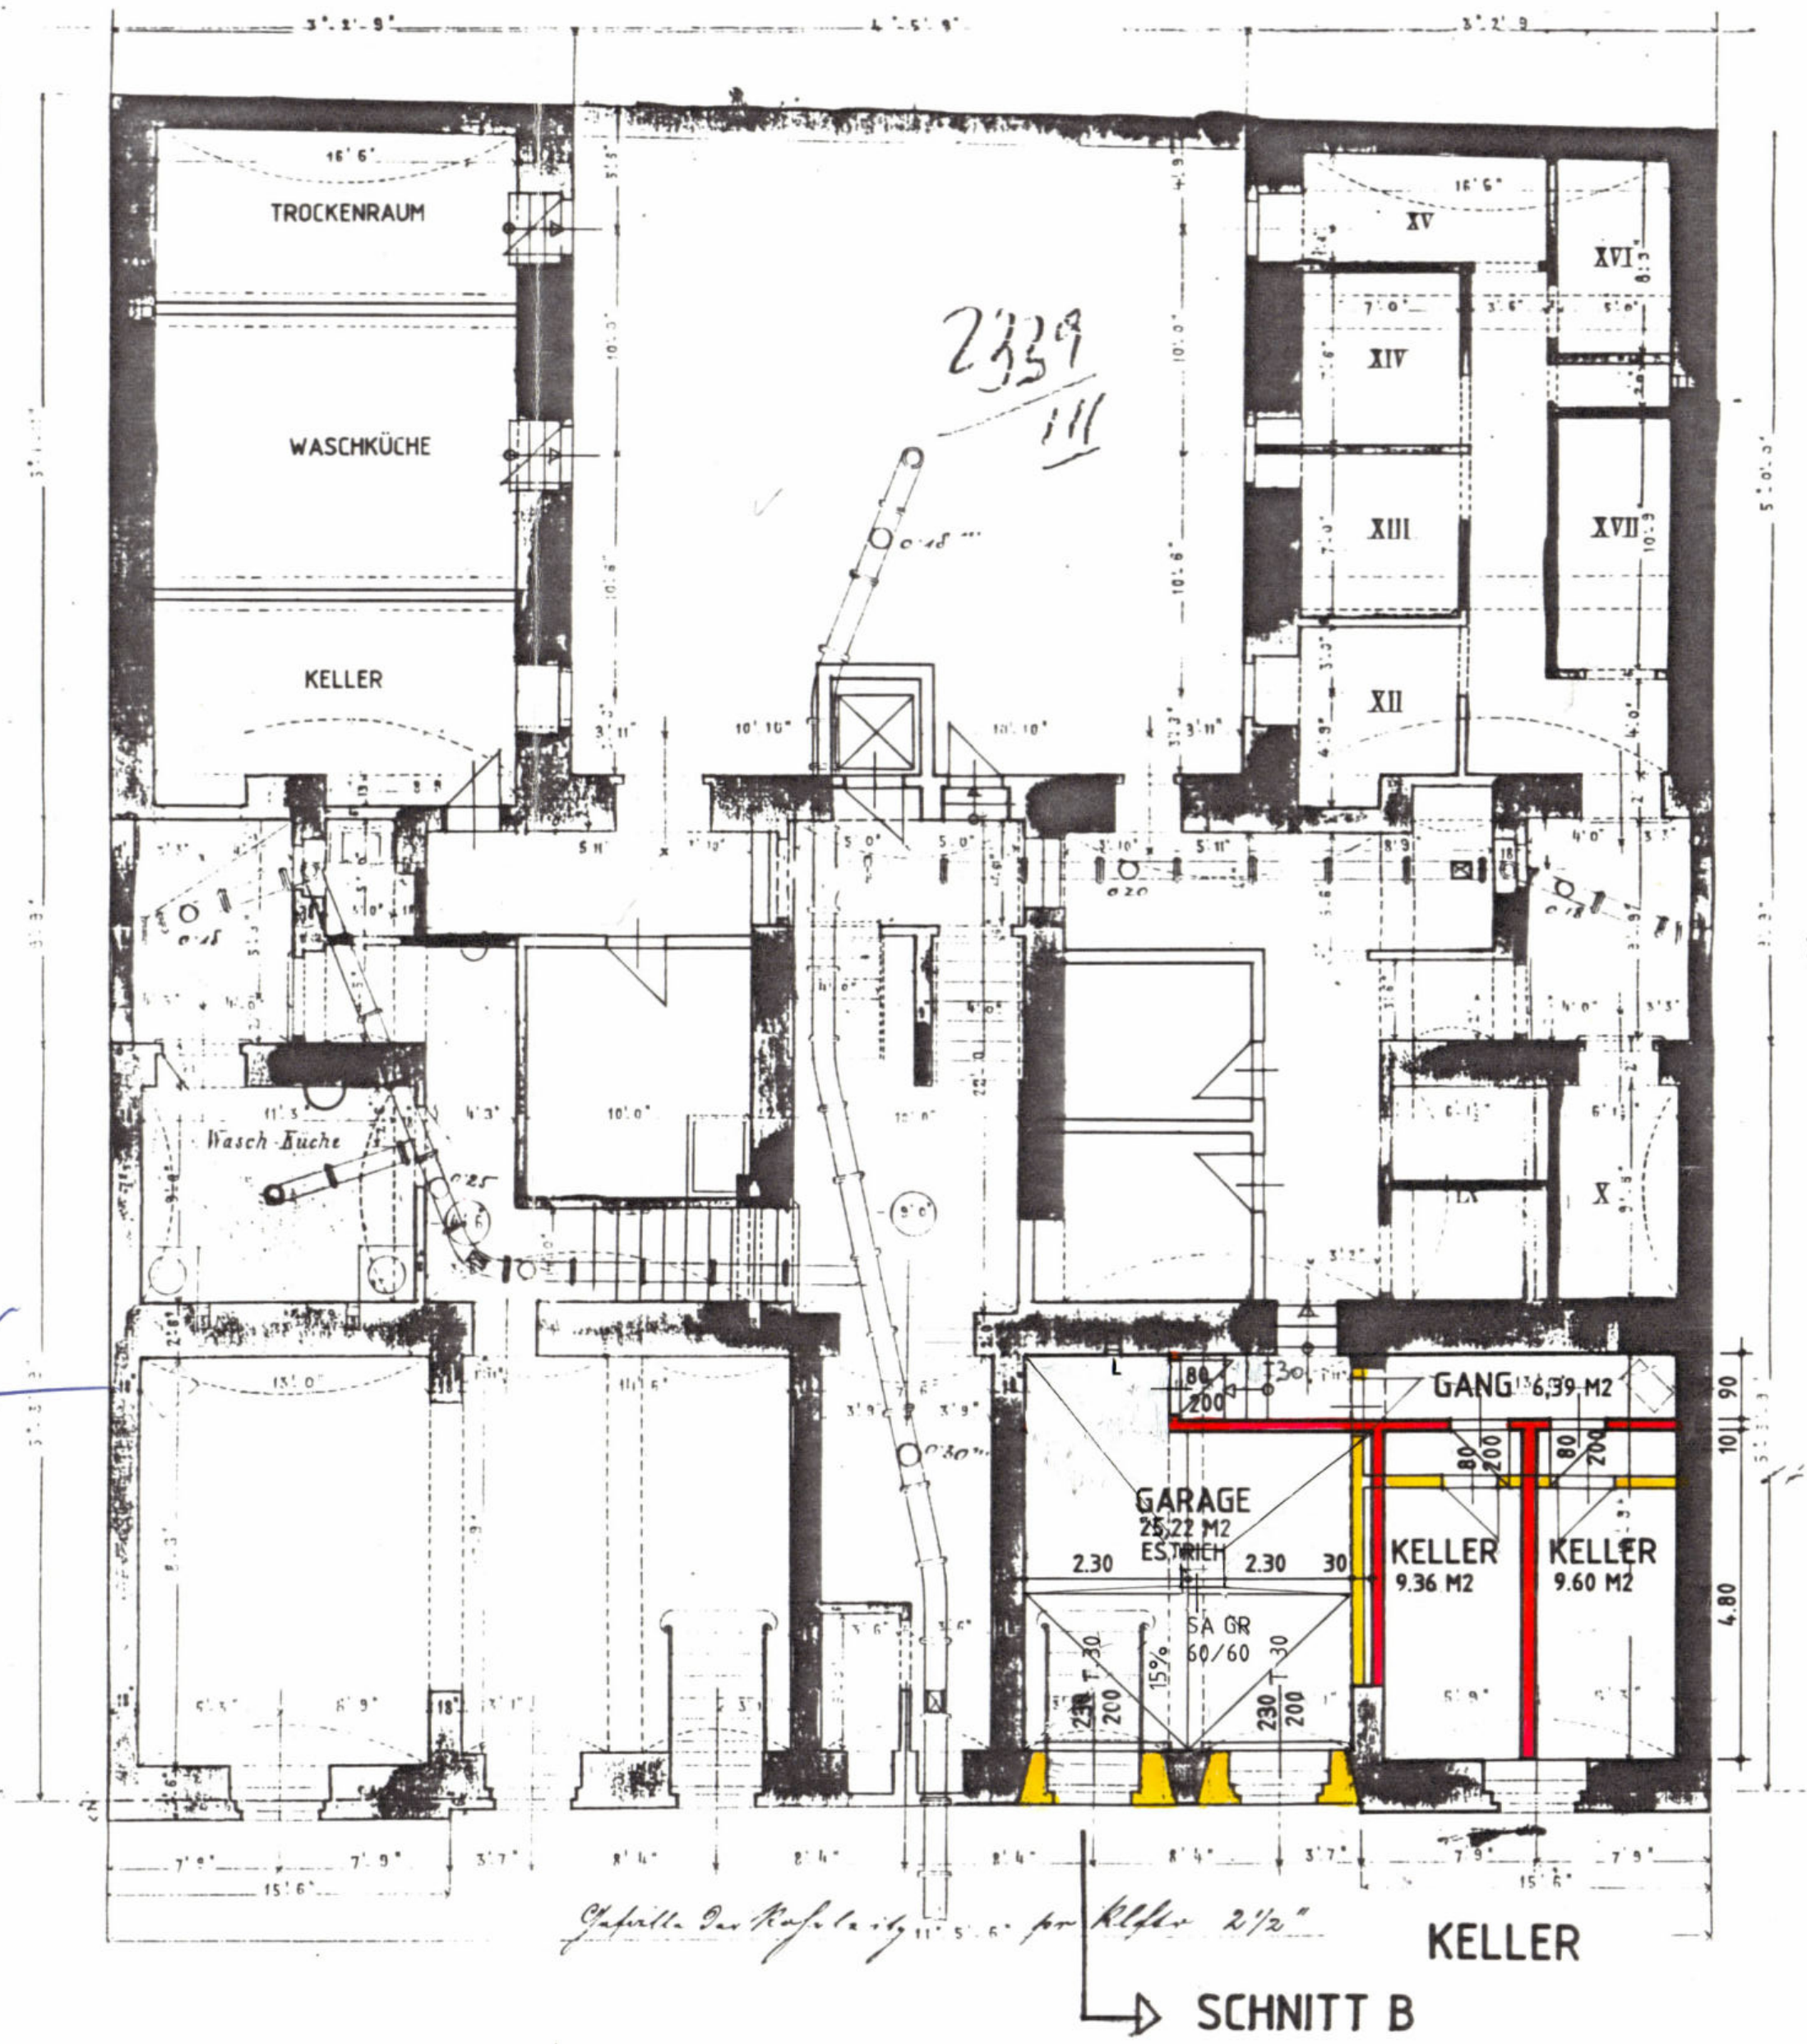

KELLER