




SCHNITT A-B
M 1:50

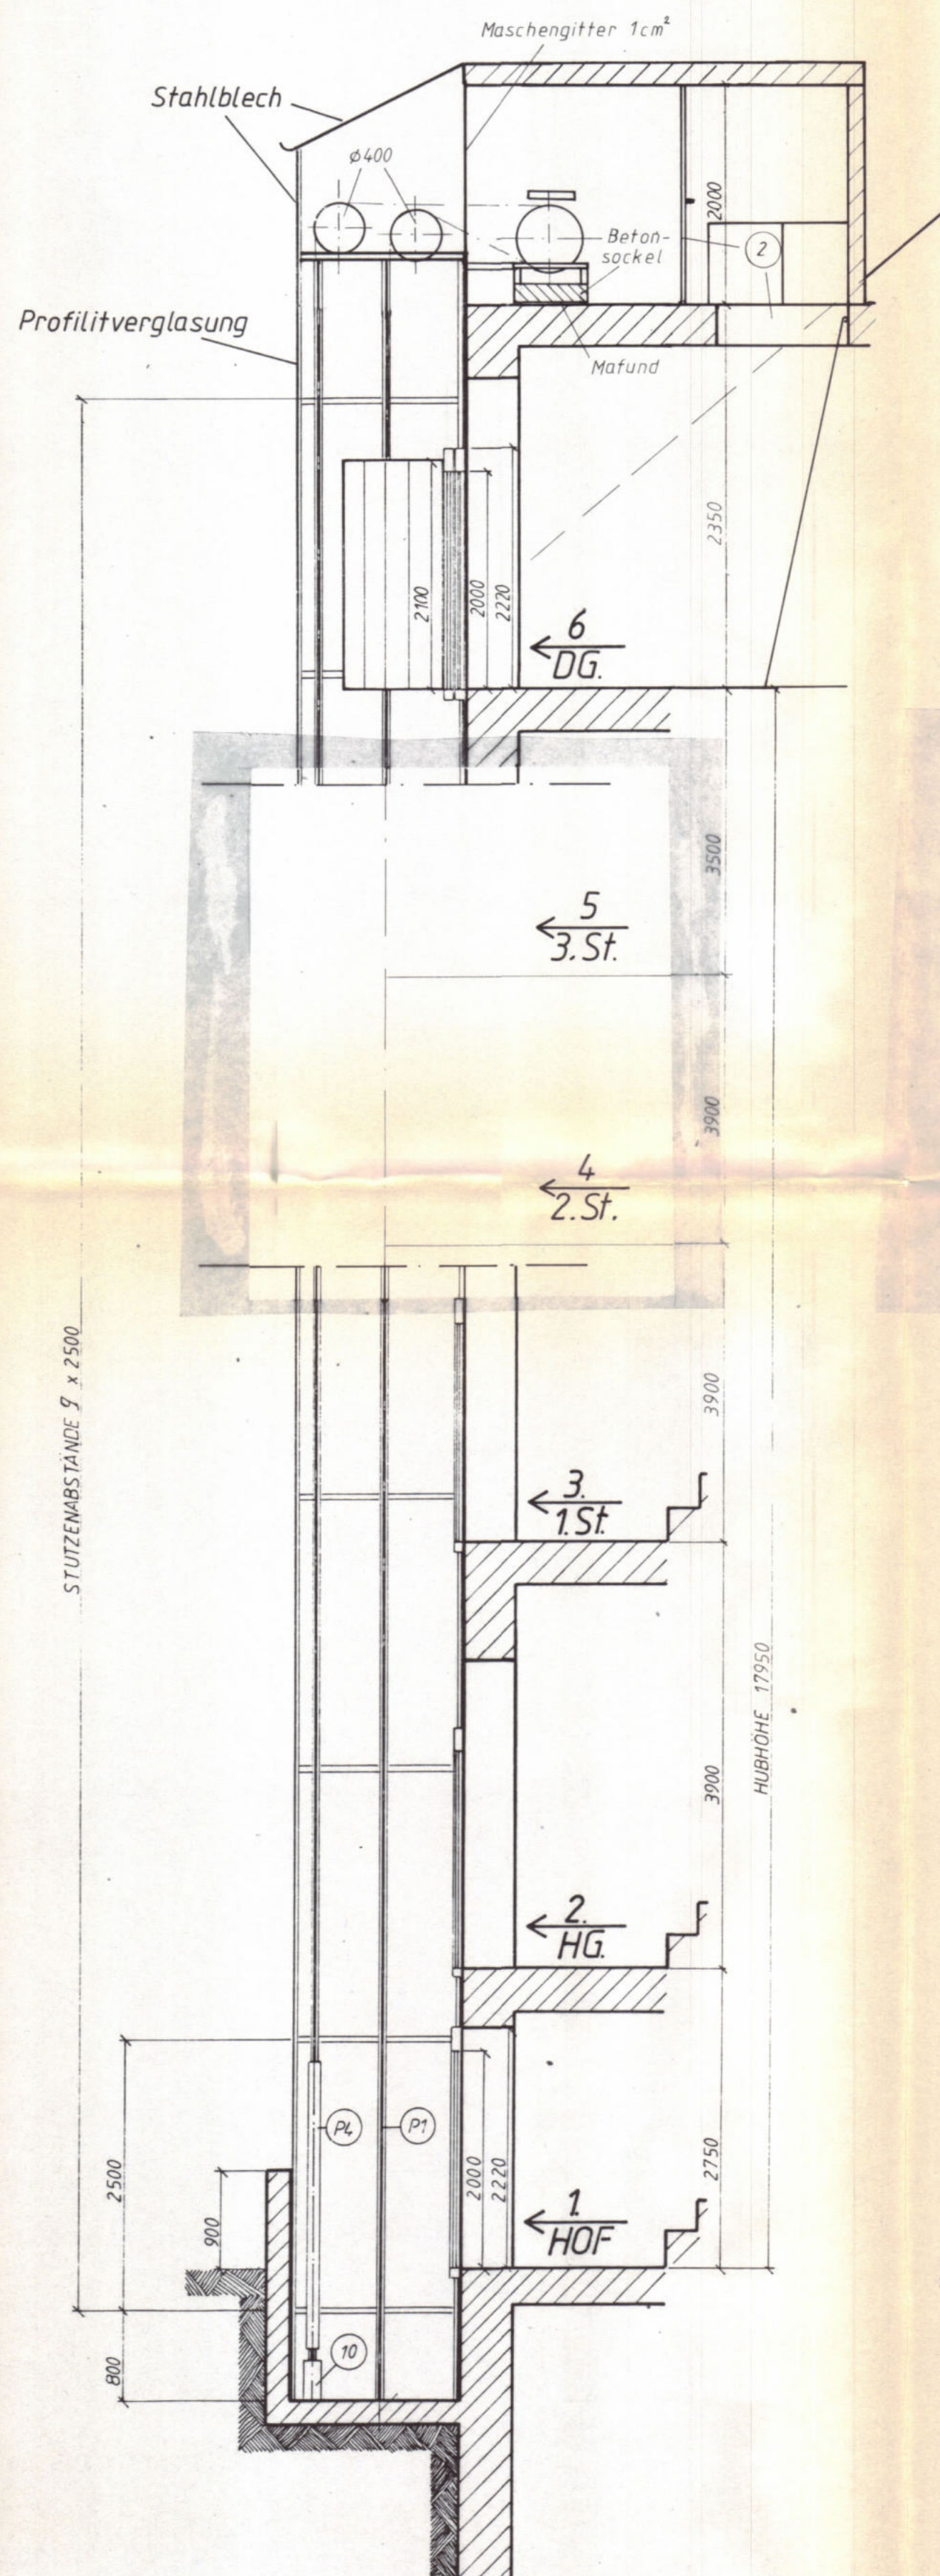


SCHNITT C-D
M 1:50

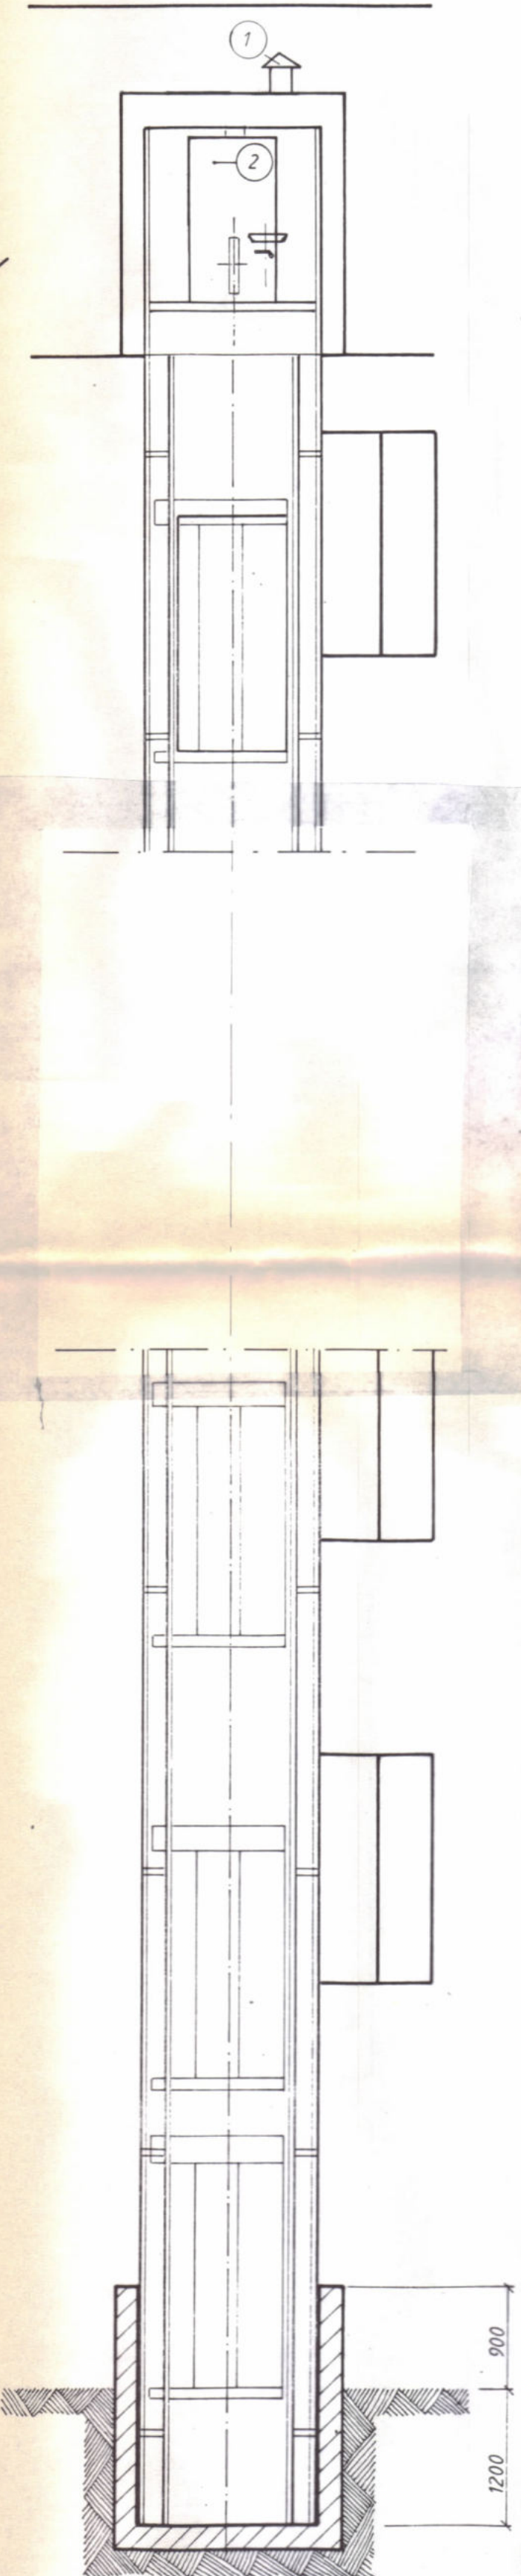


SCHACHTGRUNDRISS
M 1:20

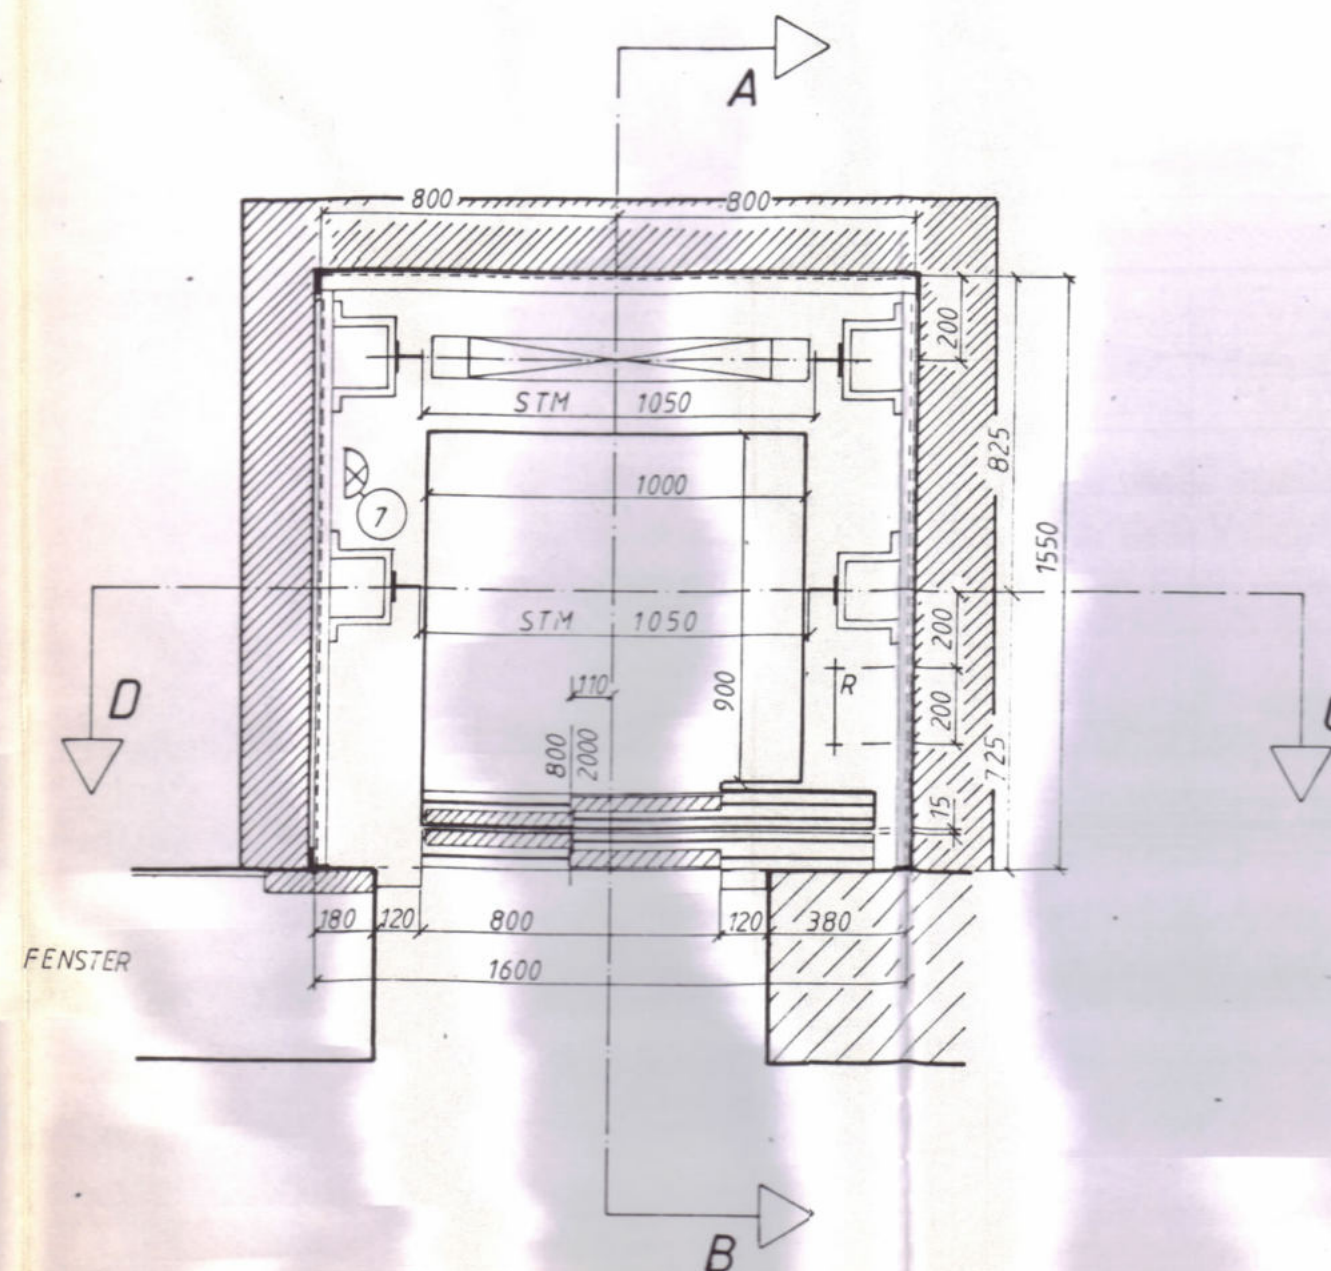

TWR-GRUNDRISS
M 1:25 ZUGANG ÜBER DACHBODEN

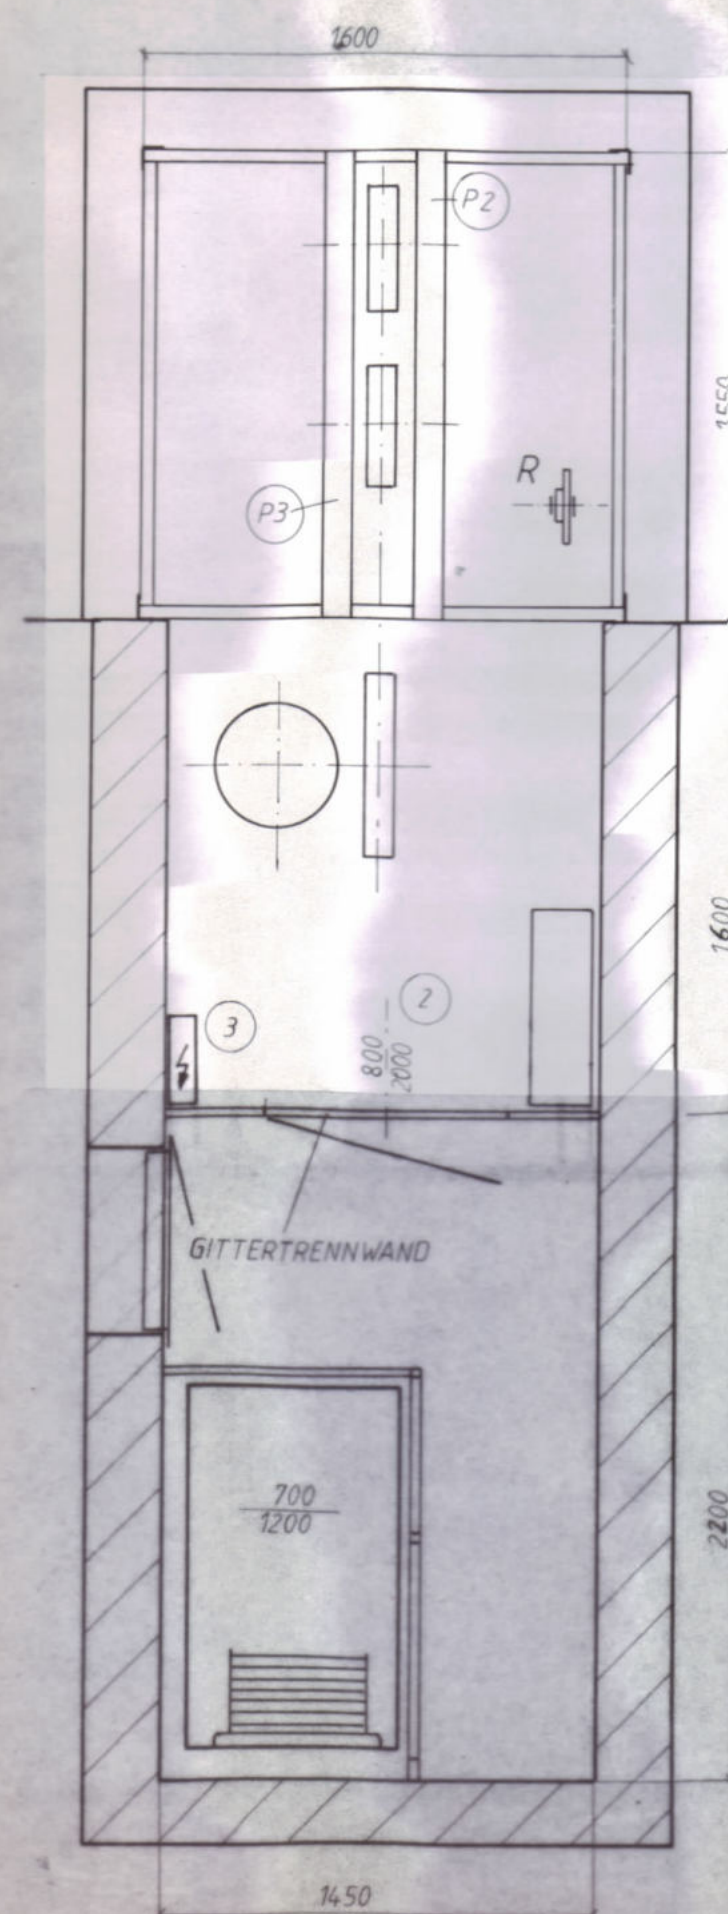

LAGEPLAN

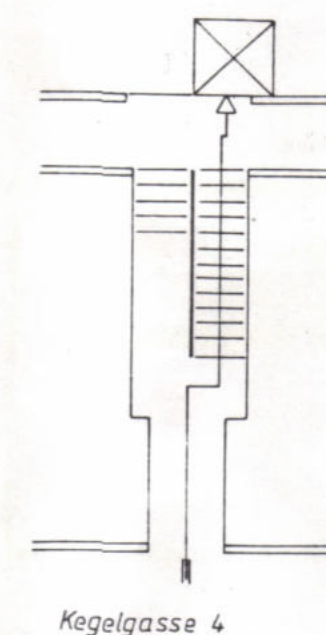

EINRICHTUNGEN UND BAUSEITIGE VORKEHRUNGEN		
1	Ständig wirkende Be- u. Entlüftung ins Freie min. 300 cm ² , im Triebwerksraum, bemessen für abzuführende Wärmemenge v. kJ/h, dabei Raumtemperatur min.+10°C max. +35°C, -min.+15°C max.+ 30°C.	
2	Versperbare eiserne PWT-Türe bzw. ausbalancierte Eisenabdeckung.	
3	Stromzuleitung laut NORM (Informationsblatt)	
4	Geländer, selbstschließender Schranken, Sicherheitskette	
5	Umkehrung laut (Informationsblatt) NORM.	
6	Podeste zwischen den Türen müssen dauerhaft glatt sein (z.B. Hartputz mit Glanzstrich, Glas v. Vaborsky Aufzüge, GLEICHGERICHTE BAUGLITE.	
7	Schachtbeleuchtung laut ÖNORM (Informationsblatt).	
8	Handstärker (haken) DK 50 mm v. Triebwerksraumdecke Tragkraft 1 kN.	
9	Montageöffnung mit abschließbarer PWT Diffusorabdeckung	
10	Betonsockel laut Montageangaben	
11	Einstiebstreppenanbau mit Lieferfirma festlegen	
12	Leitwagnenmin. Eisenleiter	
13	Gittertrennwand (wagnenbar) 10mm M. 1,5mm Drahtstähle	
14	Schallschottung	
15	Stöfester Anstrich für Grube, Triebwerksraum, Installationenkäbe 150mm hoch	
16	Beputetes, bitumiertes Stahlrohr 81 bzw. wasserdicht.	
P	Betriebs- und Fanglasten incl. 30% Stoßzuschlag ohne Eigengewicht von Betonsockeln, Decken, Hauptträgern usw.	
P1 13 kN P2 8,8 kN P3 8,8 kN P4 9 kN P5 — kN P6 — kN P7 — kN P8 — kN H1 — kN H2 — kN Horizontalkräfte bei jeder Stützenreihe wirkend		
UNTERSCHRIFT		ANSCHRIFT
DER BAUWERBER	<i>Hannelore Schwanzer</i>	1010 WIEN, JOSEFPLATZ 6
DER GRUND- UND HAUSEIGENTÜMER	<i>W. W. W. W.</i>	1010 WIEN, JOSEFPLATZ 6
DER PLANVERFASSER UND AUFZUGERBAUER	<i>T. Taborsky</i>	H. TABORSKY-AUFZÜGE OHG. 1100 WIEN, LEEBGASSE 80 TEL. 604 47 37 - 604 87 49
DER BAUFÜHRER FÜR DIE BAUMEISTERARBEITEN	E. SATLER Bauplanung m. b. H. Kegelgasse 57 1234 Wien, 69 49 81 Fax 69 49 85	
DER GRUNDEIGENTÜMER		
Art des Aufzuges: PERSONENAUFZUG		H. TABORSKY-AUFZÜGE
Auftraggeber: Fr. Mag. Hannelore Schwanzer 1010 Wien, Josefplatz 6		1100-WIEN LEEBGASSE 80
Aufstellungsort: 1030-Wien, Kegelgasse 4		Zeichnungsanz: 212
M. 1:20	Tragkraft: 320 kp oder 4 Personen	TAG Name 10.03.88
1:50	Hubhöhe: 12,95 m Halt: 6	25.11.91
1:100	V _m 0,8/0,2 Motorleistung	1:100
	DK-Rufsystem elektronik	Fabr. Nr.: 212