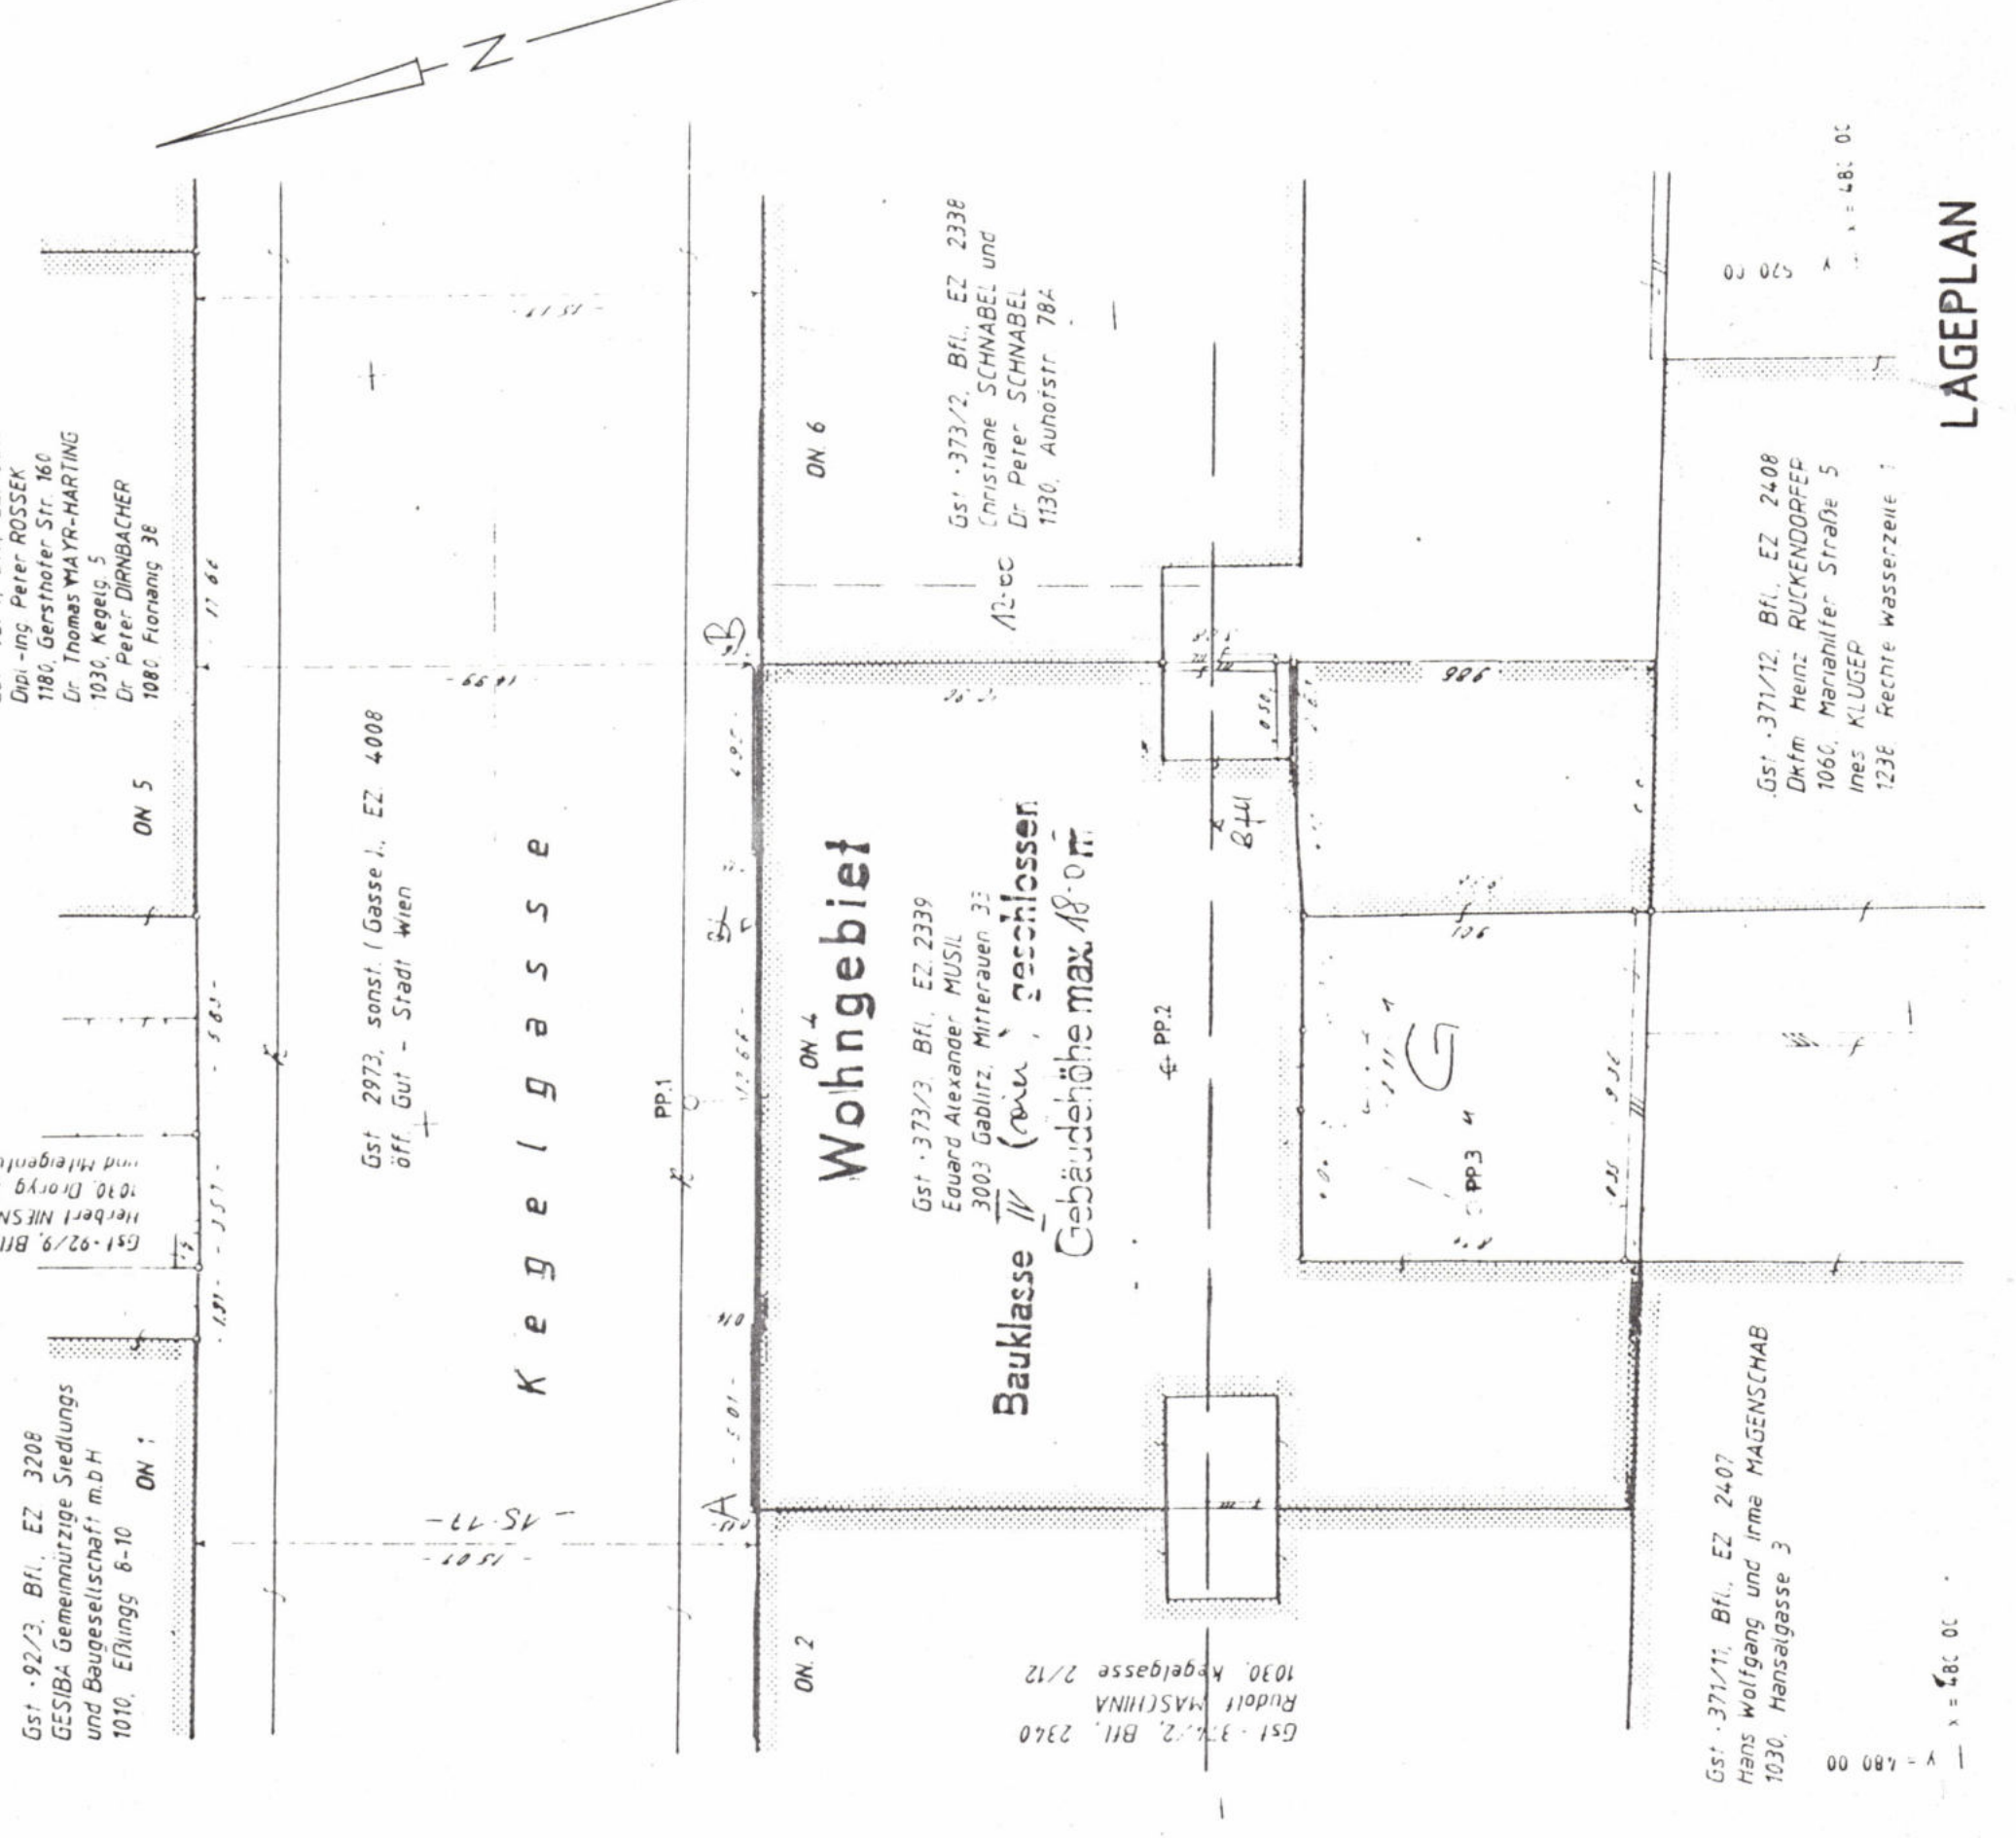


KONSTRUKTION

- ① AUSSENWÄNDE
- 150 cm GK - PLATTEN
 - 150-150 cm ZIEGELHAUWERK
 - AUSSENPUTZ
- ② DACHAUFBAU
- DACHREGEL
 - 300 cm KONSTRUKTION
 - DACHPAPE
 - 250 cm SCHÜLUNG
 - 150 cm SPÄNEN
 - 300 cm 2x15 OFF-PLATTEN
 - BEI GAUBEN BLENDENKUNDE
 - 125 cm GK - PLATTEN
 - 125 cm GK - PLATTEN
 - WÜRMSTRENNWAND ZWISCHUNG
- ③ ZWISCHENWÄNDE
- 125 cm GK - PLATTEN
 - 600 cm PROFILSTÄNDER - DAMPUNG
 - 125 cm GK - PLATTEN
 - WÜRMSTRENNWAND ZWISCHUNG
- ④ FUßBODENAUFBAU
- 100 cm BODENBELAG
 - 300 cm BRANDSCHUTZPLATTEN
 - 200 cm STUKATUR, PUTZ
 - BRANDSCHUTZDECKE
 - BRANDSCHUTZDECKE
- ⑤ MASSAUFBAU
- 100 cm FLESEN
 - 100 cm F - ISOLIERUNG
 - 600 cm ESTRICH
 - 150 cm WÄRMEDÄMMUNG
 - 150 cm STB - DECKE
- ⑥ ZWISCHENDECKE
- 100 cm BODENBELAG
 - 200 cm SPARKLATEN
 - 800 cm STAPFELKONSTRUKTION
 - 150 cm GK - PLATTEN
- ⑦ TERRASSEN- / DACHAUFBAU
- 500 cm BETONPLATTEN
 - 200 cm LAGER ELASTISCH
 - 800 cm PROFILATE
 - FEUCHTIGKEITSDAMPUNG 3-FACH
 - 500-1000 cm GEFÄLLEBETON
 - 200 cm STB - DECKE

Magistral der Stadt Wien
Magistralabteilung 37
Baupolizei

Hierauf bezieht sich der Bescheid
MA 37/13-1000/1468/12
Wien, 15. April 1993
Für den Abgabenden:

AUSWECHSLUNGSPLAN
FÜR DEN DACHGESCHOSSAUSBAU
1030 WIEN, KEGELGASSE 4
GST Nr 373/3, EZ 2339, KG. LANDSTR.
M 1:100
WIEN, AUGUST 1993

- LEGENDE
- ABBRUCH
 - BESTAND
 - STÄHLBETON
 - ZIEGEL
 - TRAGENDE STAHL U. HOLZKONSTRUKTIONEN F 60
 - ZWISCHENWÄNDE, GK - STÄNDERKONSTRUKTION


FRITZL & PARTNER GmbH
1030 WIEN, BAUGASSE 3
1330 55 84 Seite
1330 55 84 Seite
1330 55 84 Seite

GRUNDEIGENTÜMER:


BAUWERBER:

BAUFÜHRER:


E. SATLER
Bauplanungsamt
1030 WIEN, BAUGASSE 3
1330 55 84 Seite

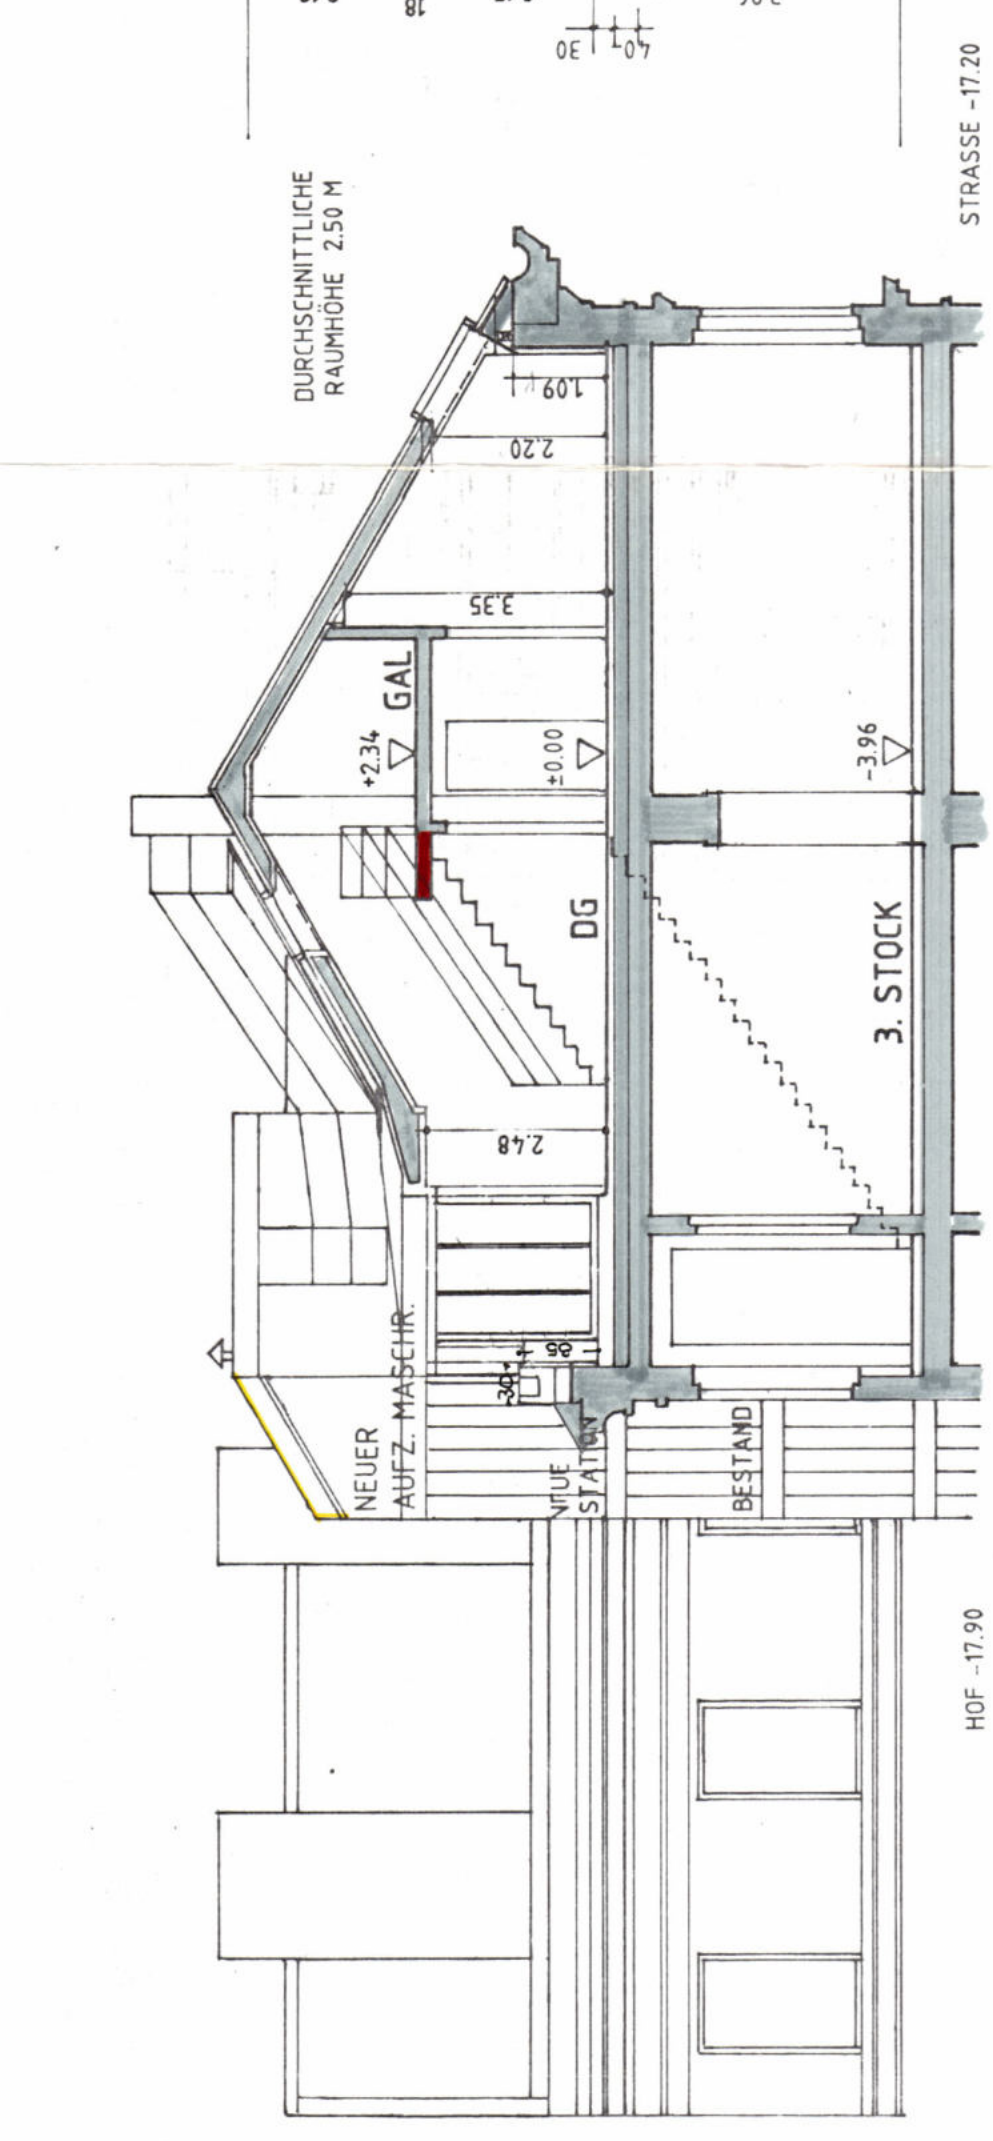


SCHNITT A-A

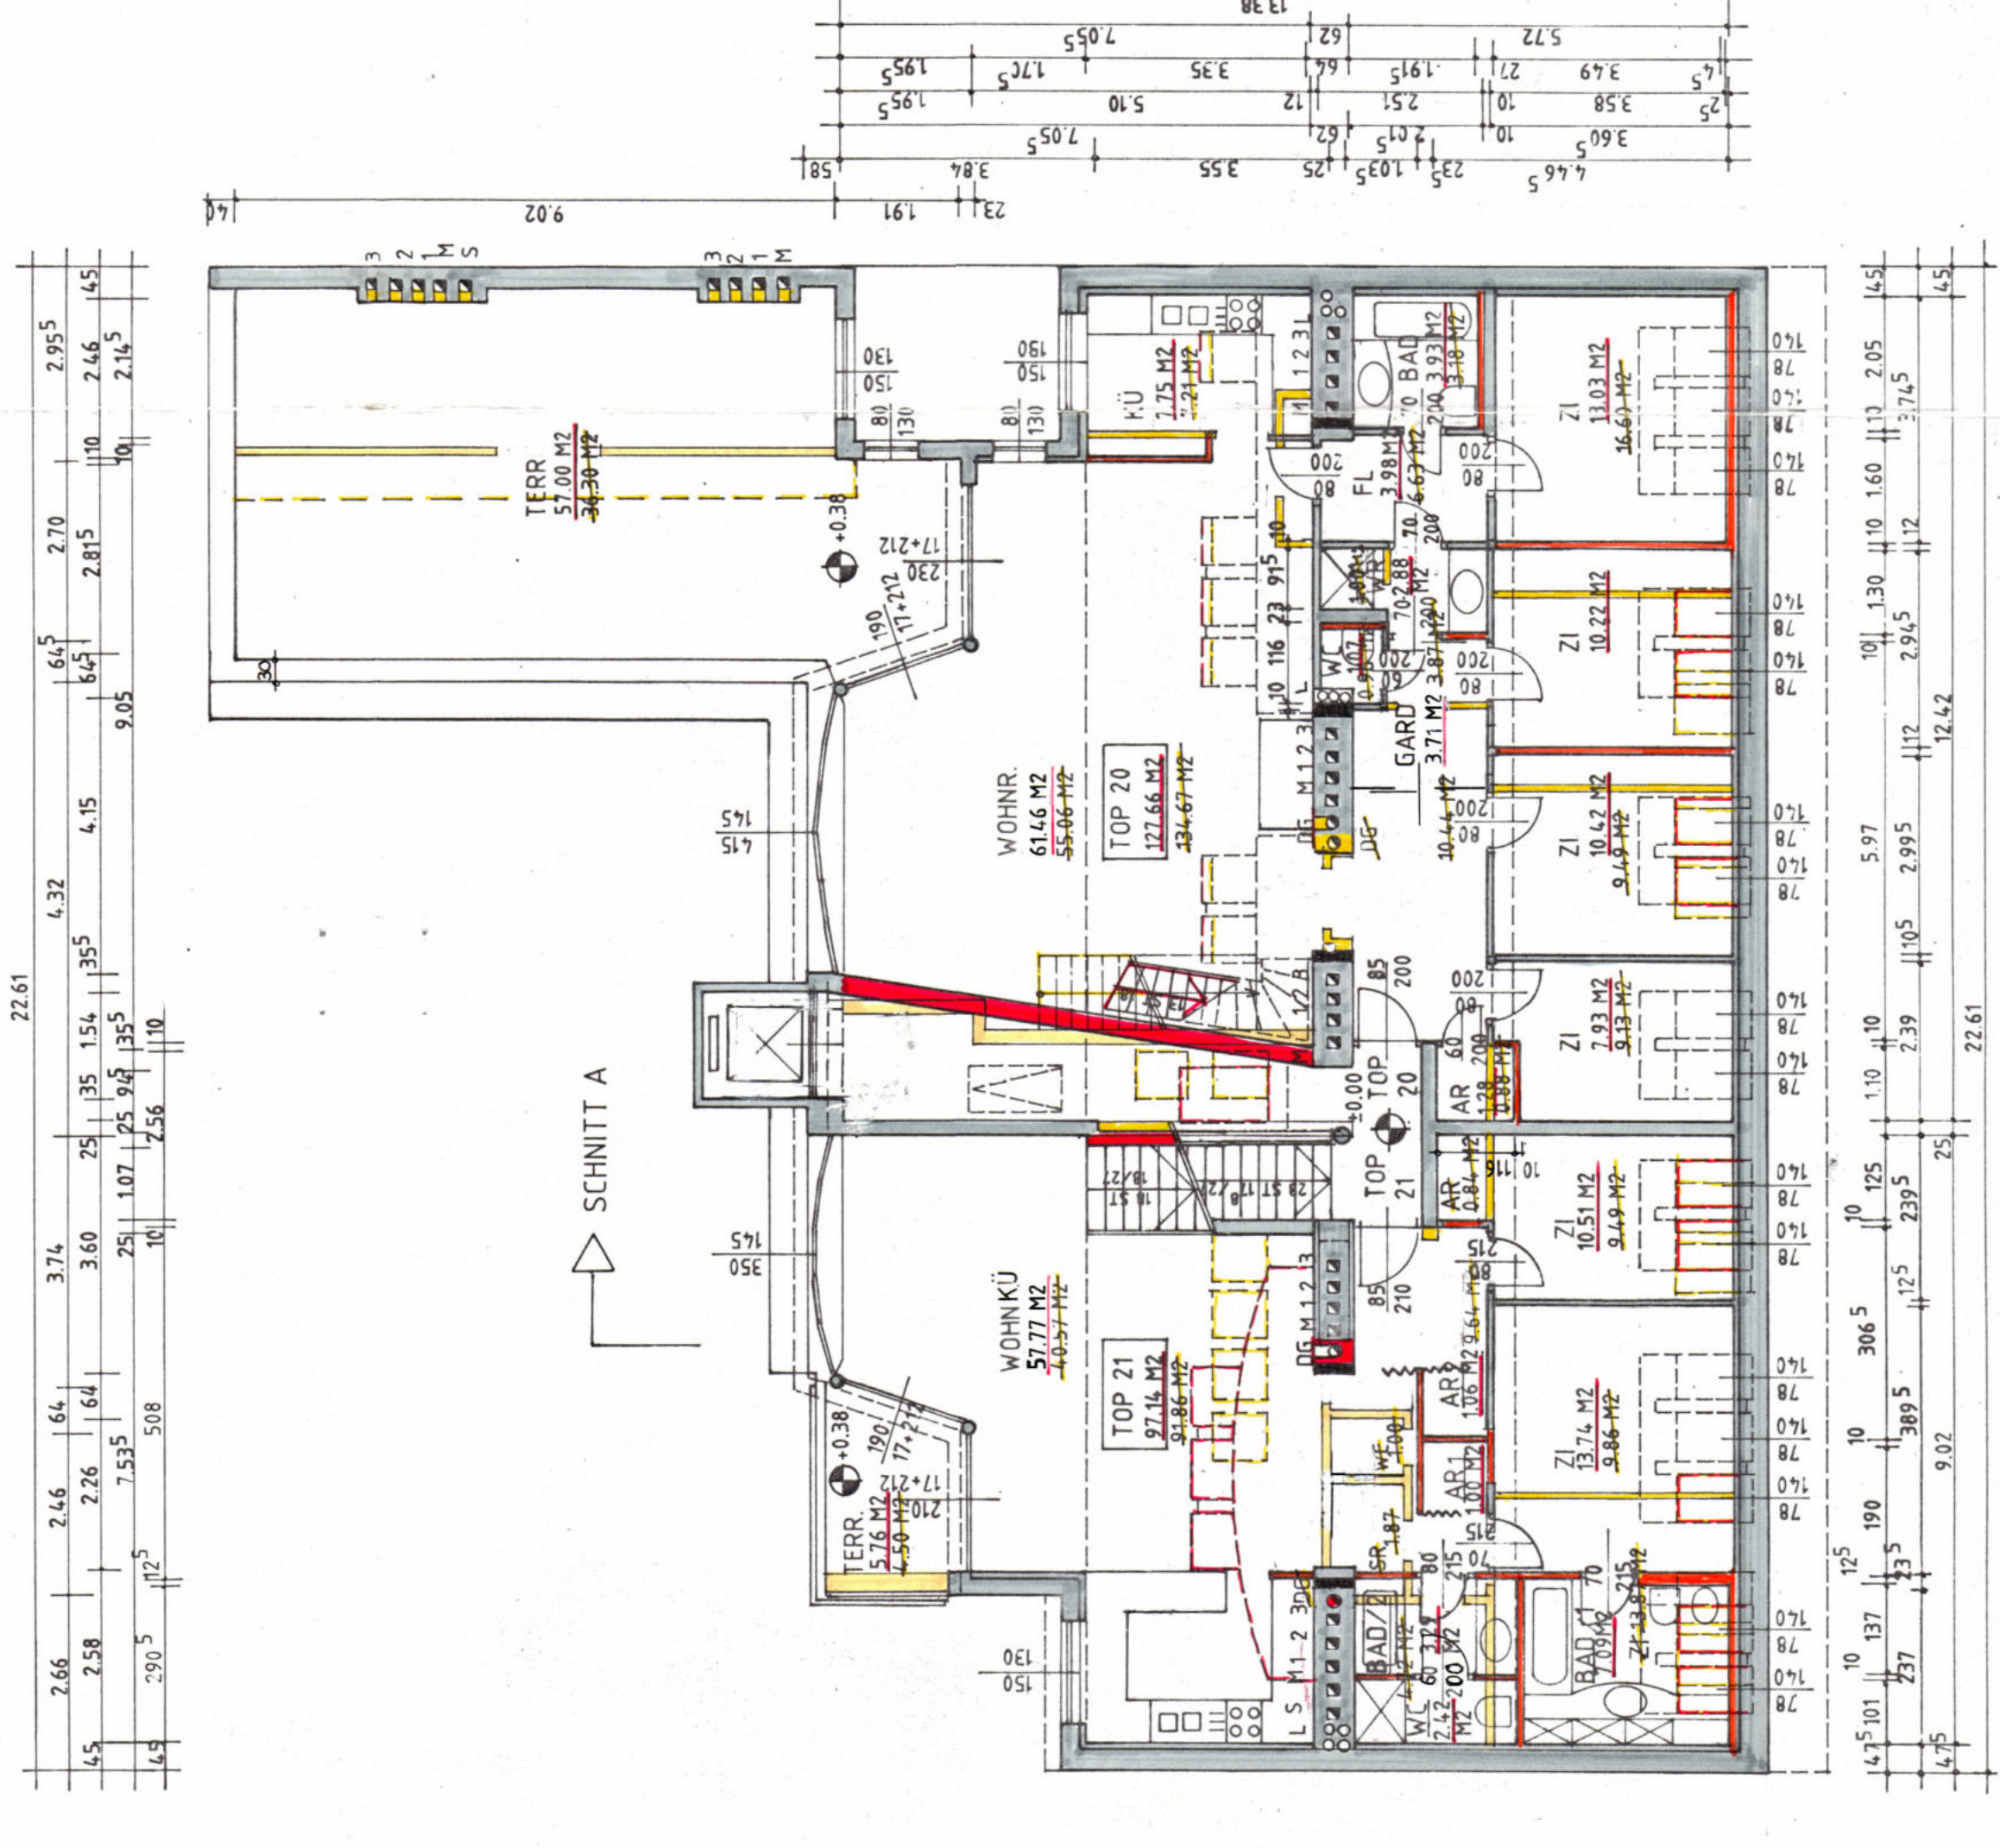

DACHGESCHOSS

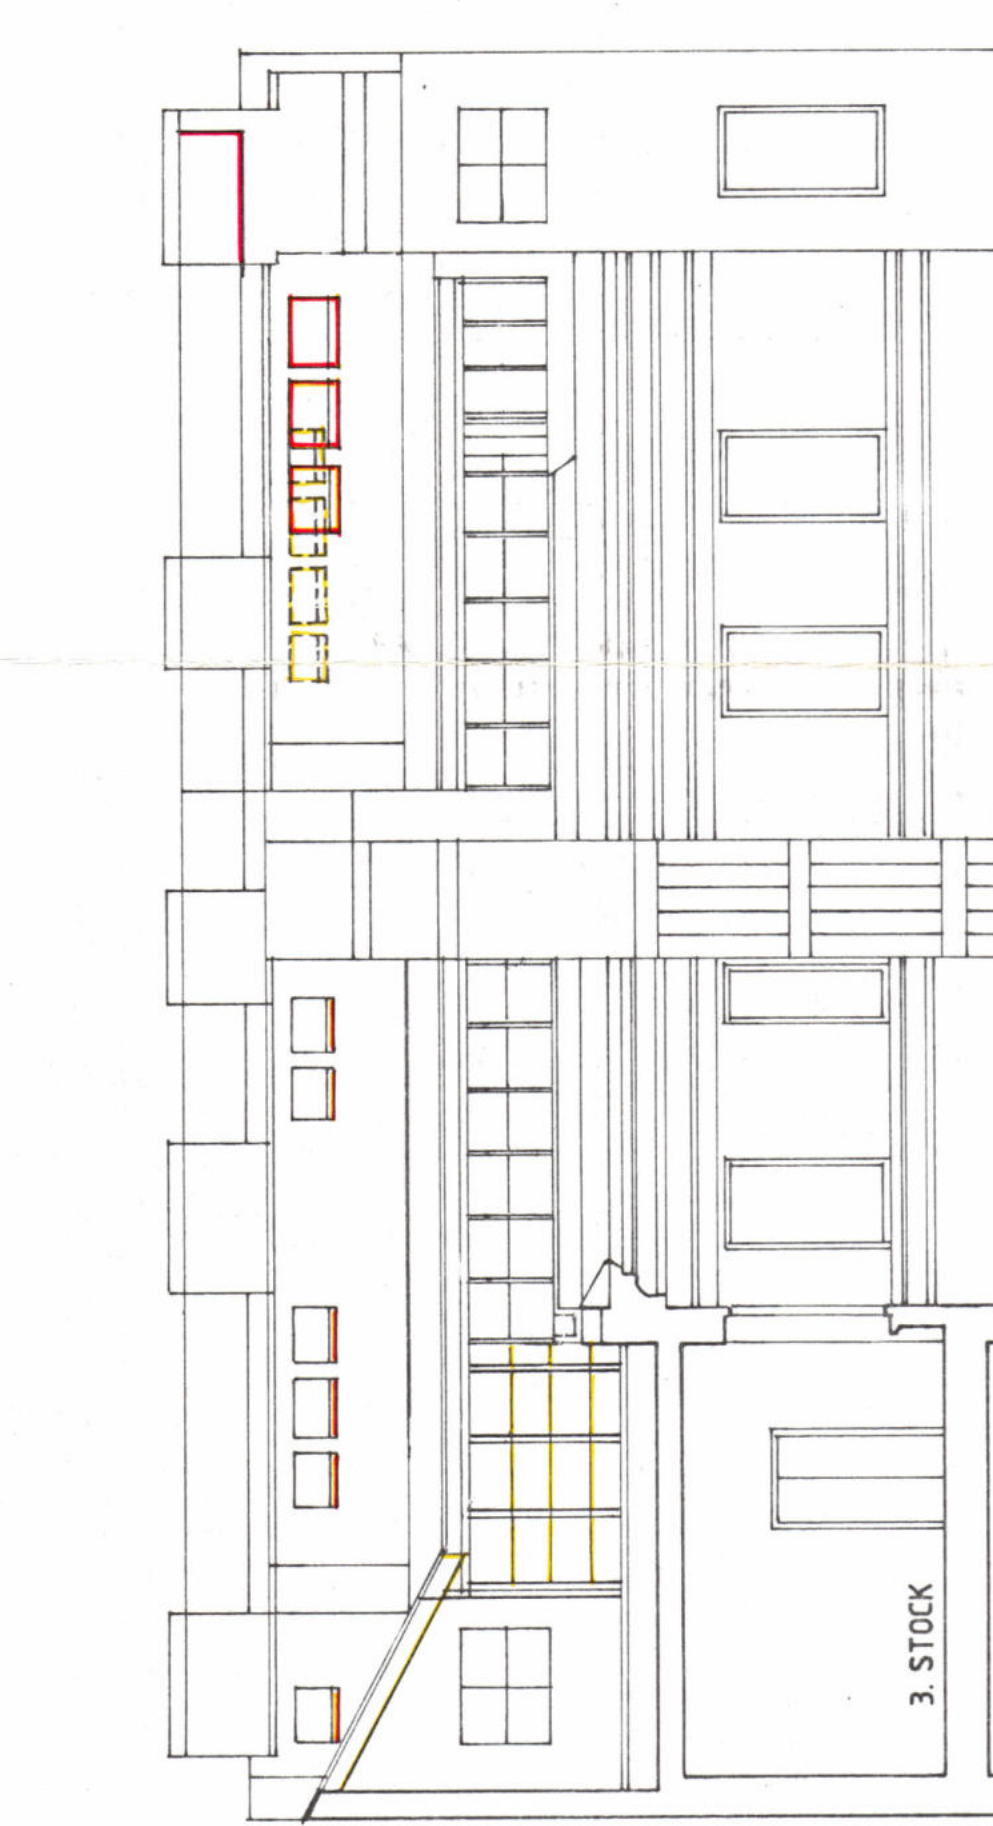


HOFANSICHT

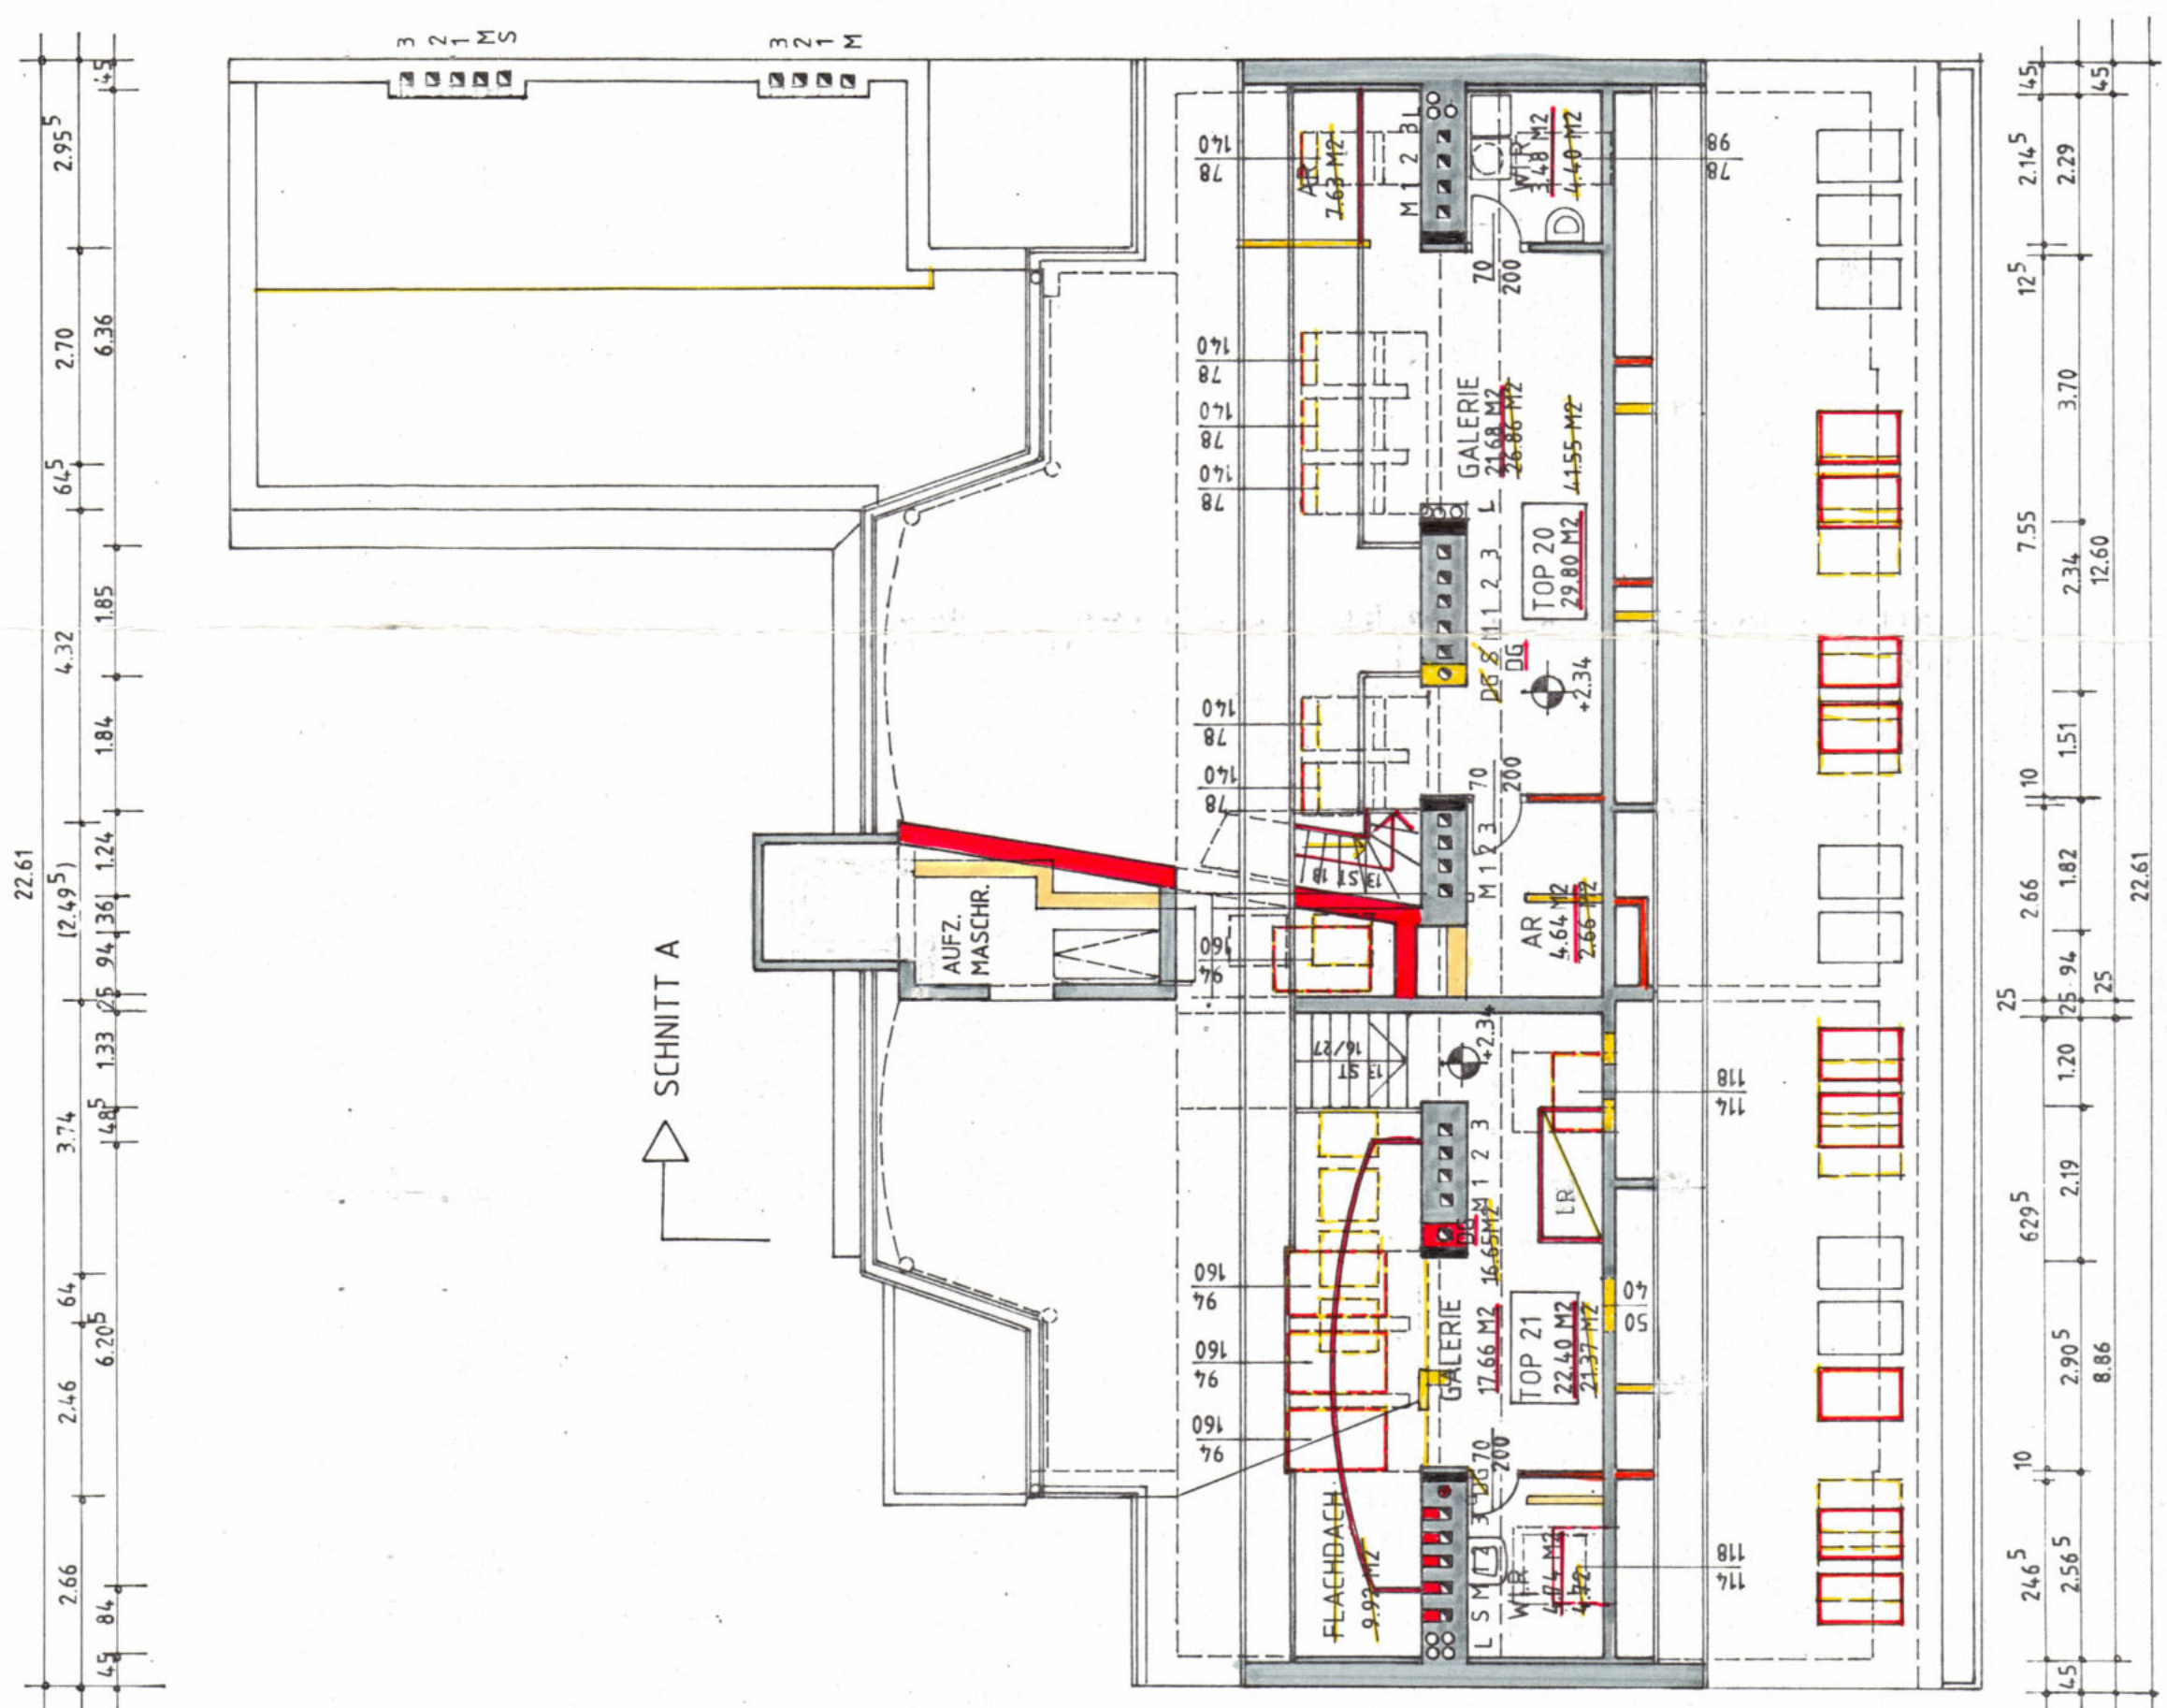

DACHGESCHOSS



STRASSENANSICHT

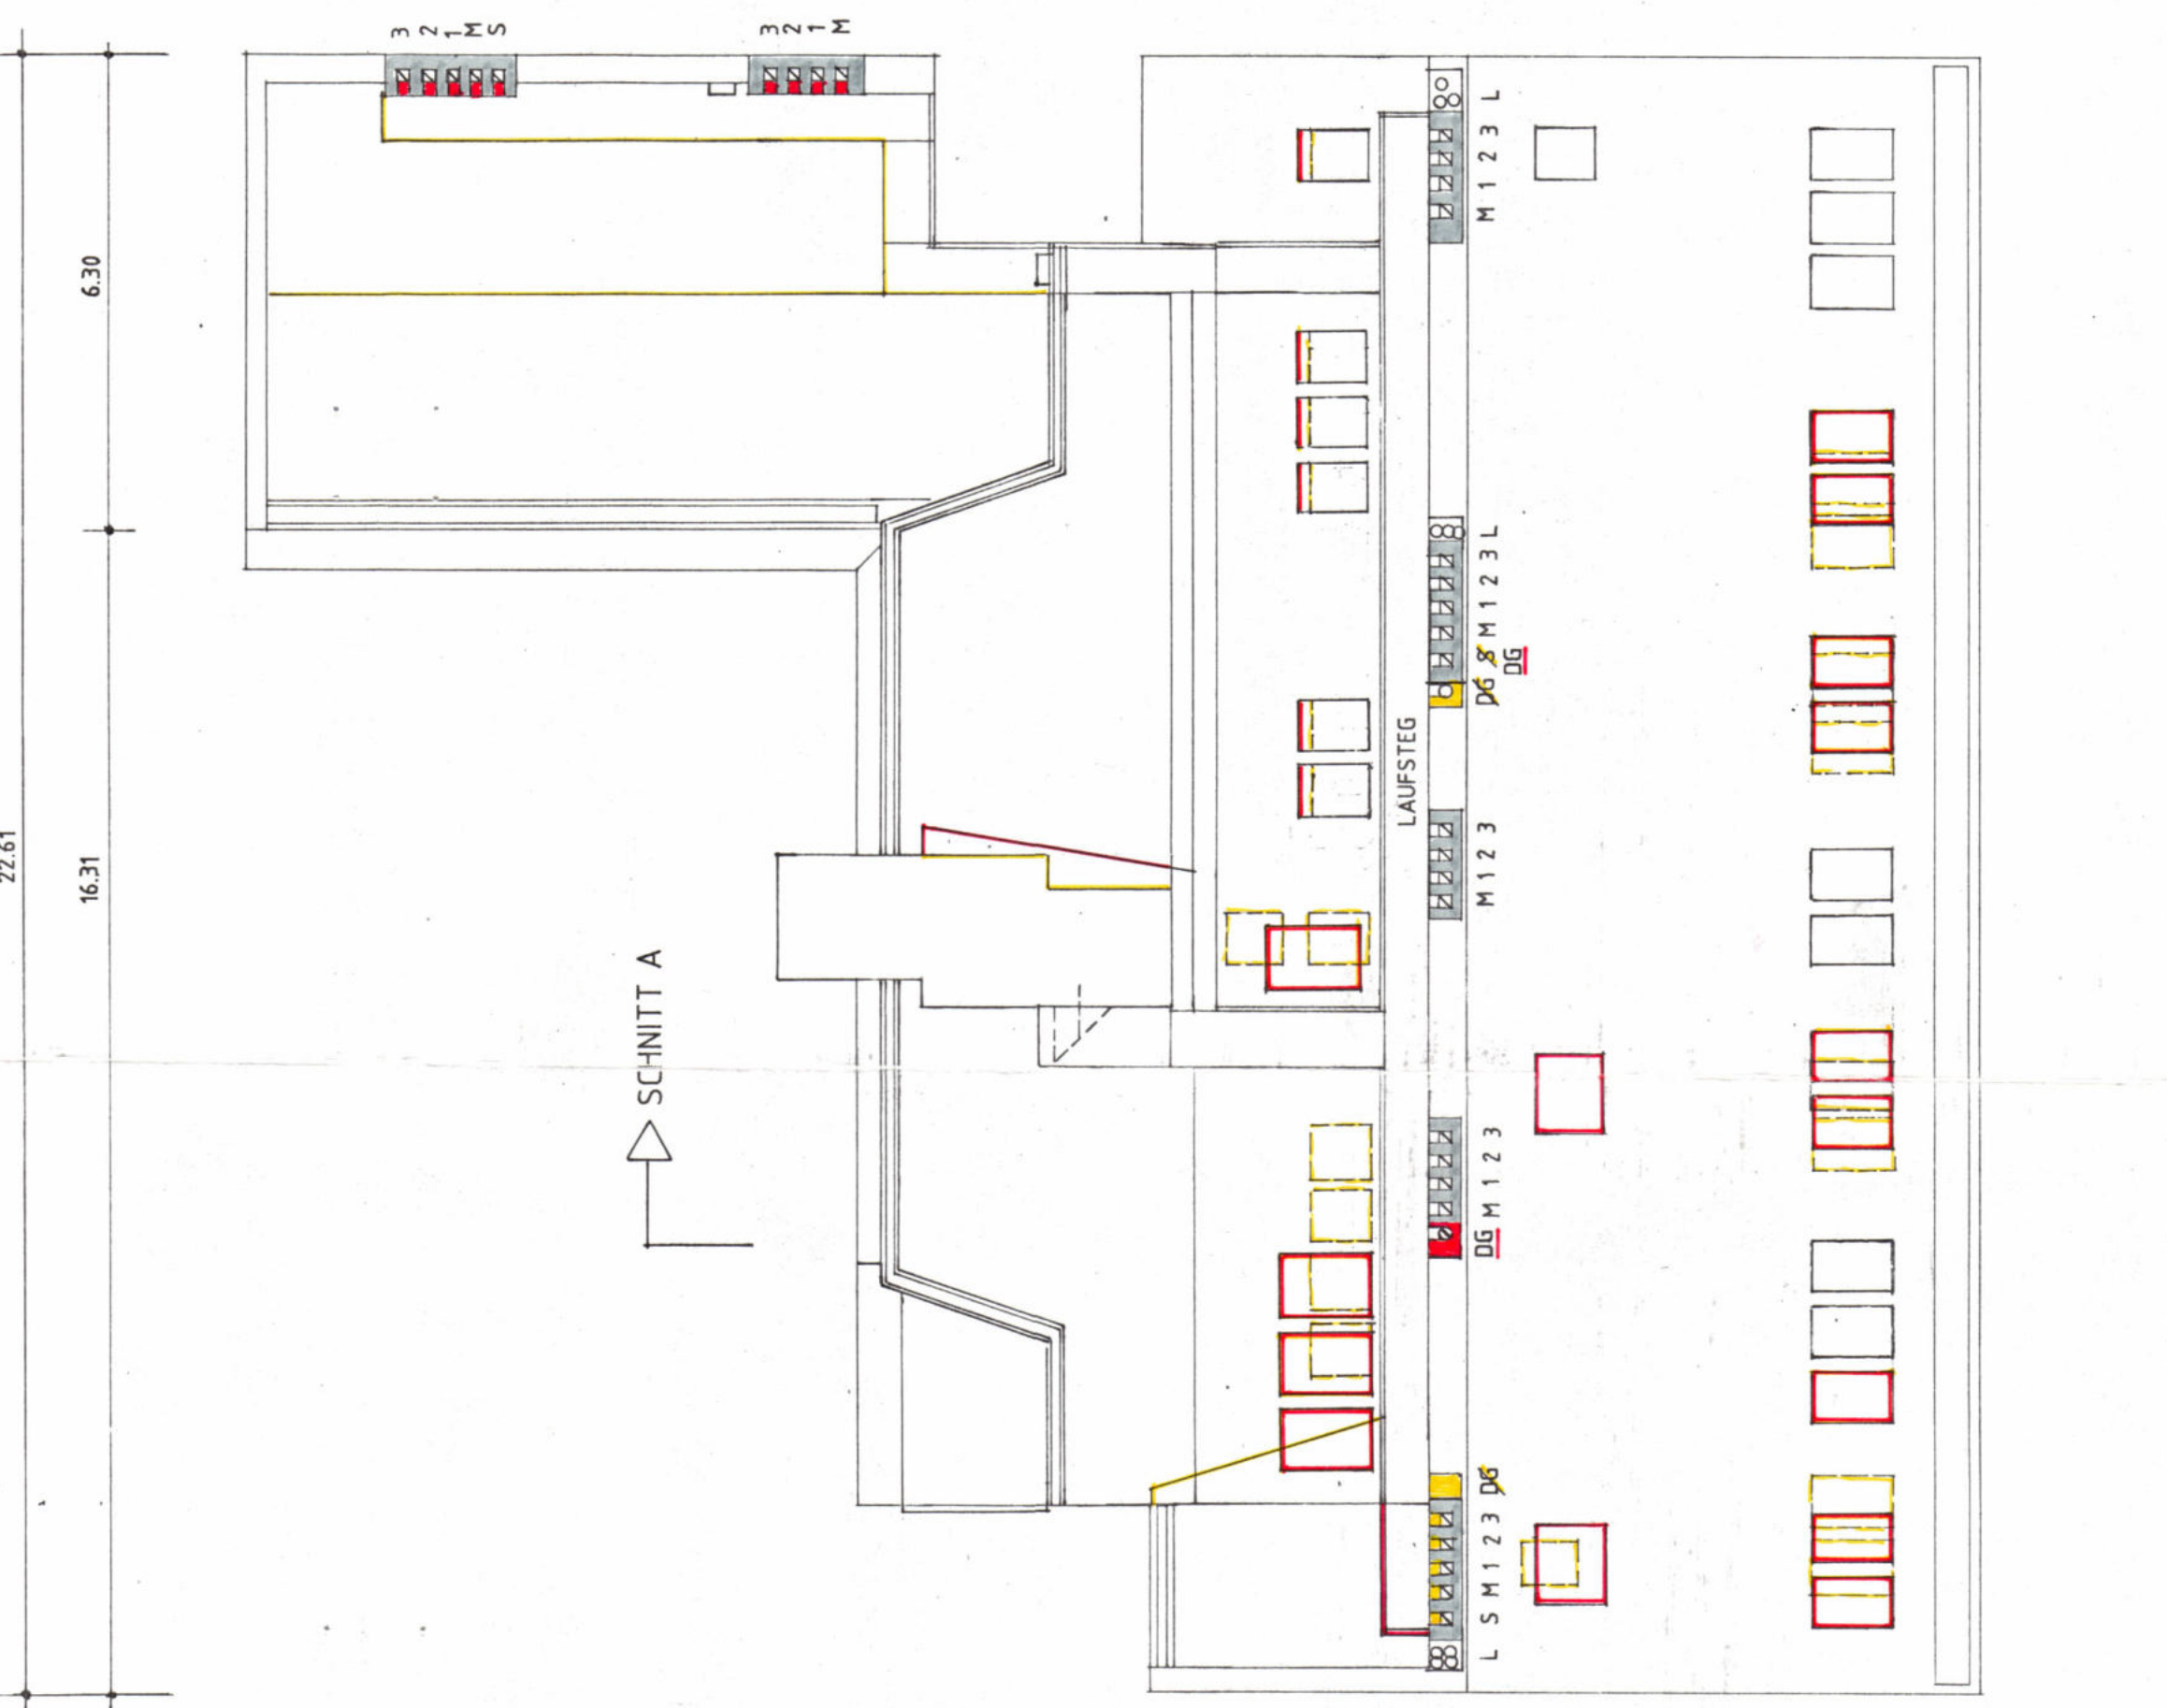

DACHGESCHOSS