

6
1-2

Magistrat der Stadt Wien
Stadtbauamt, Magistratsabteilung 36
Bau-, Feuer- u. Gewerbepolizei f. d. Bez. 1-9 u. 20
Im selbständigen Wirkungsbereiche.

M. Abt. 36 - 3., Kegelgasse 4
2/54

E. Z. 2339 Grdb. Landstraße

Planwechsel. Wien, am 26. Mai 1954.

30. Mai 1954
Plankammer zur Einlage E. Z. 2339
Abteilungsleiter:

B e s c h e i d

Auf Grund des durchgeführten Ermittlungsverfahrens wird nach dem mit dem Genehmigungsvermerk versehenen Plan gemäß § 70 der BO. für Wien, in Anwendung des § 86, Abs. 2a der BO. für Wien, in Verbindung mit § 6, Abs. 3 d. WWAG. vom 13.7.1951, LGB. 20/51, die Bewilligung erteilt, bei der mit der Baubewilligung vom 10.8.1953, M. Abt. 36 - 3., Kegelgasse 4 genehmigten Fundamentunterfangung auf der Liegenschaft E. Z. 2339 d. Grdb. Landstraße, 3., Kegelgasse 4, eine Änderung vorzunehmen, die darin besteht, daß das Gebäude nicht durch zwei getrennte Fundamentstreifen mit Überlagen, sondern durch einen 3.40 m breiten Stahlbetonstreifen unter der Straßenhauptmauer und der Mittelmauer unterfangen wird.

Gleichzeitig wird gemäß § 1 (1) des Gebrauchsgebührengesetzes vom 12. Dezember 1947. LGB. für Wien Nr. 4/1948 die Erlaubnis zum Gebrauch der in Verwaltung der Stadt Wien stehenden Verkehrsfläche bzw. des darüber befindlichen Luftraumes erteilt.

Die Bedingungen der Baubewilligung vom 10.8.1953, Zl. M. Abt. 36-3., Kegelgasse 4 bleiben vollinhaltlich aufrecht.

Zusätzlich wird bedungen:

Für die Erlaubnis zur Benützung der Verkehrsfläche bzw. des darüber befindlichen Luftraumes durch die Verbreiterung der Grundmauern im Ausmaß von 22.70 m² ist eine einmalige Gebrauchsgebühr von S 341.- zu entrichten.

Die Einzahlung der einmaligen Gebühr im Betrage von S 341.- hat binnen 8 Tagen nach Zustellung des Bescheides bei der Stadtkasse für den 3. Bezirk zu erfolgen.

B e g r ü n d u n g :

Der Berechnung der Gebühr liegen zu Grunde:

Für die Fundamentverbreiterung S 15.- gemäß Tarif A Post 1

Gegen diesen Bescheid ist das binnen 2 Wochen, hinsichtlich der Bemessung der Gebrauchsgebühr aber innerhalb eines Monats nach Zustellung schriftlich oder telegraphisch bei der M. Abt. 36, Wien, 17., Parhamerplatz 18 einzubringende Rechtsmittel zulässig. Das Rechtsmittel ist zu begründen und hat hinsichtlich der Zahlungsverpflichtung keine aufschiebende Wirkung. Das Rechtsmittel ist, wenn es sich gegen die Gebührenvorschrift richtet, mit einer S 2.- Taxmarke, sonst mit einem S 6.- Bundesstempel zu versehen.

OS 7dA M
Vermerk im Bau- und
Anlagenamt

25 110/53

Ergoht an:

- 1.) den Bauwerber und Hauseigentümer: Ferdinand Brauchbar, z.Hd.Herrn H.V. Hermann Streiff, Wien, 3., Fasengasse 20, mit Plan A und B und stat. Berechnung A.

In Abschrift an:

- 2.) den Bauführer: Herrn Bmstr. Ing. J. Tscherringer, Wien, 14., Breitenfurterstraße 37,
- 3.) die M.Abt. 36, mit Plan C und stat. Berechnung C,
- 4.) die M.Abt. 35 G,
- 5.) die M.Abt. 4 - Grundbesitzabgaben,
- 6.) die Finanzlandesdirektion für Wien, N.O. und Burgenland, Wirtschaftl. Inform.-Dienst, 3., Vordere Zollamtsstraße 7.

Für die Richtigkeit
der Ausfertigung.
Der Kanzleileiter:



Der Abteilungsleiter:

Dipl.Ing.Skolaut

Oberstadtbaurat.

M. Abt. 20
Plan- und Schriftenkammer
Vorgemerkt im Baubewilligungsbuch

22/011 28

M. Abt. 20
Plan- und Schriftenkammer
E.L. 2339 Bezirk III
Archivstück

6
2

Magistral der Stadt Wien
Magistratsabteilung 36
Bau-, Feuer- und Gewerbepolizei
Bezirke 1-9 u. 20

Genehmigt gemäß § 70 B. O.
M. Abt. 36 - 3.1. Kegelg. 4

Wien, am 26. Mai 88 2/88

Der Abteilungsleiter:

Korait



C

Magistratsabteilung 36
Magistratsabteilung 36
XVII, P. 18




Wien III. Kegelgasse 4
Auswechslungsplan

110/53

WIEN III, KEGELGASSE 4, E.Z. 2339 FUNDAMENTUNTERFANGUNG AVSWECHSLUNGSPLAN 1:100

SOUTERRAIN,

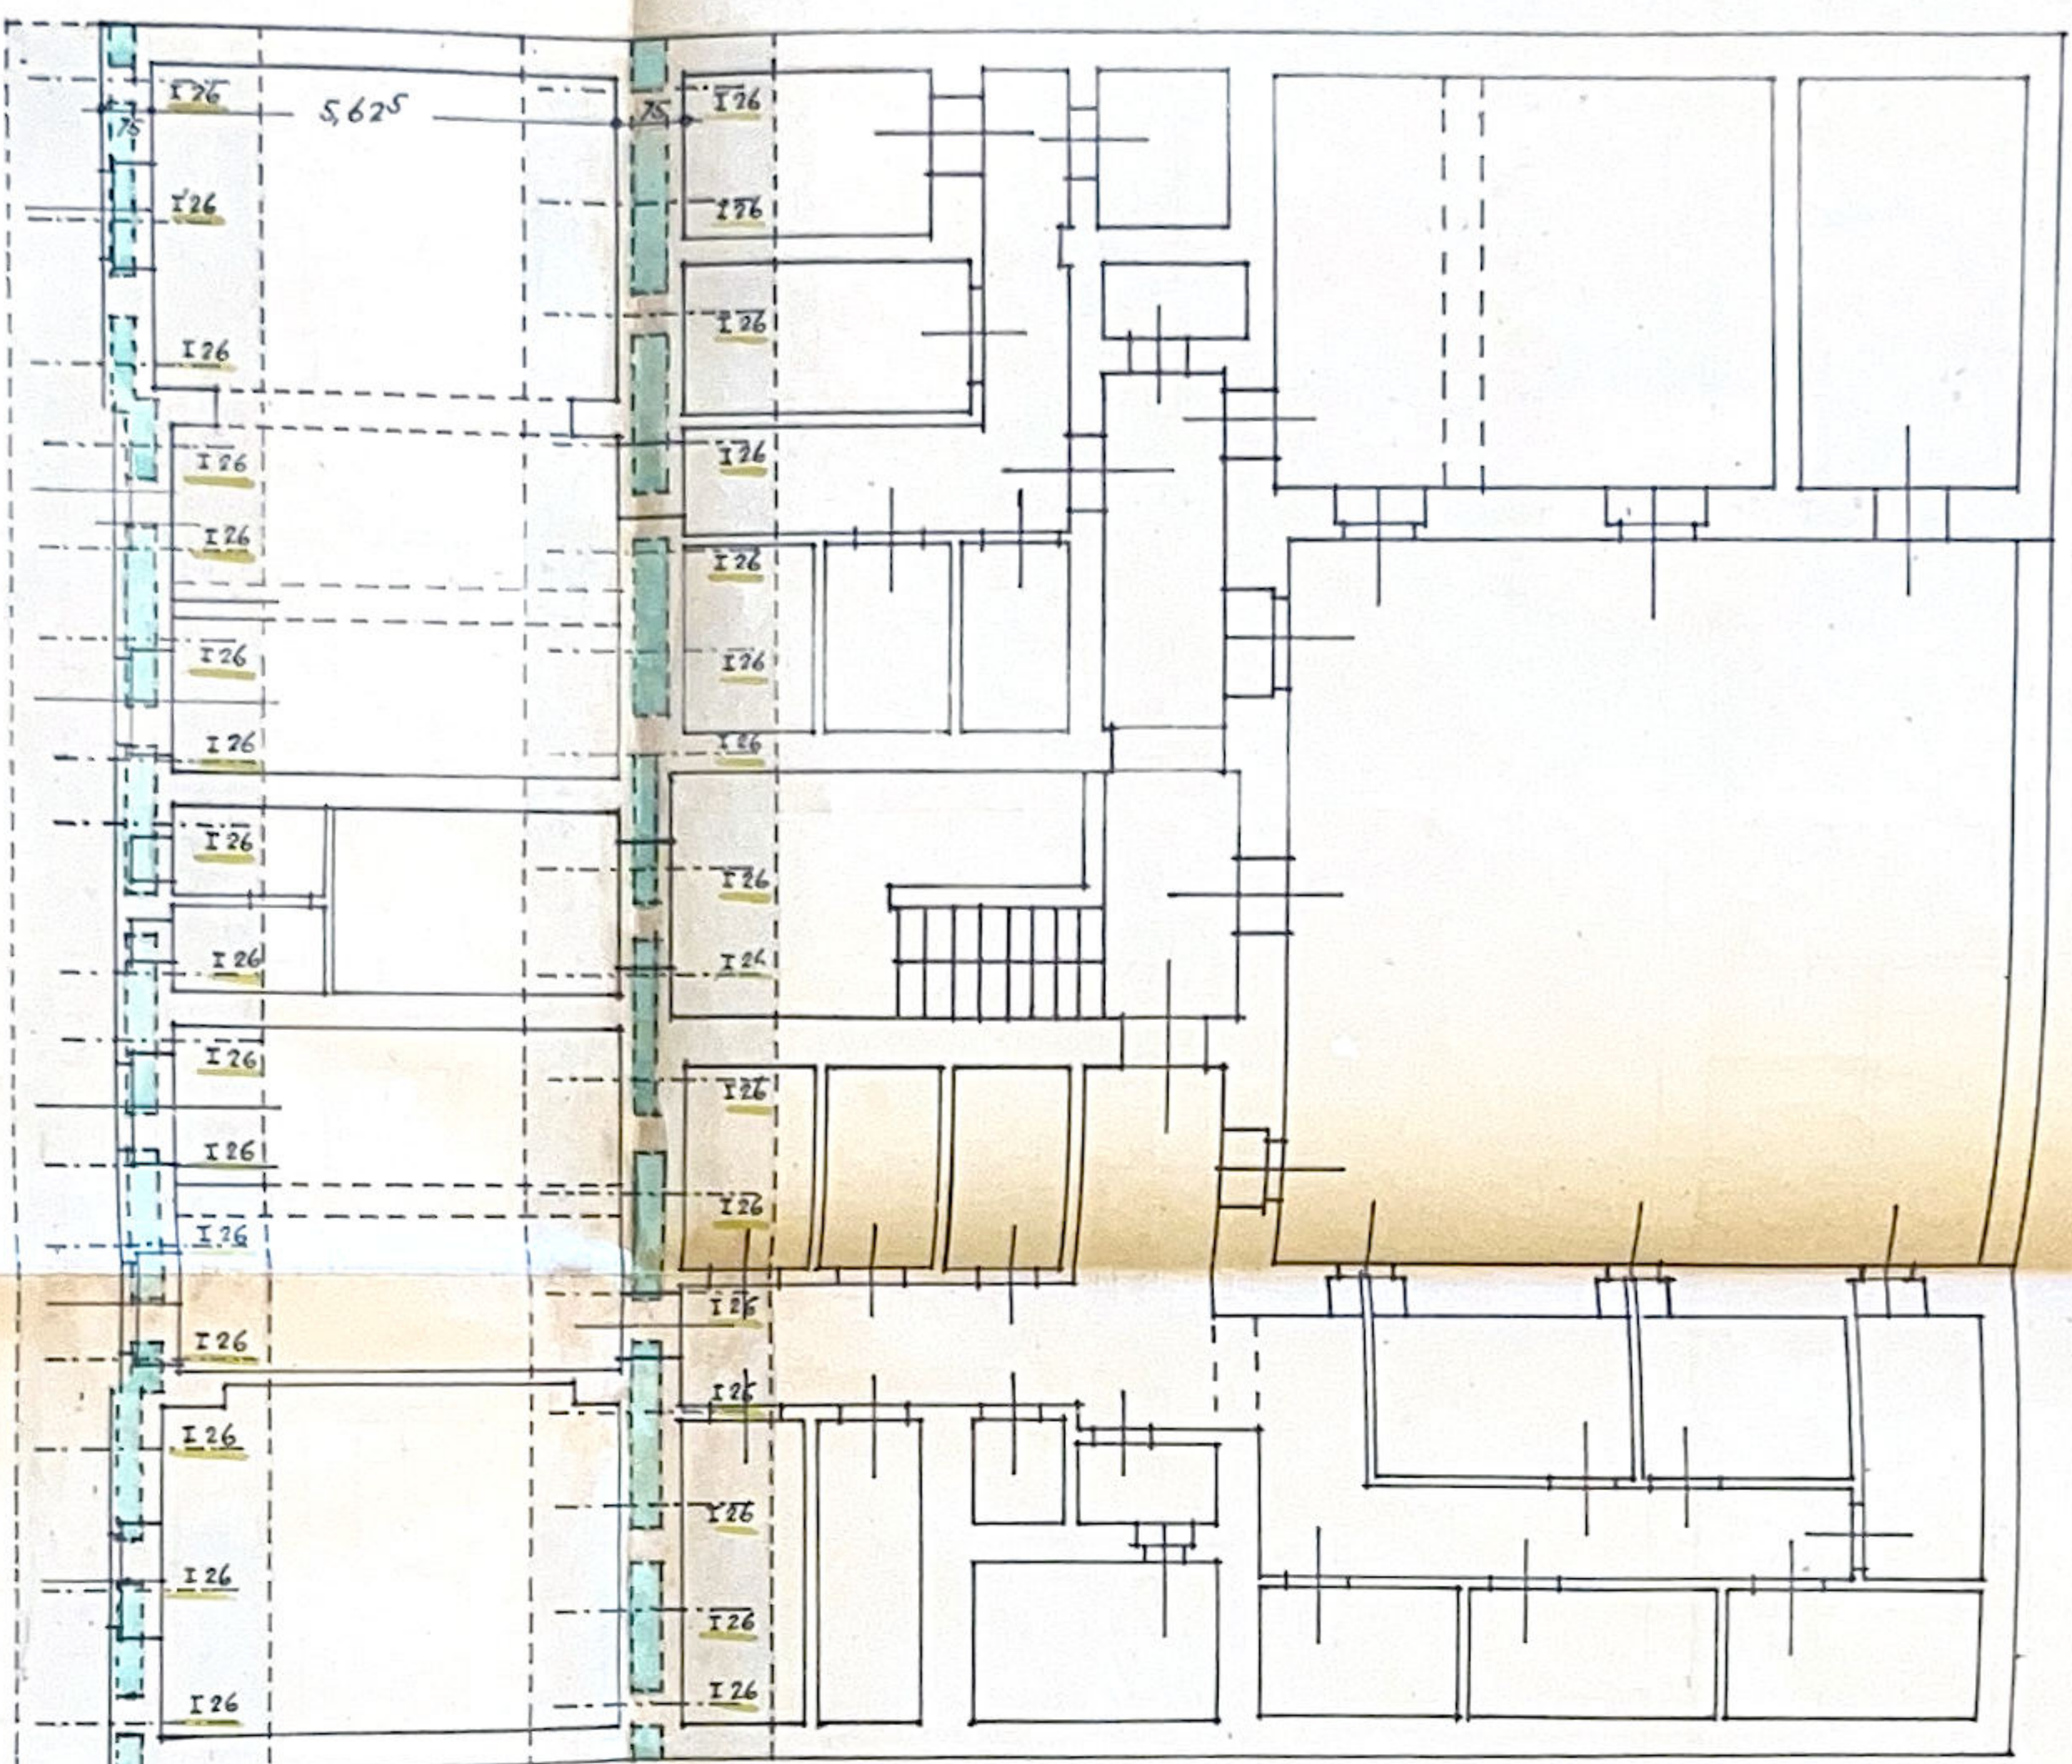

BAUWERBER U. EIGENTÜMER
VERTRETEN DURCH,

Hermann Ströhl
Geb. Verwalter
Friedlstr. 20
1010 Wien


Hermann Ströhl

BAUFÜHRER U. PLANVERFASSER:

ING. J. TSCHERFINGER
STADTBAUMEISTER
WIEN, XIV, BREITENSEERSTR. 37
TEL. Y 10-1-95


Ing. J. Tschering

SCHNITT DURCH MITELMAUER

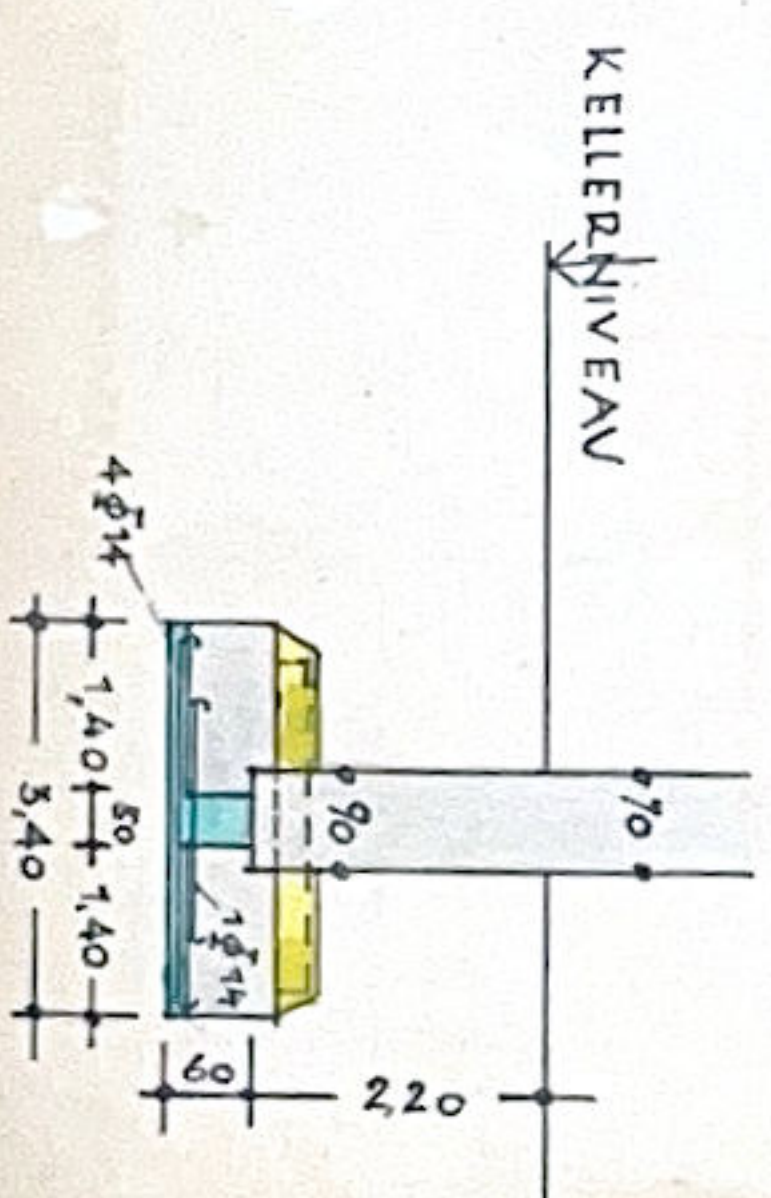

KELLERNIVEAU

SCHNITT DURCH HAUPTMAUER,

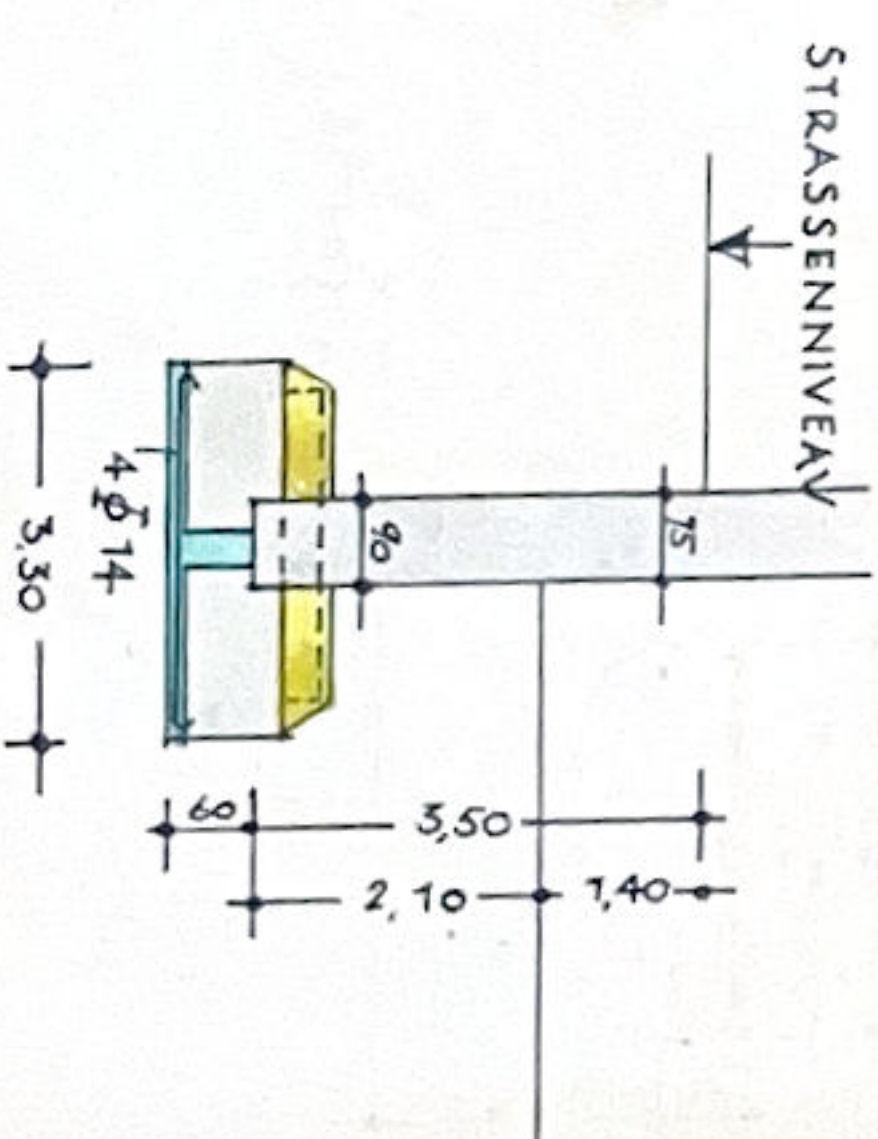

STRASSENIVEAU

ZUSÄTZLICHE
FUNDAMENTUNTERFANGUNG,

WIEN, IM APRIL 1954,